


SHEET#	DWG#	DRAWING NAME														
1 2 3	CP D01 D02	COVER PAGE ITEM A - SHOW FLOOR VENUE FLOOR PLAN ITEM A - SHOW FLOOR DETAILS														
Centre / Stage FROZEN ITEM A - SHOW FLOOR CONSTRUCTION DESIGN PLAN SET V3 24/07/26																
iceworks design ICEWORKS DESIGN PTY. LTD. 5/747 Fairfield Rd, Yeerongpilly, QLD. 4105 PO Box 624, Fairfield Gardens, QLD. 4103 T: + 617 3352 4511 www.iceworksdesign.com			Centre / Stage			THESE DRAWINGS ARE CONCEPT & DESIGN ONLY. FURTHER CONSTRUCTION & DETAIL DRAWINGS MAY BE REQUIRED. These drawings are © copyright 2025 ICEWORKS DESIGN. Drawings, illustrations & 3D Renders are not to be used, reproduced or copied without permission from ICEWORKS DESIGN. All dimensions are to be checked on site prior to commencing any construction, if in doubt please contact ICEWORKS DESIGN. Do not scale from drawings. Any building work is to comply with the building act, BCA and standard regulations where applicable.			DESIGN APPROVAL sign:..... print name:..... APPROVED / REVISE [circle] comments..... date:..... /..... /.....			CLIENT: CENTRESTAGE PROJECT: FROZEN DESIGNER: HARRY GILL VENUE: CIVIC THEATRE ADDRESS: 375 HUNTER ST NEWCASTLE, NSW 2300 JOB No: 26150		DRAWING NAME: COVER PAGE DRAWN BY: GAVIN HAMPSTEAD ISSUE: DATE DESCRIPTION 22/07/26 ISSUE FOR COSTING & CLIENT REVIEW 23/07/26 REVISED. ISSUE FOR CLIENT APPROVAL FOR CONSTRUCTION 24/07/26 FEATHER EDGE ADDED. ISSUE FOR CLIENT APPROVAL 00/00/00 XXXX 00/00/00 XXXX 00/00/00 XXXX		SCALE: N/A @ A3 DWG No: CP SHEET No: 1 / 3

A PLAN VIEW
1:100A3

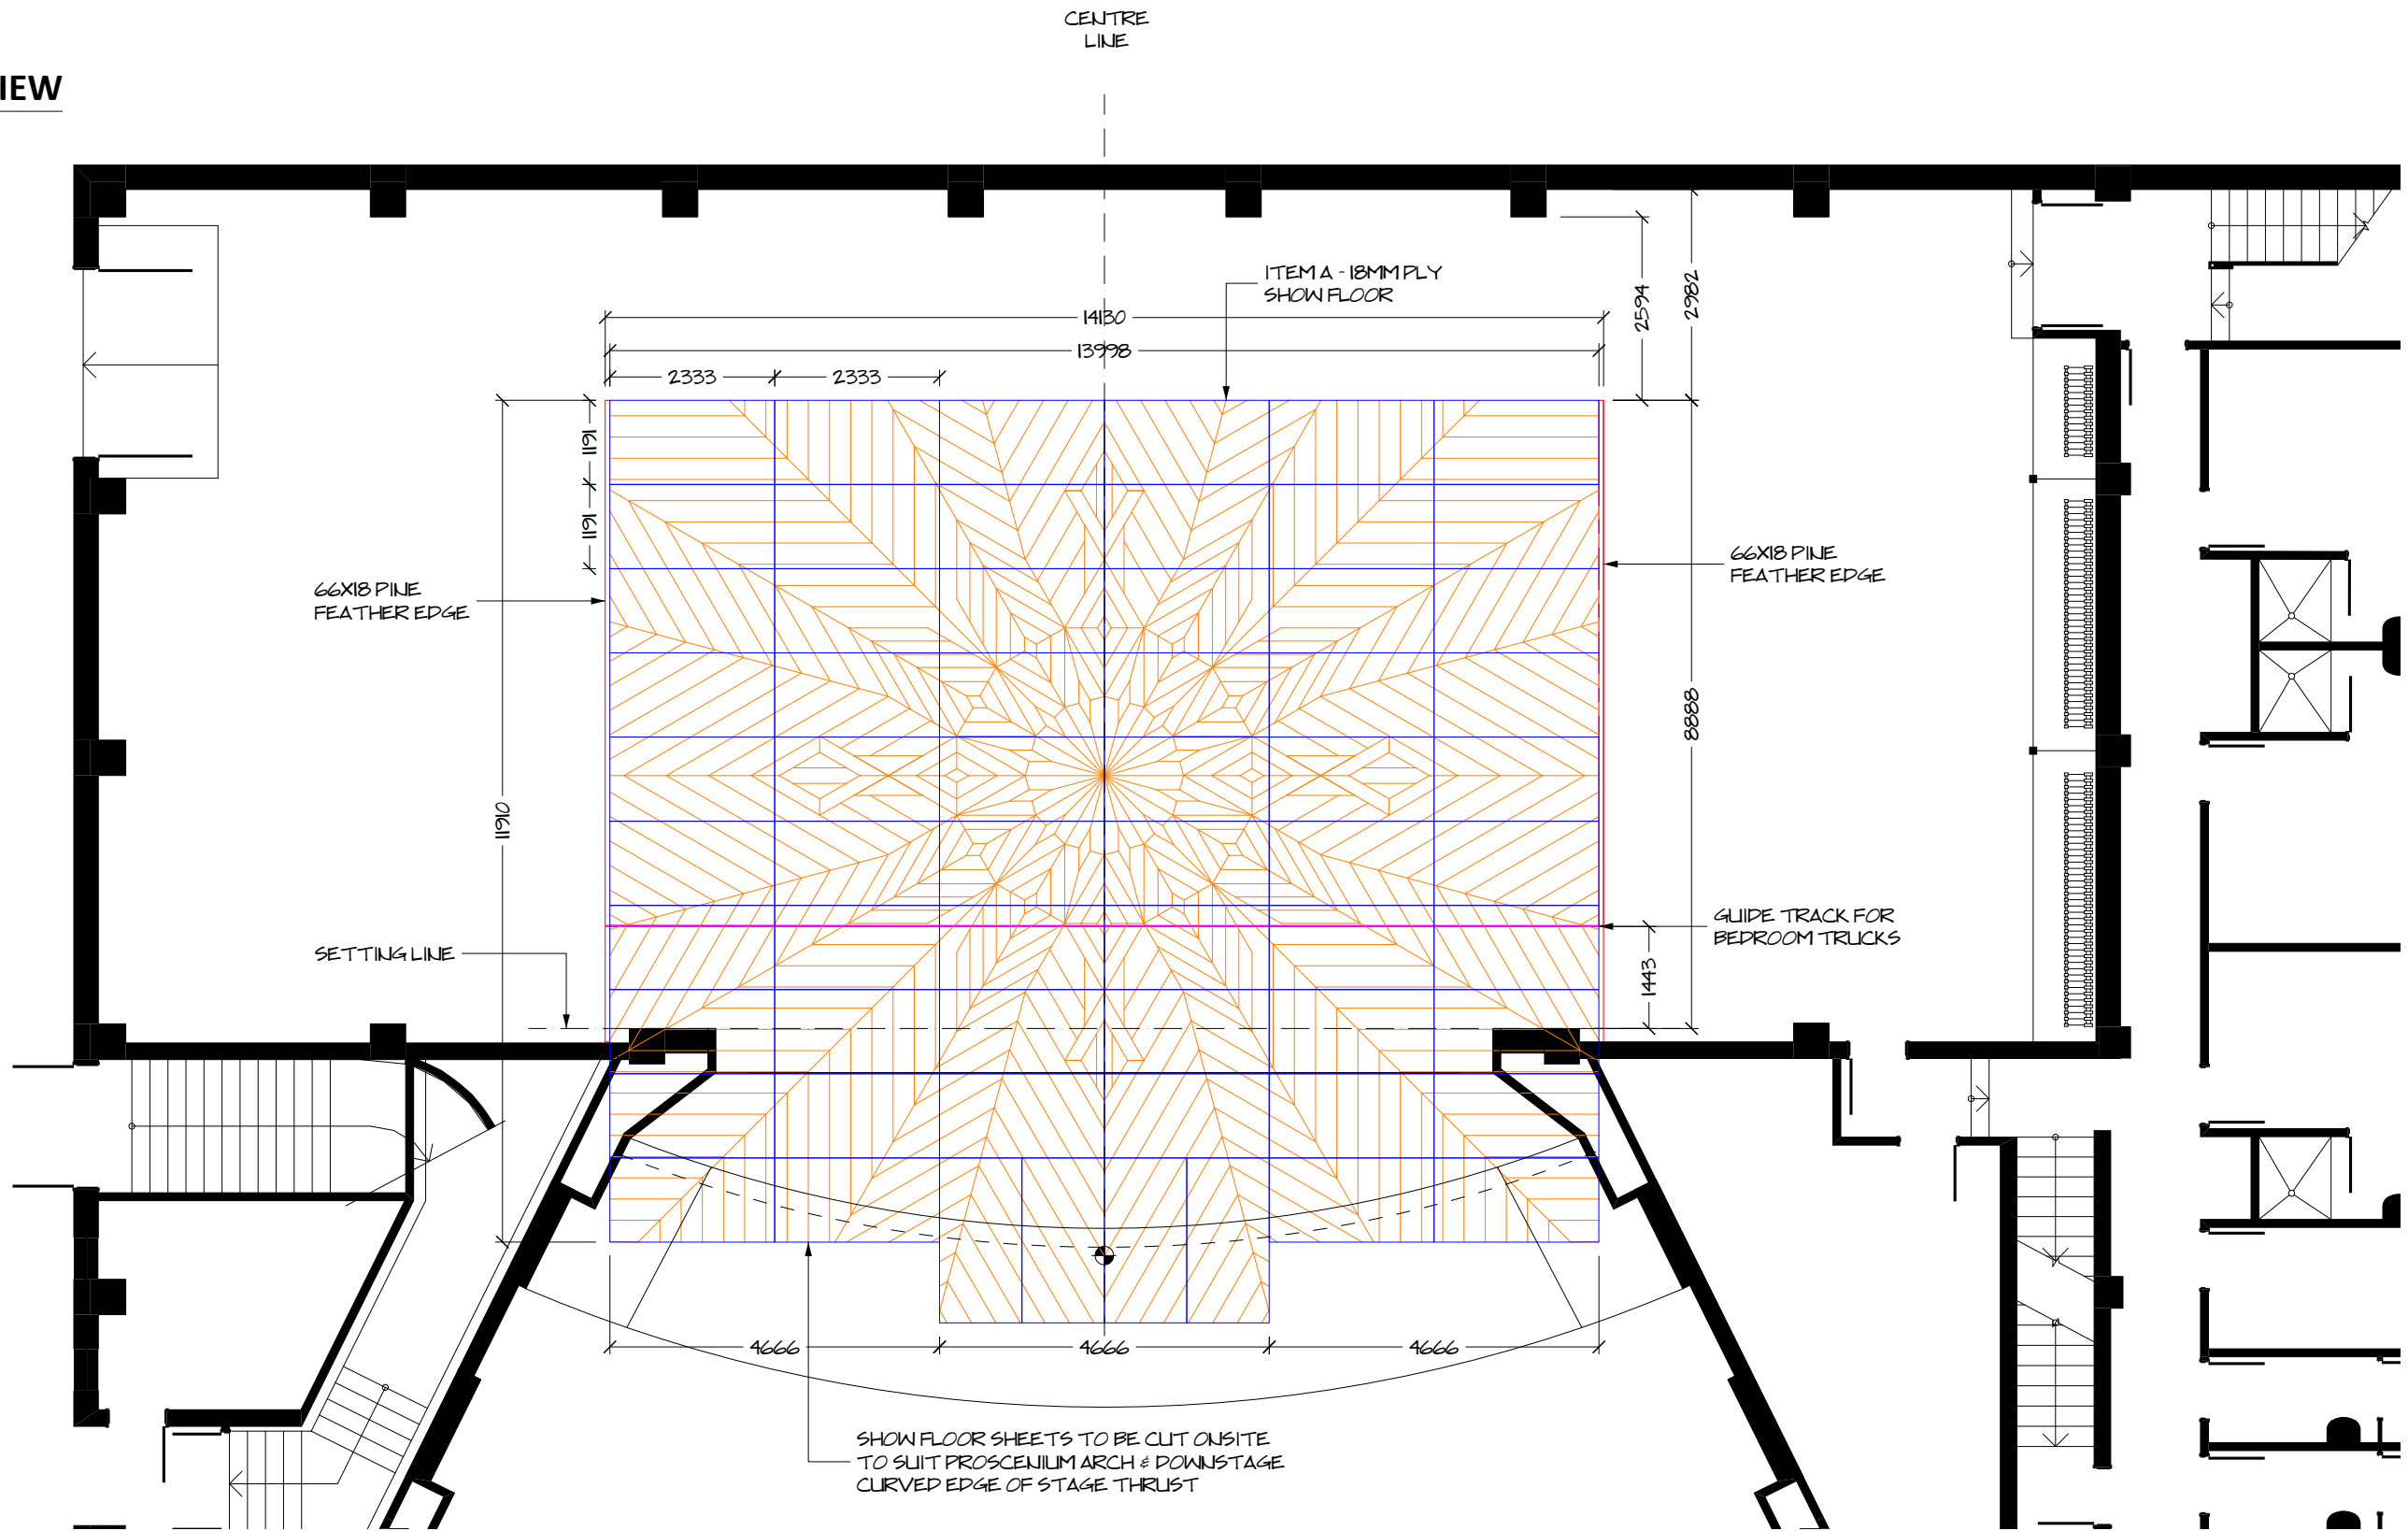

iceworks
design

ICEWORKS DESIGN PTY. LTD.
5/747 Fairfield Rd, Yeerongpilly, QLD. 4105
PO Box 624, Fairfield Gardens, QLD. 4103
T: + 617 3352 4511
www.iceworksdesign.com

Centre/Stage

THESE DRAWINGS ARE CONCEPT & DESIGN ONLY.
FURTHER CONSTRUCTION & DETAIL DRAWINGS
MAY BE REQUIRED.

These drawings are © copyright 2025 ICEWORKS DESIGN.
Drawings, illustrations & 3D Renders are not to be used,
reproduced or copied without permission from ICEWORKS DESIGN.
All dimensions are to be checked on site prior to commencing any
construction, if in doubt please contact ICEWORKS DESIGN. Do
not scale from
drawings. Any building work is to comply with the building act,
BCA and standard regulations where applicable.



DESIGN APPROVAL

sign:.....
print name:.....
APPROVED / REVISE [circle]
comments.....
date:..... /..... /.....

CLIENT:	CENTRESTAGE
PROJECT	FROZEN
DESIGNER:	HARRY GILL
VENUE:	CIVIC THEATRE
ADDRESS:	375 HUNTER ST NEWCASTLE, NSW 2300
JOB No:	26150

DRAWING NAME:	ITEM A - SHOW FLOOR VENUE FLOOR PLAN	
DRAWN BY:	GAVIN HAMPSTEAD	
ISSUE:	DATE	DESCRIPTION
	22/07/26	ISSUE FOR COSTING & CLIENT REVIEW
	23/07/26	REVISED. ISSUE FOR CLIENT APPROVAL FOR CONSTRUCTION
	24/07/26	FEATHER EDGE ADDED. ISSUE FOR CLIENT APPROVAL
	00/00/00	XXXX
	00/00/00	XXXX
	00/00/00	XXXX

SCALE:	1:100 @ A3
DWG No:	D01
SHEET No:	2 / 3

A **DETAIL FRONT VIEW**
1:2@A3

FRONT VIEW

18MM PLY SHOW FLOOR

66


66X18 PINE FEATHER EDGE TO STAGE LEFT AND RIGHT EDGES OF SHOW FLOOR

18


2

VENUE STAGE

A **PLAN VIEW**
1:75@A3

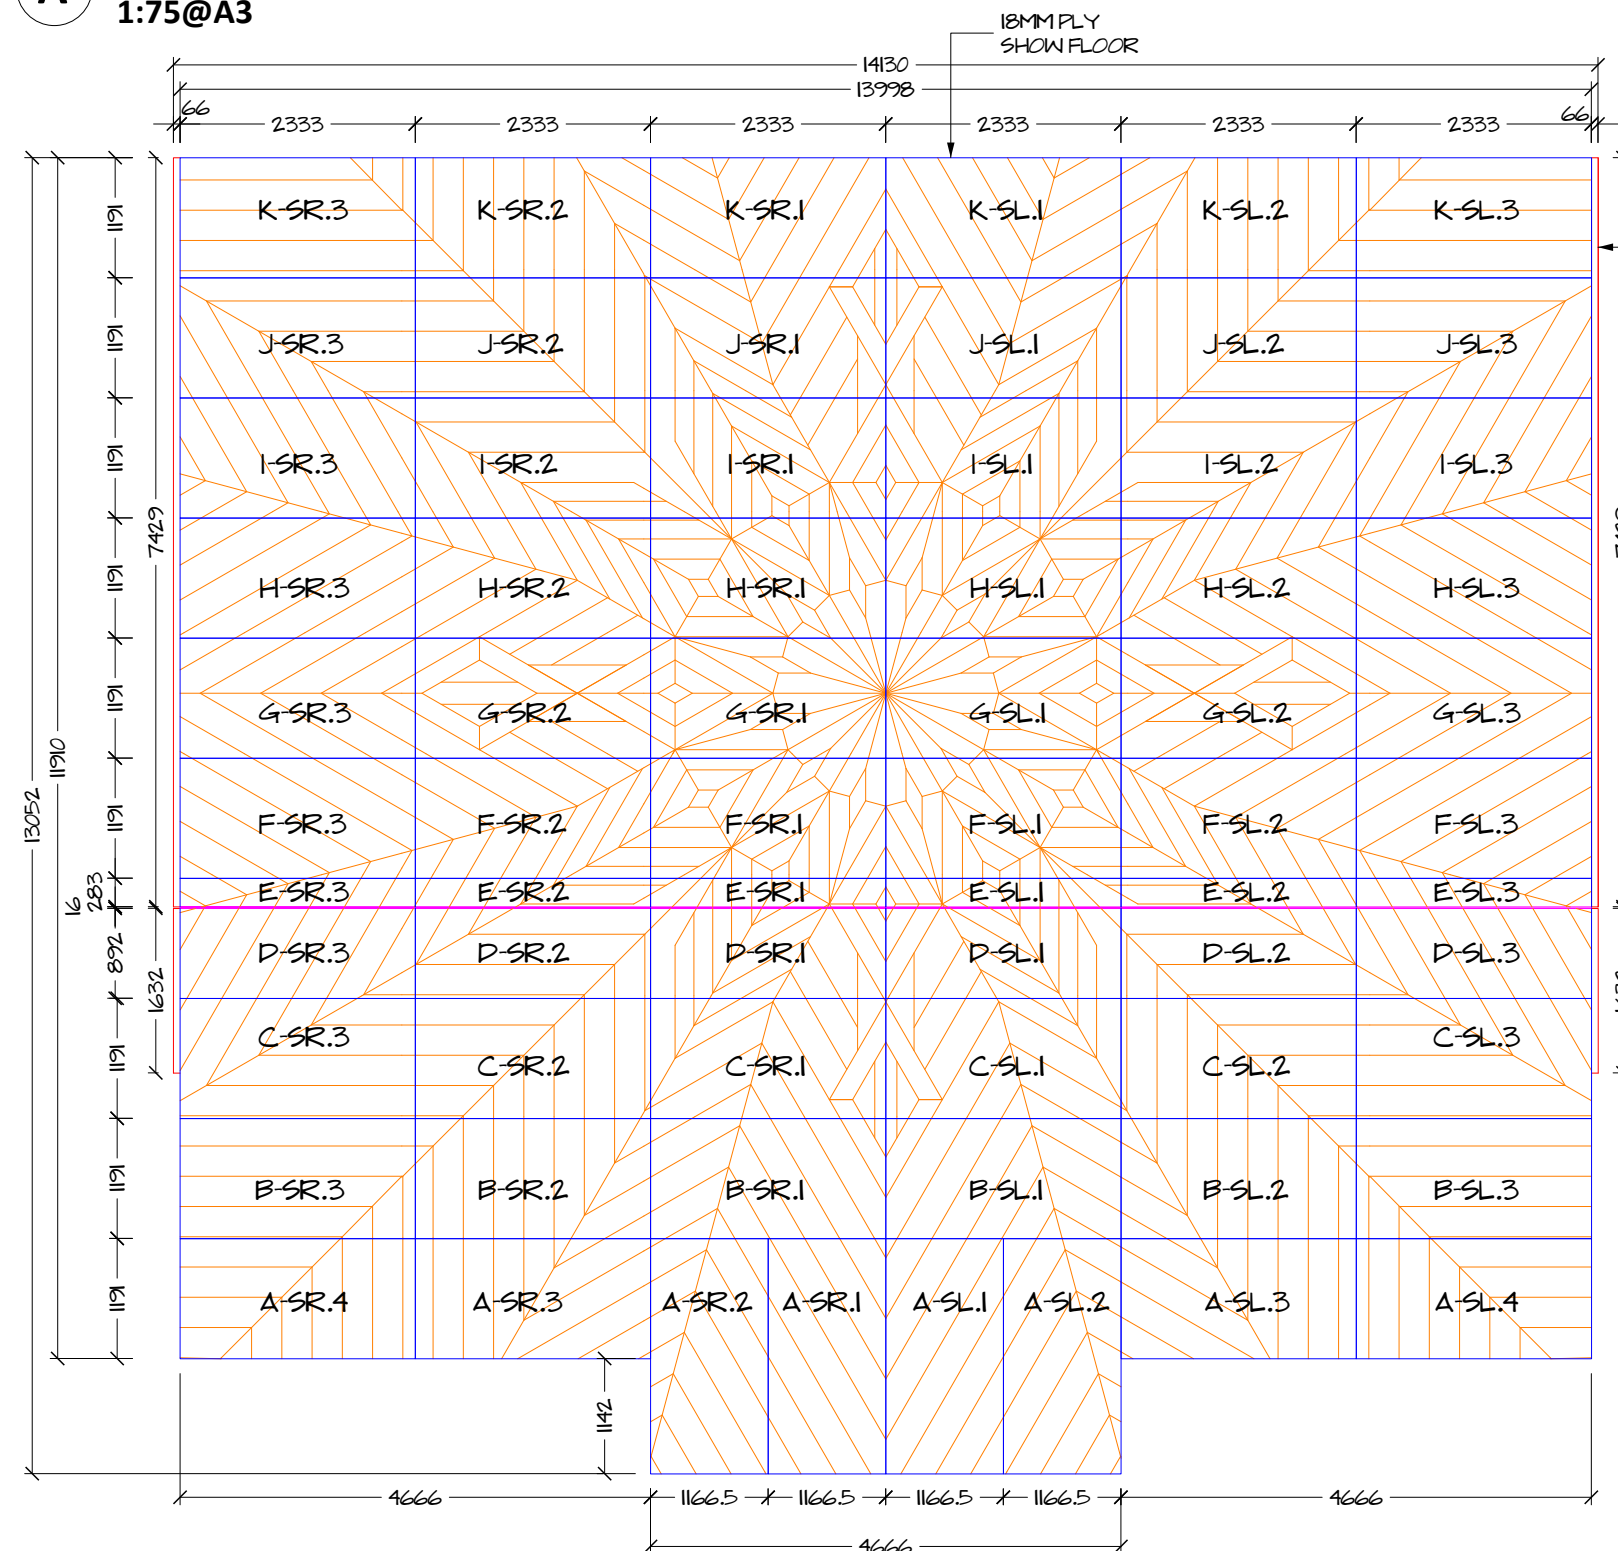

A **DETAIL END VIEW**
1:2@A3

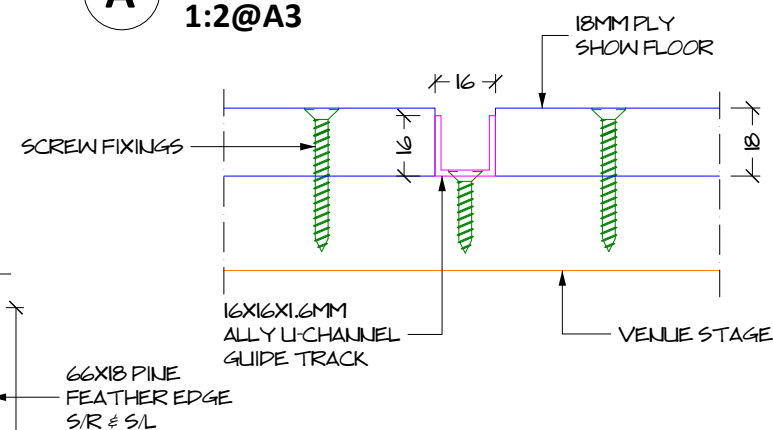

MAKE 1 X ITEM AS SHOWN.

CONSTRUCTED FROM 18MM SELECTED PLY, CNC CUT TO SHAPE. DECORATIVE PATTERN DETAIL CNC CUT 5MM WIDE V GROOVES INTO TOP FACE. SCENIC PAINT FINISH TO MATCH SCENIC REFERENCE IMAGE SUPPLIED BY SET DESIGNER.

SCREW FIX 16X16X1.6MM ALUMINIUM U-CHANNEL TO VENUE FLOOR WITH COUNTERSUNK 19MM 8G TIMBER SCREWS BETWEEN SHOW FLOOR SHEETS TO CREATE GUIDE TRACK FOR BEDROOM TRUCKS.

MAKE 4 X FEATHER EDGES FROM 66X18 PINE, CUT ANGLE AS SHOWN. PAINT FINISH LOW SHEEN BLACK. SCREW FIX OR GAFFA TAPE IN POSITION ON SITE.

SCREW FIX SHOW FLOOR SHEETS TO VENUE FLOOR WITH 35MM COUNTERSUNK 8G TIMBER SCREWS TBC BY PRODUCTION MANAGER & CIVIC THEATRE TO CONFIRM STAGE FLOOR THICKNESS.

SCENIC FINISH REFERENCE



iceworks
design

ICEWORKS DESIGN PTY. LTD.
5/747 Fairfield Rd, Yeerongpilly, QLD. 4105
PO Box 624, Fairfield Gardens, QLD. 4103
T: + 617 3352 4511
www.iceworksdesign.com

Centre / Stage

THESE DRAWINGS ARE CONCEPT & DESIGN ONLY.
FURTHER CONSTRUCTION & DETAIL DRAWINGS
MAY BE REQUIRED.

These drawings are © copyright 2025 ICEWORKS DESIGN.
Drawings, illustrations & 3D Renders are not to be used,
reproduced or copied without permission from ICEWORKS DESIGN
All dimensions are to be checked on site prior to commencing any
construction, if in doubt please contact ICEWORKS DESIGN. Do
not scale from
drawings. Any building work is to comply with the building act,
BCA and standard regulations where applicable.

METRES

DESIGN APPROVAL

sign:.....

```
print name:.....
```

APPROVED / REVISE [circle]

comments.....

date:..... /..... /.....

CLIENT: **CENTRESTAGE**

PROJECT	FROZEN
---------	--------

DESIGNER:	HARRY GILL
-----------	------------

VENUE:	CIVIC THEATRE
--------	---------------

ADDRESS: 375 HUNTER ST
NEWCASTLE, NSW 2300

JOB No:	26150
---------	-------

DRAWING

DRAWING NAME: **ITEM A - SHOW FLOOR DETAILS**

DRAWN BY:	GAVIN HAMPSTEAD
-----------	-----------------

ISSUE:

DESCRIPTION

22/07/26	ISSUE FOR COSTING & CLIENT REVIEW
----------	-----------------------------------

23/07/26	REVISED. ISSUE FOR CLIENT APPROVAL FOR CONSTRUCTION
----------	---

24/07/26	FEATHER EDGE ADDED. ISSUE FOR CLIENT APPROVAL.
----------	--

00/00/00	XXX
----------	-----

00/00/00	XXX
----------	-----

00/00/00	XXX
----------	-----

SCALE: *AS SHOWN @ A3*

	DWG
	No:

D02

SHEET
No:

3 / 3