

SHEET#	DWG#	DRAWING NAME													
1	CP	COVER PAGE													
2	D01	RENDERED VIEWS													
3	D02	ASSEMBLED VIEWS													
4	D03	ITEM C.1 - D/S PILLARS													
5	D04	ITEM C.2 - D/S HEADER													
6	D05	ITEM C.3 - D/S ARCH													
7	D06	ITEM C.1-C.3 - CNC FILES													
			Centre/Stage FROZEN ITEM C.1-C.3 - DOWNSTAGE PILLARS & ARCH CONSTRUCTION DESIGN PLAN SET V1 29/07/26												
iceworksdesign ICEWORKS DESIGN PTY. LTD. 5/747 Fairfield Rd, Yeerongpilly, QLD. 4105 PO Box 624, Fairfield Gardens, QLD. 4103 T: + 617 3352 4511 www.iceworksdesign.com			Centre/Stage		THESE DRAWINGS ARE CONCEPT & DESIGN ONLY. FURTHER CONSTRUCTION & DETAIL DRAWINGS MAY BE REQUIRED. These drawings are © copyright 2025 ICEWORKS DESIGN. Drawings, illustrations & 3D Renders are not to be used, reproduced or copied without permission from ICEWORKS DESIGN. All dimensions are to be checked on site prior to commencing any construction, if in doubt please contact ICEWORKS DESIGN. Do not scale from drawings. Any building work is to comply with the building act, BCA and standard regulations where applicable.		DESIGN APPROVAL sign:..... print name:..... APPROVED / REVISE [circle] comments..... date:..... /..... /.....		CLIENT:	CENTRESTAGE	DRAWING NAME:	COVER PAGE		SCALE:	N/A @ A3
									PROJECT:	FROZEN	DRAWN BY:	GAVIN HAMPSTEAD		DWG No:	CP
									DESIGNER:	HARRY GILL	ISSUE:	DATE	DESCRIPTION		
									VENUE:	CIVIC THEATRE		29/07/26	ISSUE FOR COSTING & CLIENT REVIEW	SHEET No:	1 / 7
									ADDRESS:	375 HUNTER ST NEWCASTLE, NSW 2300		00/00/00	XXXX		
												00/00/00	XXXX		
												00/00/00	XXXX		
									JOB No:	26150		00/00/00	XXXX		


C.1-C.3

3D FRONT VIEW
NA@A3



C.1-C.3

3D REAR VIEW
NA@A3

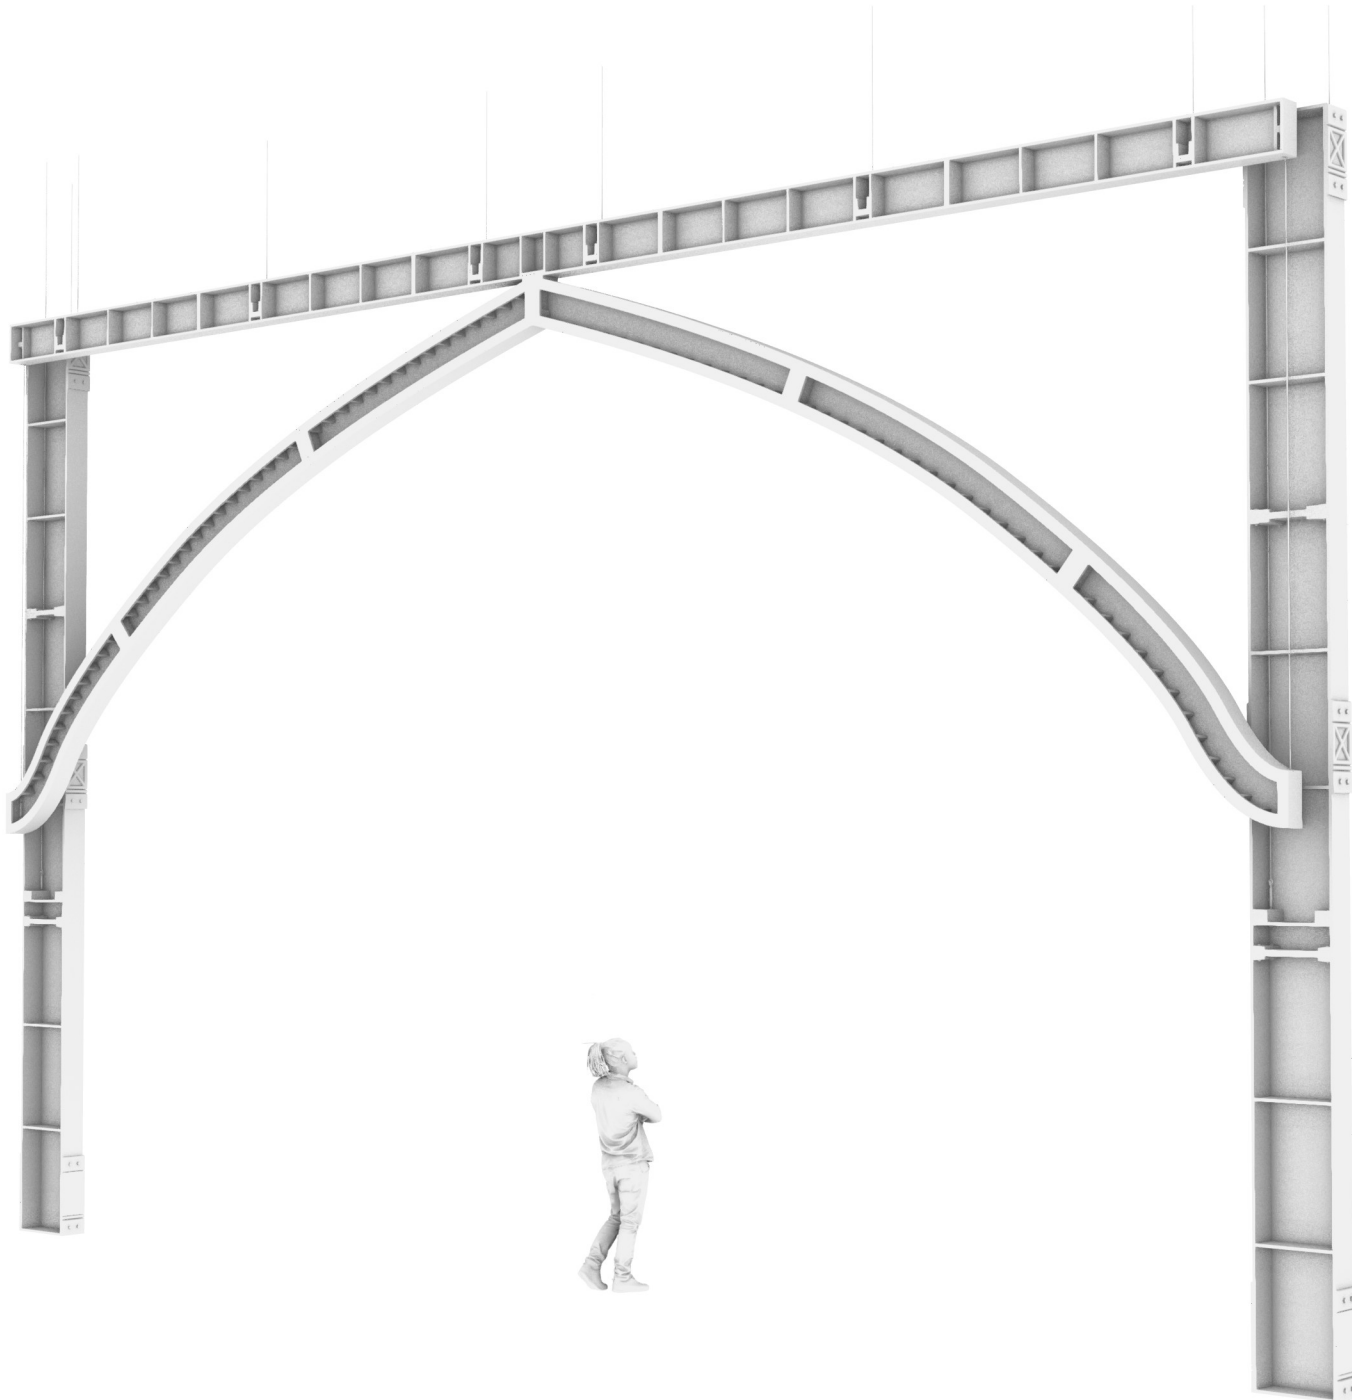

iceworks
design

ICEWORKS DESIGN PTY. LTD.
5/747 Fairfield Rd, Yeerongpilly, QLD. 4105
PO Box 624, Fairfield Gardens, QLD. 4103
T: + 617 3352 4511
www.iceworksdesign.com

Centre/Stage

THESE DRAWINGS ARE CONCEPT & DESIGN ONLY.
FURTHER CONSTRUCTION & DETAIL DRAWINGS
MAY BE REQUIRED.

These drawings are © copyright 2025 ICEWORKS DESIGN.
Drawings, illustrations & 3D Renders are not to be used,
reproduced or copied without permission from ICEWORKS DESIGN.
All dimensions are to be checked on site prior to commencing any
construction, if in doubt please contact ICEWORKS DESIGN. Do
not scale from
drawings. Any building work is to comply with the building act,
BCA and standard regulations where applicable.

DESIGN APPROVAL

sign:.....

print name:.....

APPROVED / REVISE [circle]

comments:.....

date:..... /..... /.....


CLIENT:	CENTRESTAGE
PROJECT	FROZEN
DESIGNER:	HARRY GILL
VENUE:	CIVIC THEATRE
ADDRESS:	375 HUNTER ST NEWCASTLE, NSW 2300
JOB No:	26150

DRAWING NAME:	RENDERED VIEWS	
	DRAWN BY: GAVIN HAMPSTEAD	
ISSUE:	DATE	DESCRIPTION
	29/07/26	ISSUE FOR COSTING & CLIENT REVIEW
	00/00/00	XXXX
	00/00/00	XXXX
	00/00/00	XXXX
	00/00/00	XXXX
	00/00/00	XXXX


SCALE:	NA@ A3
DWG No:	D01
SHEET No:	2 / 7

FROZEN


C.1-C.3
PLAN VIEW
1:50@A3

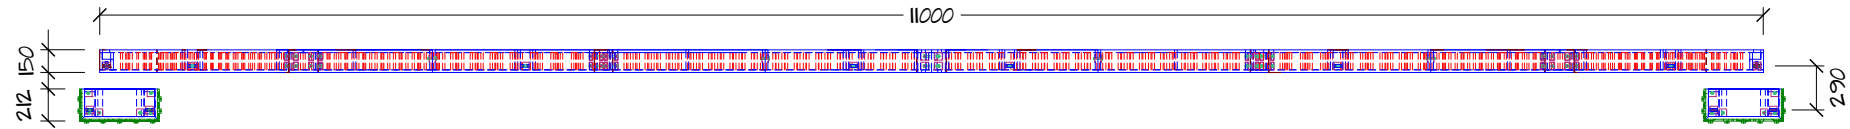

C.1-C.3
FRONT VIEW
1:50@A3

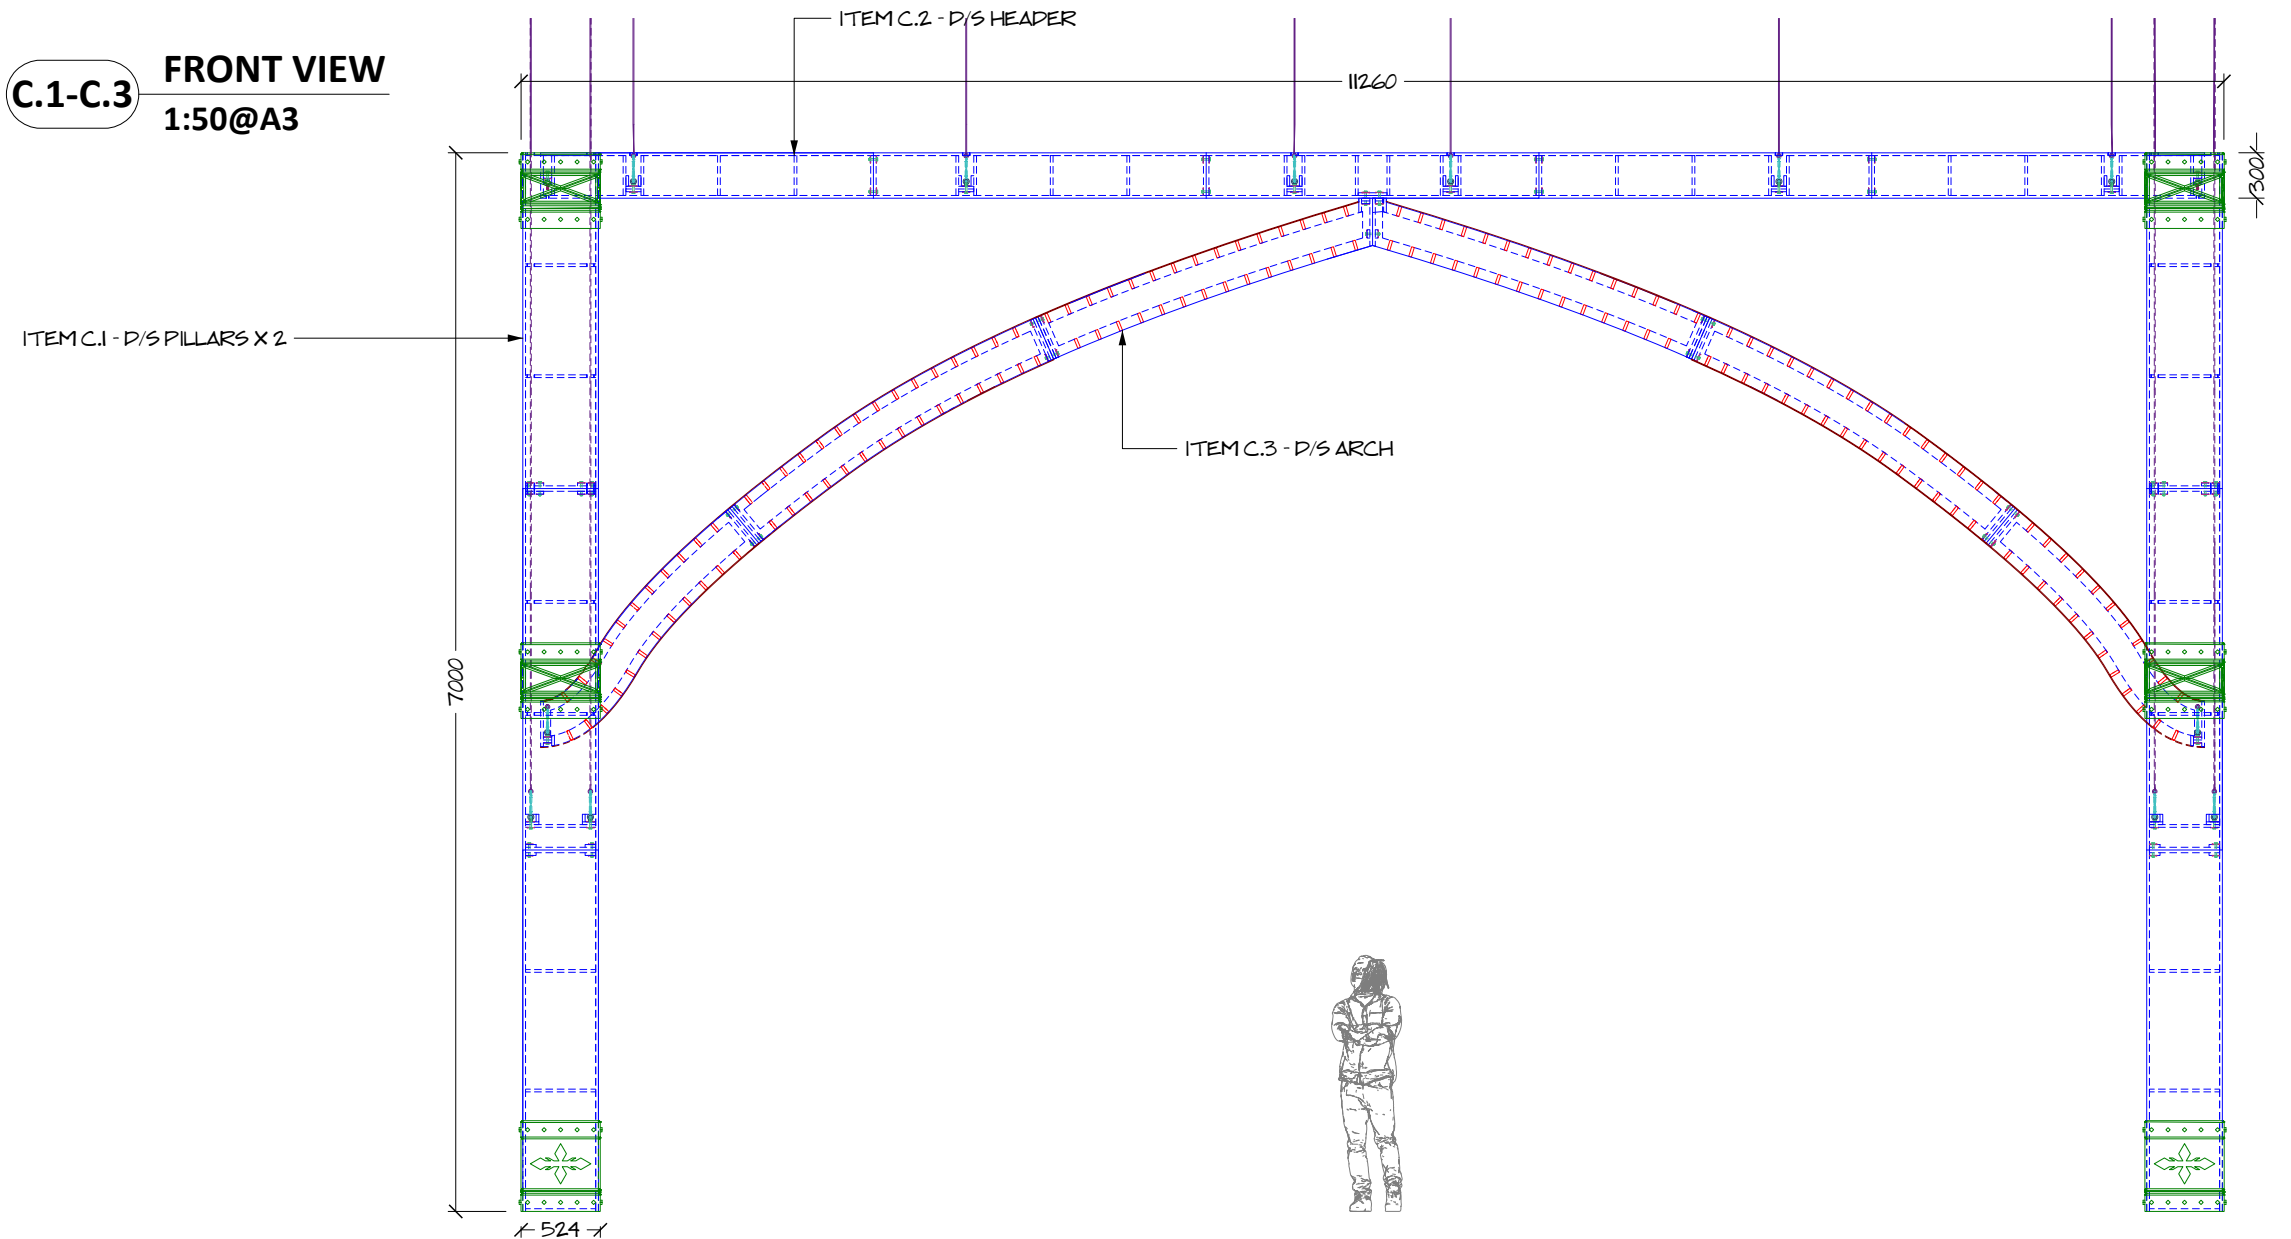

C.1-C.3
END VIEW
1:50@A3

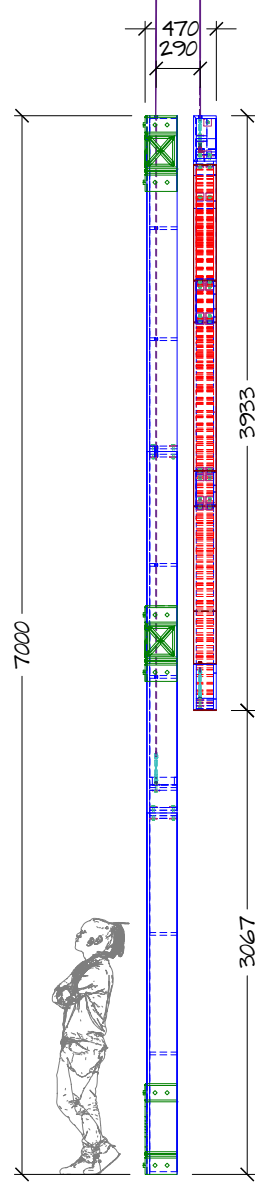


iceworks
design

ICEWORKS DESIGN PTY. LTD.
5/747 Fairfield Rd, Yeerongpilly, QLD. 4105
PO Box 624, Fairfield Gardens, QLD. 4103
T: + 617 3352 4511
www.iceworksdesign.com

Centre/Stage

THESE DRAWINGS ARE CONCEPT & DESIGN ONLY.
FURTHER CONSTRUCTION & DETAIL DRAWINGS
MAY BE REQUIRED.

These drawings are © copyright 2025 ICEWORKS DESIGN.
Drawings, illustrations & 3D Renders are not to be used,
reproduced or copied without permission from ICEWORKS DESIGN.
All dimensions are to be checked on site prior to commencing any
construction, if in doubt please contact ICEWORKS DESIGN. Do
not scale from
drawings. Any building work is to comply with the building act,
BCA and standard regulations where applicable.

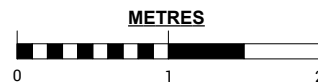

DESIGN APPROVAL

sign:.....
print name:.....
APPROVED / REVISE [circle]
comments.....
date:..... /..... /.....


CLIENT:	CENTRESTAGE
PROJECT	FROZEN
DESIGNER:	HARRY GILL
VENUE:	CIVIC THEATRE
ADDRESS:	375 HUNTER ST NEWCASTLE, NSW 2300
JOB No:	26150

DRAWING NAME:	ASSEMBLED VIEWS	
DRAWN BY:	GAVIN HAMPSTEAD	
ISSUE:	DATE	DESCRIPTION
	29/07/26	ISSUE FOR COSTING & CLIENT REVIEW
	00/00/00	XXXX
	00/00/00	XXXX
	00/00/00	XXXX
	00/00/00	XXXX
	00/00/00	XXXX


SCALE:	1:100 @ A3
DWG No:	D02
SHEET No:	3 / 7

QTY X 2


C.1 PLAN VIEW
1:5@A3

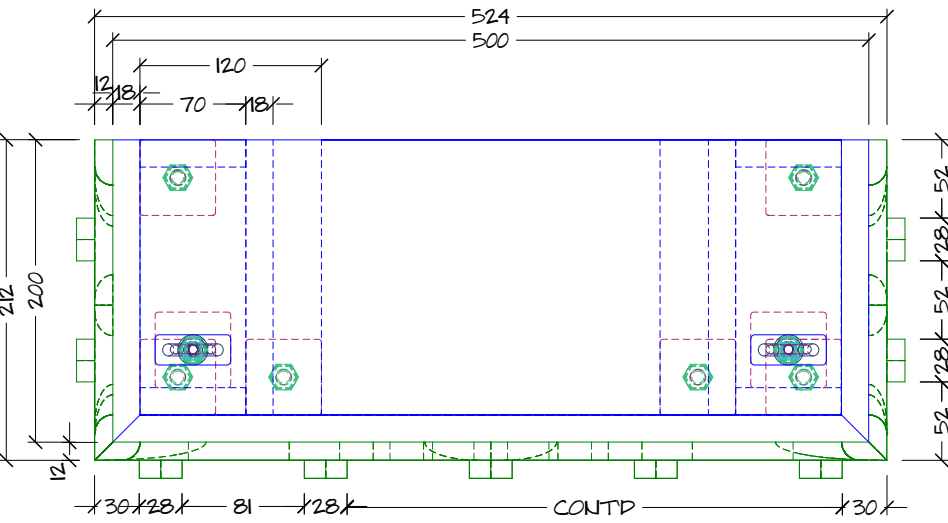


C.1 3D VIEW
NA@A3

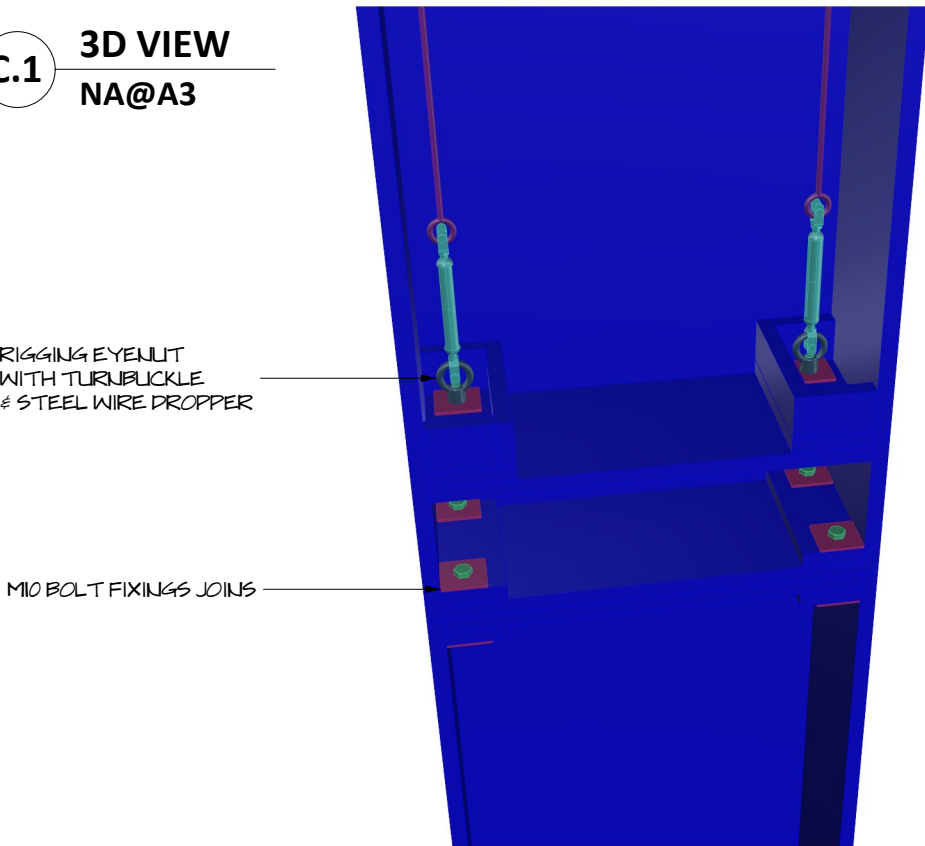


C.1 PLAN VIEW
1:50A3

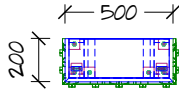

C.1 FRONT VIEW
1:50A3

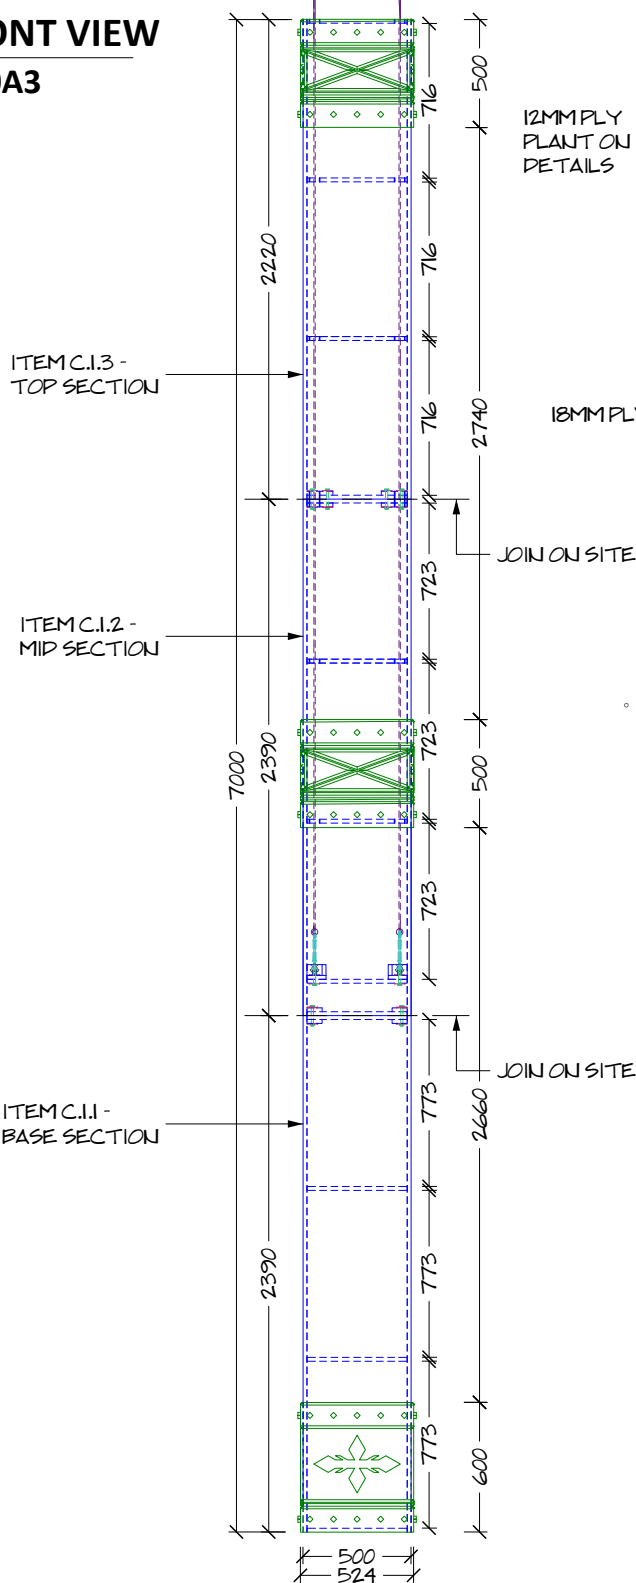

C.1 3D VIEWS
NA@A3

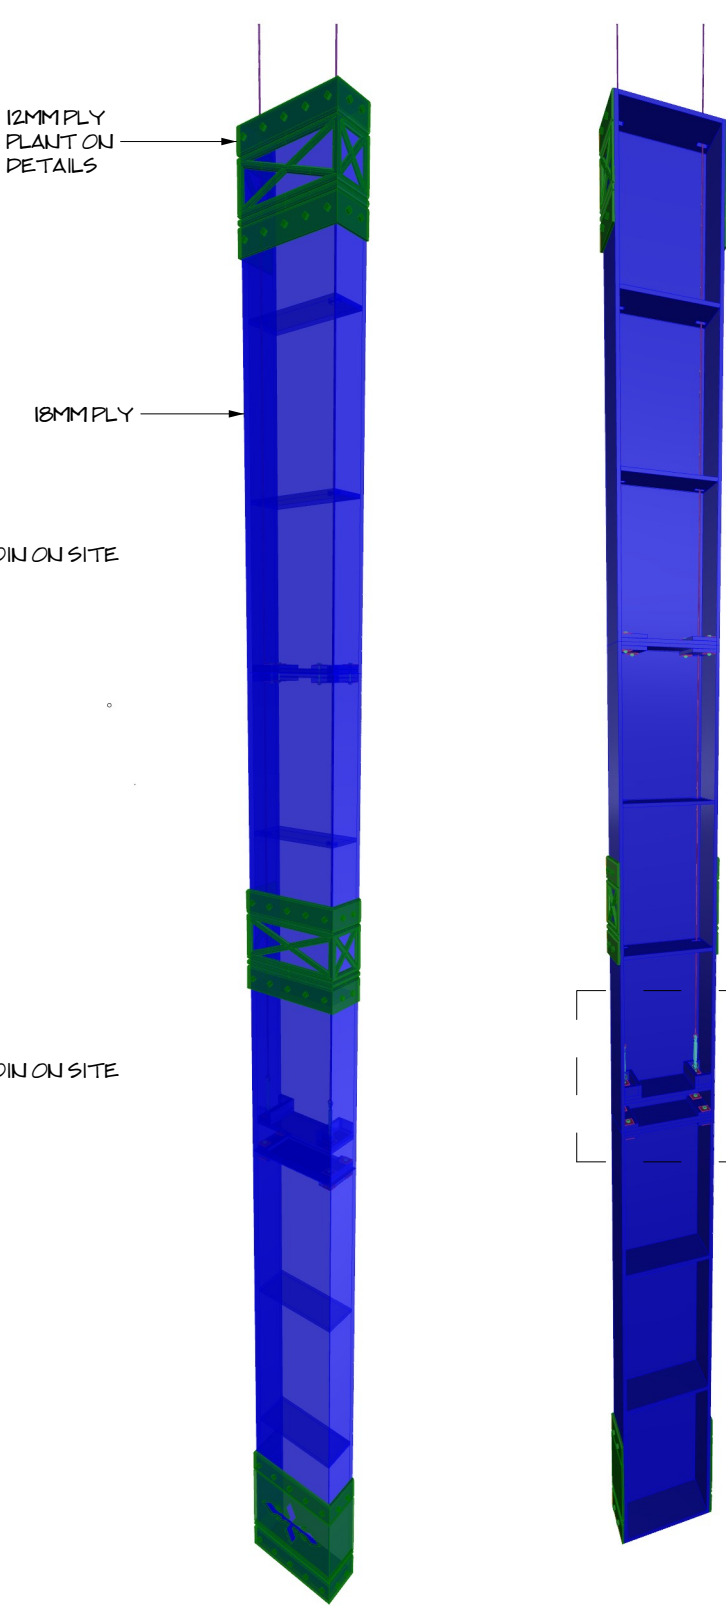

CONSTRUCTION DETAILS
MAKE 2 X ITEMS AS SHOWN.


CONSTRUCTED FROM 18MM SELEX PLY
CNC CUT TO SHAPE.
PLANT ON DETAILS CONSTRUCTED FROM
12MM SELEX PLY CNC CUT TO SHAPE. PVA
GLUE, BRAD NAIL & SCREW FIXING
ASSEMBLY.

BOLT FIX PILLAR SECTIONS TOGETHER
WITH 4 X 90MM M10 BOLTS PER JOIN.

RIGGING DETAILS - 2 X RATED M10
EYENLITS WITH M10 BOLTS TO SUIT. 2 X
JAW-JAW TURNBUCKLES WITH 2 X 5M LONG
6MM BLACK STEEL WIRE DROPPERS WITH
RATED SHACKLE. DROPPER LENGTH TBC
BY PRODUCTION MANAGER. YUPPIE
STRAPS TOP RIGGING SUPPLIED BY
PRODUCTION MANAGER.

FILL SCREW HOLES ONLY. LIGHT SAND ON
CNC PLANT ON DETAILS TO REMOVE
FURRING. UNDERCOAT AND SCENIC TOP
COAT PAINT FINISH TO MATCH SCENIC
REFERENCES SUPPLIED BY SET DESIGNER.

C.1 REAR VIEW
1:10A3

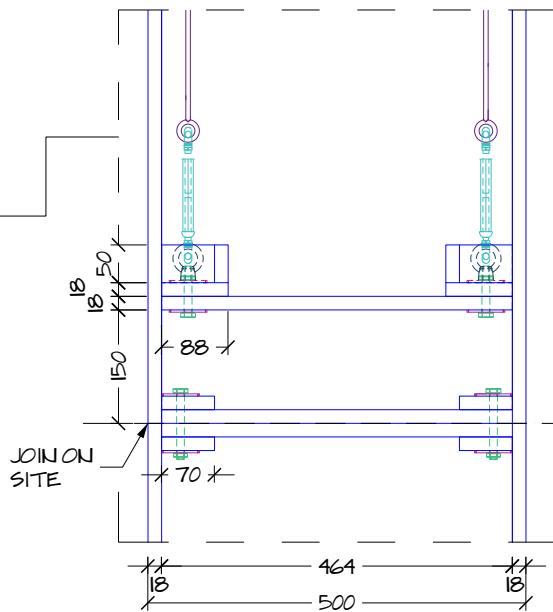

iceworks
design

ICEWORKS DESIGN PTY. LTD.
5/747 Fairfield Rd, Yeerongpilly, QLD. 4105
PO Box 624, Fairfield Gardens, QLD. 4103
T: + 617 3352 4511
www.iceworksdesign.com

Centre/Stage

THESE DRAWINGS ARE CONCEPT & DESIGN ONLY.
FURTHER CONSTRUCTION & DETAIL DRAWINGS
MAY BE REQUIRED.

These drawings are © copyright 2025 ICEWORKS DESIGN.
Drawings, illustrations & 3D Renders are not to be used,
reproduced or copied without permission from ICEWORKS DESIGN.
All dimensions are to be checked on site prior to commencing any
construction, if in doubt please contact ICEWORKS DESIGN. Do
not scale from
drawings. Any building work is to comply with the building act,
BCA and standard regulations where applicable.

DESIGN APPROVAL

sign:.....

print name:.....

APPROVED / REVISE [circle]

comments.....

date:..... /..... /.....

CLIENT: CENTRESTAGE

PROJECT: FROZEN

DESIGNER: HARRY GILL

VENUE: CIVIC THEATRE

ADDRESS: 375 HUNTER ST
NEWCASTLE, NSW 2300

JOB No: 26150

DRAWING
NAME:

ITEM C.1 - D/S PILLARS

DRAWN BY:

GAVIN HAMPSTEAD

ISSUE:

DATE DESCRIPTION

29/07/26	ISSUE FOR COSTING & CLIENT REVIEW
00/00/00	XXXX
00/00/00	XXXX
00/00/00	XXXX
00/00/00	XXXX
00/00/00	XXXX

SCALE: AS SHOWN @ A3


DWG
No:

D03

SHEET
No:

4 / 7

C.2 3D VIEWS
NA@A3

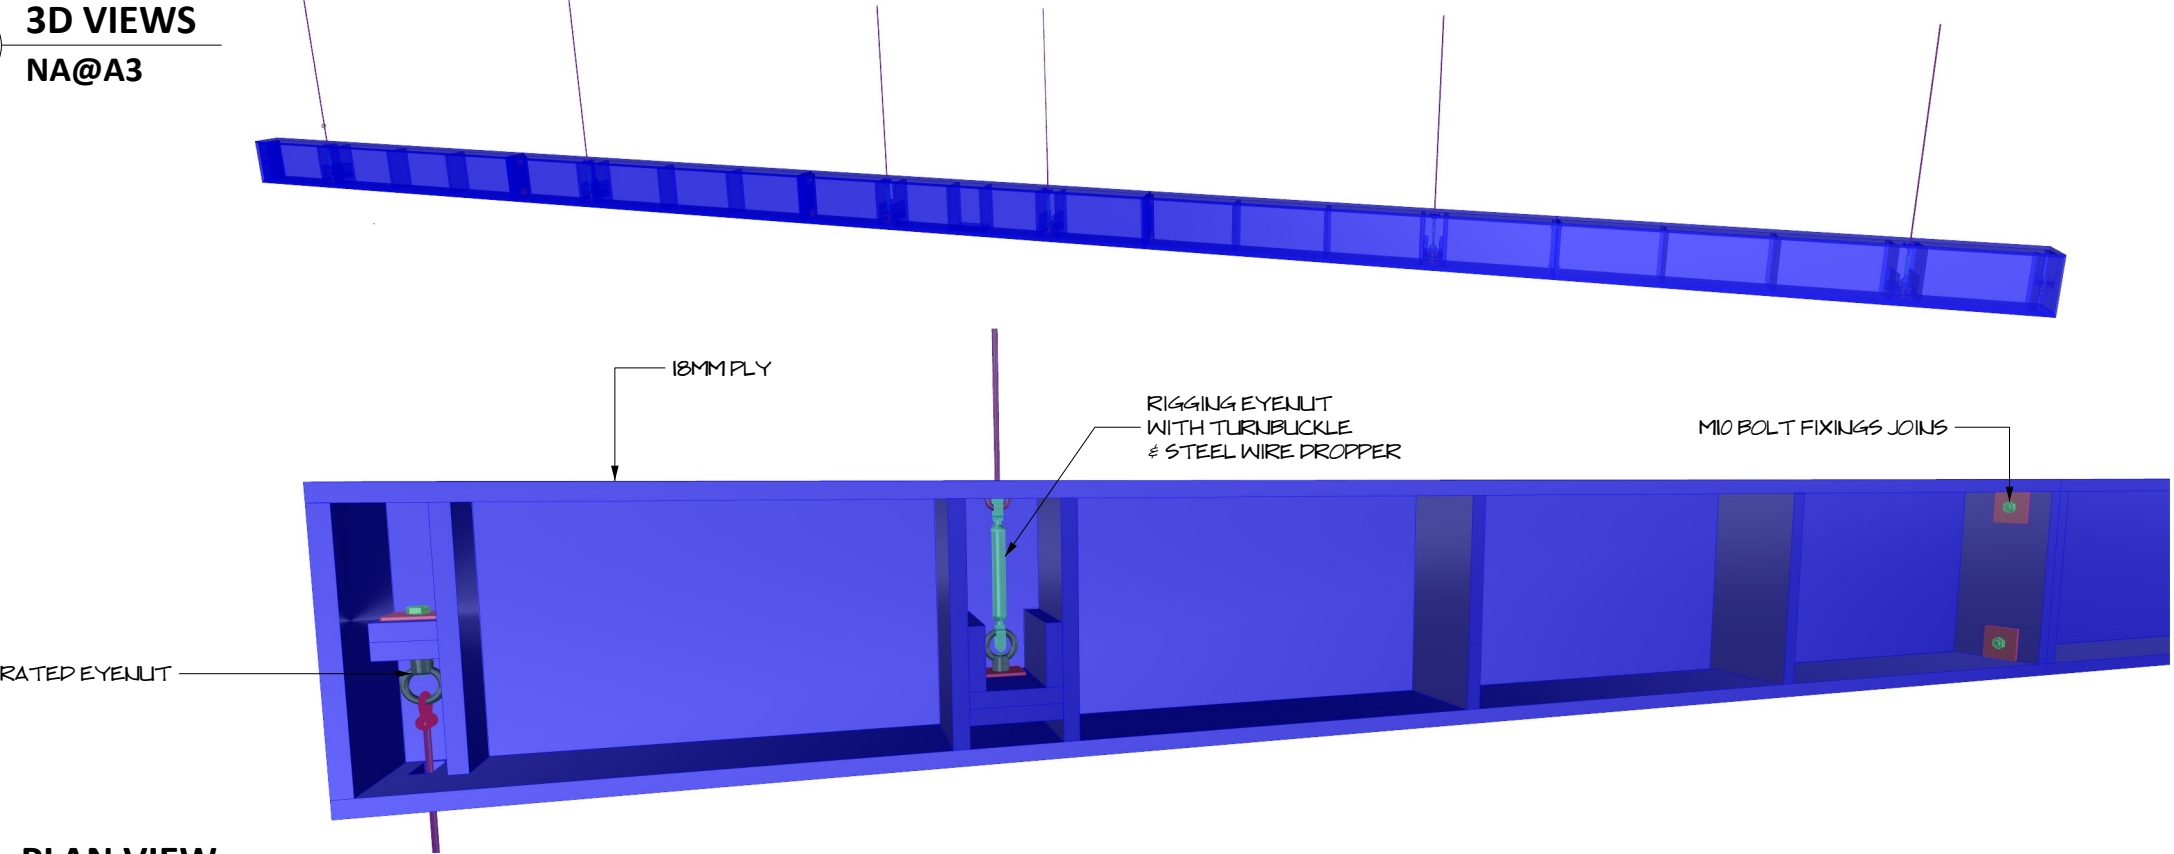

CONSTRUCTION DETAILS
MAKE 1 X ITEM AS SHOWN.


CONSTRUCTED FROM 18MM SELEX PLY
CNC CUT TO SHAPE.
PVA GLUE, BRAD NAIL & SCREW FIXING
ASSEMBLY.

BOLT FIX HEADER SECTIONS TOGETHER
WITH 2 X 50MM M10 BOLTS PER JOIN.


RIGGING DETAILS - 6 X RATED M10
EYENLITS WITH M10 BOLTS TO SUIT. 6 X
JAW-JAW TURNBUCKLES WITH 6 X 1M LONG
6MM BLACK STEEL WIRE DROPPERS WITH
RATED SHACKLE. DROPPER LENGTH TBC
BY PRODUCTION MANAGER. YUPPIE
STRAPS TOP RIGGING SUPPLIED BY
PRODUCTION MANAGER. 2 X RATED
EYENLITS TO PICK UP SUB HUNG ITEM C.3
ARCH AS SHOWN.

FILL SCREW HOLES ONLY. UNDERCOAT
AND SCENIC TOP COAT PAINT FINISH TO
MATCH SCENIC REFERENCES SUPPLIED BY
SET DESIGNER.

C.2 PLAN VIEW
1:30@A3

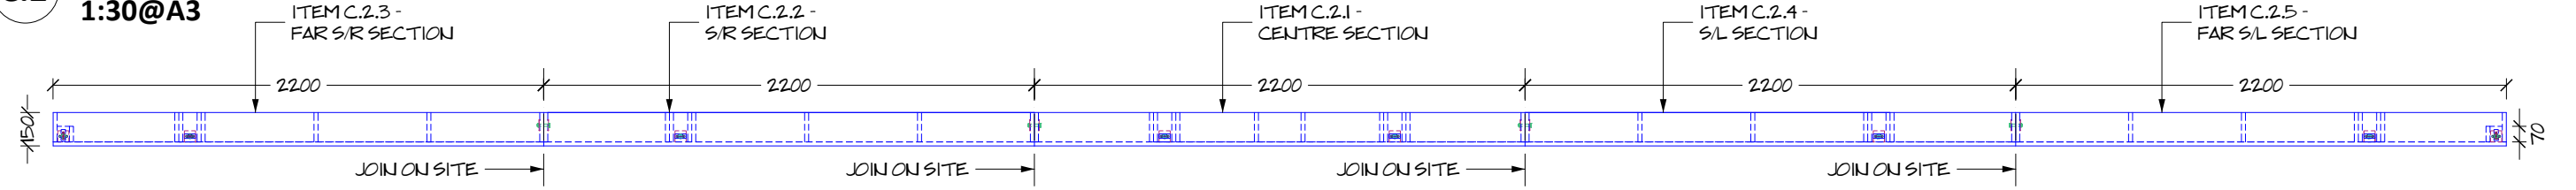

C.2 FRONT VIEW
1:30@A3

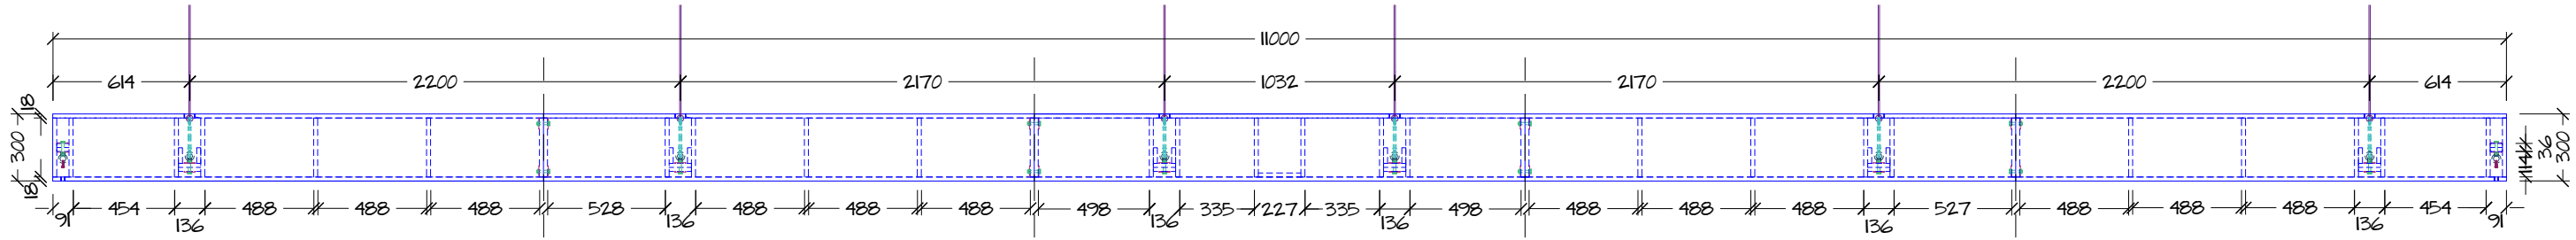

DESIGN APPROVAL

sign:.....
print name:.....
APPROVED / REVISE [circle]
comments.....
date:..... /..... /.....

CLIENT:	CENTRESTAGE
PROJECT	FROZEN
DESIGNER:	HARRY GILL
VENUE:	CIVIC THEATRE
ADDRESS:	375 HUNTER ST NEWCASTLE, NSW 2300
JOB No:	26150

DRAWING NAME:	ITEM C.2 - D/S HEADER	
DRAWN BY:	GAVIN HAMPSTEAD	
ISSUE:	DATE	DESCRIPTION
	29/07/26	ISSUE FOR COSTING & CLIENT REVIEW
	00/00/00	XXXX
	00/00/00	XXXX
	00/00/00	XXXX
	00/00/00	XXXX
	00/00/00	XXXX

FROZEN

C.3 3D VIEW
NA@A3

RIGGING EYEJOLT
WITH TURNBUCKLE
STEEL WIRE DROPPER

C.3 PLAN VIEW
1:35@A3

C.3 FRONT VIEW
1:35@A3

C.3 3D VIEW
NA@A3

18MM PLY
66X18 PINE

M10 BOLTS

5MM BENDY PLY

5MM BENDY PLY

CONSTRUCTION DETAILS



MAKE 1 X ITEM AS SHOWN.

CONSTRUCTED FROM 18MM SELEX PLY CNC CUT TO
SHAPE, 66X18 PINE FRAMING # 5MM BENDY PLY RETURN
SKINS.
PVA GLUE, BRAD NAIL # SCREW FIXING ASSEMBLY.

BOLT FIX ARCH SECTIONS TOGETHER WITH 4 X 50MM M10
BOLTS PER JOIN.

RIGGING DETAILS - 2 X RATED M10 EYEJOLTS WITH M10
BOLTS TO SUIT. 2 X JAW-JAW TURNBUCKLES WITH 2 X
3.2M LONG 6MM BLACK STEEL WIRE DROPPERS WITH
RATED SHACKLE. DROPPER LENGTH TBC BY DESIGNER
WITH TURNBUCKLE SPECIFIED BY RIGGER IS CONFIRMED.
YUPPIE STRAPS TOP RIGGING SUPPLIED BY
PRODUCTION MANAGER.

FILL SCREW HOLES ONLY. UNDERCOAT AND SCENIC TOP
COAT PAINT FINISH TO MATCH SCENIC REFERENCES
SUPPLIED BY SET DESIGNER.

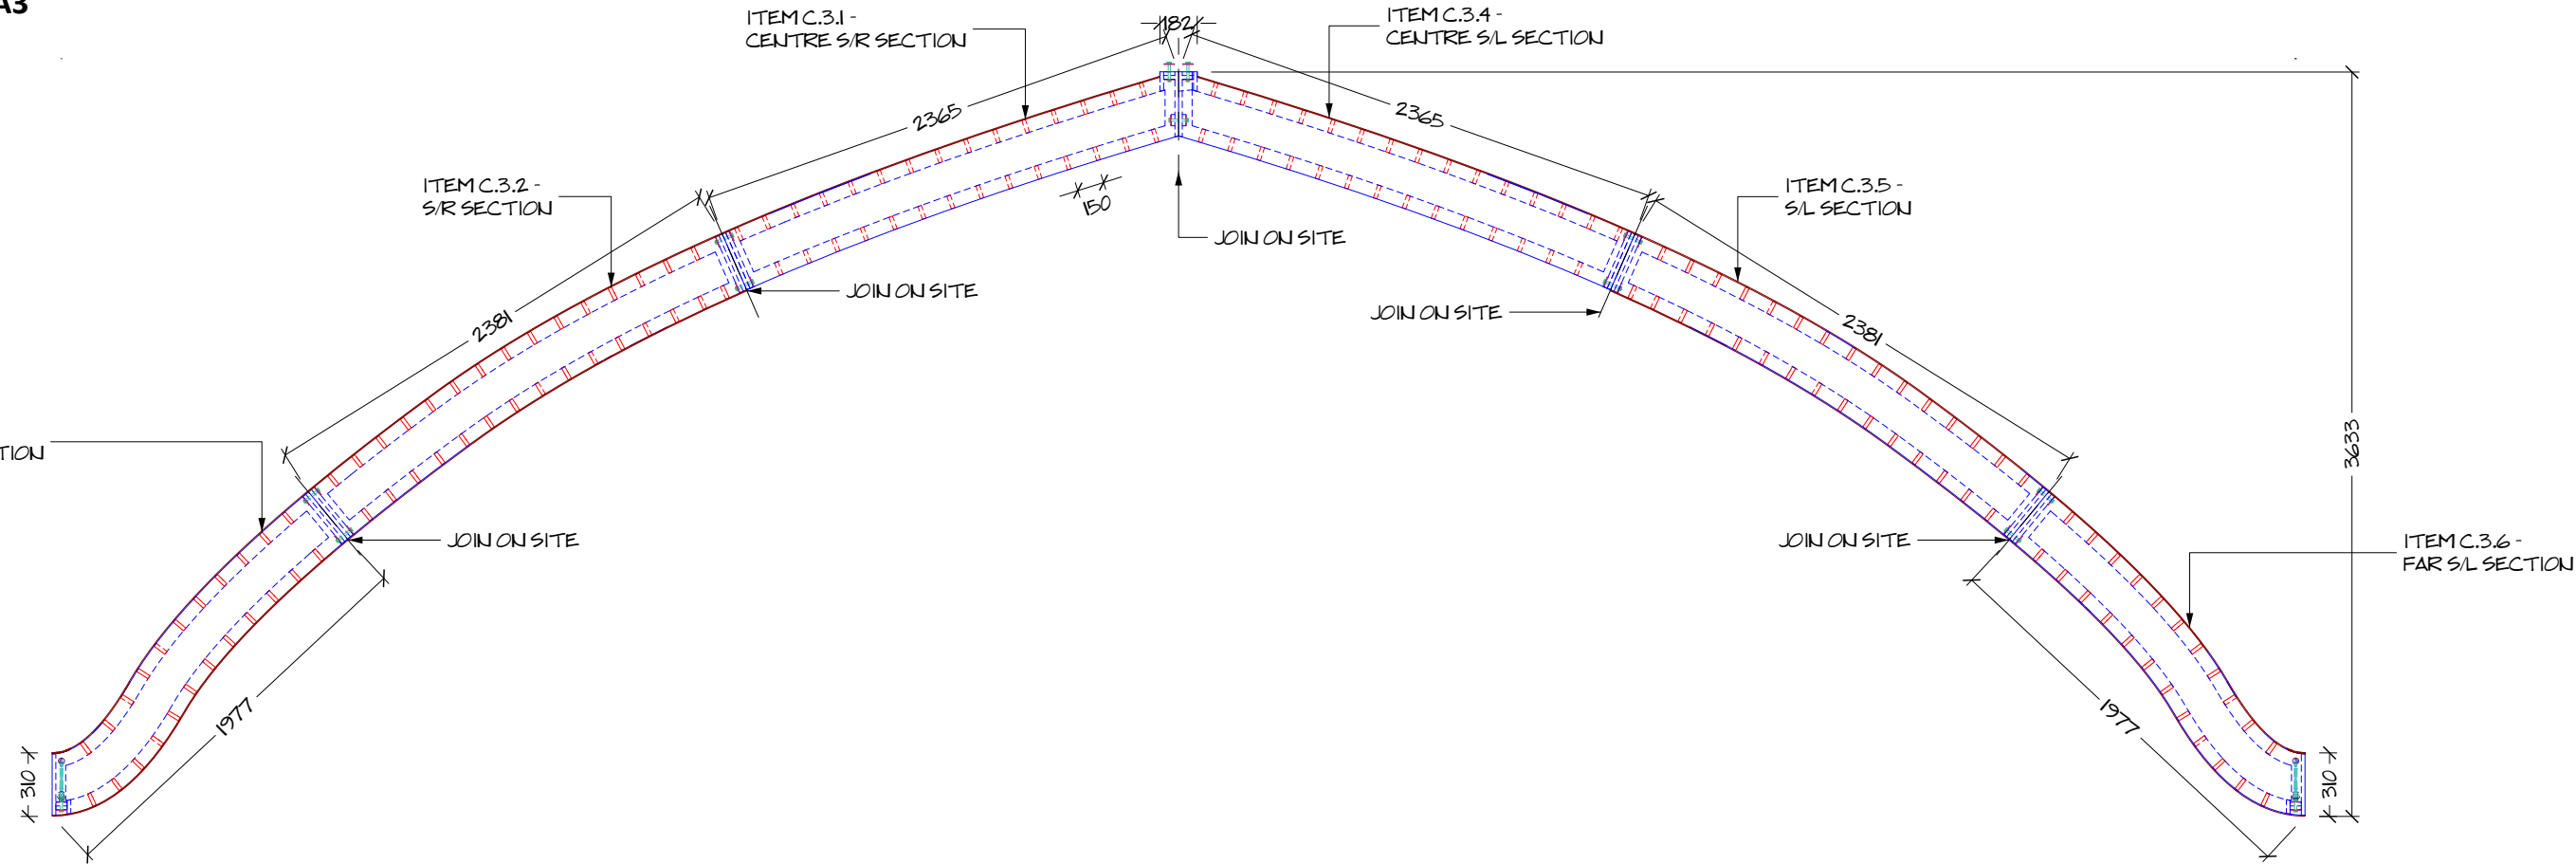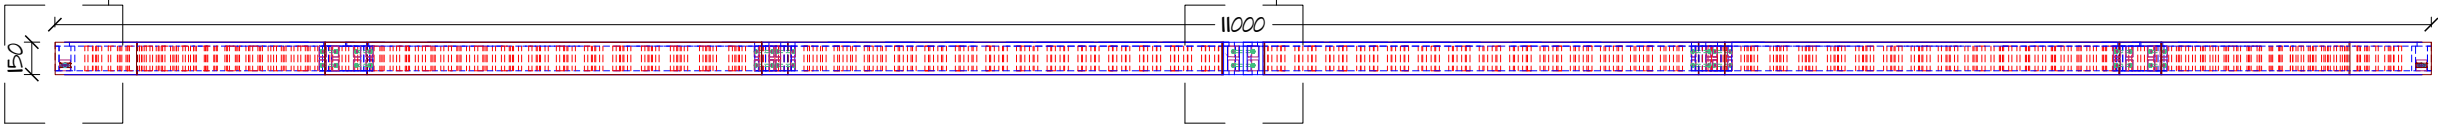


iceworks
design

ICEWORKS DESIGN PTY. LTD.
5/747 Fairfield Rd, Yeerongpilly, QLD. 4105
PO Box 624, Fairfield Gardens, QLD. 4103
T: + 617 3352 4511
www.iceworksdesign.com

Centre/Stage

THESE DRAWINGS ARE CONCEPT & DESIGN ONLY.
FURTHER CONSTRUCTION & DETAIL DRAWINGS
MAY BE REQUIRED.

These drawings are © copyright 2025 ICEWORKS DESIGN.
Drawings, illustrations & 3D Renders are not to be used,
reproduced or copied without permission from ICEWORKS DESIGN.
All dimensions are to be checked on site prior to commencing any
construction, if in doubt please contact ICEWORKS DESIGN. Do
not scale from
drawings. Any building work is to comply with the building act,
BCA and standard regulations where applicable.

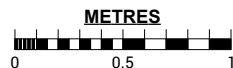

DESIGN APPROVAL

sign:.....

print name:.....

APPROVED / REVISE [circle]

comments:.....

date:..... /..... /.....

CLIENT: CENTRESTAGE

PROJECT: FROZEN

DESIGNER: HARRY GILL

VENUE: CIVIC THEATRE

ADDRESS: 375 HUNTER ST
NEWCASTLE, NSW 2300

JOB No: 26150

DRAWING
NAME:

ITEM C.3 - D/S ARCH

DRAWN BY:

GAVIN HAMPSTEAD

ISSUE:

DATE DESCRIPTION

29/07/26 ISSUE FOR COSTING & CLIENT REVIEW

00/00/00 XXXX

00/00/00 XXXX

00/00/00 XXXX

00/00/00 XXXX




SCALE: 1:35 @ A3

DWG
No:

D05

SHEET
No:

6 / 7

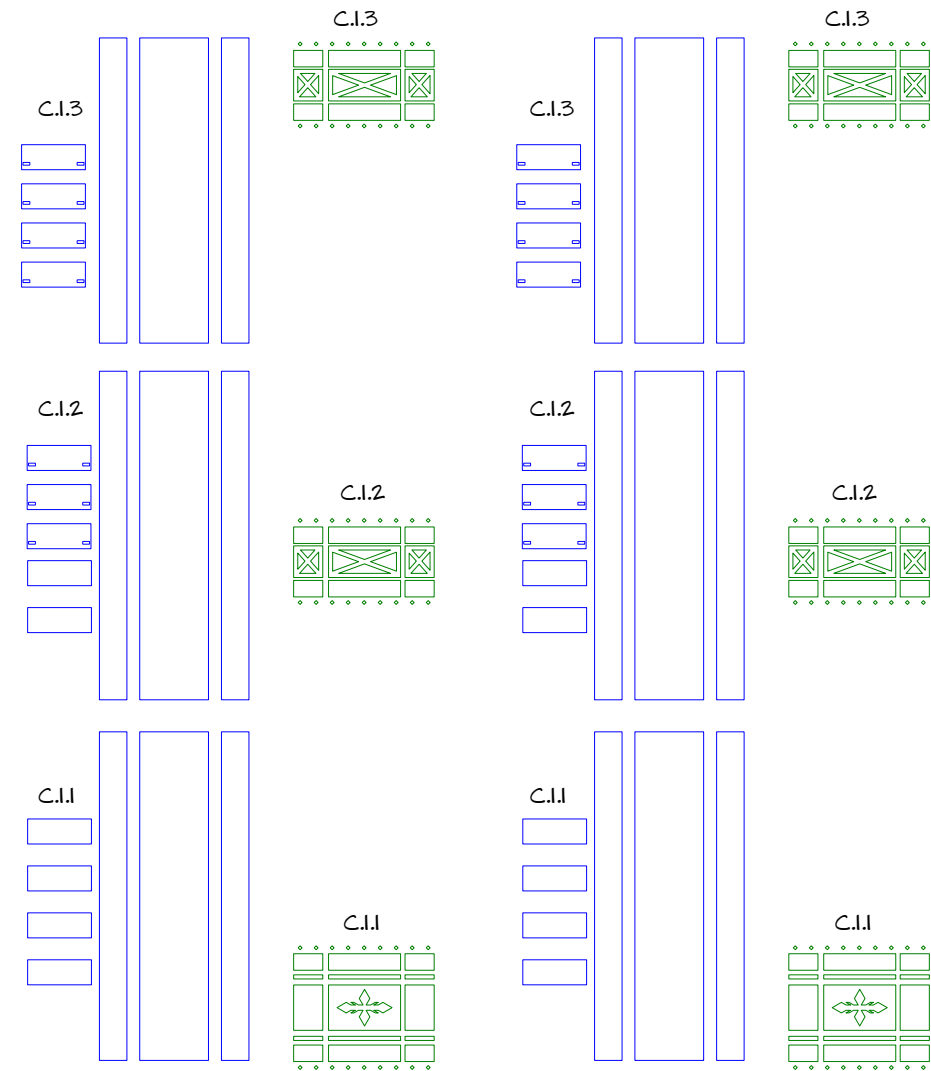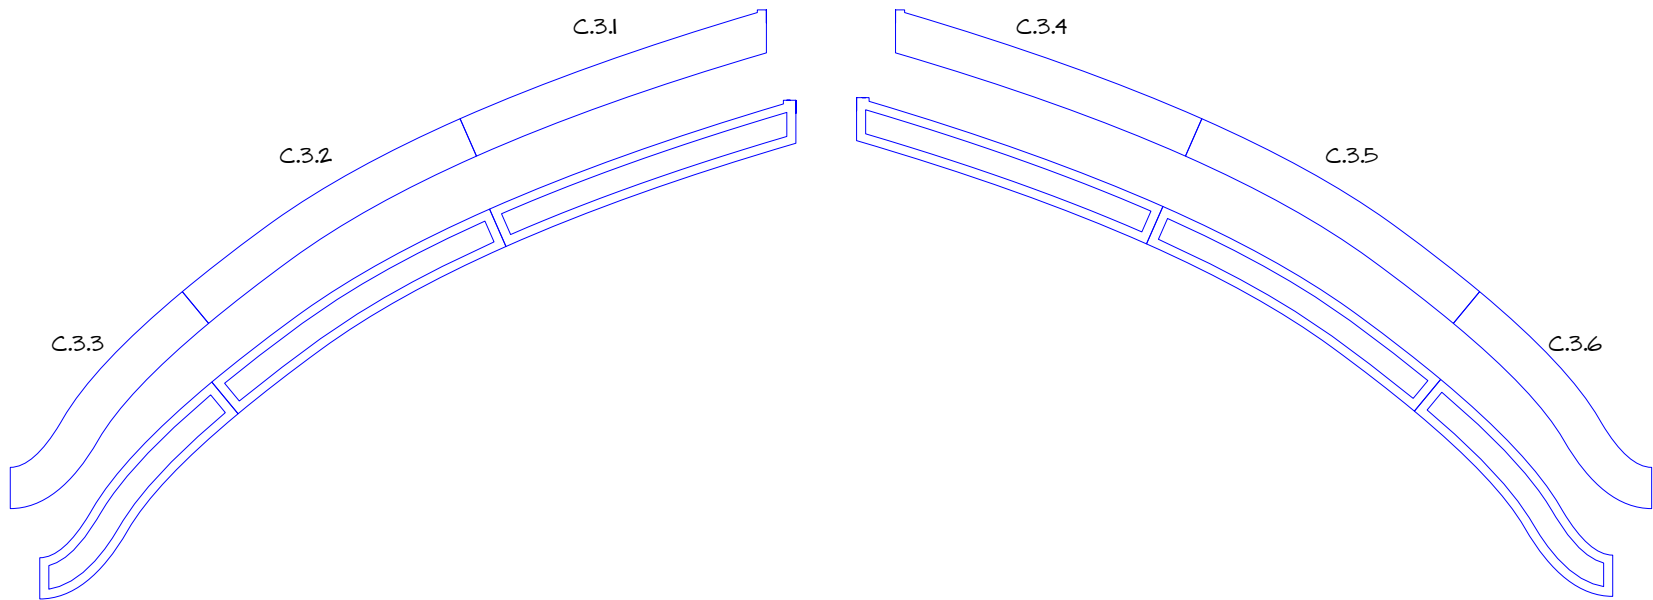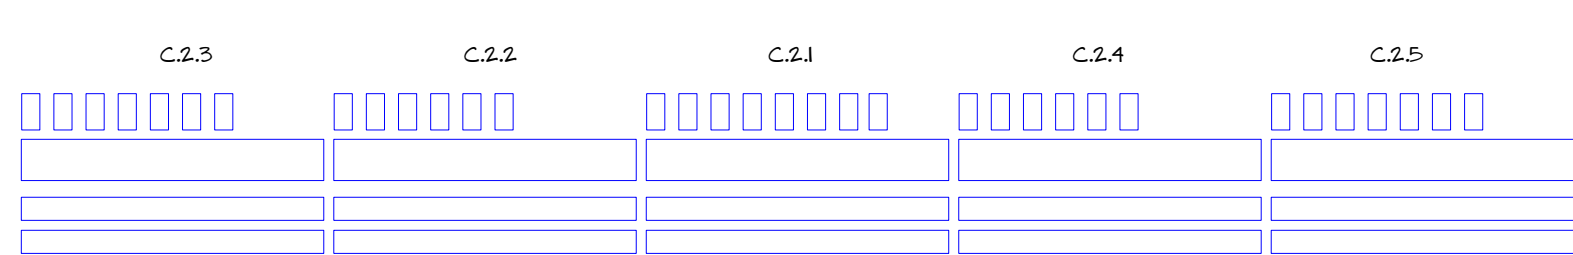

ICEWORKS DESIGN PTY. LTD.
5/747 Fairfield Rd, Yeerongpilly, QLD. 4105
PO Box 624, Fairfield Gardens, QLD. 4103
T: + 617 3352 4511
www.iceworksdesign.com

Centre/Stage

THESE DRAWINGS ARE CONCEPT & DESIGN ONLY.
FURTHER CONSTRUCTION & DETAIL DRAWINGS
MAY BE REQUIRED.

These drawings are © copyright 2025 ICEWORKS DESIGN.
Drawings, illustrations & 3D Renders are not to be used,
reproduced or copied without permission from ICEWORKS DESIGN.
All dimensions are to be checked on site prior to commencing any
construction, if in doubt please contact ICEWORKS DESIGN. Do
not scale from
drawings. Any building work is to comply with the building act,
BCA and standard regulations where applicable.

DESIGN APPROVAL

sign:.....

print name:.....

APPROVED / REVISE [circle]

comments.....

date:..... /..... /.....

CLIENT: CENTRESTAGE

PROJECT: FROZEN

DESIGNER: HARRY GILL

VENUE: CIVIC THEATRE

ADDRESS: 375 HUNTER ST
NEWCASTLE, NSW 2300

JOB No: 26150

DRAWING
NAME:

ITEM C.1-C.3 - CNC FILES

DRAWN BY:

GAVIN HAMPSTEAD

ISSUE:

DATE DESCRIPTION

29/07/26 ISSUE FOR COSTING & CLIENT REVIEW

00/00/00 XXXX

00/00/00 XXXX

00/00/00 XXXX

00/00/00 XXXX

00/00/00 XXXX

SCALE: NTS @ A3

DWG
No:

D06

SHEET
No:

7 / 7