

SHEET#	DWG#	DRAWING NAME																									
1	CP	COVER PAGE																									
2	D01	RENDERED VIEWS																									
3	D02	ITEM E.1 - S/R BEDROOM TRUCK ASSEMBLED																									
4	D03	ITEM E.1.1 - ROLLING TRUCK																									
5	D04	ITEM E.1.2 - OFF STAGE FLAT																									
6	D05	ITEM E.1.3 - REAR FLAT																									
7	D06	ITEM E.1.4 - ARCHES																									
8	D07	ITEM E.3 - BEDS X 2																									
9	D08	ITEM E.4 - FIREPLACE																									
10	D09	CNC FILES																									
			Centre / Stage FROZEN ITEM E - BEDROOM TRUCKS CONSTRUCTION DESIGN PLAN SET V3 04/08/26																								
iceworks design ICEWORKS DESIGN PTY. LTD. 5/747 Fairfield Rd, Yeerongpilly, QLD. 4105 PO Box 624, Fairfield Gardens, QLD. 4103 T: + 617 3352 4511 www.iceworksdesign.com Centre / Stage THESE DRAWINGS ARE CONCEPT & DESIGN ONLY. FURTHER CONSTRUCTION & DETAIL DRAWINGS MAY BE REQUIRED. These drawings are © copyright 2025 ICEWORKS DESIGN. Drawings, illustrations & 3D Renders are not to be used, reproduced or copied without permission from ICEWORKS DESIGN. All dimensions are to be checked on site prior to commencing any construction, if in doubt please contact ICEWORKS DESIGN. Do not scale from drawings. Any building work is to comply with the building act, BCA and standard regulations where applicable.			DESIGN APPROVAL sign:..... print name:..... APPROVED / REVISE [circle] comments..... date:..... /..... /.....			CLIENT: CENTRESTAGE PROJECT: FROZEN DESIGNER: HARRY GILL VENUE: CIVIC THEATRE ADDRESS: 375 HUNTER ST NEWCASTLE, NSW 2300 JOB No: 26150		DRAWING NAME: COVER PAGE DRAWN BY: GAVIN HAMPSTEAD ISSUE: <table><tr><th>DATE</th><th>DESCRIPTION</th></tr><tr><td>31/07/26</td><td>ISSUE FOR COSTING & CLIENT REVIEW</td></tr><tr><td>03/08/26</td><td>REVISED. ISSUE FOR COSTING & CLIENT REVIEW</td></tr><tr><td>04/08/26</td><td>REVISED. ISSUE FOR COSTING & CLIENT REVIEW</td></tr><tr><td>00/00/00</td><td>XXXX</td></tr><tr><td>00/00/00</td><td>XXXX</td></tr><tr><td>00/00/00</td><td>XXXX</td></tr></table>			DATE	DESCRIPTION	31/07/26	ISSUE FOR COSTING & CLIENT REVIEW	03/08/26	REVISED. ISSUE FOR COSTING & CLIENT REVIEW	04/08/26	REVISED. ISSUE FOR COSTING & CLIENT REVIEW	00/00/00	XXXX	00/00/00	XXXX	00/00/00	XXXX	SCALE: N/A @ A3	DWG No: CP	SHEET No: 1 / 10
DATE	DESCRIPTION																										
31/07/26	ISSUE FOR COSTING & CLIENT REVIEW																										
03/08/26	REVISED. ISSUE FOR COSTING & CLIENT REVIEW																										
04/08/26	REVISED. ISSUE FOR COSTING & CLIENT REVIEW																										
00/00/00	XXXX																										
00/00/00	XXXX																										
00/00/00	XXXX																										

ITEM E.1 - S/R BEDROOM TRUCK



ITEM E.2 - S/L BEDROOM TRUCK



iceworks
design

ICEWORKS DESIGN PTY. LTD.
5/747 Fairfield Rd, Yeerongpilly, QLD. 4105
PO Box 624, Fairfield Gardens, QLD. 4103
T: + 617 3352 4511
www.iceworksdesign.com

Centre/Stage

THESE DRAWINGS ARE CONCEPT & DESIGN ONLY.
FURTHER CONSTRUCTION & DETAIL DRAWINGS
MAY BE REQUIRED.

These drawings are © copyright 2025 ICEWORKS DESIGN.
Drawings, illustrations & 3D Renders are not to be used,
reproduced or copied without permission from ICEWORKS DESIGN.
All dimensions are to be checked on site prior to commencing any
construction, if in doubt please contact ICEWORKS DESIGN. Do
not scale from
drawings. Any building work is to comply with the building act,
BCA and standard regulations where applicable.

DESIGN APPROVAL

sign:.....

print name:.....

APPROVED / REVISE [circle]

comments.....

date:..... /..... /.....

CLIENT:	CENTRESTAGE
PROJECT	FROZEN
DESIGNER:	HARRY GILL
VENUE:	CIVIC THEATRE
ADDRESS:	375 HUNTER ST NEWCASTLE, NSW 2300
JOB No:	26150

DRAWING NAME:	RENDERED VIEWS	
DRAWN BY:	GAVIN HAMPSTEAD	
ISSUE:	DATE	DESCRIPTION
	31/07/26	ISSUE FOR COSTING & CLIENT REVIEW
	03/08/26	REVISED. ISSUE FOR COSTING & CLIENT REVIEW
	04/08/26	REVISED. ISSUE FOR COSTING & CLIENT REVIEW
	00/00/00	XXXX
	00/00/00	XXXX
	00/00/00	XXXX

SCALE: 1:100 @ A3

DWG No:


D01

SHEET No:

2 / 10

FROZEN

E.1 PLAN VIEW
1:25@A3

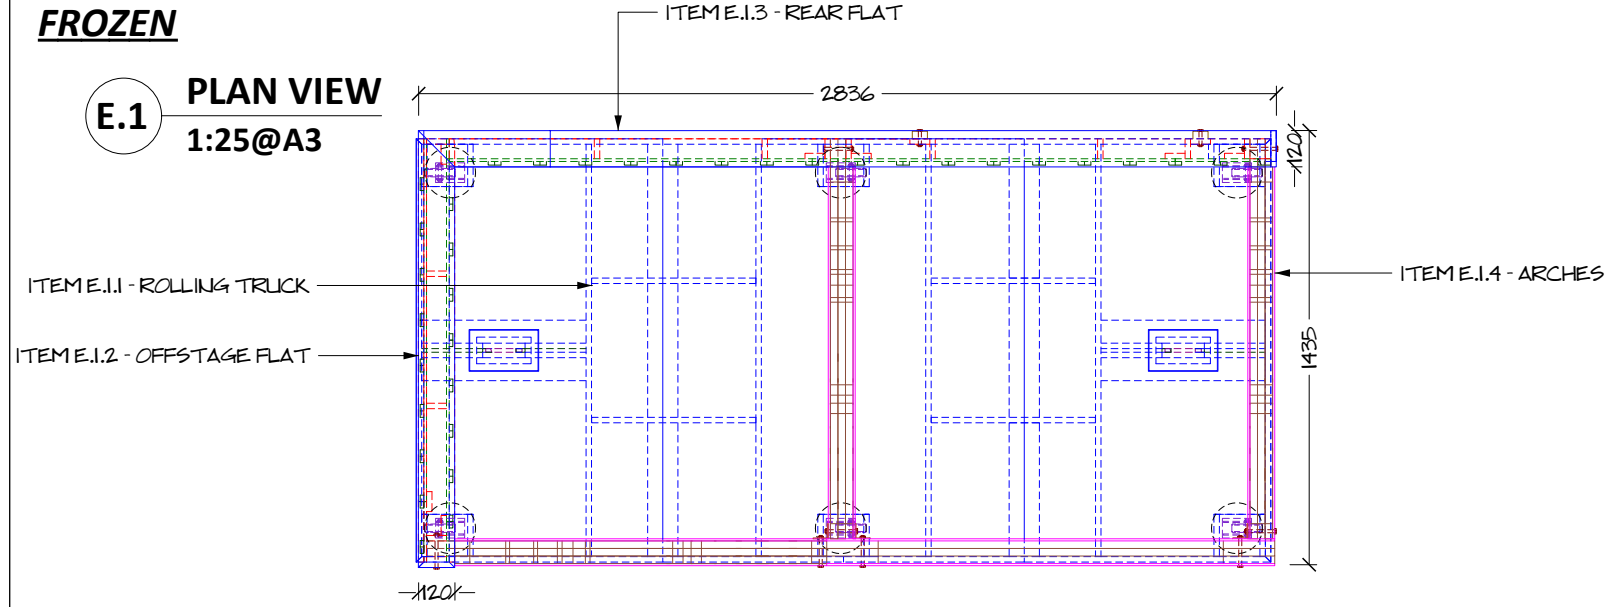


CONSTRUCTION DETAILS

MAKE 2 X ITEMS TOTAL -


1 X S/R BEDROOM TRUCK AS PER PLANS.

1 X S/L BEDROOM TRUCK - FLIP PLANS LEFT TO RIGHT.


E.1 FRONT VIEW
1:25@A3

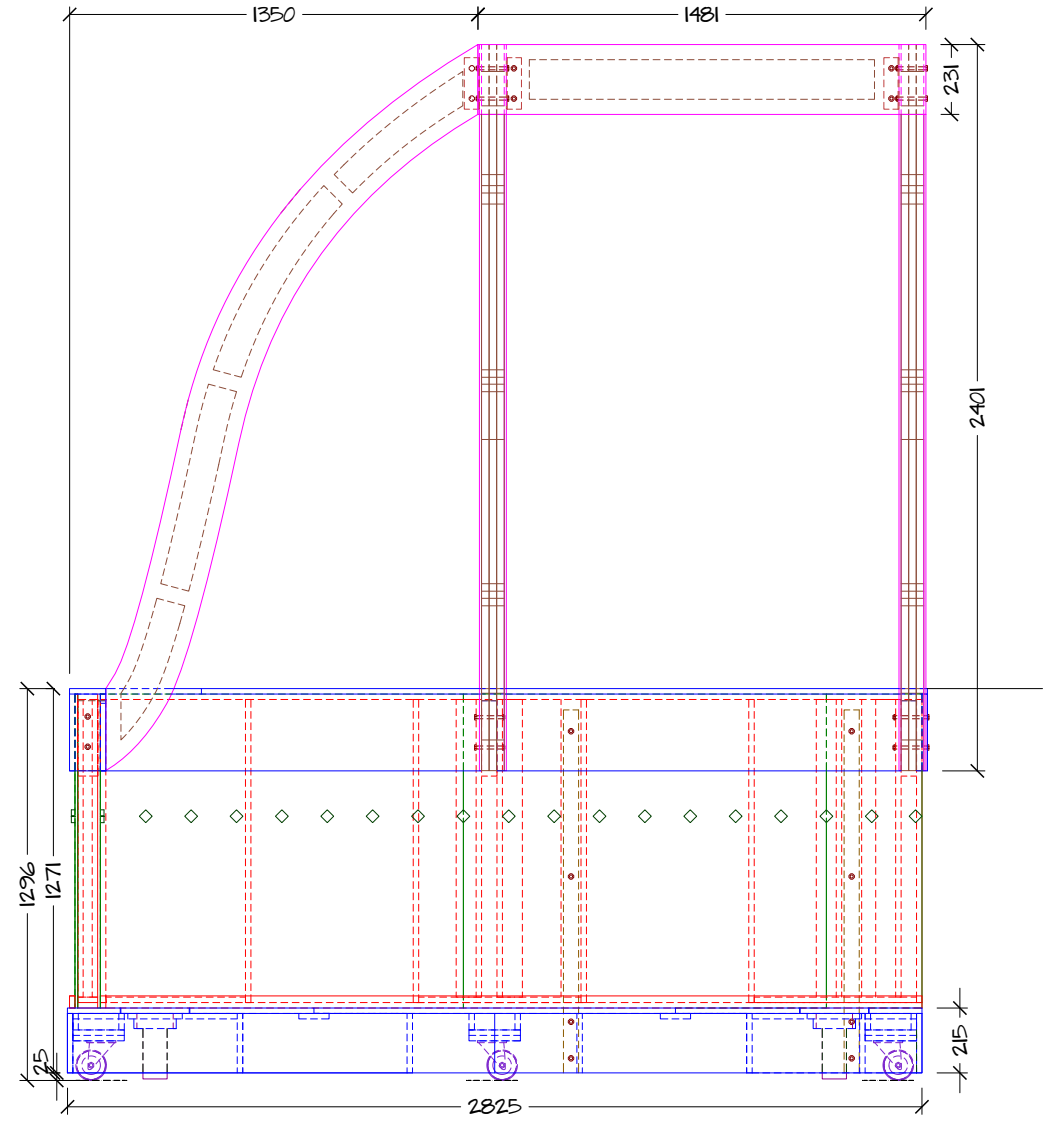

E.1 END VIEW
1:25@A3

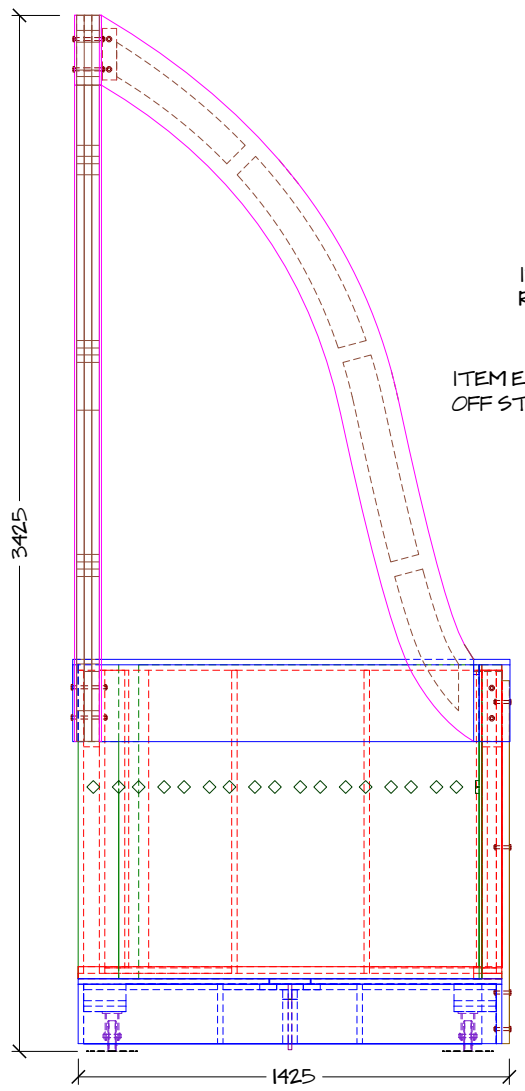

E.1 3D VIEW
NA@A3

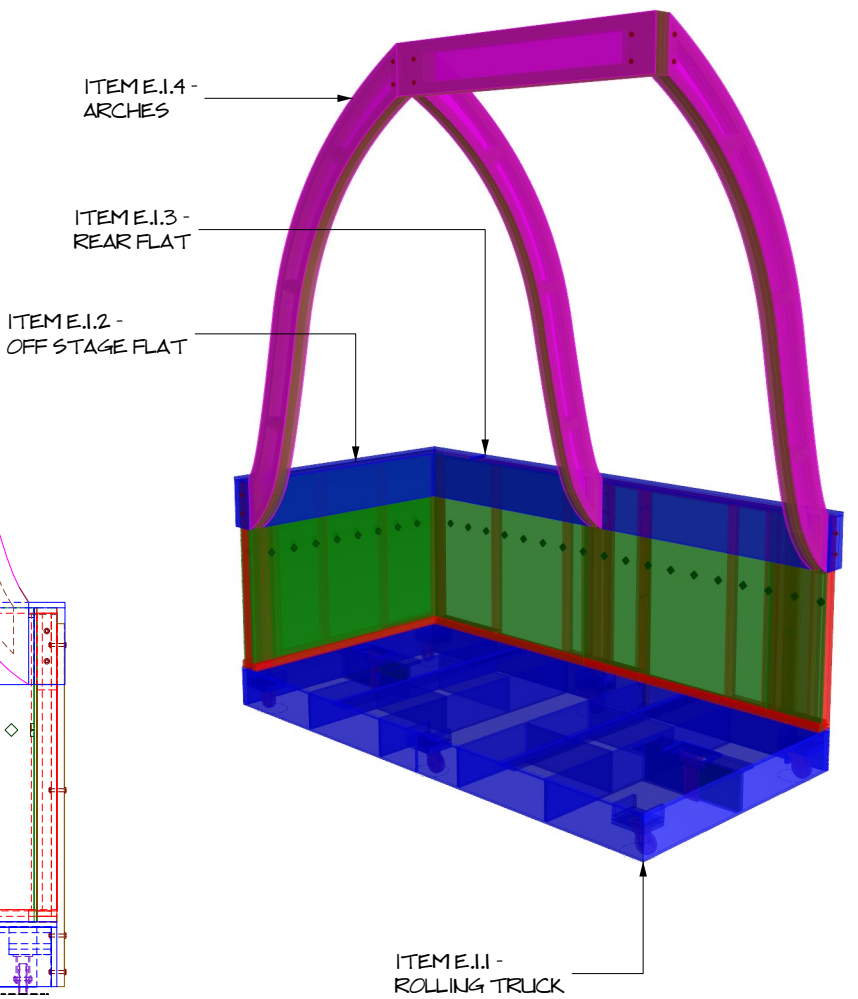


iceworks
design

ICEWORKS DESIGN PTY. LTD.
5/747 Fairfield Rd, Yeerongpilly, QLD. 4105
PO Box 624, Fairfield Gardens, QLD. 4103
T: + 617 3352 4511
www.iceworksdesign.com

Centre/Stage

THESE DRAWINGS ARE CONCEPT & DESIGN ONLY.
FURTHER CONSTRUCTION & DETAIL DRAWINGS
MAY BE REQUIRED.

These drawings are © copyright 2025 ICEWORKS DESIGN.
Drawings, illustrations & 3D Renders are not to be used,
reproduced or copied without permission from ICEWORKS DESIGN.
All dimensions are to be checked on site prior to commencing any
construction, if in doubt please contact ICEWORKS DESIGN. Do
not scale from
drawings. Any building work is to comply with the building act,
BCA and standard regulations where applicable.

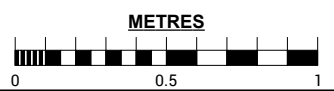

DESIGN APPROVAL

sign:.....

print name:.....

APPROVED / REVISE [circle]

comments:.....


date:..... /..... /.....

CLIENT:	CENTRESTAGE
PROJECT	FROZEN
DESIGNER:	HARRY GILL
VENUE:	CIVIC THEATRE
ADDRESS:	375 HUNTER ST NEWCASTLE, NSW 2300
JOB No:	26150

DRAWING NAME:	ITEM E.1 - S/R BEDROOM TRUCK ASSEMBLED	
DRAWN BY:	GAVIN HAMPSTEAD	
ISSUE:	DATE	DESCRIPTION
	31/07/26	ISSUE FOR COSTING & CLIENT REVIEW
	03/08/26	REVISED. ISSUE FOR COSTING & CLIENT REVIEW
	04/08/26	REVISED. ISSUE FOR COSTING & CLIENT REVIEW
	00/00/00	XXXX
	00/00/00	XXXX
	00/00/00	XXXX

SCALE:	1:25@A3
DWG No:	D02
SHEET No:	3 / 10

E.1.1 3D VIEW
NA@A3

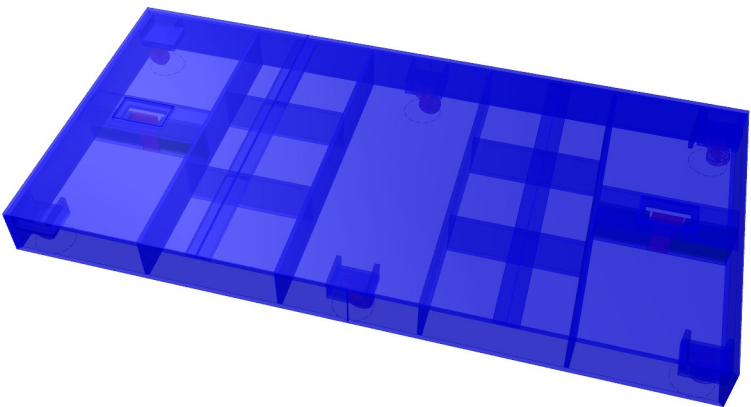

RICHMOND S4362
100MM BLACK CASTOR
WHEEL.



CONSTRUCTION DETAILS


CONSTRUCTED FROM 18MM SELEX PLY, PVA GLUE, BRAD NAIL & SCREW
FIXING ASSEMBLY. MOUNT 6 X SWIVEL CASTORS WITH M8 BOLTS.
CASTOR SPECIFICATION - RICHMOND S4362 100MM BLACK CASTOR WHEEL.

GUIDE KNIVES X 2 CONSTRUCTED FROM 12MM UHDPE CUT TO
SHAPE. MAKE ACCESS HATCHES IN TRUCK TOP TO INSTALL & REMOVE
GUIDE KNIVES FROM TRUCK. SCREW FIX ACCESS HATCHES TO LOCK
KNIVES IN POSITION.


TRUCK KNIVES SUPPORT FRAMES CONSTRUCTED FROM 18MM PLY &
12MM PLY. ADD IMPACKER TO 12MM PLY TO ALLOW 12MM UHDPE KNIVES
TO SLIDE IN & OUT. SET KNIVES 5MM ABOVE FLOOR LEVEL TO LOCATE
INTO 16X16X1.6MM ALUMINIUM U-CHANNEL GUIDE TRACK SET INTO SHOW
FLOOR.

FILL SCREW HOLES ONLY. UNDERCOAT AND TOP COAT SCENIC PAINT
FINISH TO MATCH SCENIC REFERENCES SUPPLIED BY SET DESIGNER.
FIRE RETARD PAINT ADDITIVE INCLUDED IN UNDERCOAT PAINT.


E.1.1 PLAN VIEW
1:15@A3

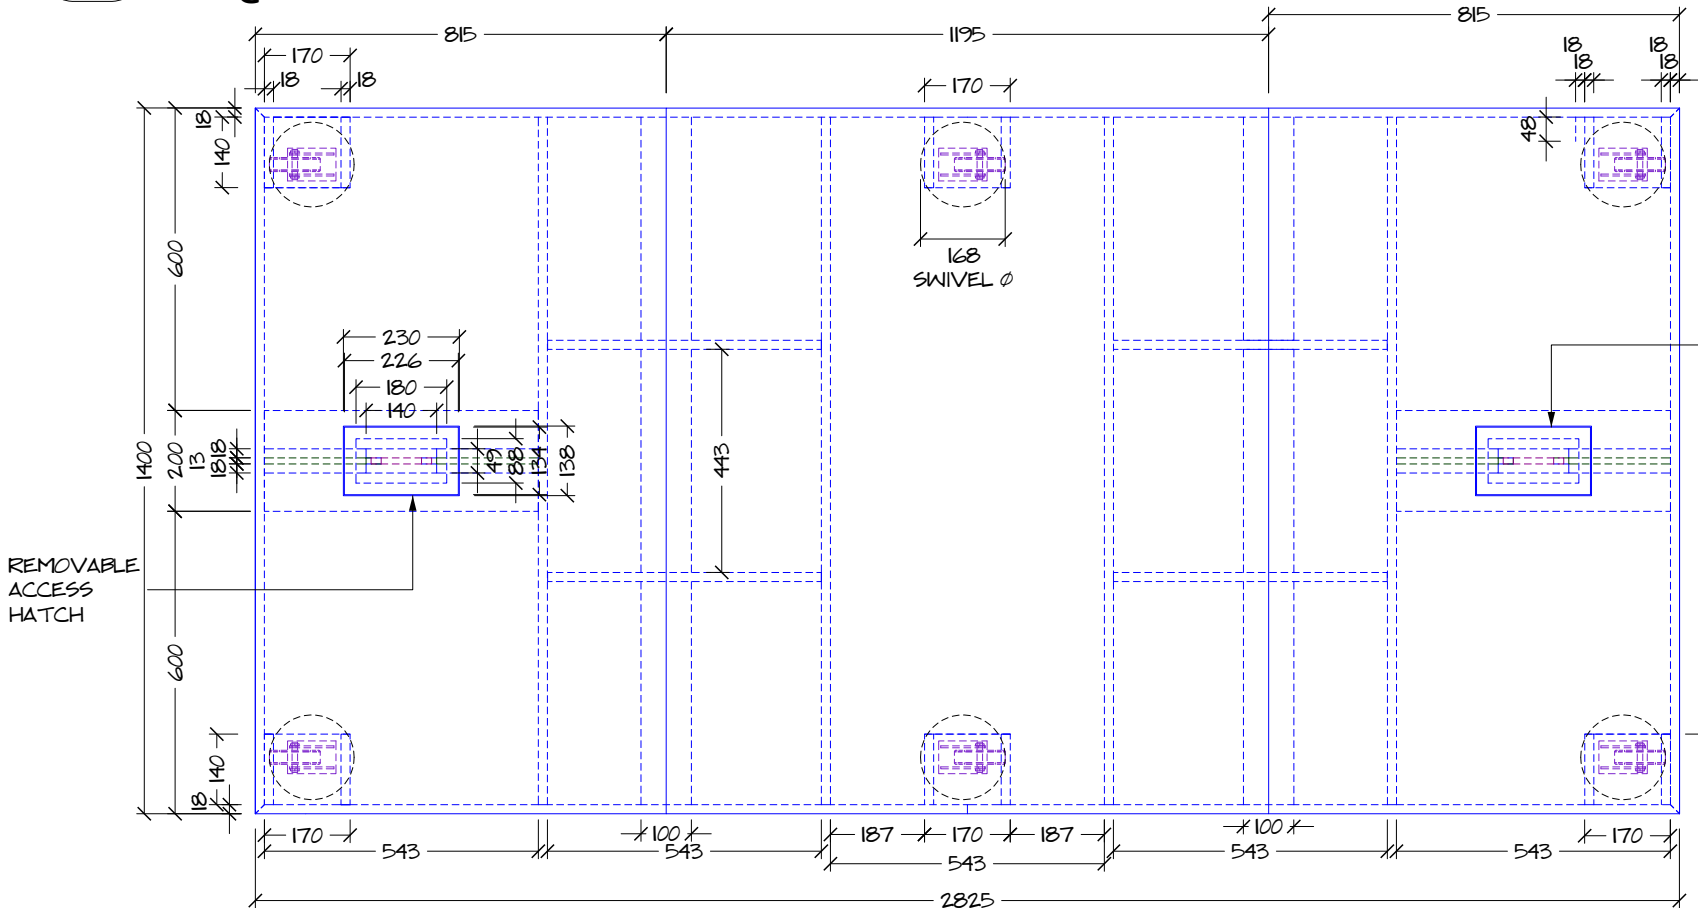


E.1.1 3D VIEW
NA@A3

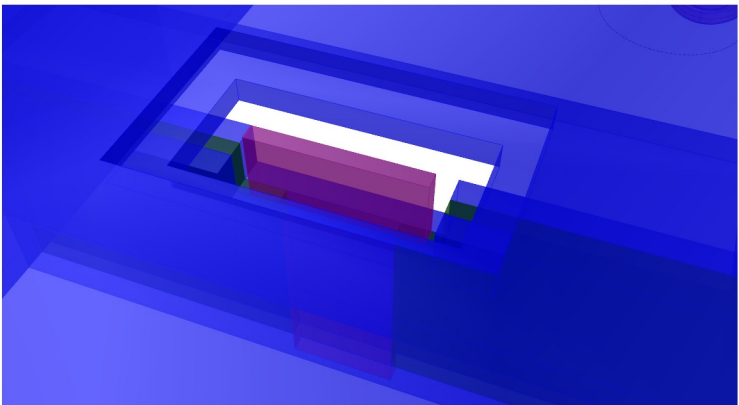


E.1.1 3D VIEW
NA@A3

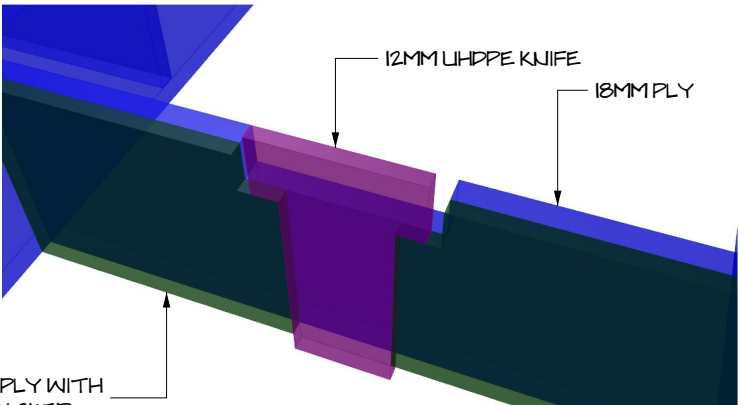

E.1.1 FRONT VIEW
1:15@A3

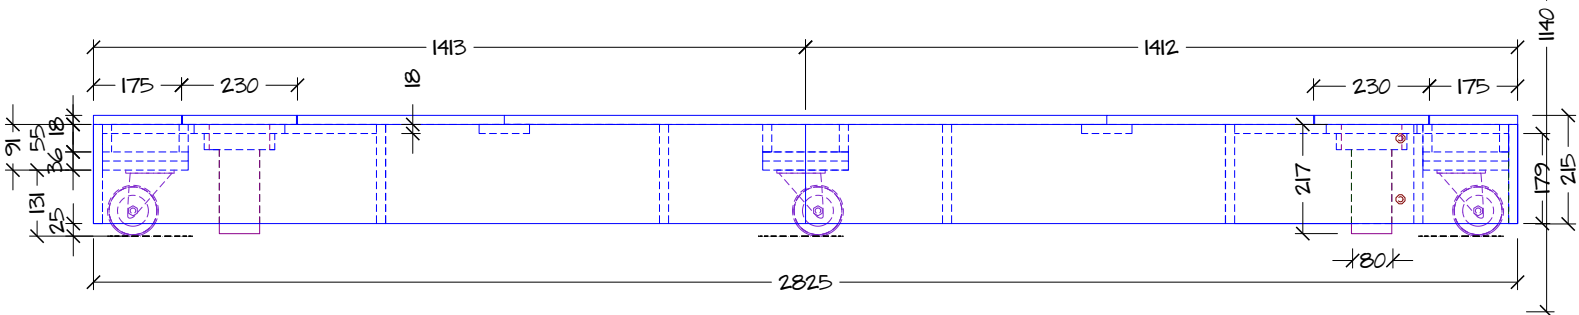

E.1.1 END VIEW
1:15@A3

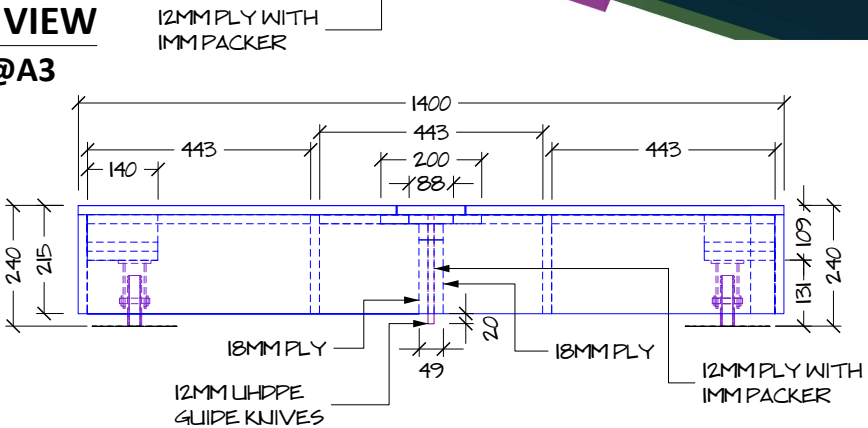


iceworks
design

ICEWORKS DESIGN PTY. LTD.
5/747 Fairfield Rd, Yeerongpilly, QLD. 4105
PO Box 624, Fairfield Gardens, QLD. 4103
T: + 617 3352 4511
www.iceworksdesign.com

Centre/Stage

THESE DRAWINGS ARE CONCEPT & DESIGN ONLY.
FURTHER CONSTRUCTION & DETAIL DRAWINGS
MAY BE REQUIRED.

These drawings are © copyright 2025 ICEWORKS DESIGN.
Drawings, illustrations & 3D Renders are not to be used,
reproduced or copied without permission from ICEWORKS DESIGN.
All dimensions are to be checked on site prior to commencing any
construction, if in doubt please contact ICEWORKS DESIGN. Do
not scale from
drawings. Any building work is to comply with the building act,
BCA and standard regulations where applicable.

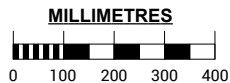

DESIGN APPROVAL

sign:.....

print name:.....

APPROVED / REVISE [circle]

comments:.....

date:..... /..... /.....

CLIENT: CENTRESTAGE

PROJECT: FROZEN

DESIGNER: HARRY GILL

VENUE: CIVIC THEATRE

ADDRESS: 375 HUNTER ST
NEWCASTLE, NSW 2300

JOB No: 26150

DRAWING
NAME:

ITEM E.1.1 - ROLLING TRUCK

DRAWN BY:

GAVIN HAMPSTEAD

ISSUE:

DATE DESCRIPTION

31/07/26 ISSUE FOR COSTING & CLIENT REVIEW

03/08/26 REVISED. ISSUE FOR COSTING & CLIENT REVIEW

04/08/26 REVISED. ISSUE FOR COSTING & CLIENT REVIEW

00/00/00 XXXX

00/00/00 XXXX

00/00/00 XXXX

SCALE:

1:15@A3


DWG
No:

D03


SHEET
No:

4 / 10


E.1.2 PLAN VIEW
1:10@A3

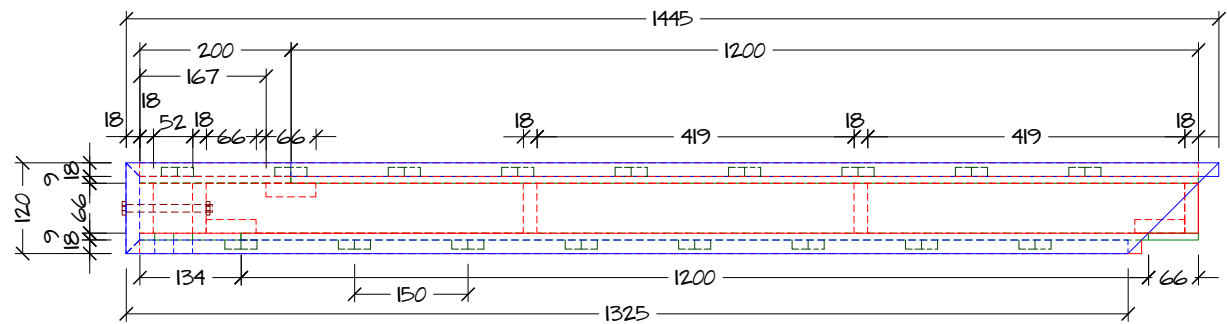


E.1.2 FRONT VIEW
1:10@A3

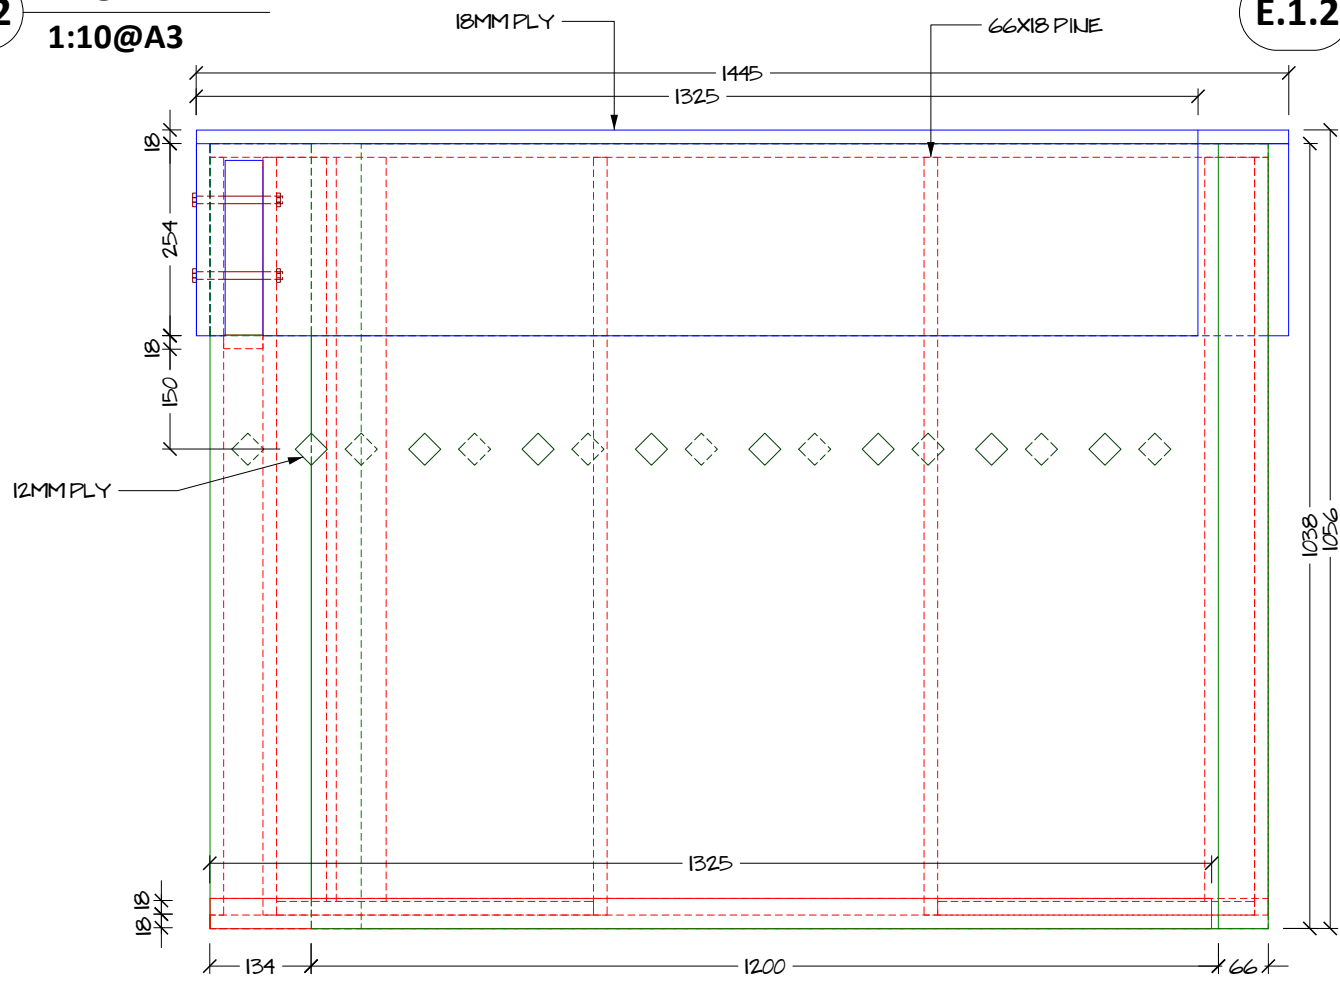


E.1.2 END VIEW
1:15@A3

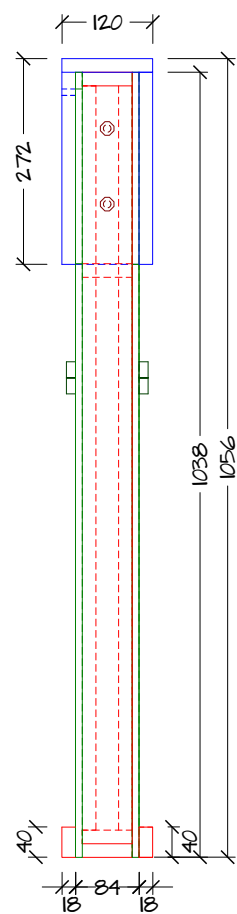

E.1.2 3D VIEW
NA@A3

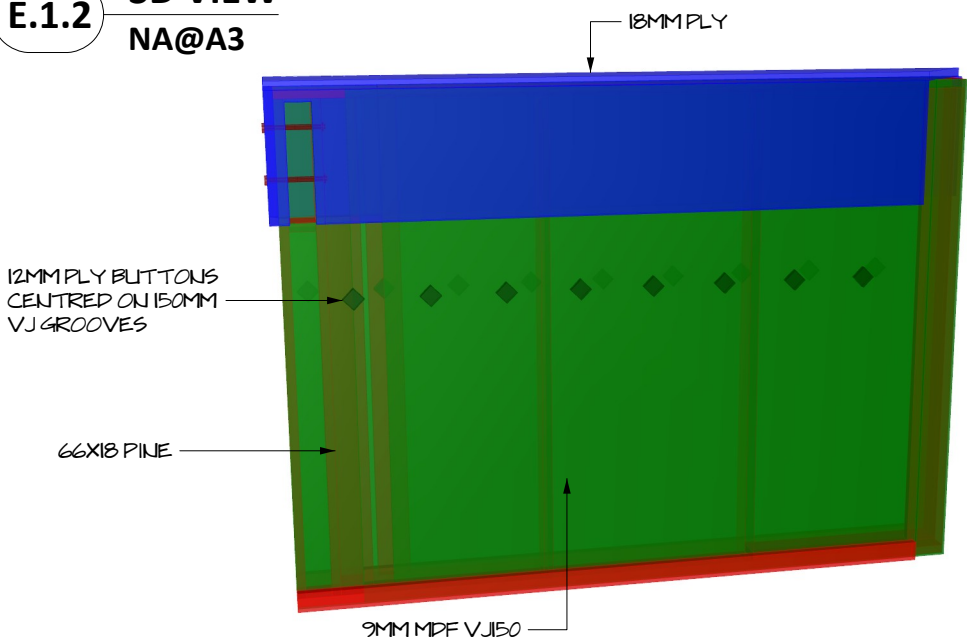

E.1.2 3D VIEW
NA@A3

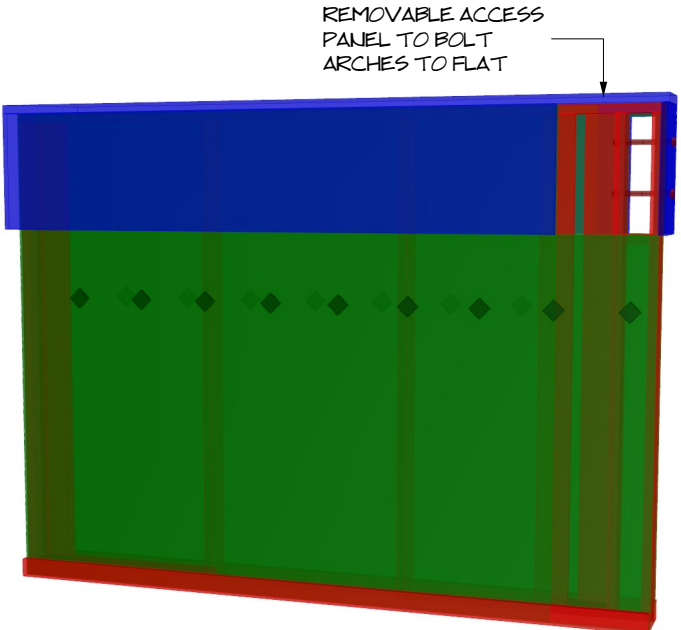

CONSTRUCTION DETAILS

CONSTRUCTED FROM 66X18 PINE FRAMING WITH 9MM MDF VJ150 FACE SKINS. 18MM PLY TOP CAPPING AS SHOWN. PVA GLUE, BRAD NAIL & SCREW FIXING ASSEMBLY.



12MM PLY PLANT ON BUTTON HEADS CENTRED ON VJ150 GROOVES.

REMOVABLE ACCESS PANEL TO BOLT ARCHES INTO FLATS.


SCREW FIX FLATS TO ROLLING TRUCK BASE WITH 104 TIMBER BATTEN SCREWS. SCREW FIX THROUGH UNDERSIDE OF ROLLING TRUCK UP INTO BOTTOM FLAT FRAMING.

FILL SCREW HOLES ONLY. UNDERCOAT AND TOP COAT SCENIC PAINT FINISH TO MATCH SCENIC REFERENCES SUPPLIED BY SET DESIGNER. FIRE RETARD PAINT ADDITIVE INCLUDED IN UNDERCOAT PAINT.


E.1.3 **3D VIEWS**
NA@A3

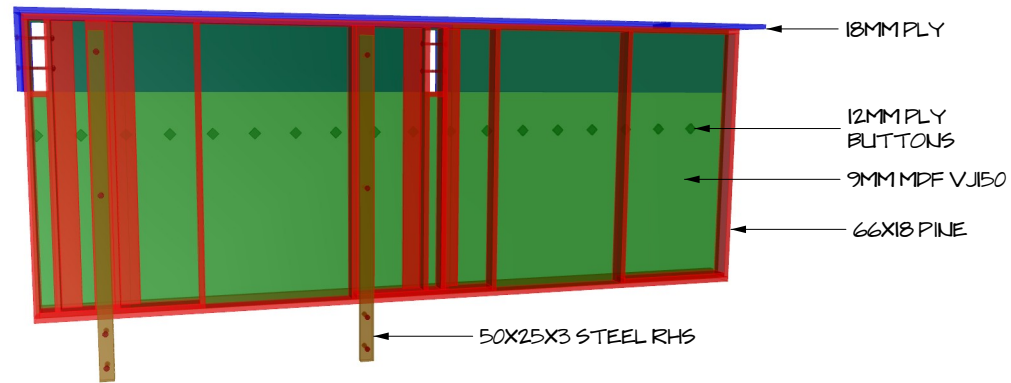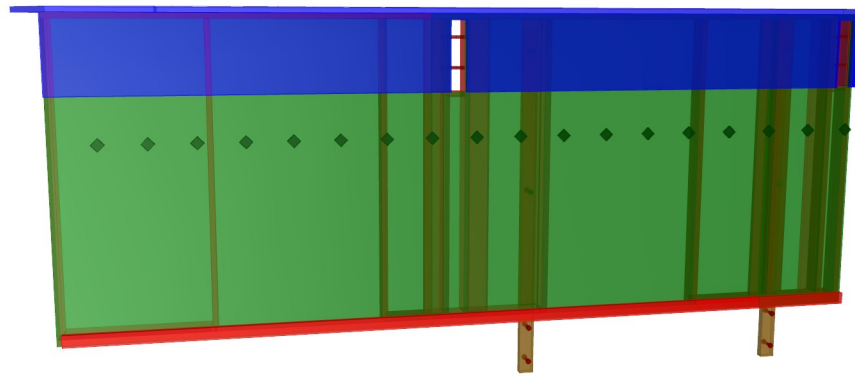


E.1.3 **PLAN VIEW**
1:10@A3

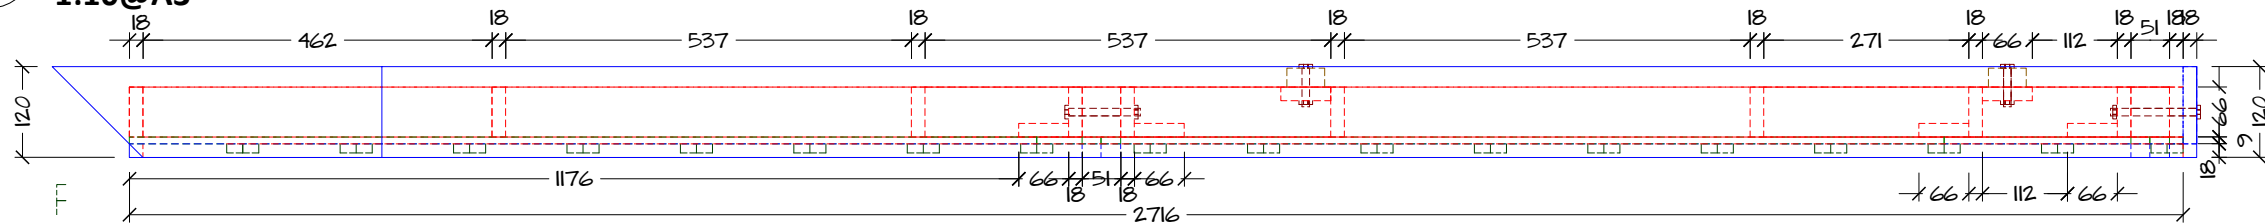

E.1.3 FRONT VIEW
1:10@A3

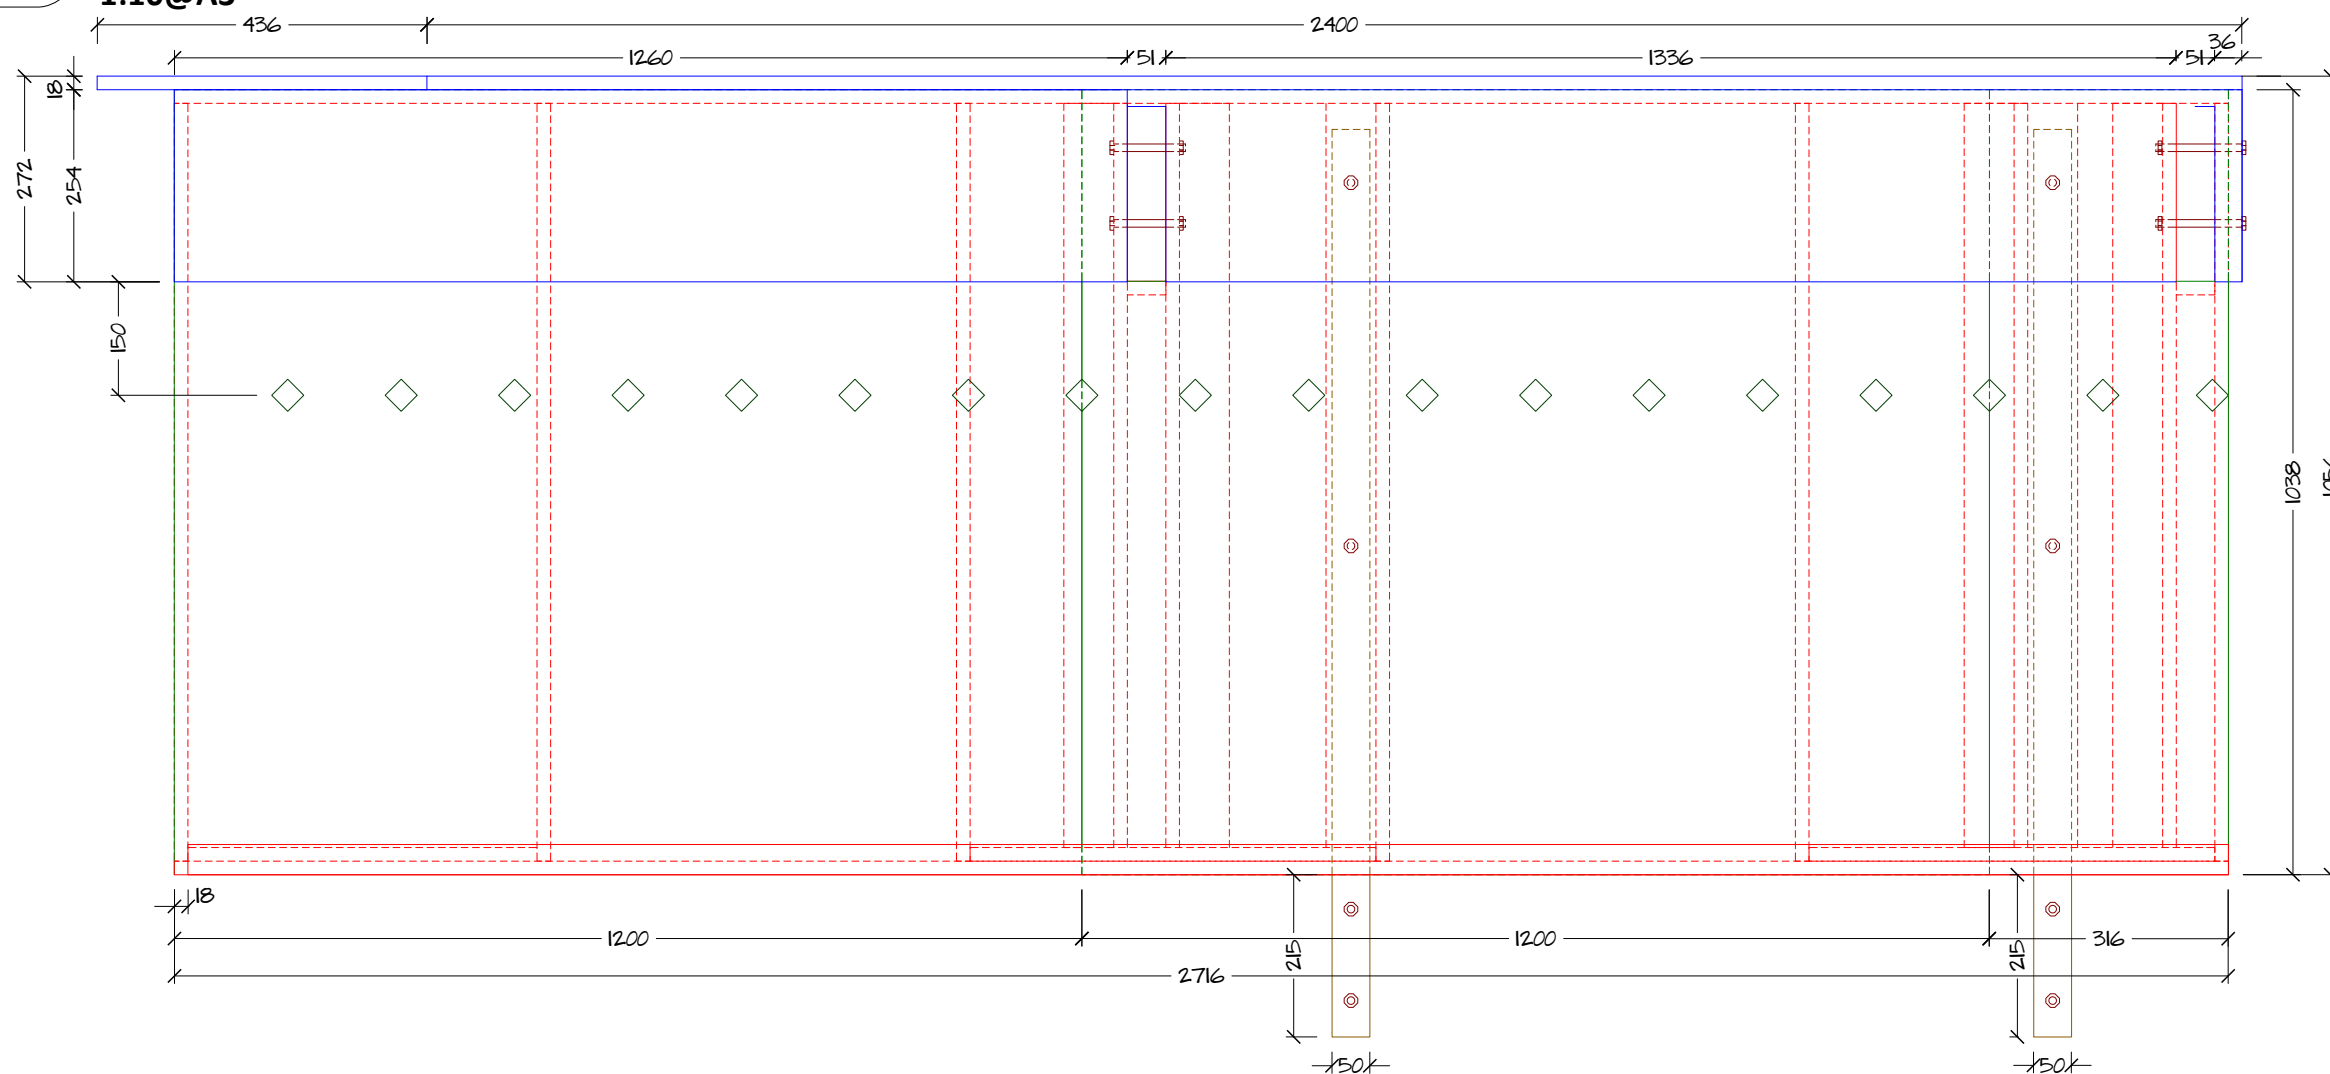


E.1.3 **END VIEW**
1:10@A3

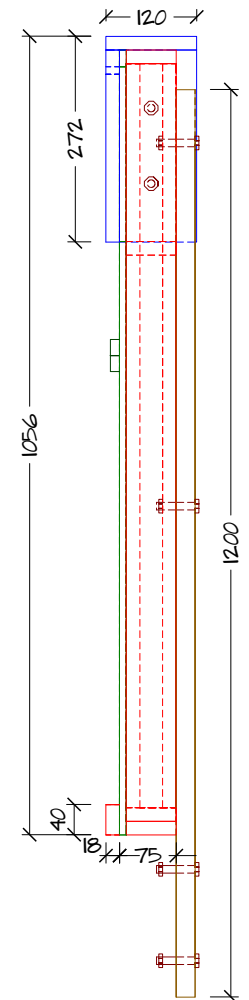


FILL SCREW HOLES ONLY. UNDERCOAT AND TOP COAT SCENIC PAINT FINISH TO MATCH SCENIC REFERENCES SUPPLIED BY SET DESIGNER. FIRE RETARD PAINT ADDITIVE INCLUDED IN UNDERCOAT PAINT.

FROZEN


E.1.4 PLAN VIEW
1:20@A3

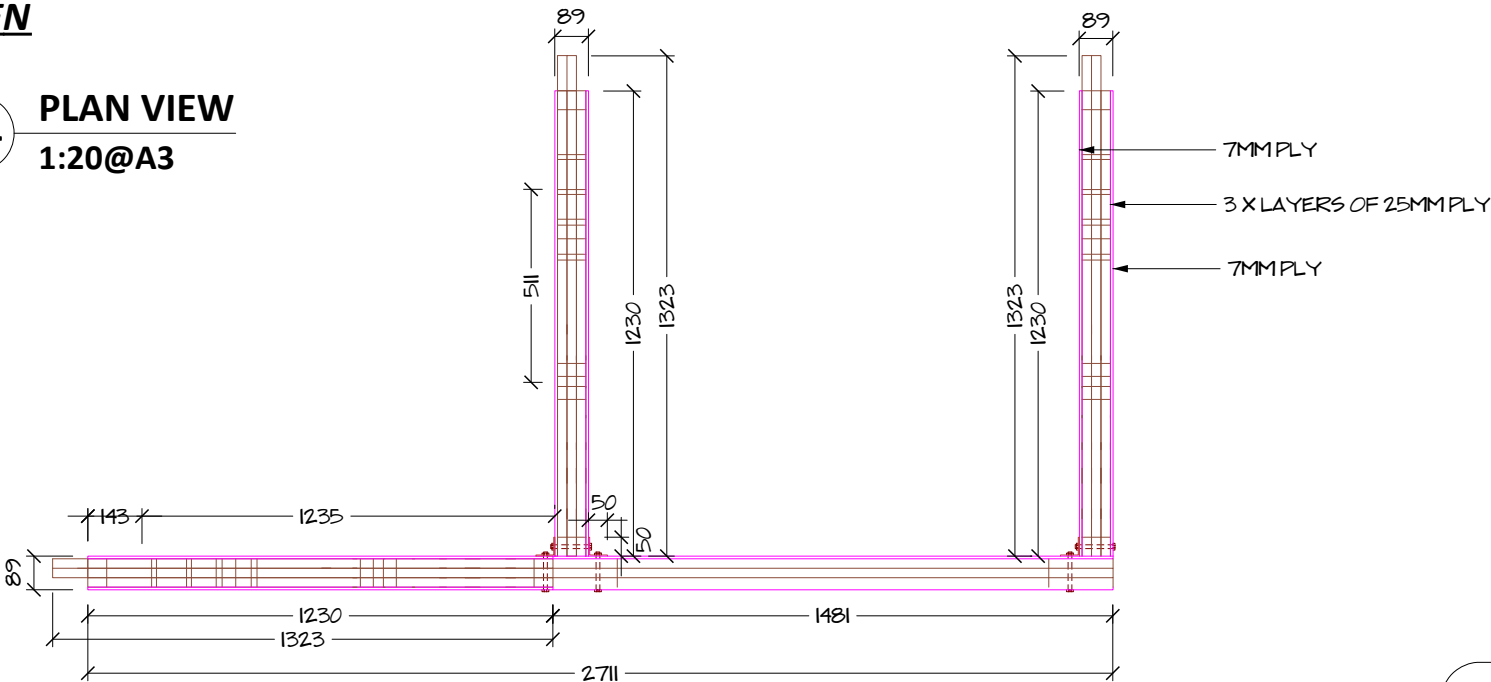

E.1.4 FRONT VIEW
1:20@A3

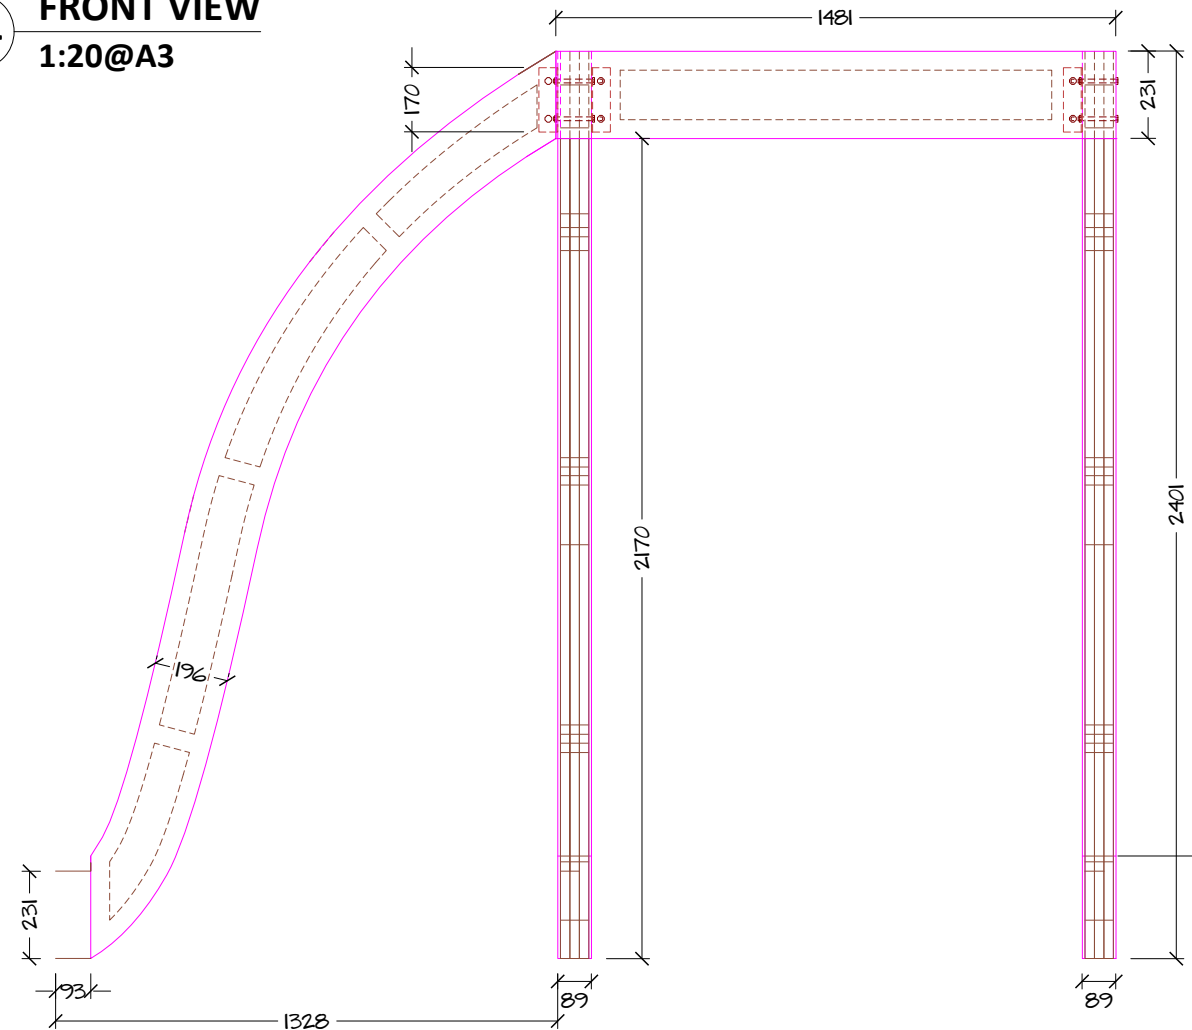

E.1.4 END VIEW
1:20@A3

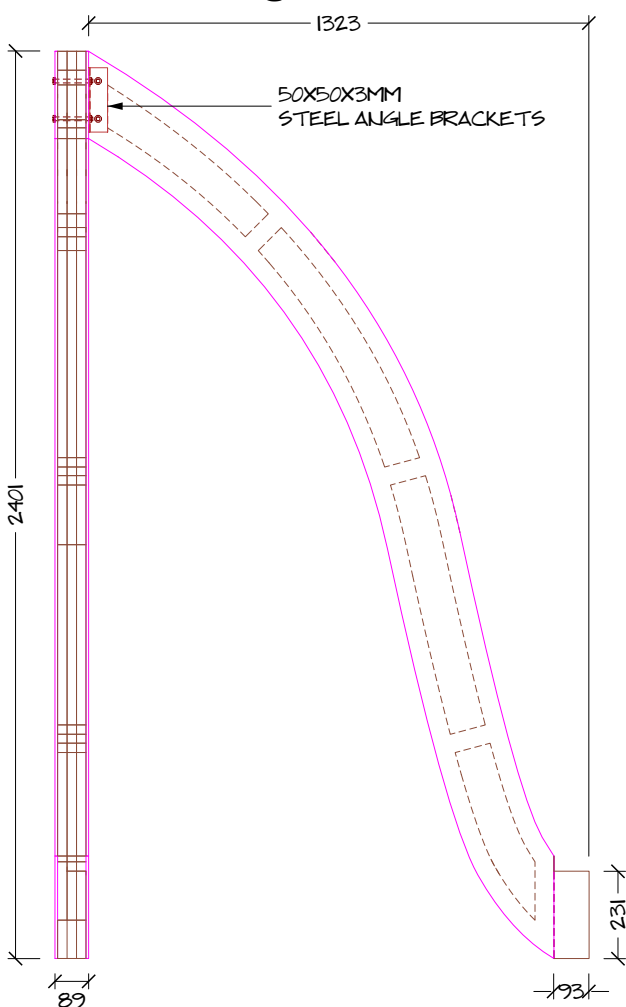

CONSTRUCTION DETAILS


CONSTRUCTED FROM 25MM PLY FORMERS CNC CUT TO SHAPE WITH 7MM PLY EXTERNAL SKINS, PVA GLUE, BRAD NAIL & SCREW FIXING ASSEMBLY.

ASSEMBLE ARCHES TOGETHER WITH 50X50X3MM STEEL ANGLE BRACKETS & 100MM M10 BOLTS AS SHOWN.

FIX ARCH INTO OFF STAGE & REAR FLATS WITH M10 BOLTS.

FILL SCREW HOLES ONLY. UNDERCOAT AND TOP COAT SCENIC PAINT FINISH TO MATCH SCENIC REFERENCES SUPPLIED BY SET DESIGNER. FIRE RETARD PAINT ADDITIVE INCLUDED IN UNDERCOAT PAINT.

E.1.4 3D VIEWS
NA@A3

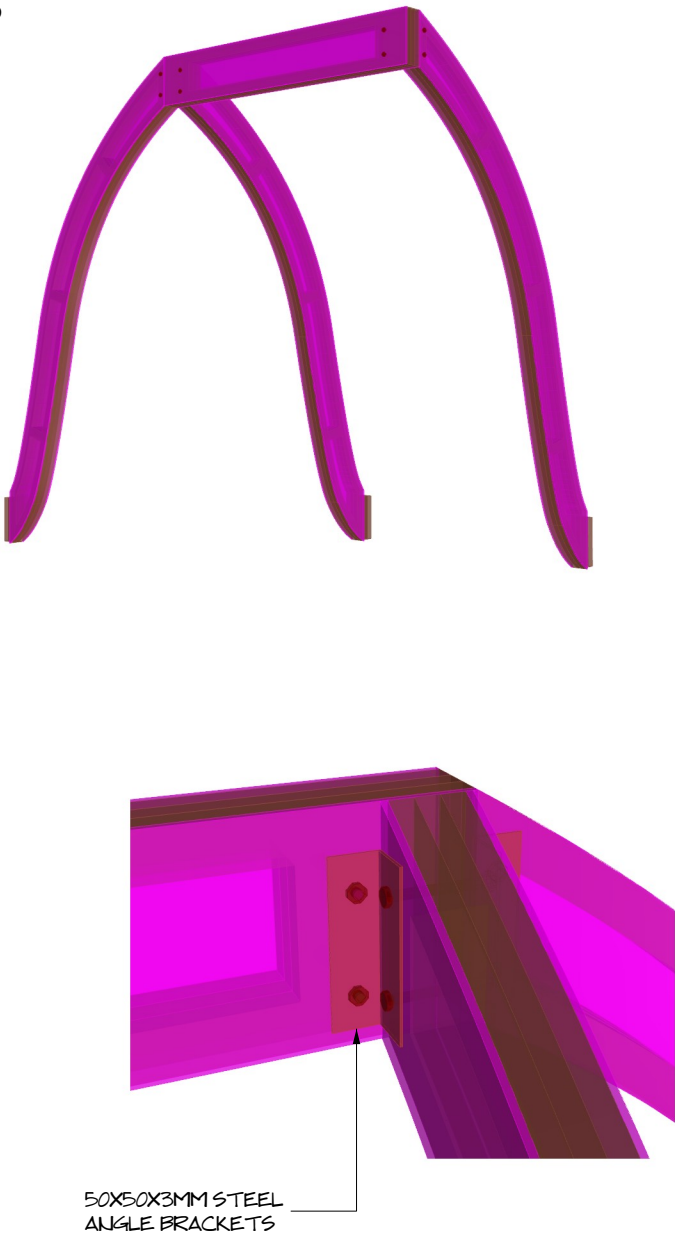


iceworks
design

ICEWORKS DESIGN PTY. LTD.
5/747 Fairfield Rd, Yeerongpilly, QLD. 4105
PO Box 624, Fairfield Gardens, QLD. 4103
T: + 617 3352 4511
www.iceworksdesign.com

Centre/Stage

THESE DRAWINGS ARE CONCEPT & DESIGN ONLY.
FURTHER CONSTRUCTION & DETAIL DRAWINGS
MAY BE REQUIRED.

These drawings are © copyright 2025 ICEWORKS DESIGN.
Drawings, illustrations & 3D Renders are not to be used,
reproduced or copied without permission from ICEWORKS DESIGN.
All dimensions are to be checked on site prior to commencing any
construction, if in doubt please contact ICEWORKS DESIGN. Do
not scale from
drawings. Any building work is to comply with the building act,
BCA and standard regulations where applicable.

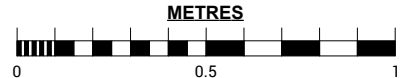

DESIGN APPROVAL


sign:.....
print name:.....
APPROVED / REVISE [circle]
comments.....
date:..... /..... /.....

CLIENT:	CENTRESTAGE
PROJECT	FROZEN
DESIGNER:	HARRY GILL
VENUE:	CIVIC THEATRE
ADDRESS:	375 HUNTER ST NEWCASTLE, NSW 2300
JOB No:	26150


DRAWING NAME:	ITEM E.1.4 - ARCHES	
DRAWN BY:	GAVIN HAMPSTEAD	
ISSUE:	DATE	DESCRIPTION
	31/07/26	ISSUE FOR COSTING & CLIENT REVIEW
	03/08/26	REVISED. ISSUE FOR COSTING & CLIENT REVIEW
	04/08/26	REVISED. ISSUE FOR COSTING & CLIENT REVIEW
	00/00/00	XXXX
	00/00/00	XXXX
	00/00/00	XXXX

SCALE:	1:15@A3
DWG No:	D06
SHEET No:	7 / 10


E.3 PLAN VIEW
1:15@A3

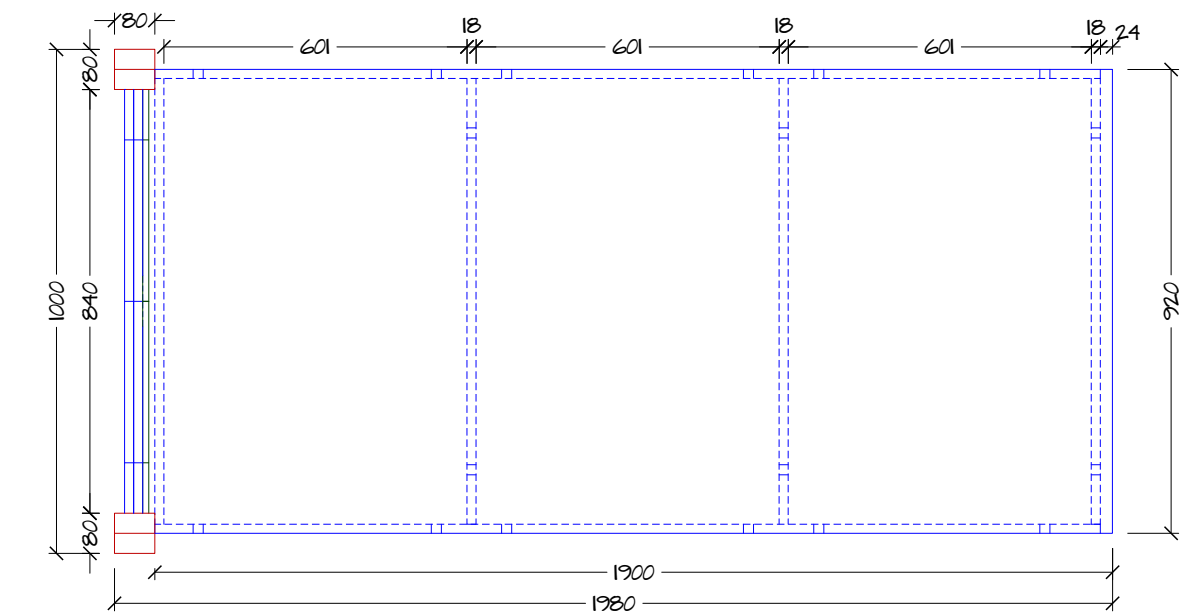

E.3 FRONT VIEW
1:15@A3

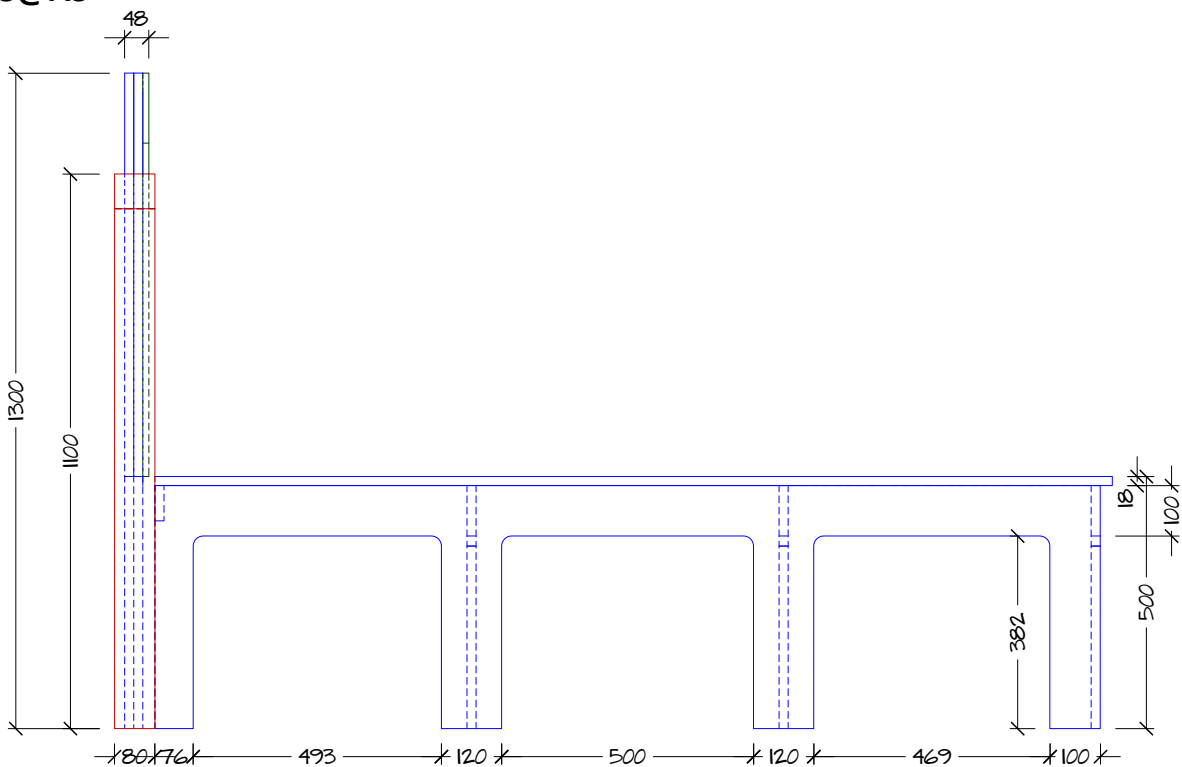

E.3 END VIEW
1:15@A3

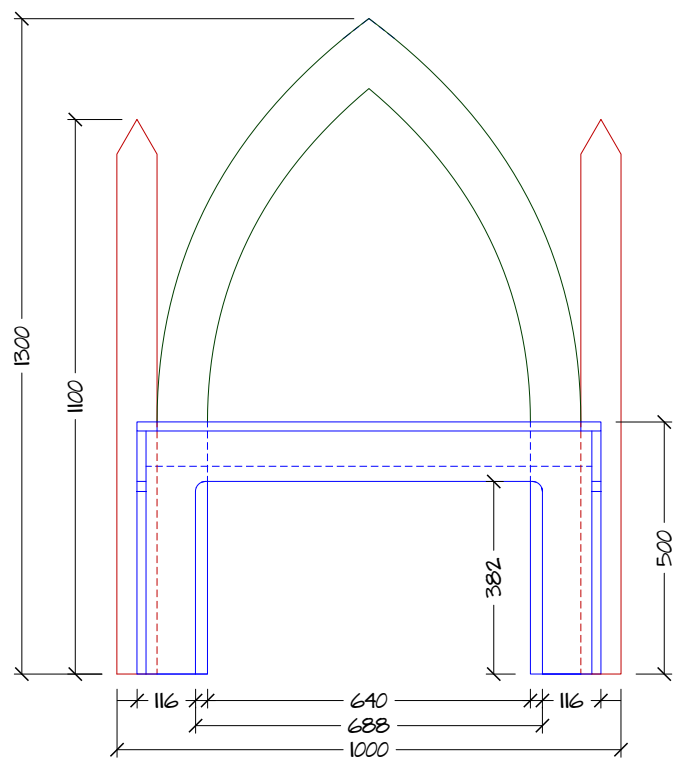


CONSTRUCTION DETAILS

BED BASE FRAME CONSTRUCTED FROM 18MM SELEX PLY CNC CUT TO SHAPE. BEDHEAD CONSTRUCTED FROM 2 X LAYERS OF 18MM & 1 X LAYER OF 12MM SELEX PLY CNC CUT TO SHAPE. PVA GLUE, BRAD NAIL & SCREW FIXING ASSEMBLY.

FILL SCREW HOLES ONLY. UNDERCOAT AND TOP COAT SCENIC PAINT FINISH BEDHEAD TO MATCH SCENIC REFERENCES SUPPLIED BY SET DESIGNER. FIRE RETARD PAINT ADDITIVE INCLUDED IN UNDERCOAT PAINT. PAINT BED BASE FRAME LOW SHEEN BLACK ONLY.

E.3 3D VIEW
NA@A3

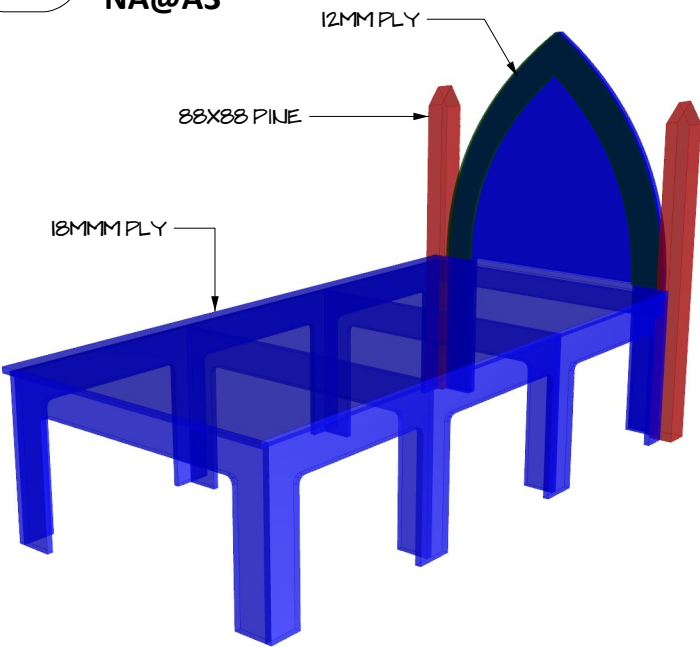

DESIGN APPROVAL

sign:.....
print name:.....
APPROVED / REVISE [circle]
comments.....
date:..... /..... /.....


CLIENT:	CENTRESTAGE
PROJECT	FROZEN
DESIGNER:	HARRY GILL
VENUE:	CIVIC THEATRE
ADDRESS:	375 HUNTER ST NEWCASTLE, NSW 2300
JOB No:	26150

DRAWING NAME:	ITEM E.3 - BEDS X 2	
DRAWN BY:	GAVIN HAMPSTEAD	
ISSUE:	DATE	DESCRIPTION
	31/07/26	ISSUE FOR COSTING & CLIENT REVIEW
	03/08/26	REVISED. ISSUE FOR COSTING & CLIENT REVIEW
	04/08/26	REVISED. ISSUE FOR COSTING & CLIENT REVIEW
	00/00/00	XXXX
	00/00/00	XXXX
	00/00/00	XXXX


SCALE:	1:15@A3
DWG No:	D07
SHEET No:	8 / 10

FROZEN


E.4 PLAN VIEW
1:10@A3

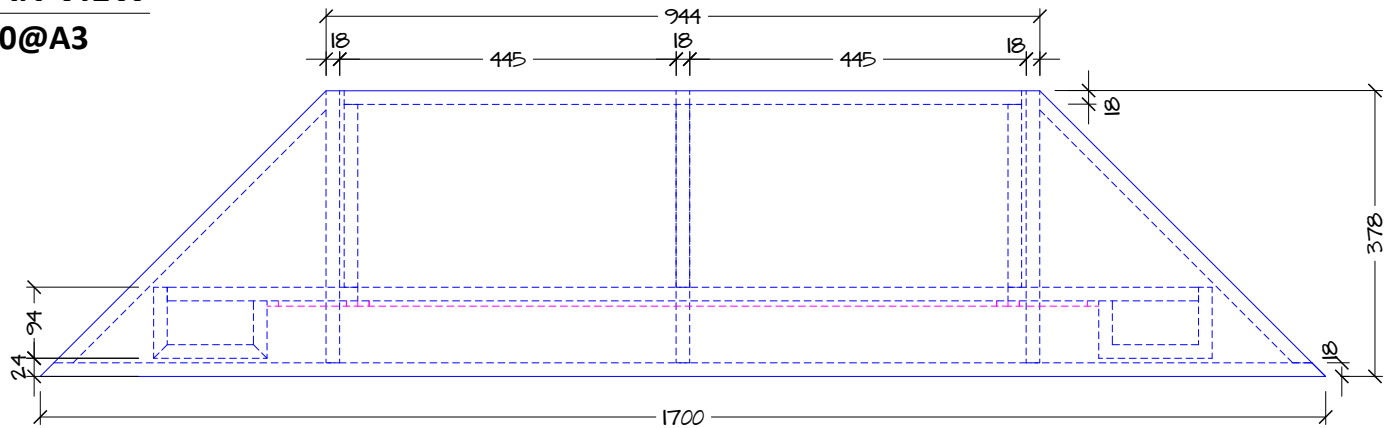

E.4 FRONT VIEW
1:10@A3

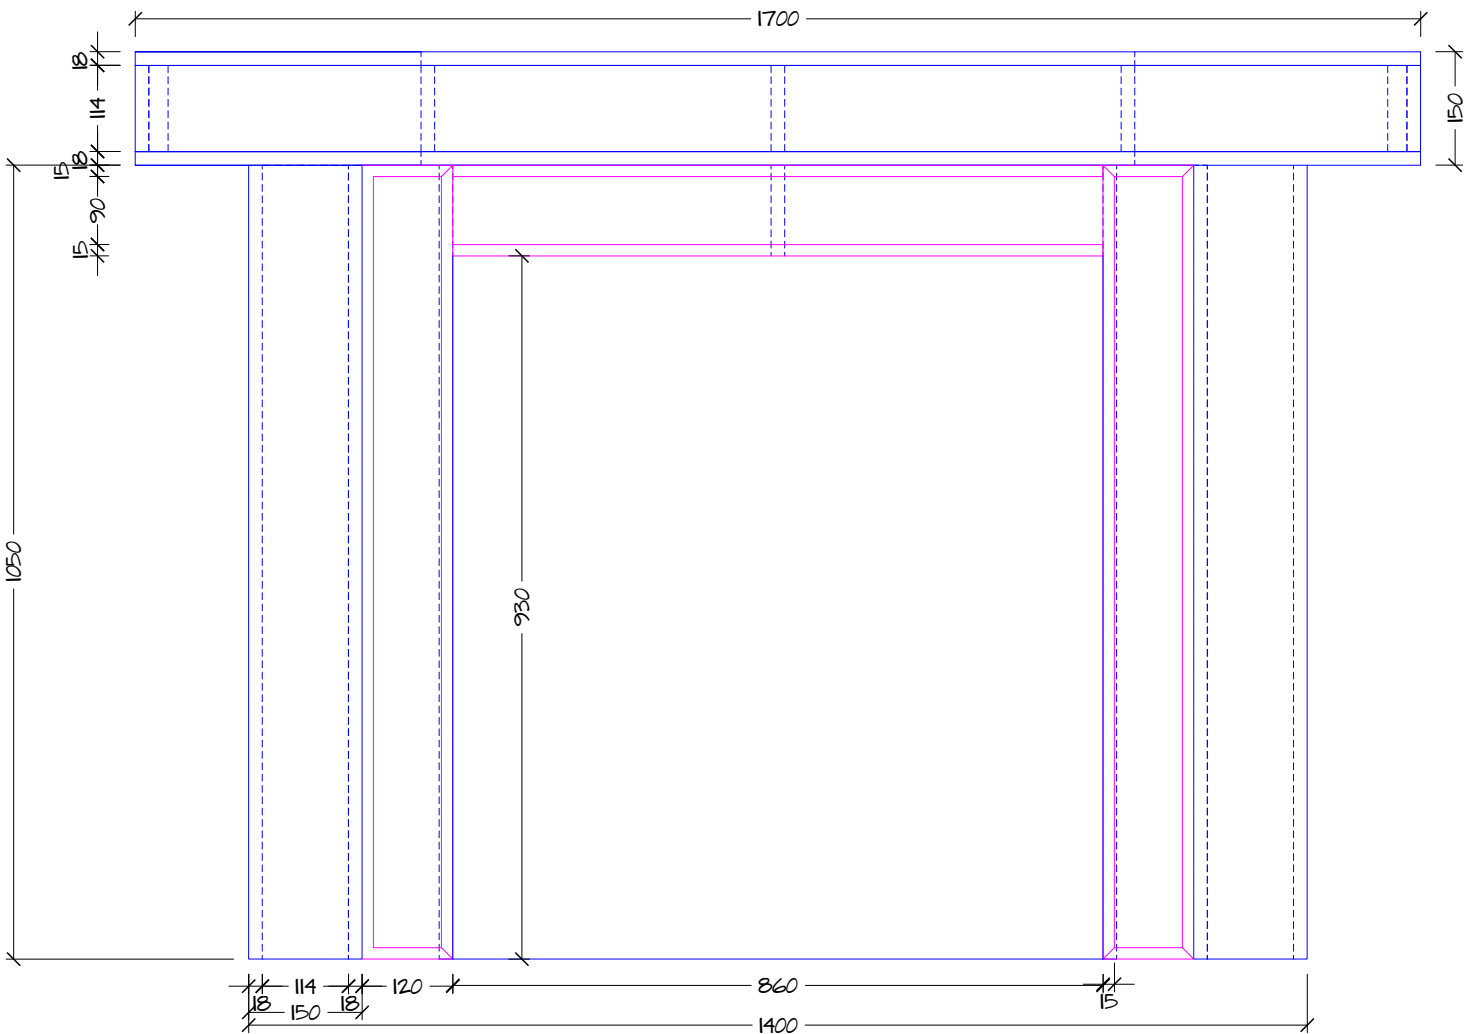

E.4 END VIEW
1:10@A3

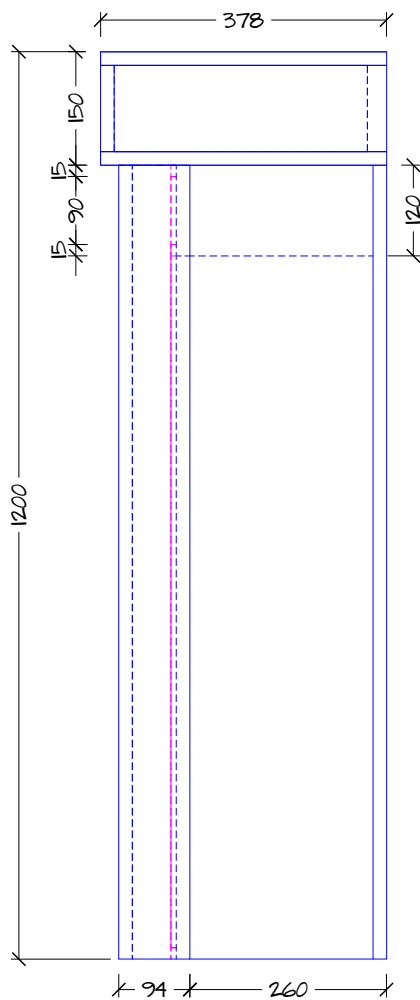


CONSTRUCTION DETAILS

CONSTRUCTED FROM 18MM SELEX PLY CNC CUT TO SHAPE. 7MM PLY PLANT ON DETAIL STRIPS. PVA GLUE, BRAD NAIL & SCREW FIXING ASSEMBLY.

FILL SCREW HOLES ONLY. UNDERCOAT AND TOP COAT SCENIC PAINT FINISH BEDHEAD TO MATCH SCENIC REFERENCES SUPPLIED BY SET DESIGNER. FIRE RETARD PAINT ADDITIVE INCLUDED IN UNDERCOAT PAINT. PAINT BED BASE FRAME LOW SHEEN BLACK ONLY.

E.5 3D VIEW
NA@A3

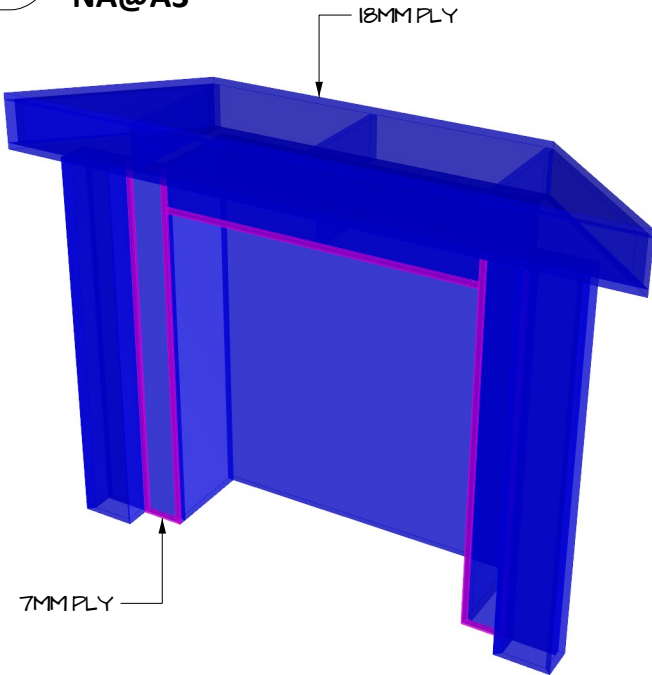


iceworks
design

ICEWORKS DESIGN PTY. LTD.
5/747 Fairfield Rd, Yeerongpilly, QLD. 4105
PO Box 624, Fairfield Gardens, QLD. 4103
T: + 617 3352 4511
www.iceworksdesign.com

Centre/Stage

THESE DRAWINGS ARE CONCEPT & DESIGN ONLY.
FURTHER CONSTRUCTION & DETAIL DRAWINGS
MAY BE REQUIRED.

These drawings are © copyright 2025 ICEWORKS DESIGN.
Drawings, illustrations & 3D Renders are not to be used,
reproduced or copied without permission from ICEWORKS DESIGN.
All dimensions are to be checked on site prior to commencing any
construction, if in doubt please contact ICEWORKS DESIGN. Do
not scale from
drawings. Any building work is to comply with the building act,
BCA and standard regulations where applicable.

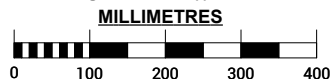

DESIGN APPROVAL


sign:.....
print name:.....
APPROVED / REVISE [circle]
comments.....
date:..... /..... /.....

CLIENT:	CENTRESTAGE
PROJECT	FROZEN
DESIGNER:	HARRY GILL
VENUE:	CIVIC THEATRE
ADDRESS:	375 HUNTER ST NEWCASTLE, NSW 2300
JOB No:	26150


DRAWING NAME:	ITEM E.4 - FIREPLACE	
DRAWN BY:	GAVIN HAMPSTEAD	
ISSUE:	DATE	DESCRIPTION
	31/07/26	ISSUE FOR COSTING & CLIENT REVIEW
	03/08/26	REVISED. ISSUE FOR COSTING & CLIENT REVIEW
	04/08/26	REVISED. ISSUE FOR COSTING & CLIENT REVIEW
	00/00/00	XXXX
	00/00/00	XXXX
	00/00/00	XXXX

SCALE:	1:10@A3
DWG No:	D08
SHEET No:	9 / 10


ITEM E.I.4 - QTY X 2 - 25MM PLY. 7MM PLY.

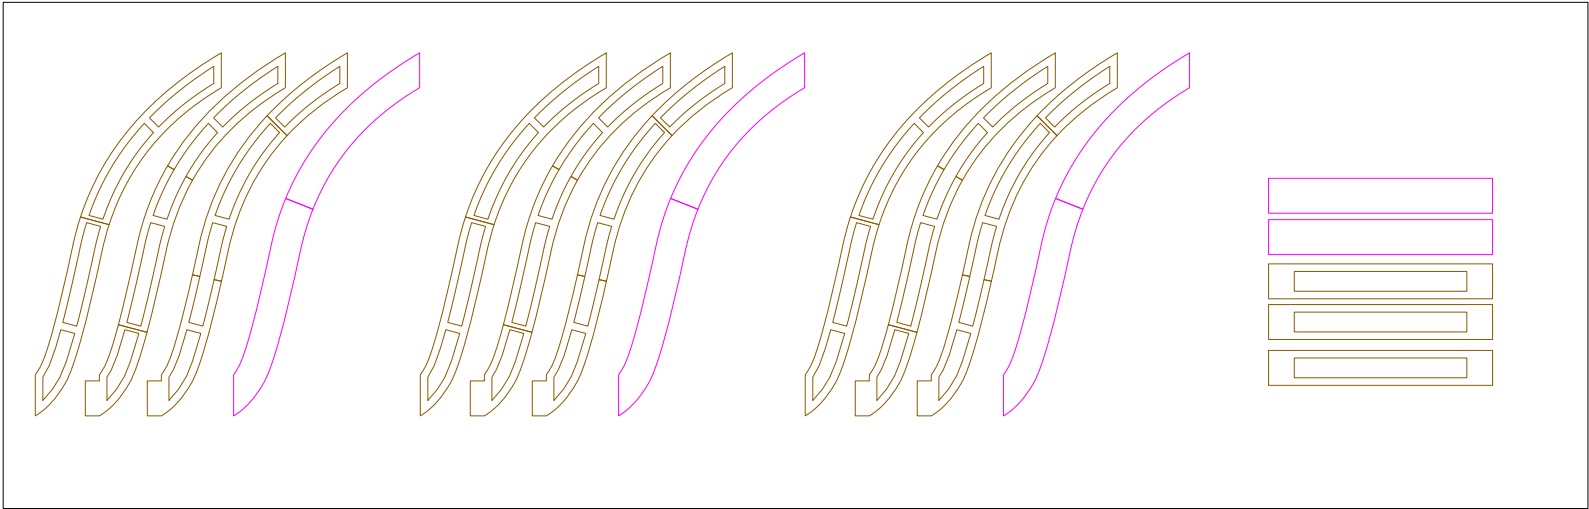


ITEM E.I.I - QTY X 2 - 18MM PLY. 12MM PLY. 12MM UHPPE

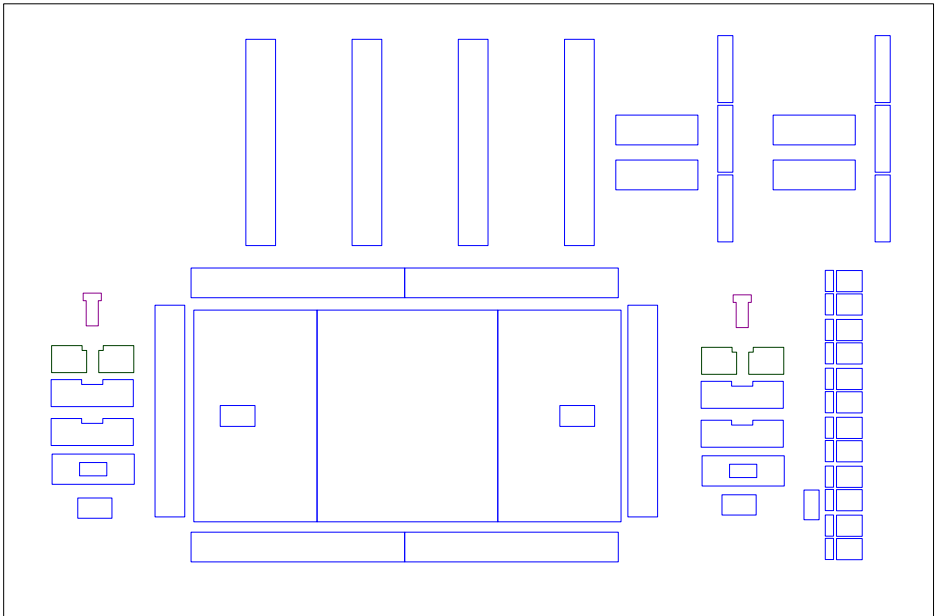

ITEM E.3 - QTY X 2 - 18MM PLY. 12MM PLY.

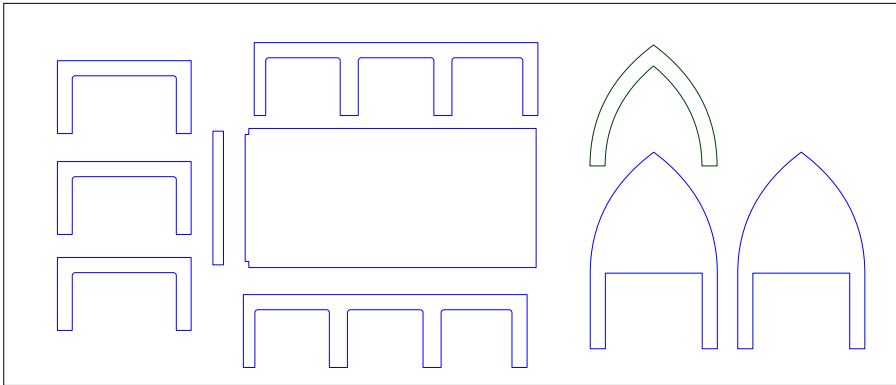

ITEM E.5 - QTY X 1 - 18MM PLY. 7MM PLY.

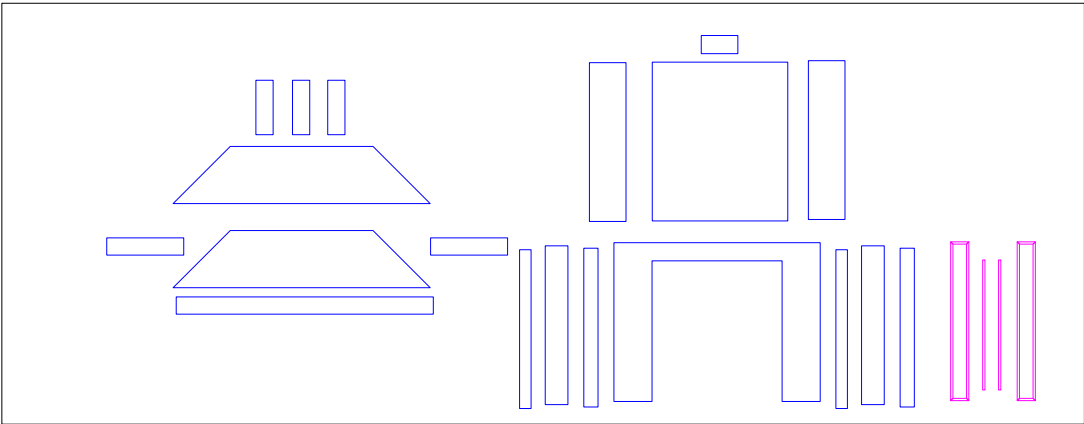

ITEM E.I.2 & E.I.3 - QTY X 2 - 12MM PLY

