

SHEET#	DWG#	DRAWING NAME
1	CP	COVER PAGE
2	D01	RENDERED VIEWS
3	D02	ITEM E.1 - S/R BEDROOM TRUCK ASSEMBLED
4	D03	ITEM E.1.1 - ROLLING TRUCK
5	D04	ITEM E.1.2 - OFF STAGE FLAT
6	D05	ITEM E.1.3 - REAR FLAT
7	D06	ITEM E.1.4 - ARCHES
8	D07	ITEM E.3 - BEDS X 2
9	D08	ITEM E.4 - FIREPLACE
10	D09	CNC FILES



FROZEN

ITEM E - BEDROOM TRUCKS
CONSTRUCTION DESIGN
PLAN SET V3
04/08/26

 ICEWORKS DESIGN PTY. LTD. 5/747 Fairfield Rd, Yeerongpilly, QLD. 4105 PO Box 624, Fairfield Gardens, QLD. 4103 T: + 617 3352 4511 www.iceworksdesign.com		THESE DRAWINGS ARE CONCEPT & DESIGN ONLY. FURTHER CONSTRUCTION & DETAIL DRAWINGS MAY BE REQUIRED. These drawings are © copyright 2025 ICEWORKS DESIGN. Drawings, illustrations & 3D Renders are not to be used, reproduced or copied without permission from ICEWORKS DESIGN. All dimensions are to be checked on site prior to commencing any construction, if in doubt please contact ICEWORKS DESIGN. Do not scale from drawings. Any building work is to comply with the building act, BCA and standard regulations where applicable.	DESIGN APPROVAL sign:..... print name:..... APPROVED / REVISE [circle] comments..... date:..... /..... /.....	CLIENT:	STODDART ENTERTAINMENT GROUP	DRAWING NAME:	COVER PAGE	SCALE:	N/A @ A3
				PROJECT	FROZEN	DRAWN BY:	GAVIN HAMPSTEAD	DWG No:	CP
				DESIGNER:	HARRY GILL	ISSUE:	DATE	DESCRIPTION	SHEET No:
				VENUE:	CIVIC THEATRE		31/07/26	ISSUE FOR COSTING & CLIENT REVIEW	
				ADDRESS:	375 HUNTER ST NEWCASTLE, NSW 2300		03/08/26	REVISED. ISSUE FOR COSTING & CLIENT REVIEW	

ITEM E.1 - S/R BEDROOM TRUCK



ITEM E.2 - S/L BEDROOM TRUCK



ICEWORKS DESIGN PTY. LTD.
5/747 Fairfield Rd, Yeerongpilly, QLD. 4105
PO Box 624, Fairfield Gardens, QLD. 4103
T: + 617 3352 4511
www.iceworksdesign.com



THESE DRAWINGS ARE CONCEPT & DESIGN ONLY.
FURTHER CONSTRUCTION & DETAIL DRAWINGS
MAY BE REQUIRED.

These drawings are © copyright 2025 ICEWORKS DESIGN.
Drawings, illustrations & 3D Renders are not to be used,
reproduced or copied without permission from ICEWORKS DESIGN.
All dimensions are to be checked on site prior to commencing any
construction, if in doubt please contact ICEWORKS DESIGN. Do
not scale from
drawings. Any building work is to comply with the building act,
BCA and standard regulations where applicable.

DESIGN APPROVAL

sign:.....

print name:.....

APPROVED / REVISE [circle]

comments.....

date:..... /..... /.....


CLIENT:	STODDART ENTERTAINMENT GROUP
PROJECT	FROZEN
DESIGNER:	HARRY GILL
VENUE:	CIVIC THEATRE
ADDRESS:	375 HUNTER ST NEWCASTLE, NSW 2300
JOB No:	26150

DRAWING NAME:	RENDERED VIEWS	
	DRAWN BY: GAVIN HAMPSTEAD	
ISSUE:	DATE	DESCRIPTION
	31/07/26	ISSUE FOR COSTING & CLIENT REVIEW
	03/08/26	REVISED. ISSUE FOR COSTING & CLIENT REVIEW
	04/08/26	REVISED. ISSUE FOR COSTING & CLIENT REVIEW
	00/00/00	XXXX
	00/00/00	XXXX
	00/00/00	XXXX

SCALE:	1:100 @ A3
DWG No:	D01
SHEET No:	2 / 10

FROZEN

E.1 PLAN VIEW
1:25@A3

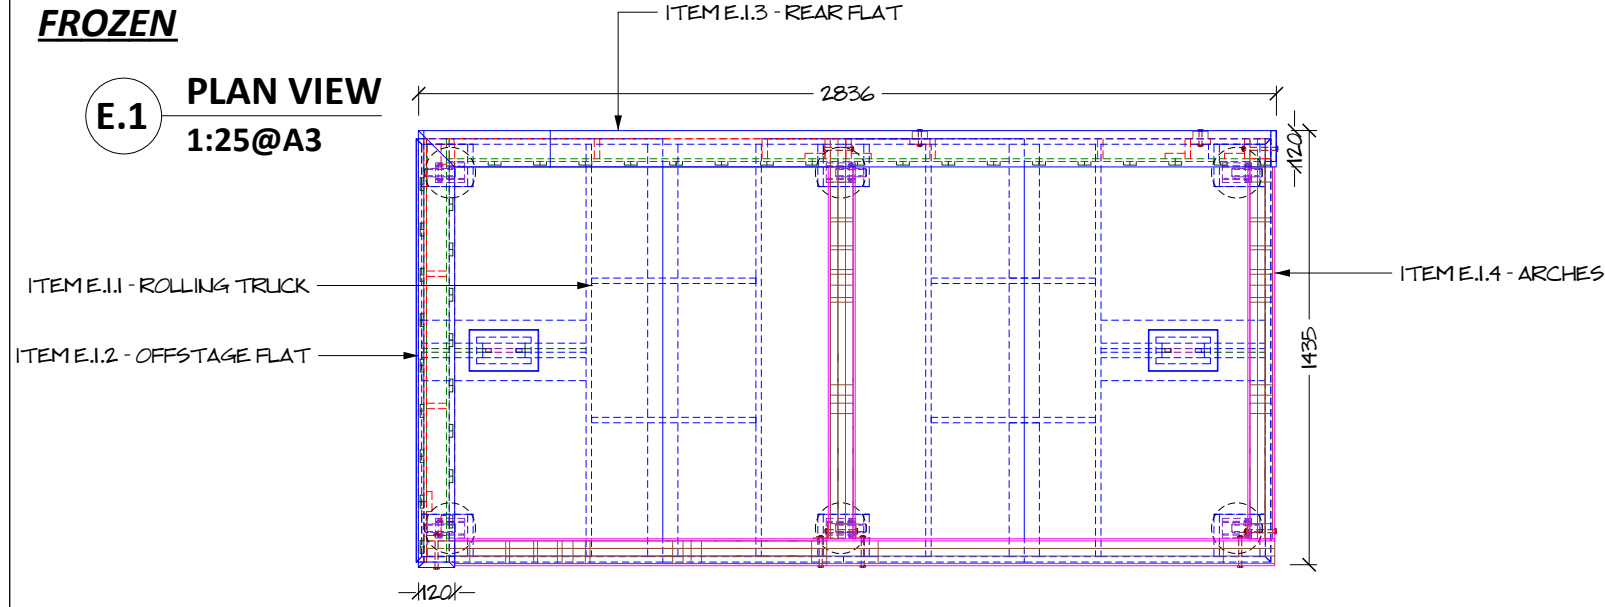


CONSTRUCTION DETAILS

MAKE 2 X ITEMS TOTAL -


1 X S/R BEDROOM TRUCK AS PER PLANS.

1 X S/L BEDROOM TRUCK - FLIP PLANS LEFT TO RIGHT.


E.1 FRONT VIEW
1:25@A3

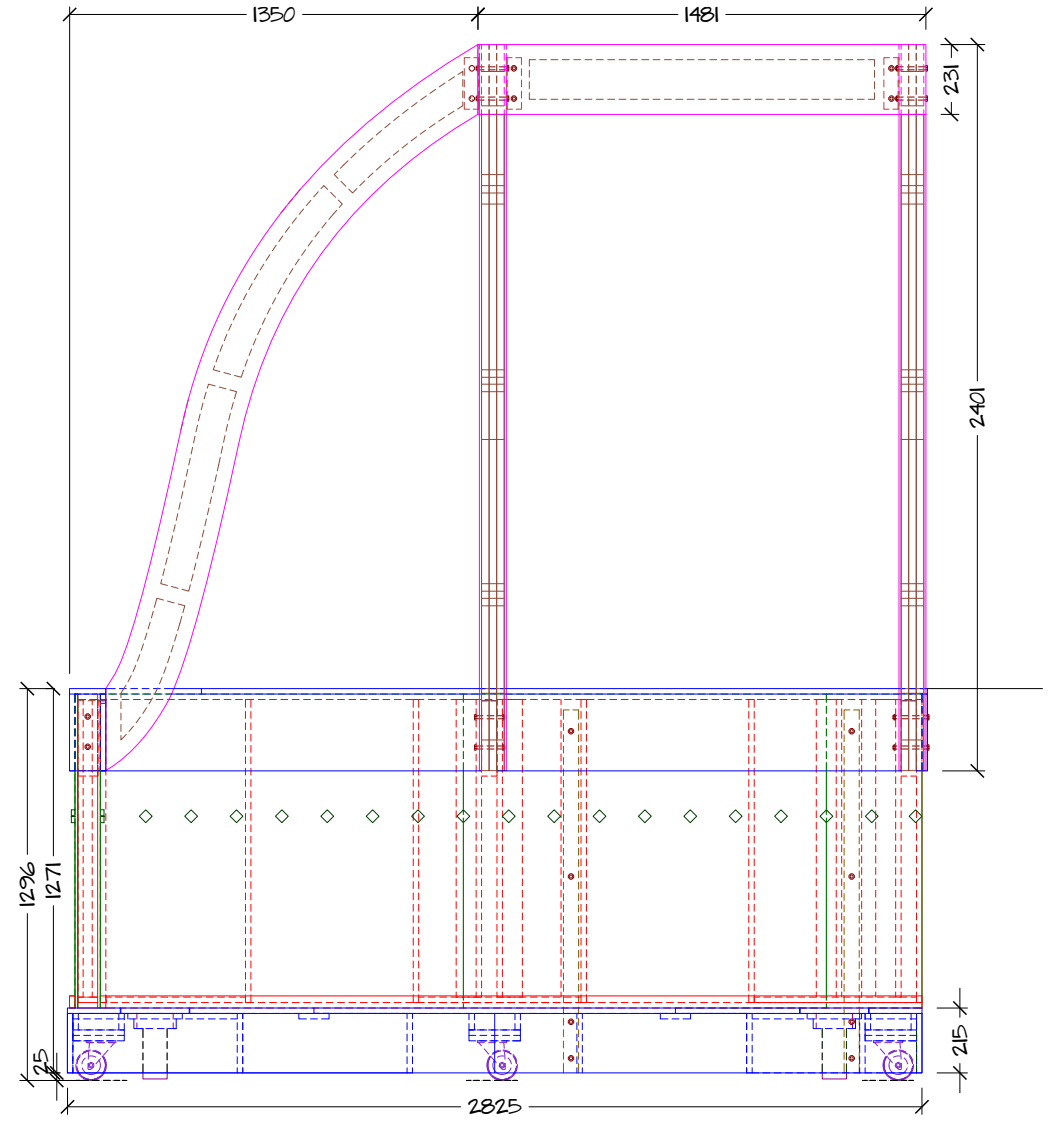

E.1 END VIEW
1:25@A3

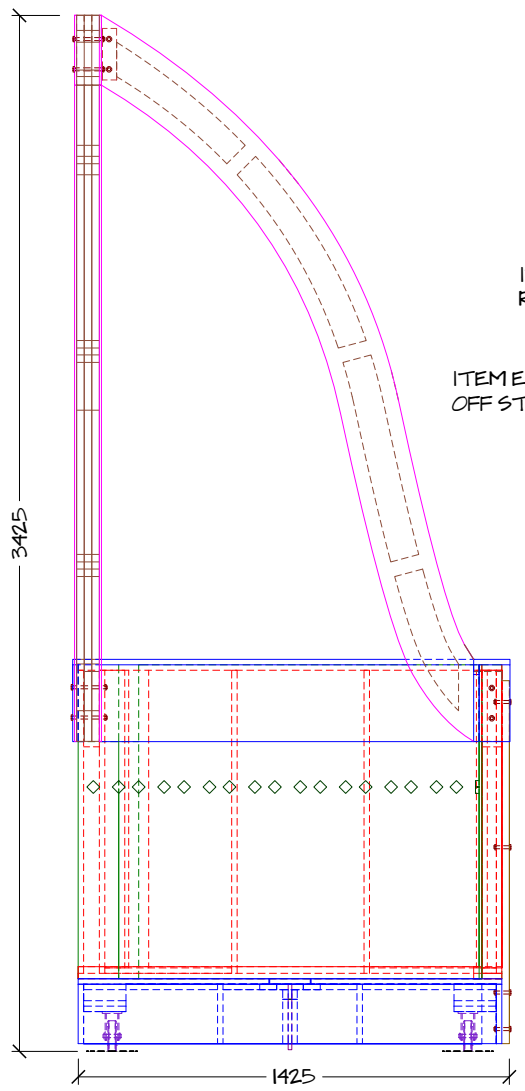

E.1 3D VIEW
NA@A3

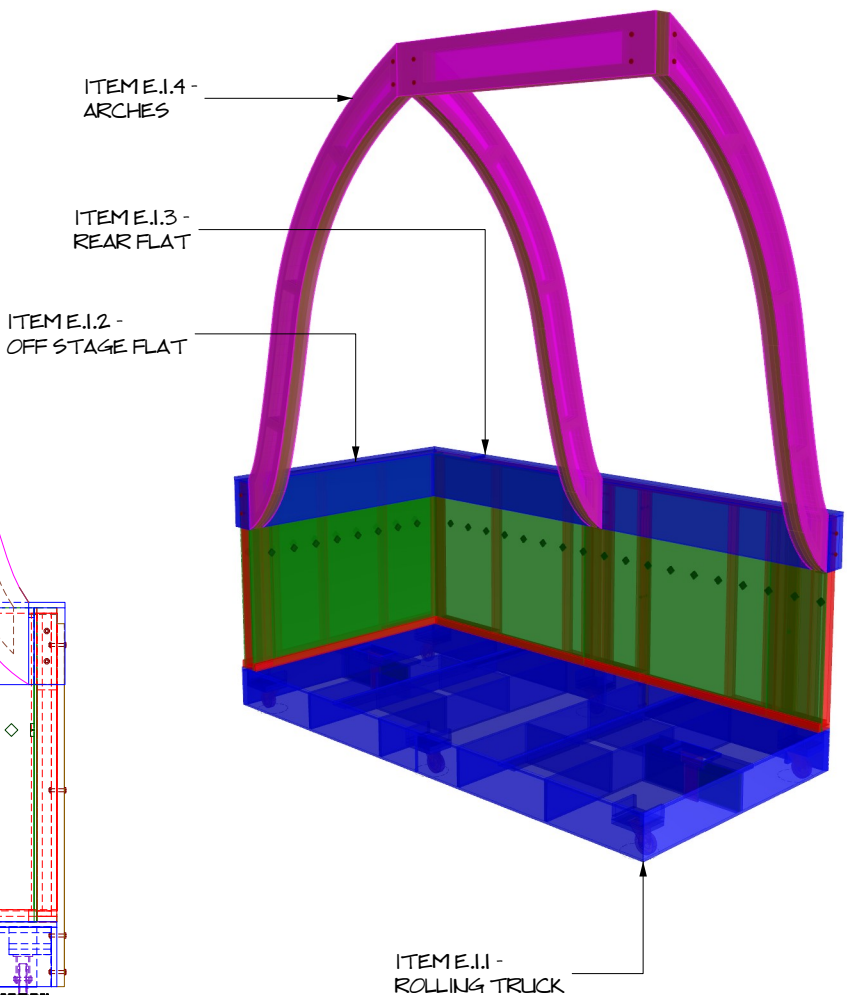


iceworks
design

ICEWORKS DESIGN PTY. LTD.
5/747 Fairfield Rd, Yeerongpilly, QLD. 4105
PO Box 624, Fairfield Gardens, QLD. 4103
T: + 617 3352 4511
www.iceworksdesign.com



THESE DRAWINGS ARE CONCEPT & DESIGN ONLY.
FURTHER CONSTRUCTION & DETAIL DRAWINGS
MAY BE REQUIRED.

These drawings are © copyright 2025 ICEWORKS DESIGN.
Drawings, illustrations & 3D Renders are not to be used,
reproduced or copied without permission from ICEWORKS DESIGN.
All dimensions are to be checked on site prior to commencing any
construction, if in doubt please contact ICEWORKS DESIGN. Do
not scale from
drawings. Any building work is to comply with the building act,
BCA and standard regulations where applicable.

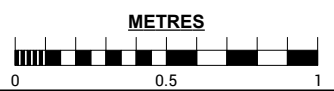

DESIGN APPROVAL

sign:.....

print name:.....

APPROVED / REVISE [circle]

comments:.....


date:..... /..... /.....

CLIENT:	STODDART ENTERTAINMENT GROUP
PROJECT	FROZEN
DESIGNER:	HARRY GILL
VENUE:	CIVIC THEATRE
ADDRESS:	375 HUNTER ST NEWCASTLE, NSW 2300
JOB No:	26150

DRAWING NAME:	ITEM E.1 - S/R BEDROOM TRUCK ASSEMBLED	
DRAWN BY:	GAVIN HAMPSTEAD	
ISSUE:	DATE	DESCRIPTION
	31/07/26	ISSUE FOR COSTING & CLIENT REVIEW
	03/08/26	REVISED. ISSUE FOR COSTING & CLIENT REVIEW
	04/08/26	REVISED. ISSUE FOR COSTING & CLIENT REVIEW
	00/00/00	XXXX
	00/00/00	XXXX
	00/00/00	XXXX

SCALE:	1:25@A3
DWG No:	D02
SHEET No:	3 / 10

E.1.1 3D VIEW
NA@A3

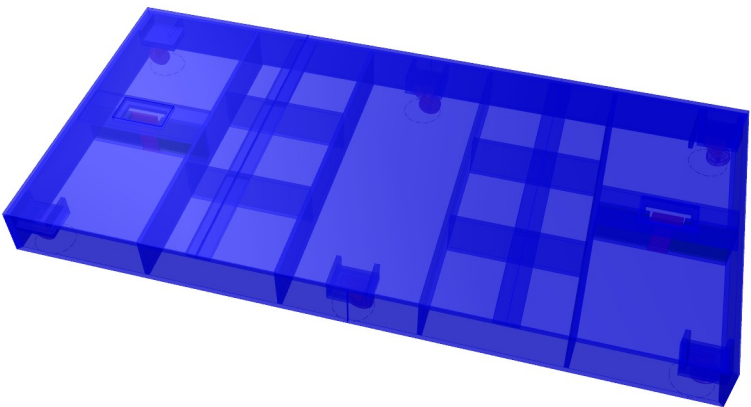

CONSTRUCTION DETAILS


CONSTRUCTED FROM 18MM SELEX PLY, PVA GLUE, BRAD NAIL & SCREW FIXING ASSEMBLY. MOUNT 6 X SWIVEL CASTORS WITH M8 BOLTS. CASTOR SPECIFICATION - RICHMOND S4362 100MM BLACK CASTOR WHEEL.

GUIDE KNIVES X 2 CONSTRUCTED FROM 12MM UHDPE CNC CUT TO SHAPE. MAKE ACCESS HATCHES IN TRUCK TOP TO INSTALL & REMOVE GUIDE KNIVES FROM TRUCK. SCREW FIX ACCESS HATCHES TO LOCK KNIVES IN POSITION.


TRUCK KNIVES SUPPORT FRAMES CONSTRUCTED FROM 18MM PLY & 12MM PLY. ADD IMPACKER TO 12MM PLY TO ALLOW 12MM UHDPE KNIVES TO SLIDE IN & OUT. SET KNIVES 5MM ABOVE FLOOR LEVEL TO LOCATE INTO 16X16X1.6MM ALUMINIUM U-CHANNEL GUIDE TRACK SET INTO SHOW FLOOR.

FILL SCREW HOLES ONLY. UNDERCOAT AND TOP COAT SCENIC PAINT FINISH TO MATCH SCENIC REFERENCES SUPPLIED BY SET DESIGNER. FIRE RETARD PAINT ADDITIVE INCLUDED IN UNDERCOAT PAINT.


E.1.1 PLAN VIEW
1:15@A3

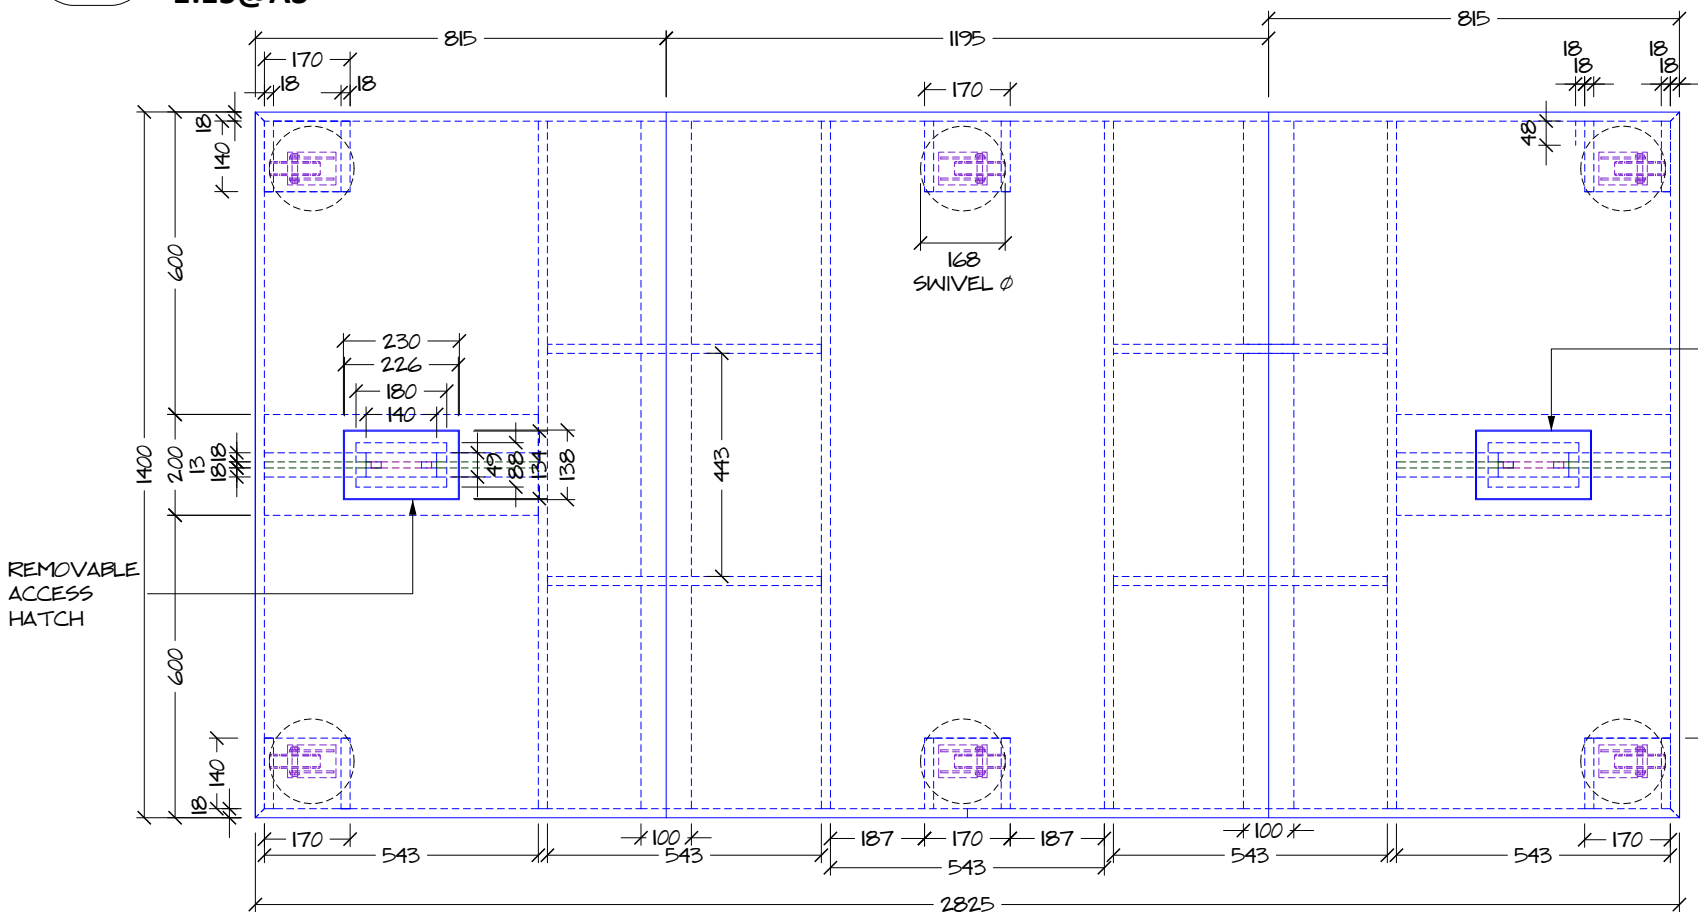


E.1.1 3D VIEW
NA@A3

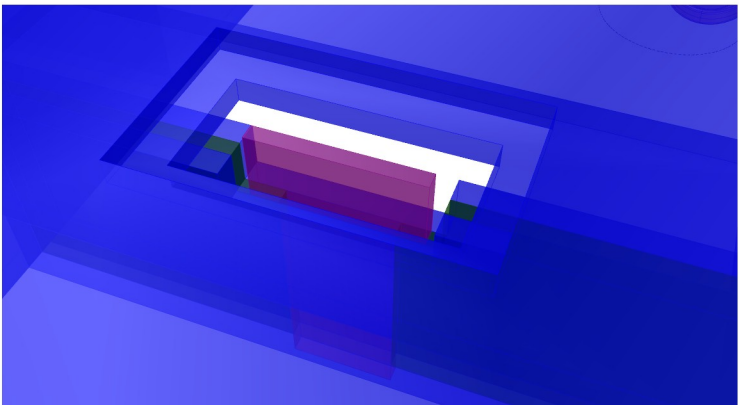


E.1.1 3D VIEW
NA@A3

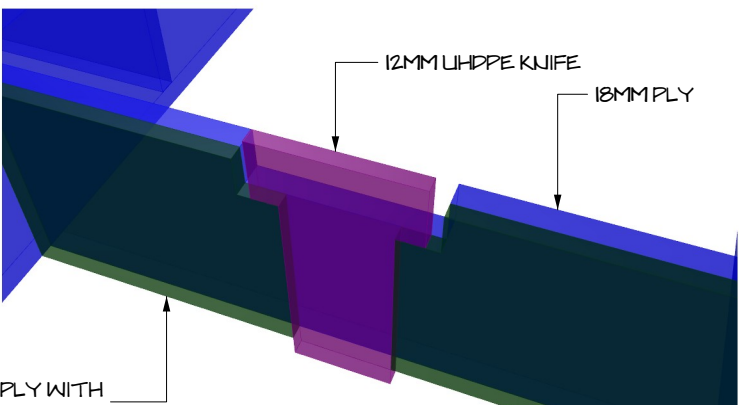

E.1.1 FRONT VIEW
1:15@A3

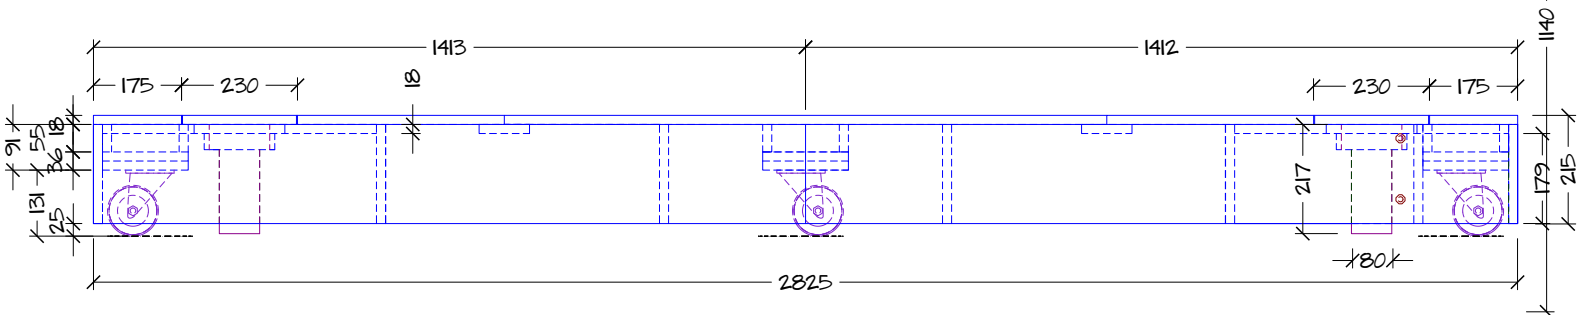

E.1.1 END VIEW
1:15@A3

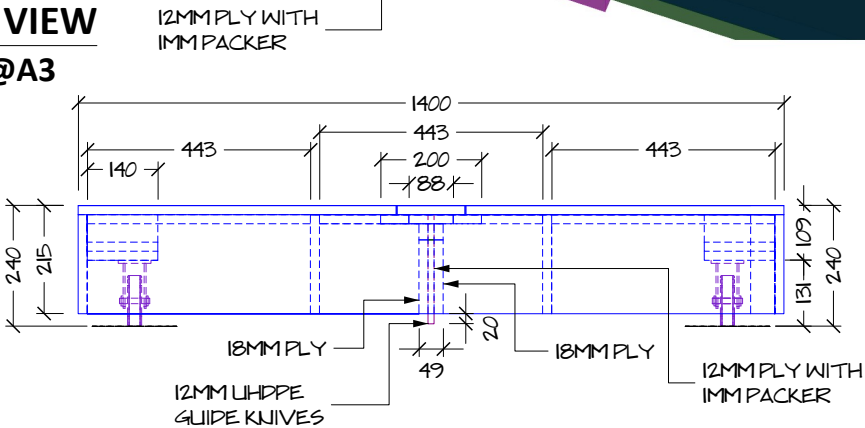


iceworks
design

ICEWORKS DESIGN PTY. LTD.
5/747 Fairfield Rd, Yeerongpilly, QLD. 4105
PO Box 624, Fairfield Gardens, QLD. 4103
T: + 617 3352 4511
www.iceworksdesign.com



THESE DRAWINGS ARE CONCEPT & DESIGN ONLY. FURTHER CONSTRUCTION & DETAIL DRAWINGS MAY BE REQUIRED.

These drawings are © copyright 2025 ICEWORKS DESIGN. Drawings, illustrations & 3D Renders are not to be used, reproduced or copied without permission from ICEWORKS DESIGN. All dimensions are to be checked on site prior to commencing any construction, if in doubt please contact ICEWORKS DESIGN. Do not scale from drawings. Any building work is to comply with the building act, BCA and standard regulations where applicable.

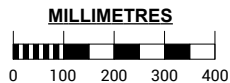

DESIGN APPROVAL

sign:.....
print name:.....
APPROVED / REVISE [circle]
comments.....
date:..... /..... /.....


CLIENT:	STODDART ENTERTAINMENT GROUP
PROJECT	FROZEN
DESIGNER:	HARRY GILL
VENUE:	CIVIC THEATRE
ADDRESS:	375 HUNTER ST NEWCASTLE, NSW 2300
JOB No:	26150

DRAWING NAME:	ITEM E.1.1 - ROLLING TRUCK	
DRAWN BY:	GAVIN HAMPSTEAD	
ISSUE:	DATE	DESCRIPTION
	31/07/26	ISSUE FOR COSTING & CLIENT REVIEW
	03/08/26	REVISED. ISSUE FOR COSTING & CLIENT REVIEW
	04/08/26	REVISED. ISSUE FOR COSTING & CLIENT REVIEW
	00/00/00	XXXX
	00/00/00	XXXX
	00/00/00	XXXX


SCALE:	1:15@A3
DWG No:	D03
SHEET No:	4 / 10

FROZEN


E.1.2 **PLAN VIEW**
1:10@A3

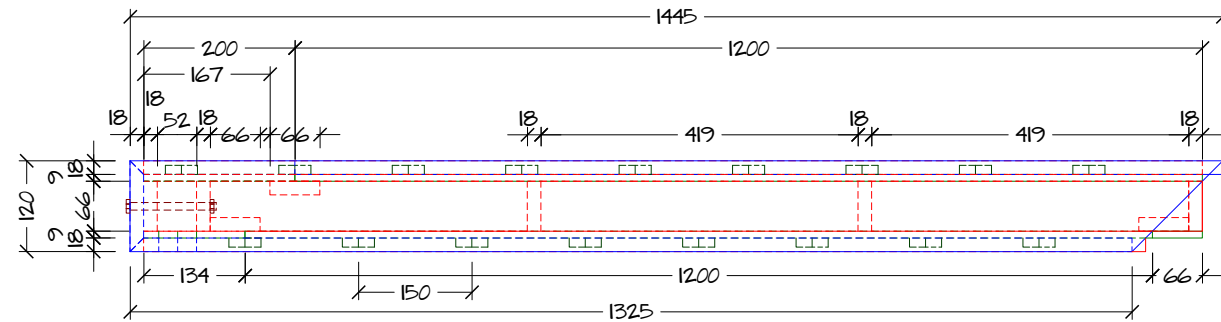


E.1.2 FRONT VIEW
1:10@A3

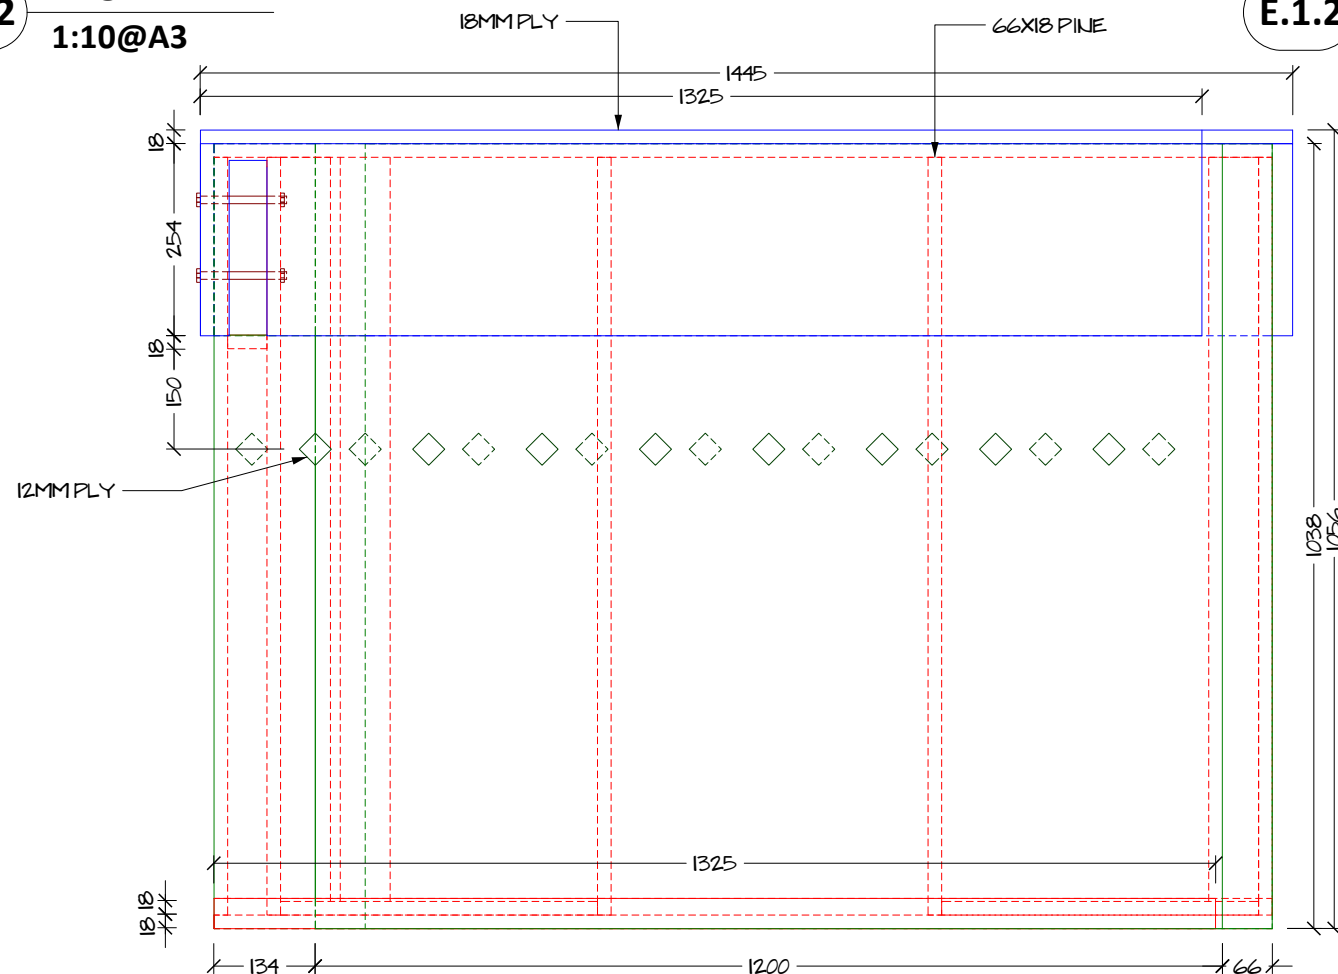


E.1.2 **END VIEW**
1:15@A3

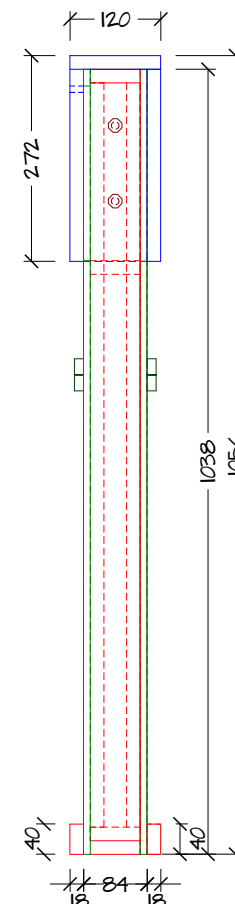

E.1.2 **3D VIEW**
NA@A3

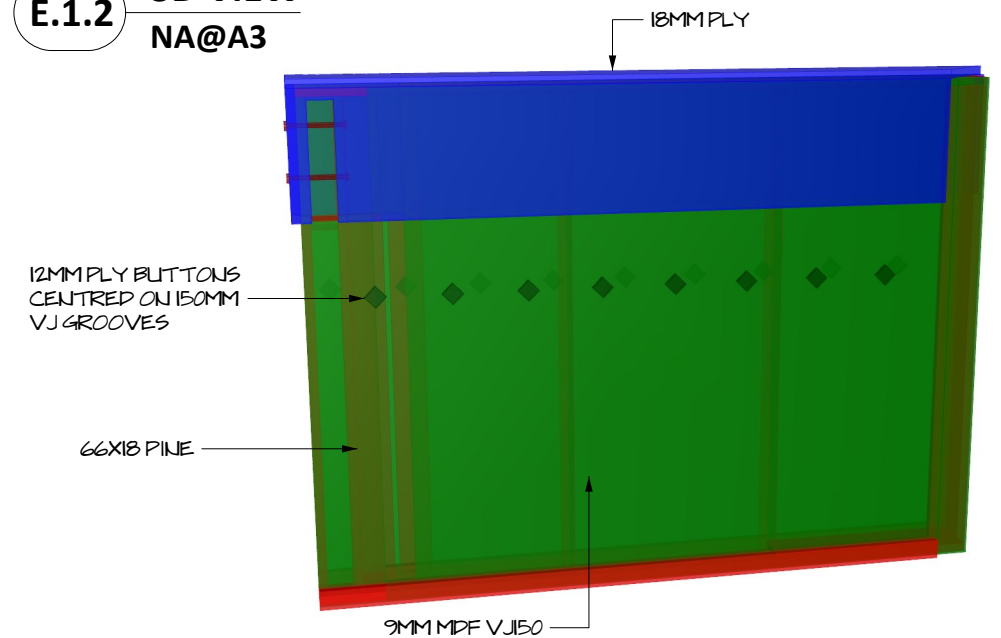

E.1.2 **3D VIEW**
NA@A3

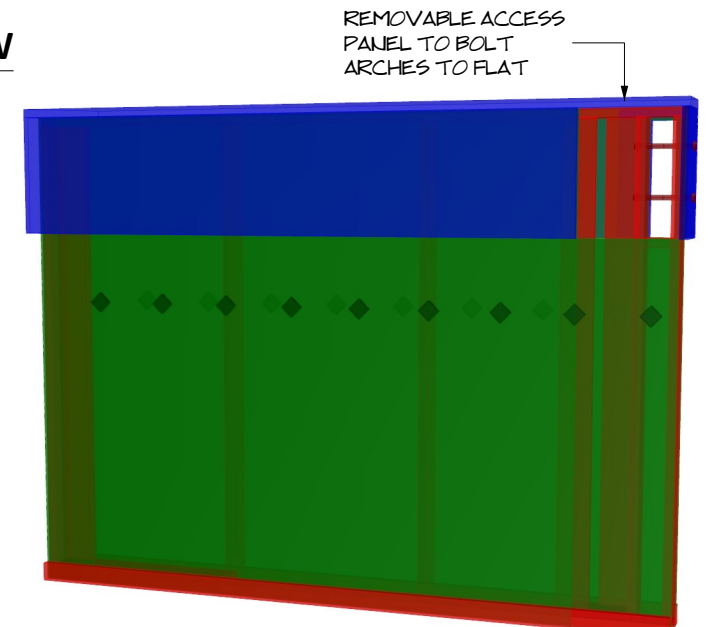

CONSTRUCTION DETAILS

CONSTRUCTED FROM 66X18 PINE FRAMING WITH 9MM MDF VJ150 FACE SKINS. 18MM PLY TOP CAPPING AS SHOWN. PVA GLUE, BRAD NAIL & SCREW FIXING ASSEMBLY.

12MM PLY PLANT ON BUTTON HEADS CENTRED ON VJ150 GROOVES.


REMOVABLE ACCESS PANEL TO BOLT ARCHES INTO FLATS.

SCREW FIX FLATS TO ROLLING TRUCK BASE WITH 10G TIMBER BATTEN
SCREWS. SCREW FIX THROUGH UNDERSIDE OF ROLLING TRUCK UP INTO
BOTTOM FLAT FRAMING.

FILL SCREW HOLES ONLY. UNDERCOAT AND TOP COAT SCENIC PAINT
FINISH TO MATCH SCENIC REFERENCES SUPPLIED BY SET DESIGNER.
FIRE RETARD PAINT ADDITIVE INCLUDED IN UNDERCOAT PAINT.

FROZEN

E.1.3 3D VIEWS
NA@A3

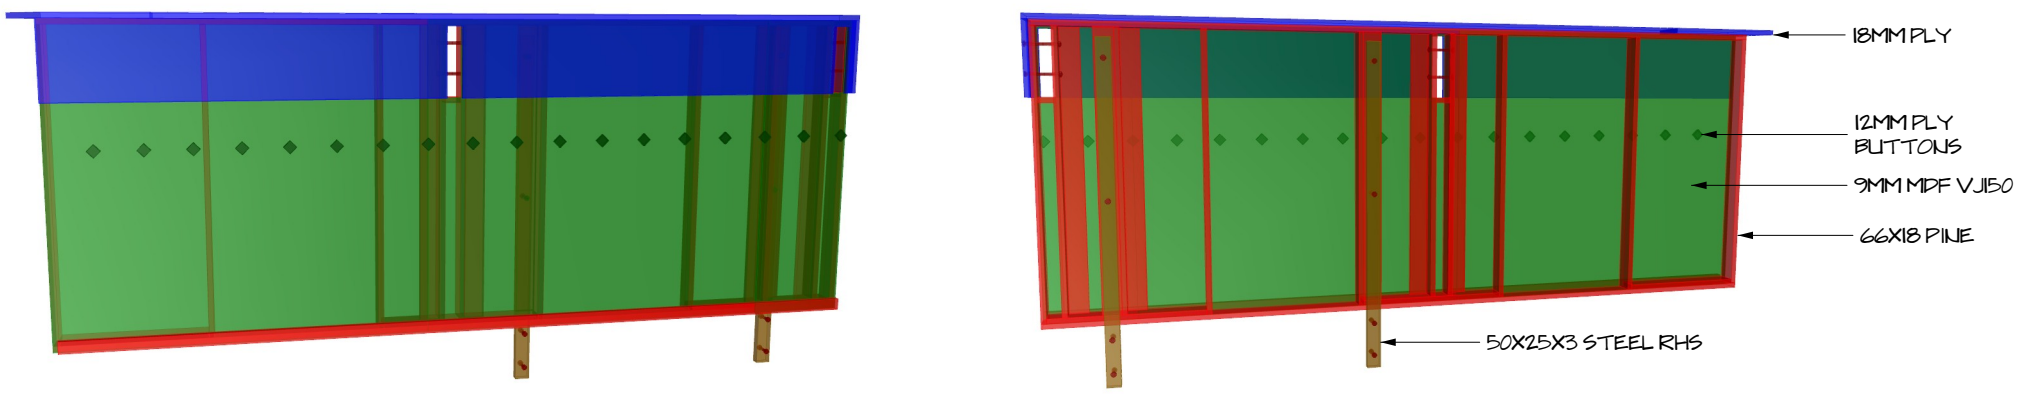

CONSTRUCTION DETAILS

CONSTRUCTED FROM 66X18 PINE FRAMING WITH 9MM MDF VJ150 FACE SKINS. 18MM PLY TOP CAPPING AS SHOWN. PVA GLUE, BRAD NAIL & SCREW FIXING ASSEMBLY.

12MM PLY PLANT ON BUTTON HEADS CENTRED ON VJ150 GROOVES.


REMOVABLE ACCESS PANEL TO BOLT ARCHES INTO FLATS.

SCREW FIX FLATS TO ROLLING TRUCK BASE WITH 10G TIMBER BATTEN SCREWS.


FIX 2 X 50X25X3MM STEEL RHS UPRIGHTS TO REAR FACE OF FLAT AND TRUCK WITH 4 X M10 BOLTS TO SUPPORT CANTILEVERED ARCHES.

FILL SCREW HOLES ONLY. UNDERCOAT AND TOP COAT SCENIC PAINT FINISH TO MATCH SCENIC REFERENCES SUPPLIED BY SET DESIGNER. FIRE RETARD PAINT ADDITIVE INCLUDED IN UNDERCOAT PAINT.


E.1.3 PLAN VIEW
1:10@A3

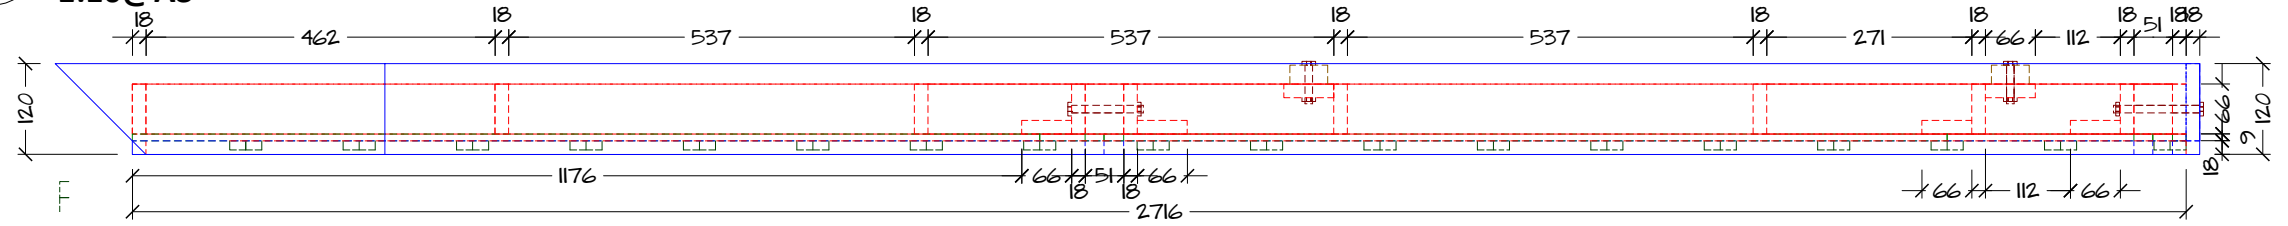

E.1.3 FRONT VIEW
1:10@A3

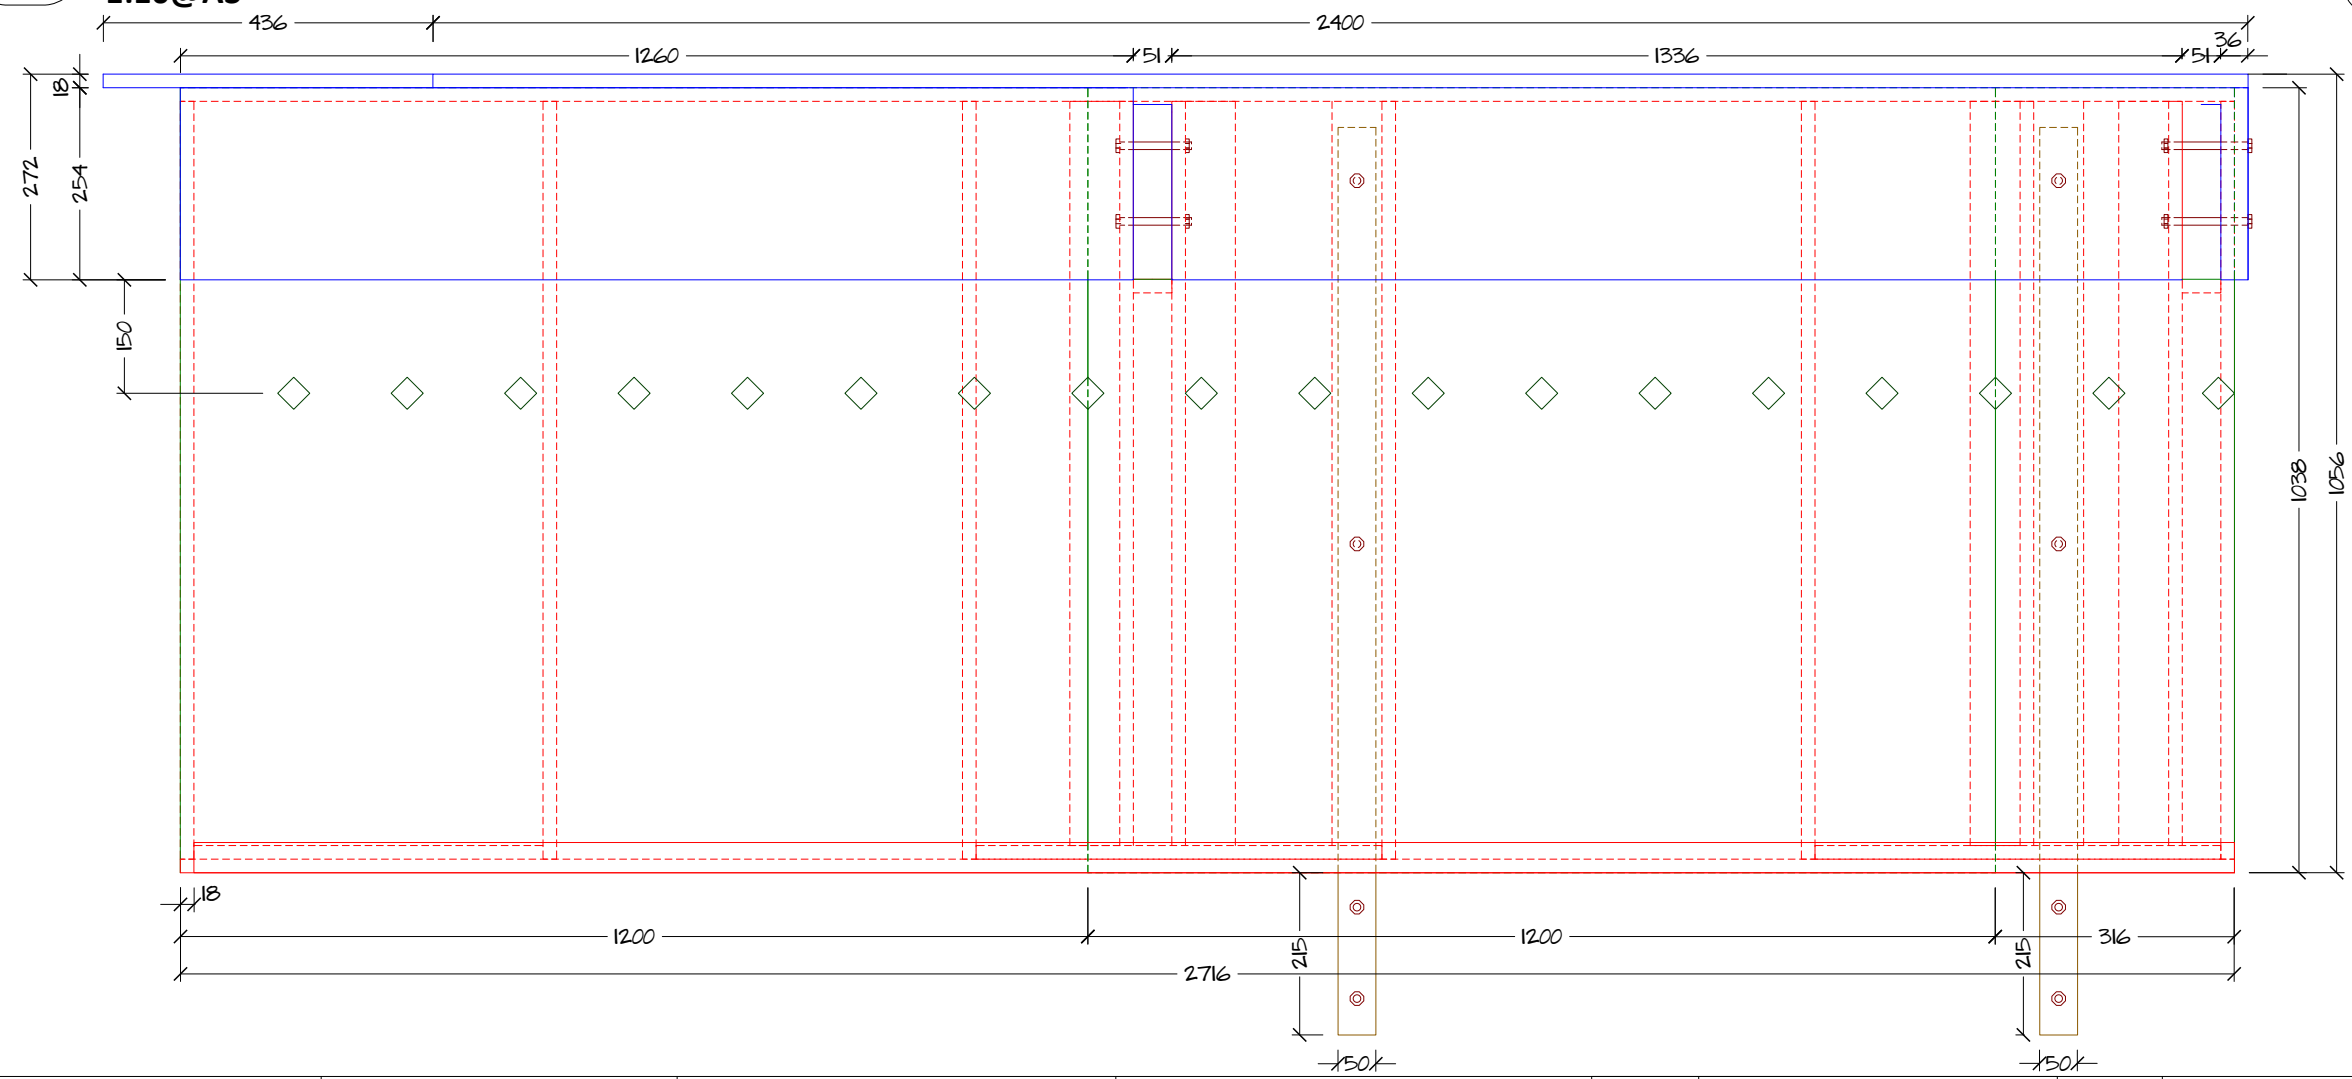

E.1.3 END VIEW
1:10@A3

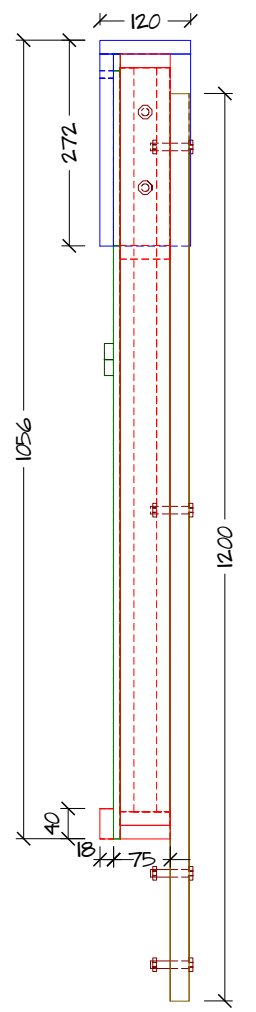

iceworks
design

ICEWORKS DESIGN PTY. LTD.
5/747 Fairfield Rd, Yeerongpilly, QLD. 4105
PO Box 624, Fairfield Gardens, QLD. 4103
T: + 617 3352 4511
www.iceworksdesign.com



THESE DRAWINGS ARE CONCEPT & DESIGN ONLY. FURTHER CONSTRUCTION & DETAIL DRAWINGS MAY BE REQUIRED.

These drawings are © copyright 2025 ICEWORKS DESIGN. Drawings, illustrations & 3D Renders are not to be used, reproduced or copied without permission from ICEWORKS DESIGN. All dimensions are to be checked on site prior to commencing any construction, if in doubt please contact ICEWORKS DESIGN. Do not scale from drawings. Any building work is to comply with the building act, BCA and standard regulations where applicable.

MILLIMETRES

0 100 200 300 400

DESIGN APPROVAL

sign:.....

print name:.....

APPROVED / REVISE [circle]

comments:.....

date:..... /..... /.....


CLIENT:	STODDART ENTERTAINMENT GROUP
PROJECT	FROZEN
DESIGNER:	HARRY GILL
VENUE:	CIVIC THEATRE
ADDRESS:	375 HUNTER ST NEWCASTLE, NSW 2300
JOB No:	26150

DRAWING NAME:	ITEM E.1.3 - REAR FLAT	
DRAWN BY:	GAVIN HAMPSTEAD	
ISSUE:	DATE	DESCRIPTION
	31/07/26	ISSUE FOR COSTING & CLIENT REVIEW
	03/08/26	REVISED. ISSUE FOR COSTING & CLIENT REVIEW
	04/08/26	REVISED. ISSUE FOR COSTING & CLIENT REVIEW
	00/00/00	XXXX
	00/00/00	XXXX
	00/00/00	XXXX


SCALE:	1:10@A3
DWG No:	D05
SHEET No:	6 / 10

FROZEN


E.1.4 PLAN VIEW
1:20@A3

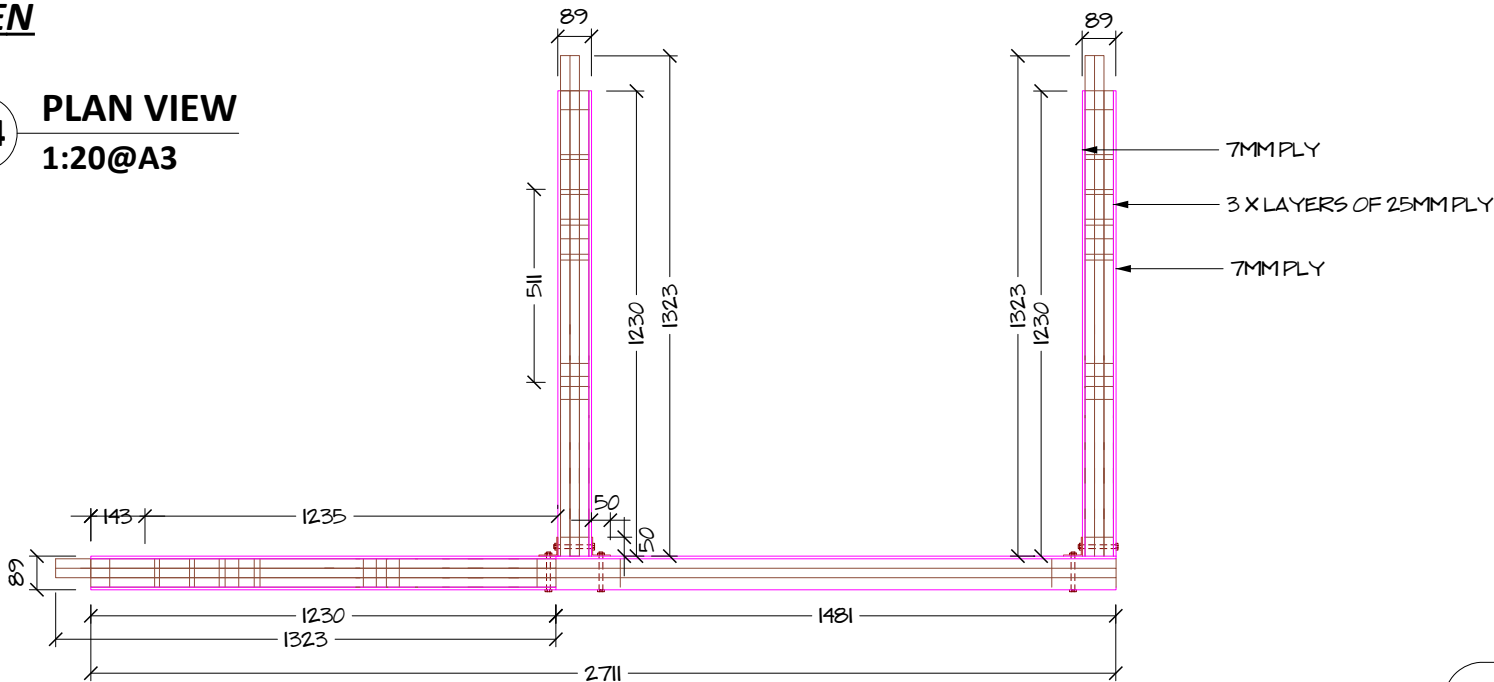

E.1.4 FRONT VIEW
1:20@A3

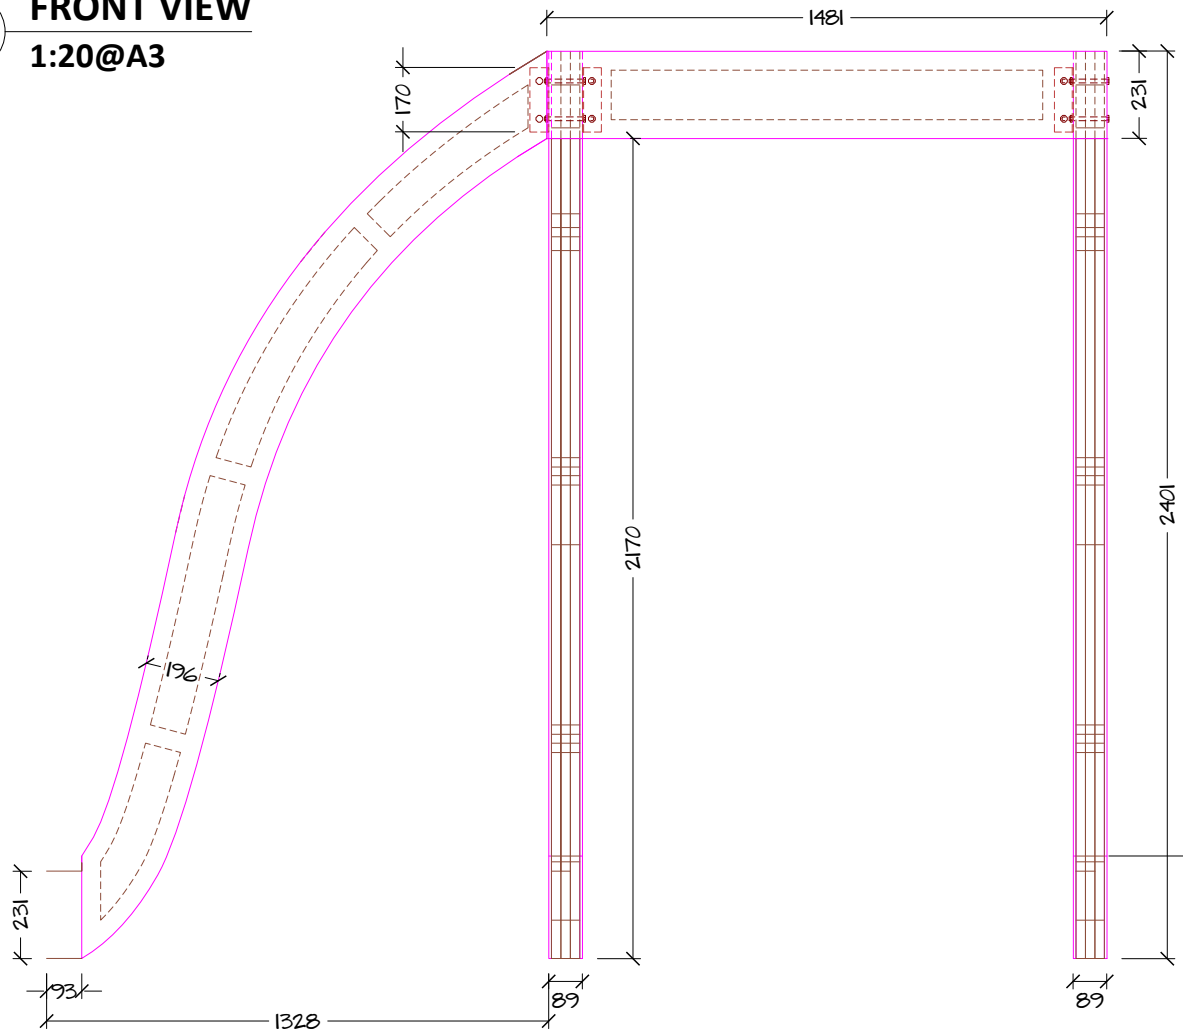

E.1.4 END VIEW
1:20@A3

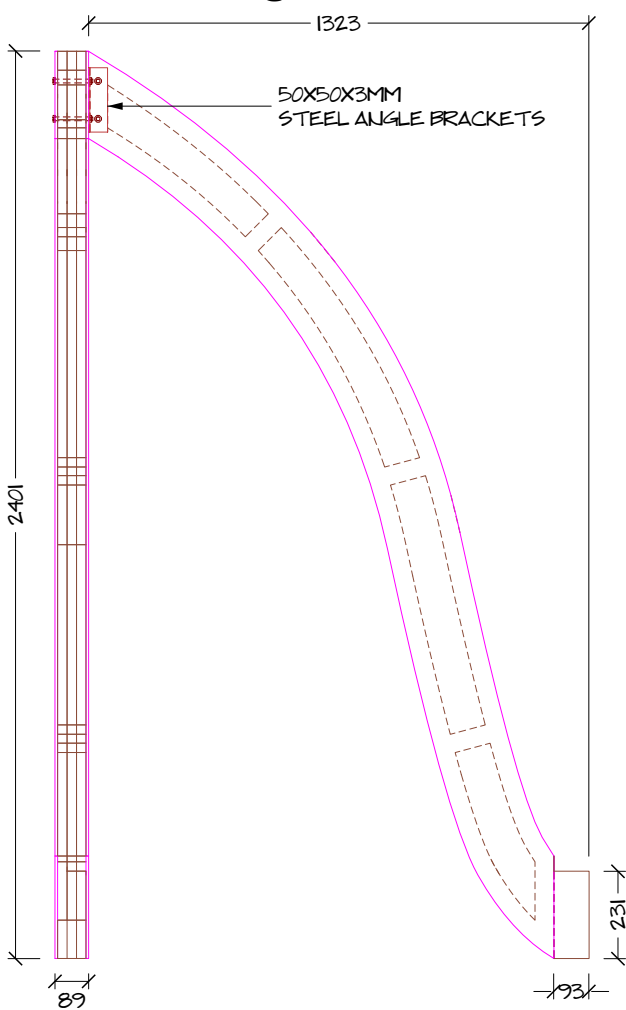

CONSTRUCTION DETAILS


CONSTRUCTED FROM 25MM PLY FORMERS CNC CUT TO SHAPE WITH 7MM PLY EXTERNAL SKINS, PVA GLUE, BRAD NAIL & SCREW FIXING ASSEMBLY.

ASSEMBLE ARCHES TOGETHER WITH 50X50X3MM STEEL ANGLE BRACKETS & 100MM M10 BOLTS AS SHOWN.

FIX ARCH INTO OFF STAGE & REAR FLATS WITH M10 BOLTS.

FILL SCREW HOLES ONLY. UNDERCOAT AND TOP COAT SCENIC PAINT FINISH TO MATCH SCENIC REFERENCES SUPPLIED BY SET DESIGNER. FIRE RETARD PAINT ADDITIVE INCLUDED IN UNDERCOAT PAINT.

E.1.4 3D VIEWS
NA@A3

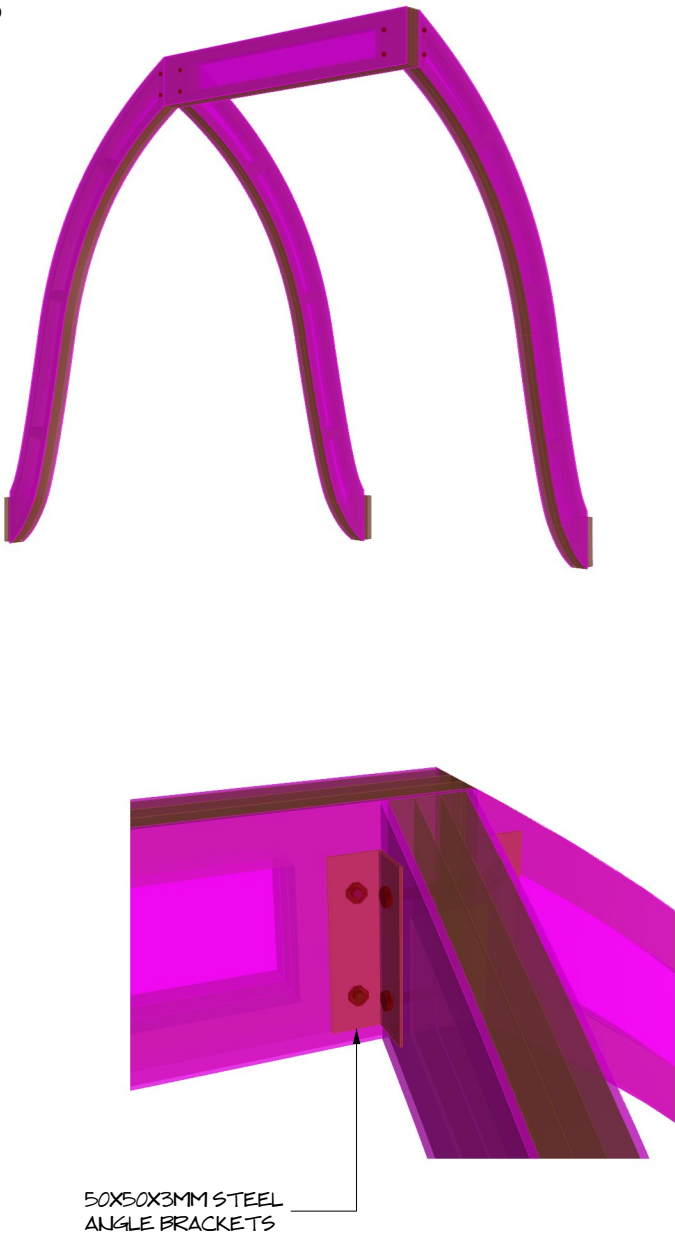


iceworks
design

ICEWORKS DESIGN PTY. LTD.
5/747 Fairfield Rd, Yeerongpilly, QLD. 4105
PO Box 624, Fairfield Gardens, QLD. 4103
T: + 617 3352 4511
www.iceworksdesign.com



THESE DRAWINGS ARE CONCEPT & DESIGN ONLY.
FURTHER CONSTRUCTION & DETAIL DRAWINGS
MAY BE REQUIRED.

These drawings are © copyright 2025 ICEWORKS DESIGN.
Drawings, illustrations & 3D Renders are not to be used,
reproduced or copied without permission from ICEWORKS DESIGN.
All dimensions are to be checked on site prior to commencing any
construction, if in doubt please contact ICEWORKS DESIGN. Do
not scale from
drawings. Any building work is to comply with the building act,
BCA and standard regulations where applicable.

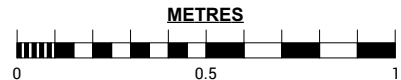

DESIGN APPROVAL

sign:.....
print name:.....
APPROVED / REVISE [circle]
comments.....
date:..... /..... /.....


CLIENT:	STODDART ENTERTAINMENT GROUP
PROJECT	FROZEN
DESIGNER:	HARRY GILL
VENUE:	CIVIC THEATRE
ADDRESS:	375 HUNTER ST NEWCASTLE, NSW 2300
JOB No:	26150

DRAWING NAME:	ITEM E.1.4 - ARCHES
DRAWN BY:	GAVIN HAMPSTEAD
ISSUE:	DATE DESCRIPTION
	31/07/26 ISSUE FOR COSTING & CLIENT REVIEW
	03/08/26 REVISED. ISSUE FOR COSTING & CLIENT REVIEW
	04/08/26 REVISED. ISSUE FOR COSTING & CLIENT REVIEW
	00/00/00 XXXX
	00/00/00 XXXX
	00/00/00 XXXX


SCALE:	1:15@A3
DWG No:	D06
SHEET No:	7 / 10

FROZEN


E.3 PLAN VIEW
1:15@A3

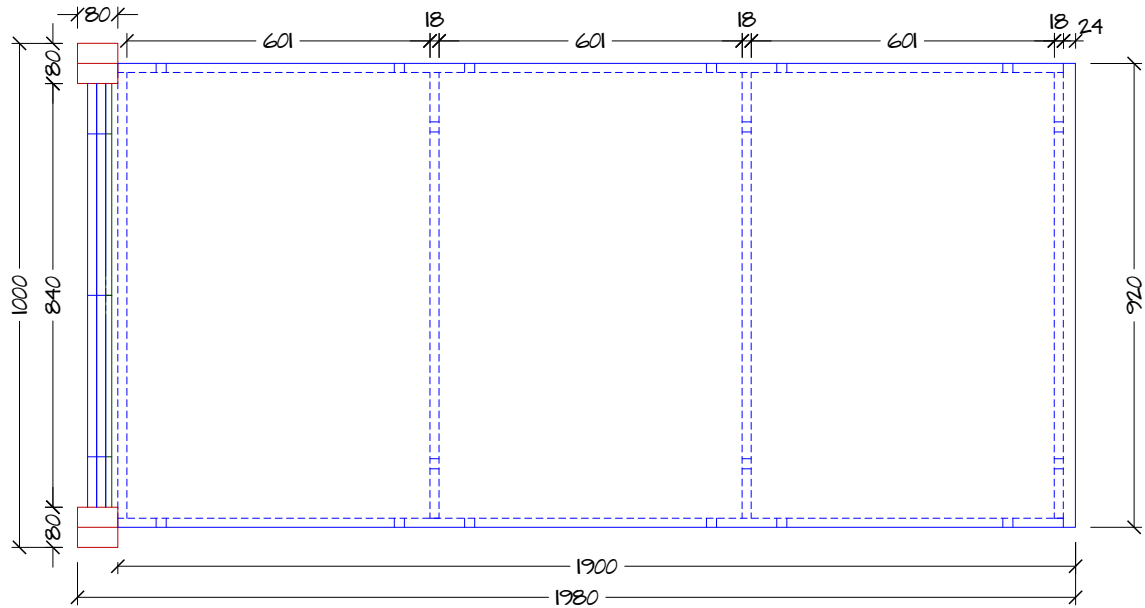

E.3 FRONT VIEW
1:15@A3

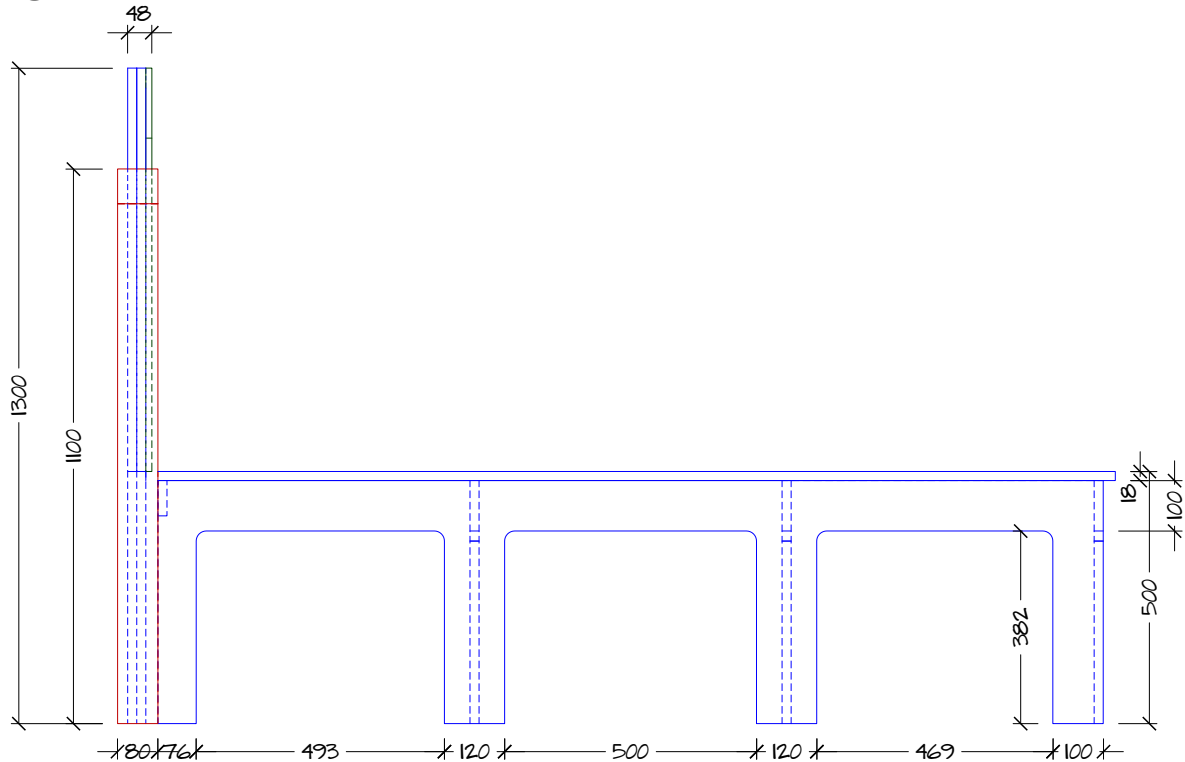

E.3 END VIEW
1:15@A3

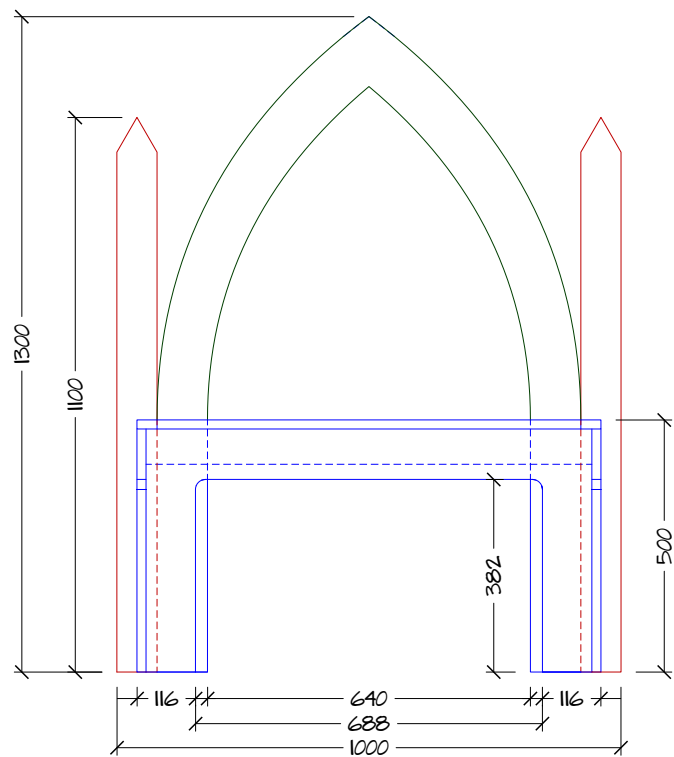


CONSTRUCTION DETAILS

BED BASE FRAME CONSTRUCTED FROM 18MM SELEX PLY CNC CUT TO SHAPE. BEDHEAD CONSTRUCTED FROM 2 X LAYERS OF 18MM & 1 X LAYER OF 12MM SELEX PLY CNC CUT TO SHAPE. PVA GLUE, BRAD NAIL & SCREW FIXING ASSEMBLY.

FILL SCREW HOLES ONLY. UNDERCOAT AND TOP COAT SCENIC PAINT FINISH BEDHEAD TO MATCH SCENIC REFERENCES SUPPLIED BY SET DESIGNER. FIRE RETARD PAINT ADDITIVE INCLUDED IN UNDERCOAT PAINT. PAINT BED BASE FRAME LOW SHEEN BLACK ONLY.

E.3 3D VIEW
NA@A3

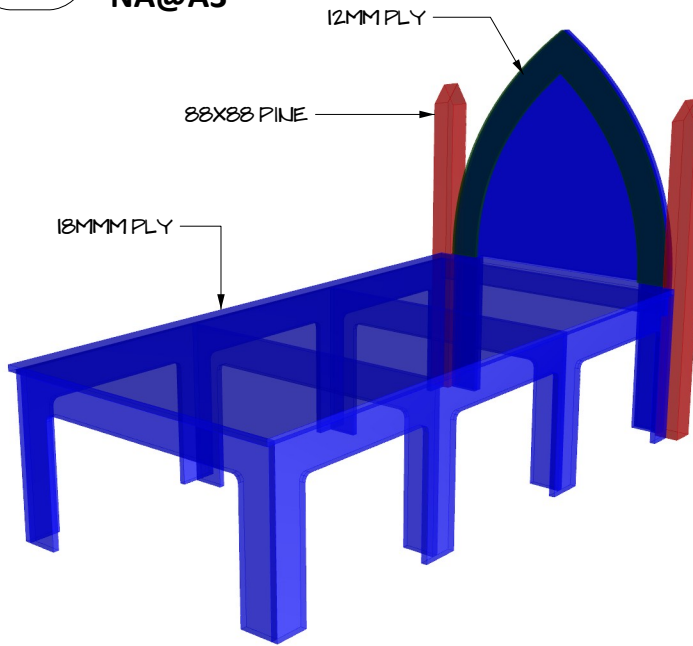


iceworks
design

ICEWORKS DESIGN PTY. LTD.
5/747 Fairfield Rd, Yeerongpilly, QLD. 4105
PO Box 624, Fairfield Gardens, QLD. 4103
T: + 617 3352 4511
www.iceworksdesign.com



THESE DRAWINGS ARE CONCEPT & DESIGN ONLY.
FURTHER CONSTRUCTION & DETAIL DRAWINGS
MAY BE REQUIRED.

These drawings are © copyright 2025 ICEWORKS DESIGN.
Drawings, illustrations & 3D Renders are not to be used,
reproduced or copied without permission from ICEWORKS DESIGN.
All dimensions are to be checked on site prior to commencing any
construction, if in doubt please contact ICEWORKS DESIGN. Do
not scale from
drawings. Any building work is to comply with the building act,
BCA and standard regulations where applicable.

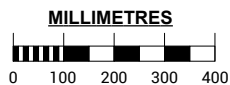

DESIGN APPROVAL

sign:.....
print name:.....
APPROVED / REVISE [circle]
comments.....
date:..... /..... /.....


CLIENT:	STODDART ENTERTAINMENT GROUP
PROJECT	FROZEN
DESIGNER:	HARRY GILL
VENUE:	CIVIC THEATRE
ADDRESS:	375 HUNTER ST NEWCASTLE, NSW 2300
JOB No:	26150

DRAWING NAME:	ITEM E.3 - BEDS X 2	
DRAWN BY:	GAVIN HAMPSTEAD	
ISSUE:	DATE	DESCRIPTION
	31/07/26	ISSUE FOR COSTING & CLIENT REVIEW
	03/08/26	REVISED. ISSUE FOR COSTING & CLIENT REVIEW
	04/08/26	REVISED. ISSUE FOR COSTING & CLIENT REVIEW
	00/00/00	XXXX
	00/00/00	XXXX
	00/00/00	XXXX


SCALE:	1:15@A3
DWG No:	D07
SHEET No:	8 / 10

FROZEN


E.4 PLAN VIEW
1:10@A3

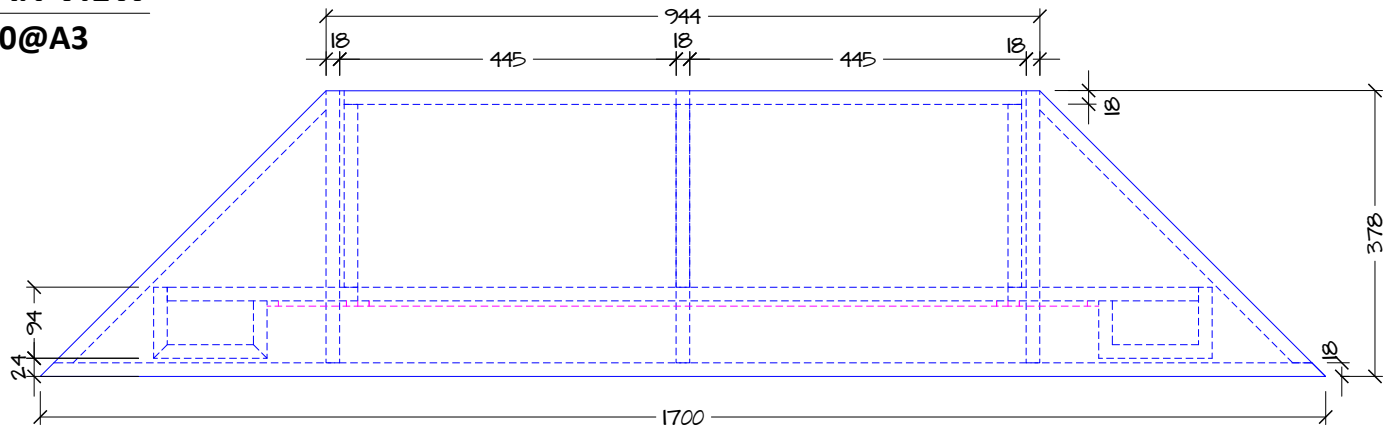

E.4 FRONT VIEW
1:10@A3

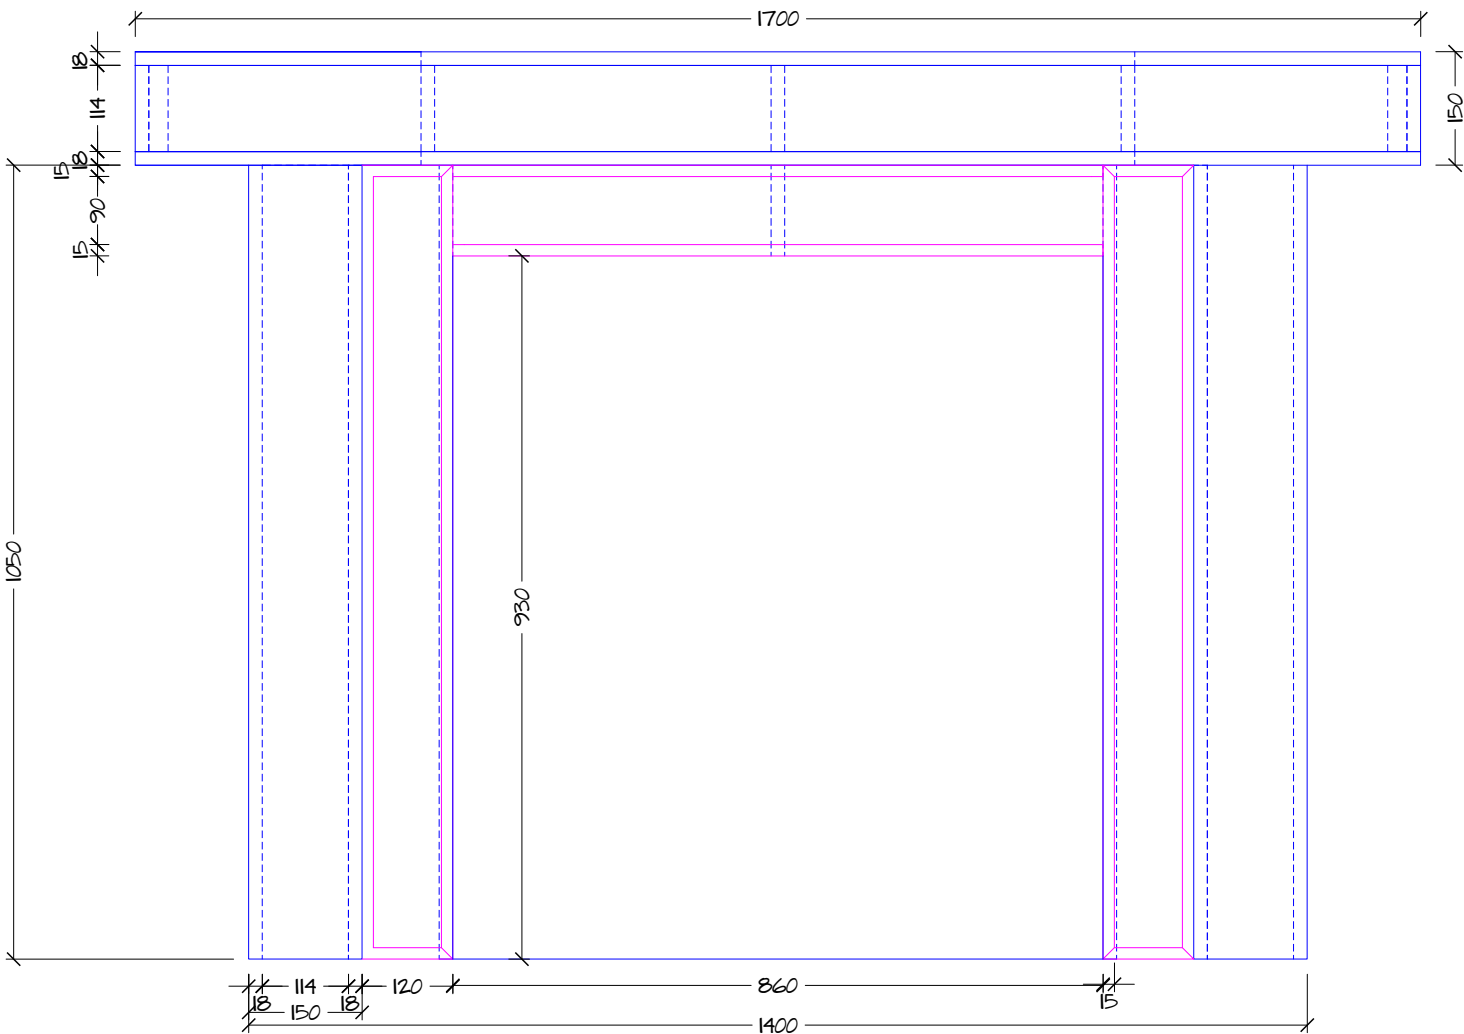

E.4 END VIEW
1:10@A3

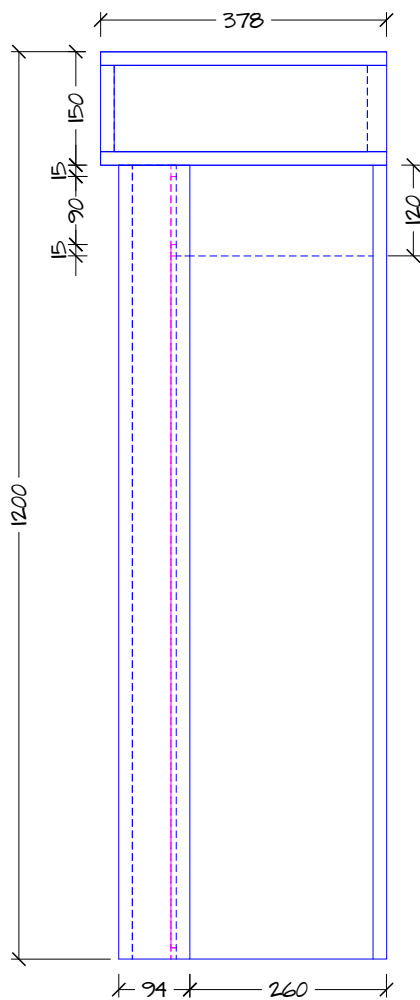


CONSTRUCTION DETAILS

CONSTRUCTED FROM 18MM SELEX PLY CNC CUT TO SHAPE. 7MM PLY PLANT ON DETAIL STRIPS. PVA GLUE, BRAD NAIL & SCREW FIXING ASSEMBLY.

FILL SCREW HOLES ONLY. UNDERCOAT AND TOP COAT SCENIC PAINT FINISH BEDHEAD TO MATCH SCENIC REFERENCES SUPPLIED BY SET DESIGNER. FIRE RETARD PAINT ADDITIVE INCLUDED IN UNDERCOAT PAINT. PAINT BED BASE FRAME LOW SHEEN BLACK ONLY.

E.5 3D VIEW
NA@A3

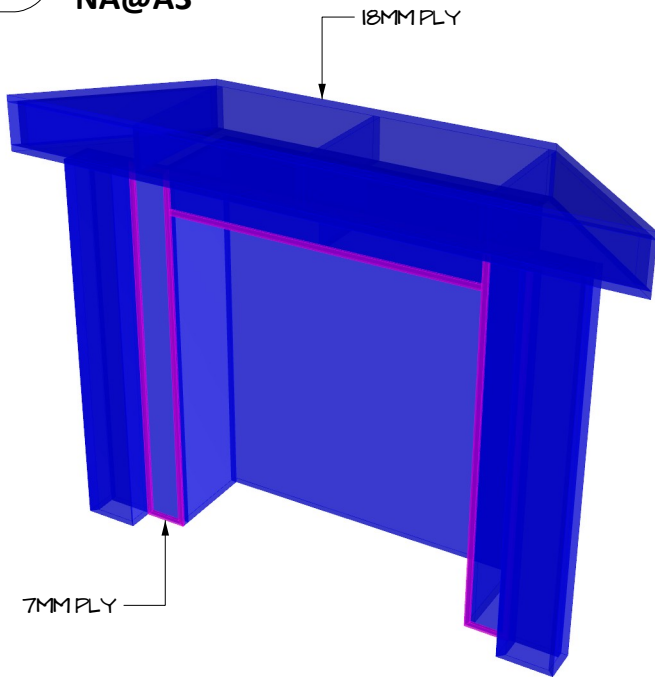


iceworks
design

ICEWORKS DESIGN PTY. LTD.
5/747 Fairfield Rd, Yeerongpilly, QLD. 4105
PO Box 624, Fairfield Gardens, QLD. 4103
T: + 617 3352 4511
www.iceworksdesign.com



THESE DRAWINGS ARE CONCEPT & DESIGN ONLY.
FURTHER CONSTRUCTION & DETAIL DRAWINGS
MAY BE REQUIRED.

These drawings are © copyright 2025 ICEWORKS DESIGN.
Drawings, illustrations & 3D Renders are not to be used,
reproduced or copied without permission from ICEWORKS DESIGN.
All dimensions are to be checked on site prior to commencing any
construction, if in doubt please contact ICEWORKS DESIGN. Do
not scale from
drawings. Any building work is to comply with the building act,
BCA and standard regulations where applicable.

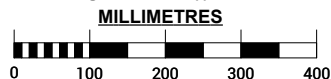

DESIGN APPROVAL


sign:.....
print name:.....
APPROVED / REVISE [circle]
comments.....
date:..... /..... /.....

CLIENT:	STODDART ENTERTAINMENT GROUP
PROJECT	FROZEN
DESIGNER:	HARRY GILL
VENUE:	CIVIC THEATRE
ADDRESS:	375 HUNTER ST NEWCASTLE, NSW 2300
JOB No:	26150


DRAWING NAME:	ITEM E.4 - FIREPLACE	
DRAWN BY:	GAVIN HAMPSTEAD	
ISSUE:	DATE	DESCRIPTION
	31/07/26	ISSUE FOR COSTING & CLIENT REVIEW
	03/08/26	REVISED. ISSUE FOR COSTING & CLIENT REVIEW
	04/08/26	REVISED. ISSUE FOR COSTING & CLIENT REVIEW
	00/00/00	XXXX
	00/00/00	XXXX
	00/00/00	XXXX

SCALE:	1:10@A3
DWG No:	D08
SHEET No:	9 / 10


ITEM E.I.4 - QTY X 2 - 25MM PLY. 7MM PLY.

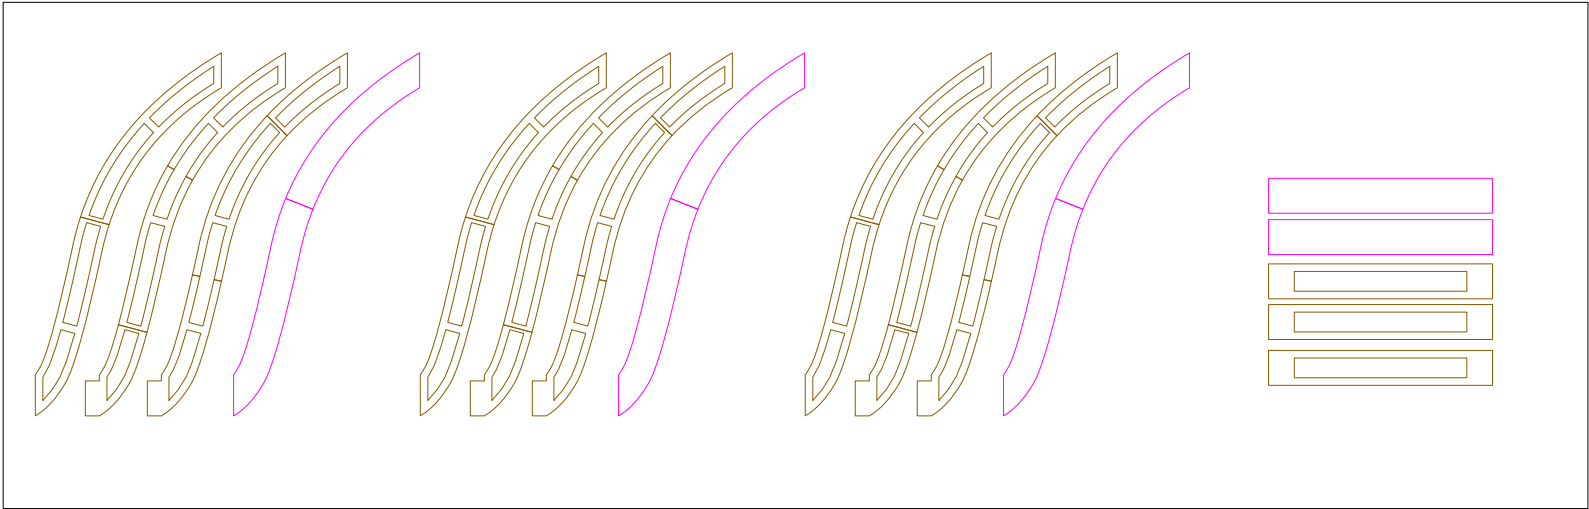


ITEM E.I.I - QTY X 2 - 18MM PLY. 12MM PLY. 12MM UHPPE

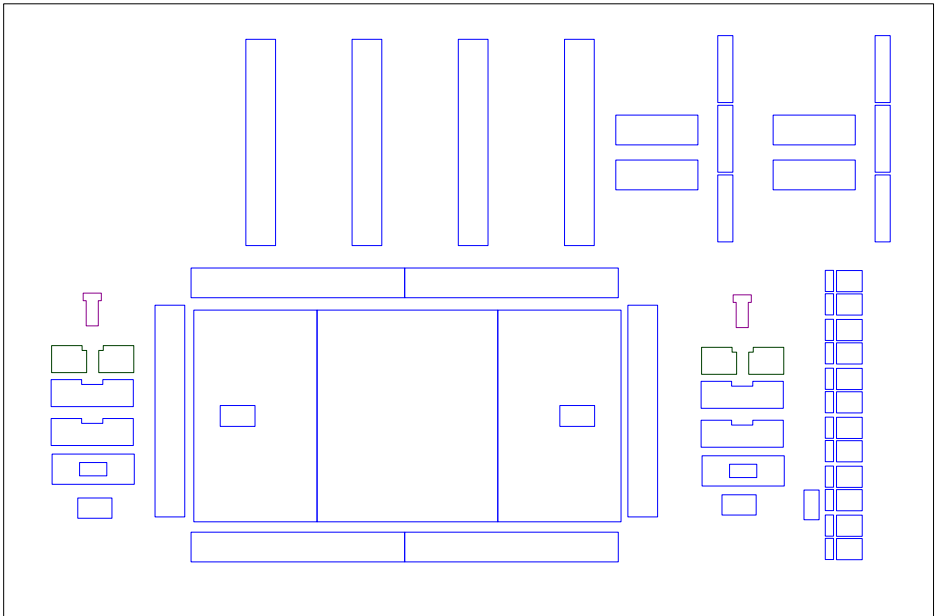


ITEM E.3 - QTY X 2 - 18MM PLY. 12MM PLY.

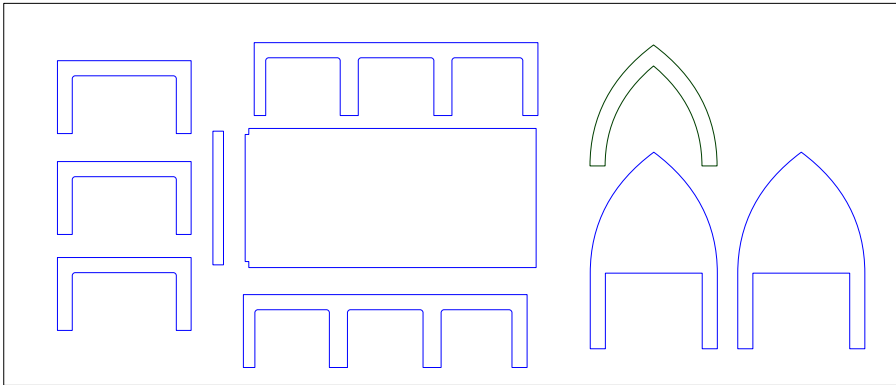

ITEM E.5 - QTY X 1 - 18MM PLY. 7MM PLY.

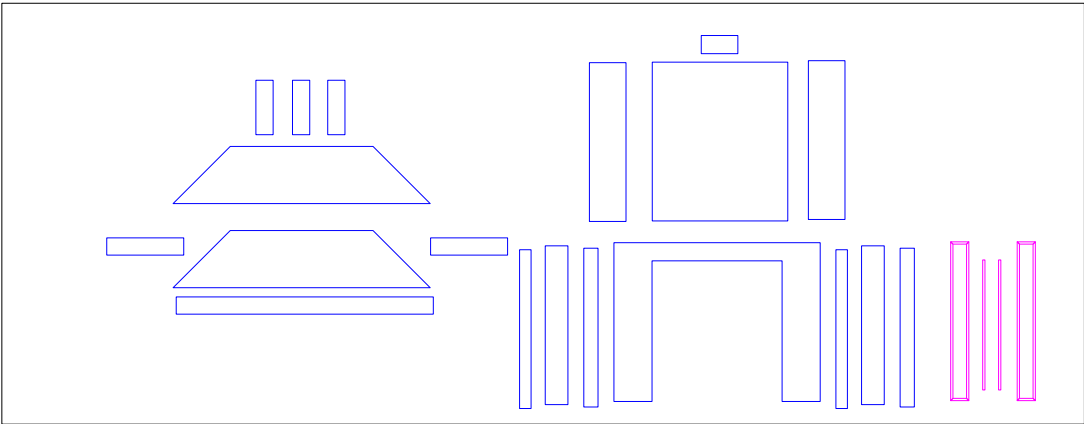

ITEM E.I.2 & E.I.3 - QTY X 2 - 12MM PLY

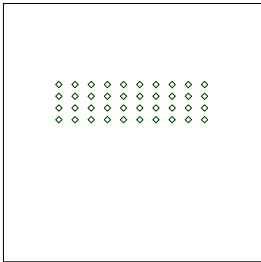


ICEWORKS DESIGN PTY. LTD.
5/747 Fairfield Rd, Yeerongpilly, QLD. 4105
PO Box 624, Fairfield Gardens, QLD. 4103
T: + 617 3352 4511
www.iceworksdesign.com



THESE DRAWINGS ARE CONCEPT & DESIGN ONLY.
FURTHER CONSTRUCTION & DETAIL DRAWINGS
MAY BE REQUIRED.

These drawings are © copyright 2025 ICEWORKS DESIGN.
Drawings, illustrations & 3D Renders are not to be used,
reproduced or copied without permission from ICEWORKS DESIGN.
All dimensions are to be checked on site prior to commencing any
construction, if in doubt please contact ICEWORKS DESIGN. Do
not scale from
drawings. Any building work is to comply with the building act,
BCA and standard regulations where applicable.

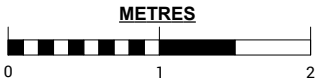

DESIGN APPROVAL

sign:.....
print name:.....
APPROVED / REVISE [circle]
comments.....
date:..... /..... /.....

CLIENT:	STODDART ENTERTAINMENT GROUP
PROJECT	FROZEN
DESIGNER:	HARRY GILL
VENUE:	CIVIC THEATRE
ADDRESS:	375 HUNTER ST NEWCASTLE, NSW 2300
JOB No:	26150

DRAWING NAME:	CNC FILES	
DRAWN BY:	GAVIN HAMPSTEAD	
ISSUE:	DATE	DESCRIPTION
	31/07/26	ISSUE FOR COSTING & CLIENT REVIEW
	03/08/26	REVISED. ISSUE FOR COSTING & CLIENT REVIEW
	04/08/26	REVISED. ISSUE FOR COSTING & CLIENT REVIEW
	00/00/00	XXXX
	00/00/00	XXXX
	00/00/00	XXXX

SCALE:	1:50@A3
DWG No:	D09
SHEET No:	10 / 10