

SHEET#	DWG#	DRAWING NAME
1	CP	COVER PAGE
2	D01	ITEM A - SHOW FLOOR VENUE FLOOR PLAN
3	D02	ITEM A - SHOW FLOOR DETAILS




FROZEN

ITEM A - SHOW FLOOR
CONSTRUCTION DESIGN
PLAN SET V3
24/07/26

 ICEWORKS DESIGN PTY. LTD. 5/747 Fairfield Rd, Yeerongpilly, QLD. 4105 PO Box 624, Fairfield Gardens, QLD. 4103 T: + 617 3352 4511 www.iceworksdesign.com		THESE DRAWINGS ARE CONCEPT & DESIGN ONLY. FURTHER CONSTRUCTION & DETAIL DRAWINGS MAY BE REQUIRED. These drawings are © copyright 2025 ICEWORKS DESIGN. Drawings, illustrations & 3D Renders are not to be used, reproduced or copied without permission from ICEWORKS DESIGN. All dimensions are to be checked on site prior to commencing any construction, if in doubt please contact ICEWORKS DESIGN. Do not scale from drawings. Any building work is to comply with the building act, BCA and standard regulations where applicable.	DESIGN APPROVAL sign:..... print name:..... APPROVED / REVISE [circle] comments..... date:..... /..... /.....	CLIENT:	STODDART ENTERTAINMENT GROUP	DRAWING NAME:	COVER PAGE	SCALE:	N/A @ A3
				PROJECT	FROZEN	DRAWN BY:	GAVIN HAMPSTEAD	DWG No:	CP
				DESIGNER:	HARRY GILL	ISSUE:	DATE	DESCRIPTION	SHEET No:
				VENUE:	CIVIC THEATRE		22/07/26	ISSUE FOR COSTING & CLIENT REVIEW	
				ADDRESS:	375 HUNTER ST NEWCASTLE, NSW 2300		23/07/26	REVISED. ISSUE FOR CLIENT APPROVAL FOR CONSTRUCTION	
				JOB No:	26150		24/07/26	FEATHER EDGE ADDED. ISSUE FOR CLIENT APPROVAL.	
							00/00/00	XXXX	
							00/00/00	XXXX	
							00/00/00	XXXX	

A PLAN VIEW
1:100A3

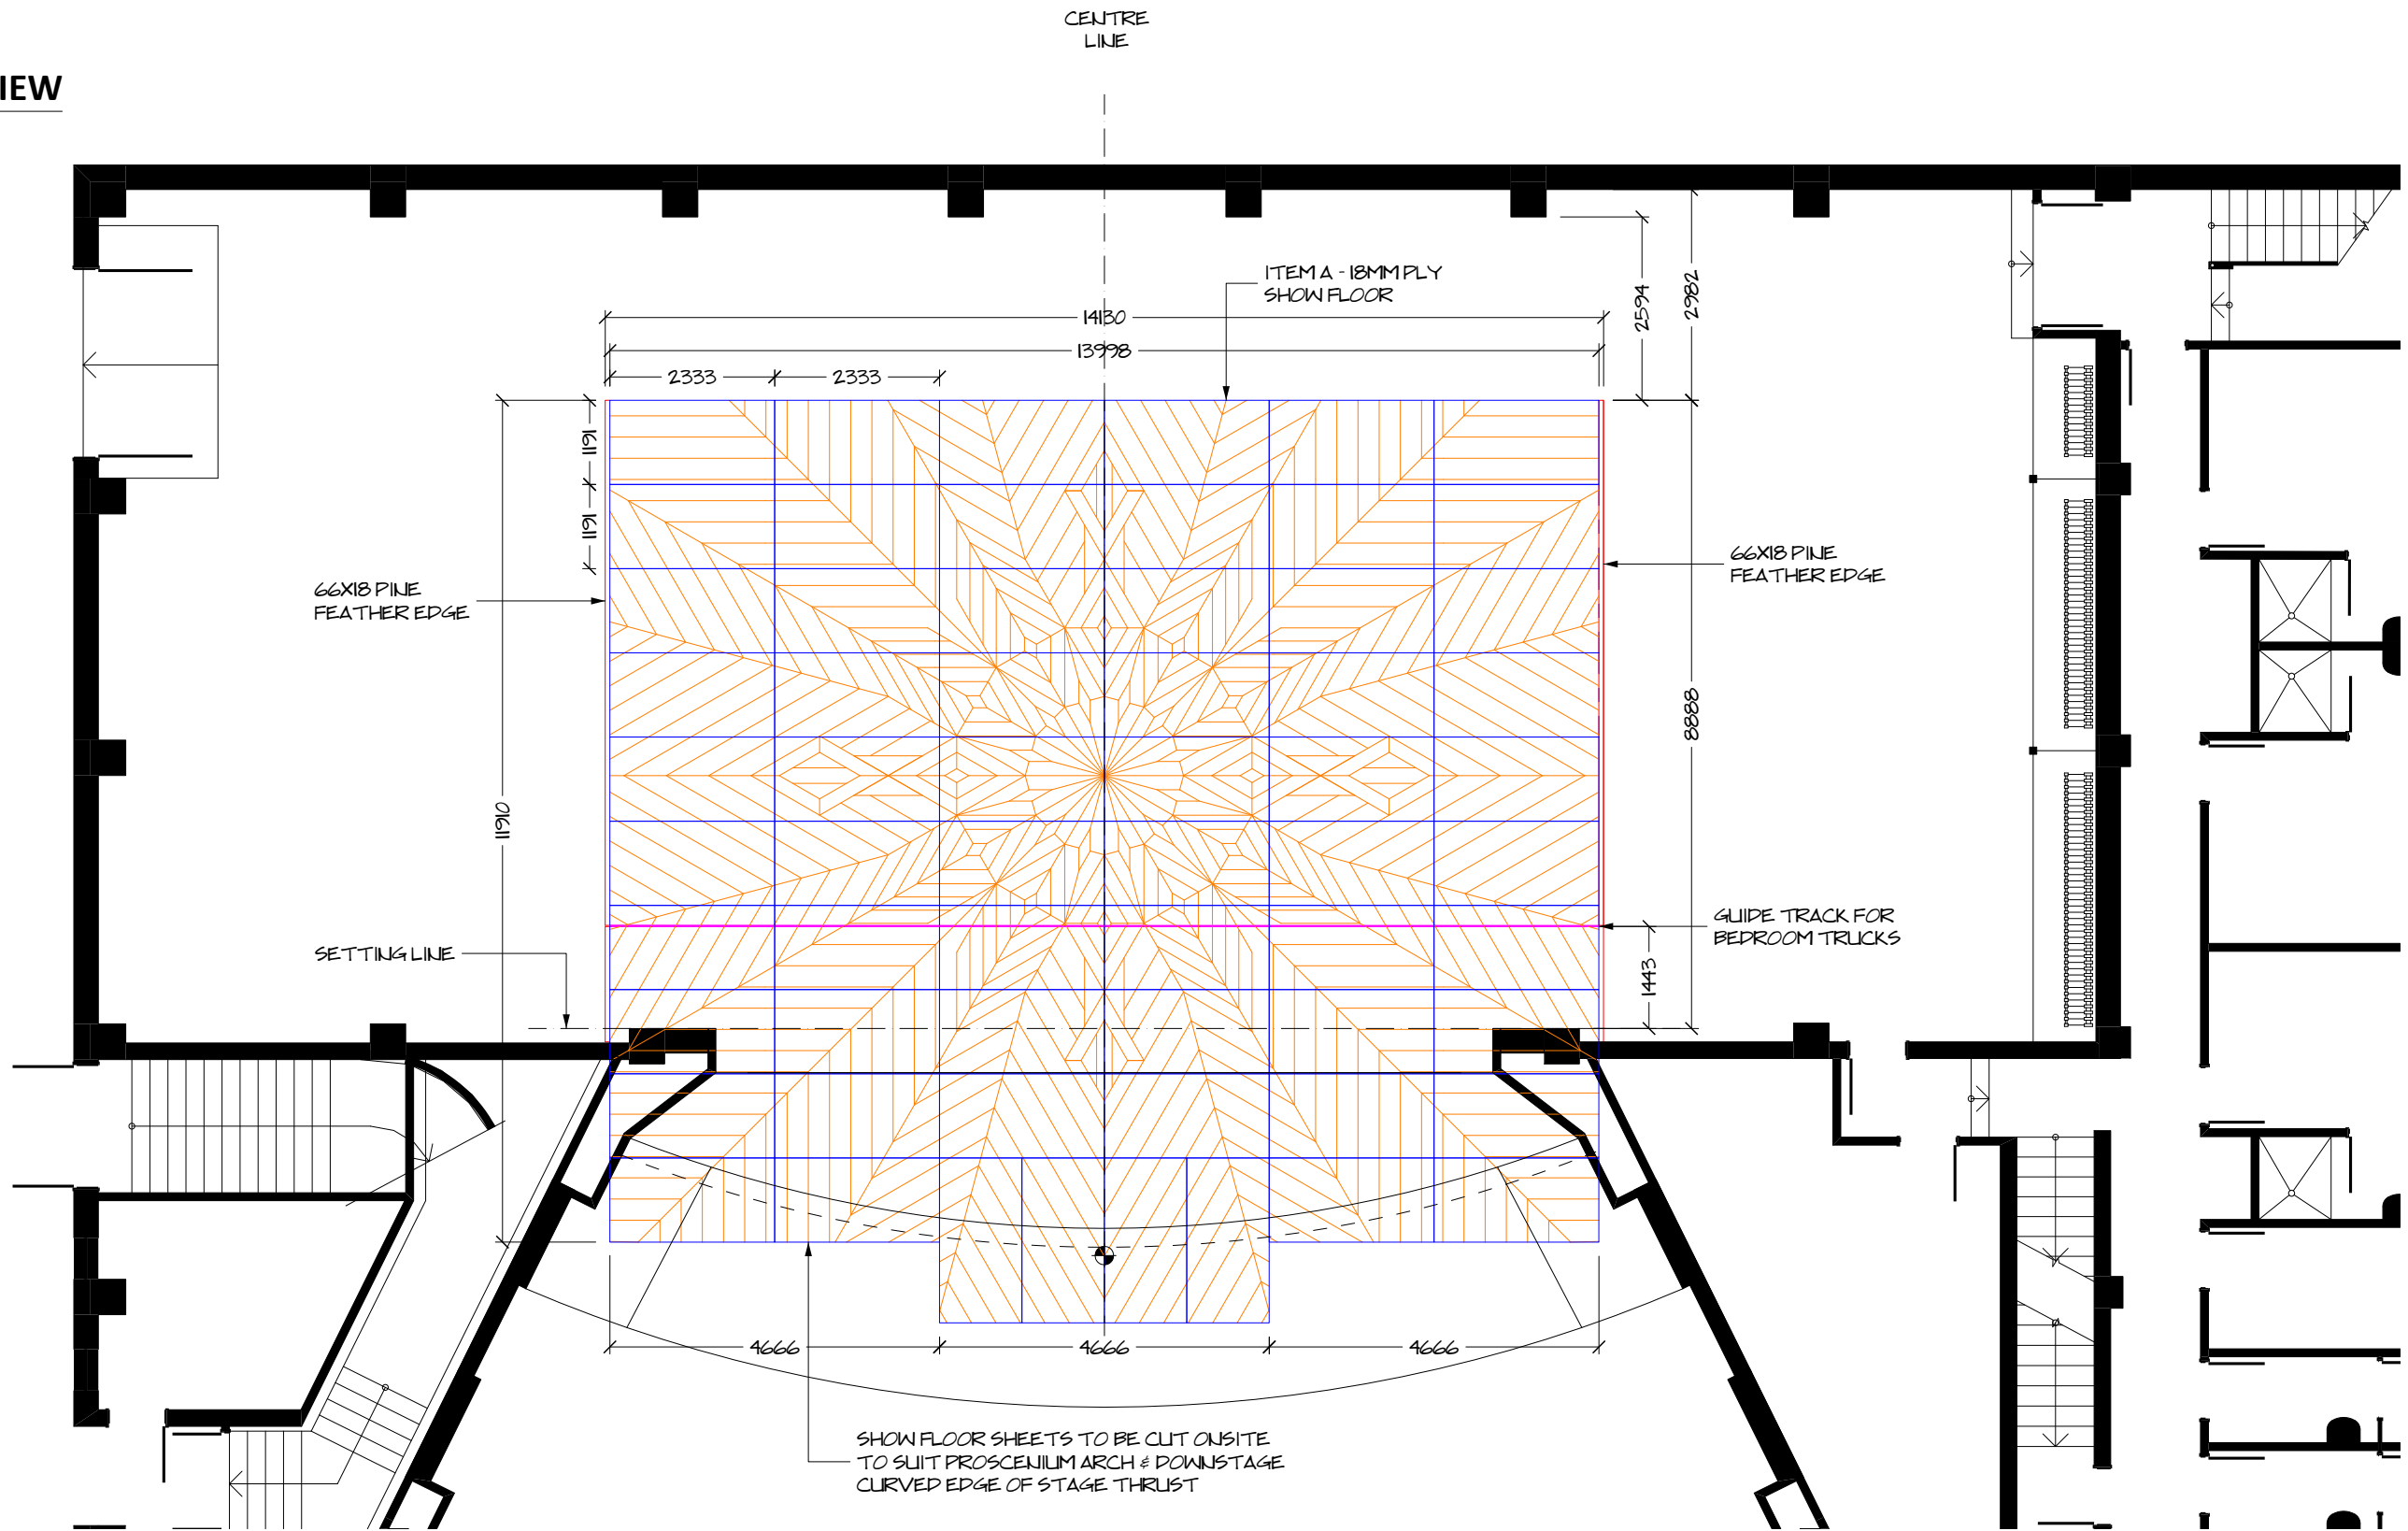


iceworks
design

ICEWORKS DESIGN PTY. LTD.
5/747 Fairfield Rd, Yeerongpilly, QLD. 4105
PO Box 624, Fairfield Gardens, QLD. 4103
T: + 617 3352 4511
www.iceworksdesign.com



THESE DRAWINGS ARE CONCEPT & DESIGN ONLY.
FURTHER CONSTRUCTION & DETAIL DRAWINGS
MAY BE REQUIRED.

These drawings are © copyright 2025 ICEWORKS DESIGN.
Drawings, illustrations & 3D Renders are not to be used,
reproduced or copied without permission from ICEWORKS DESIGN.
All dimensions are to be checked on site prior to commencing any
construction, if in doubt please contact ICEWORKS DESIGN. Do
not scale from
drawings. Any building work is to comply with the building act,
BCA and standard regulations where applicable.

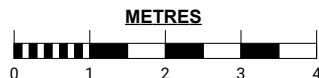

DESIGN APPROVAL

sign:.....
print name:.....
APPROVED / REVISE [circle]
comments.....
date:..... /..... /.....


CLIENT:	STODDART ENTERTAINMENT GROUP
PROJECT	FROZEN
DESIGNER:	HARRY GILL
VENUE:	CIVIC THEATRE
ADDRESS:	375 HUNTER ST NEWCASTLE, NSW 2300
JOB No:	26150

DRAWING NAME:	ITEM A - SHOW FLOOR VENUE FLOOR PLAN	
DRAWN BY:	GAVIN HAMPSTEAD	
ISSUE:	DATE	DESCRIPTION
	22/07/26	ISSUE FOR COSTING & CLIENT REVIEW
	23/07/26	REVISED. ISSUE FOR CLIENT APPROVAL FOR CONSTRUCTION
	24/07/26	FEATHER EDGE ADDED. ISSUE FOR CLIENT APPROVAL
	00/00/00	XXXX
	00/00/00	XXXX
	00/00/00	XXXX


SCALE:	1:100 @ A3
DWG No:	D01
SHEET No:	2 / 3

FROZEN

DETAIL FRONT VIEW
1:2@A3

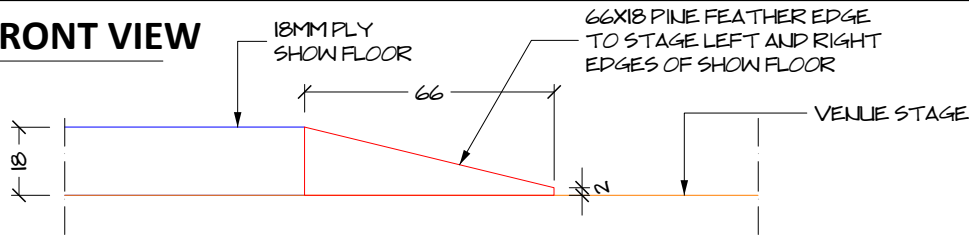

DETAIL END VIEW
1:2@A3

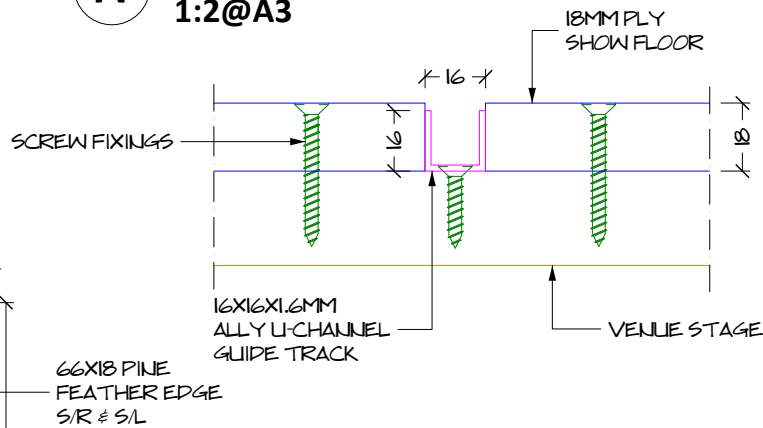

CONSTRUCTION DETAILS

MAKE 1 X ITEM AS SHOWN.


CONSTRUCTED FROM 18MM SELEX PLY, CNC CUT TO SHAPE. DECORATIVE PATTERN DETAIL CNC CUT 5MM WIDE V GROOVES INTO TOP FACE. SCENIC PAINT FINISH TO MATCH SCENIC REFERENCE IMAGE SUPPLIED BY SET DESIGNER.

SCREW FIX 16X16X1.6MM ALUMINIUM U-CHANNEL TO VENUE FLOOR WITH COUNTERSUNK 19MM 8G TIMBER SCREWS BETWEEN SHOW FLOOR SHEETS TO CREATE GUIDE TRACK FOR BEDROOM TRUCKS.


MAKE 2 X FEATHER EDGES FROM 66X18 PINE. CUT ANGLE AS SHOWN. PAINT FINISH LOW SHEEN BLACK. SCREW FIX OR GAFFA TAPE IN POSITION ON SITE.

SCREW FIX SHOW FLOOR SHEETS TO VENUE FLOOR WITH 35MM COUNTERSUNK 8G TIMBER SCREWS TBC BY PRODUCTION MANAGER & CIVIC THEATRE TO CONFIRM STAGE FLOOR THICKNESS.

PLAN VIEW
1:75@A3

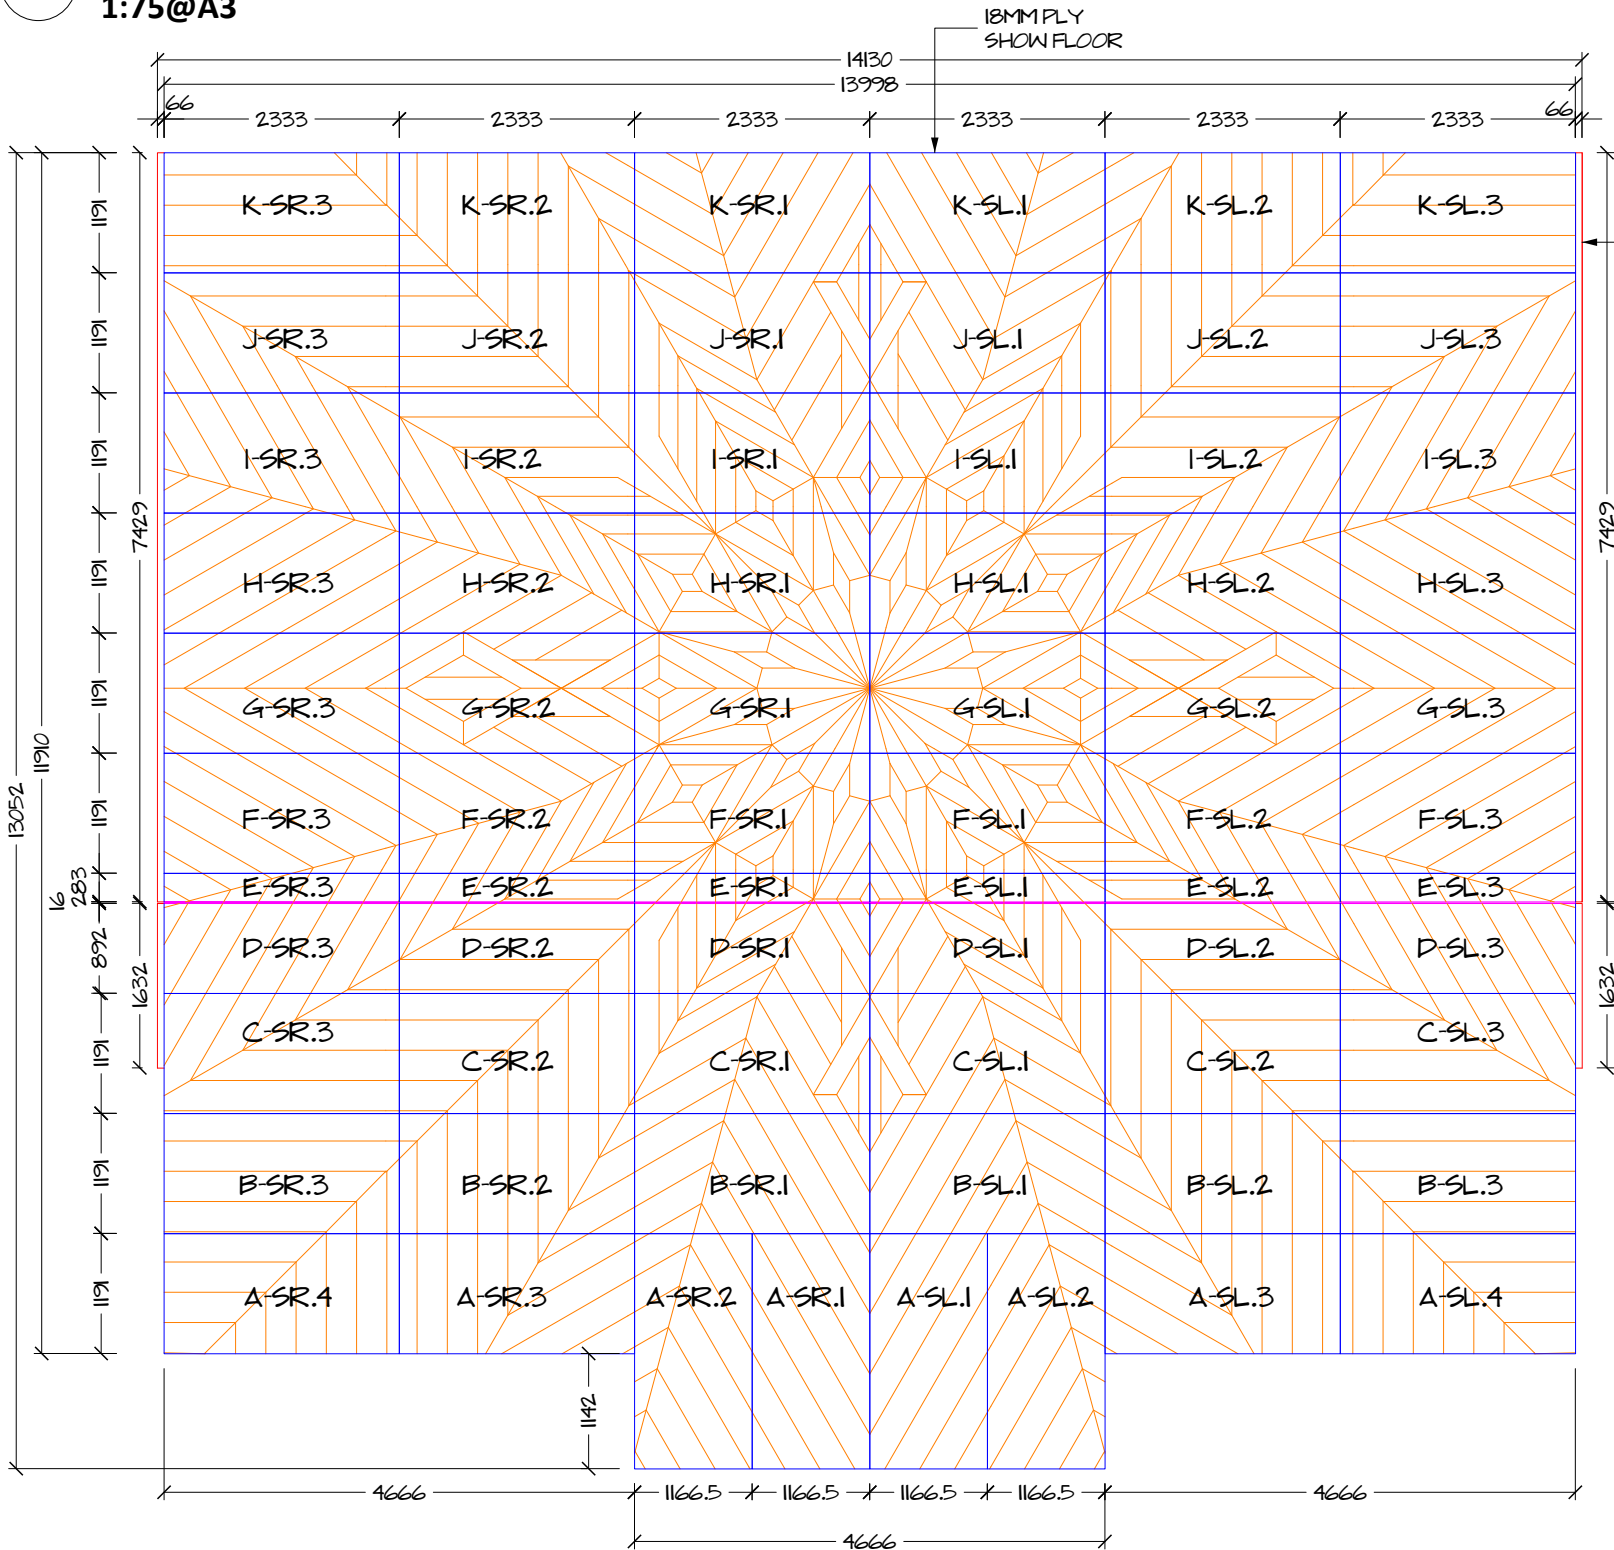

SCENIC FINISH REFERENCE

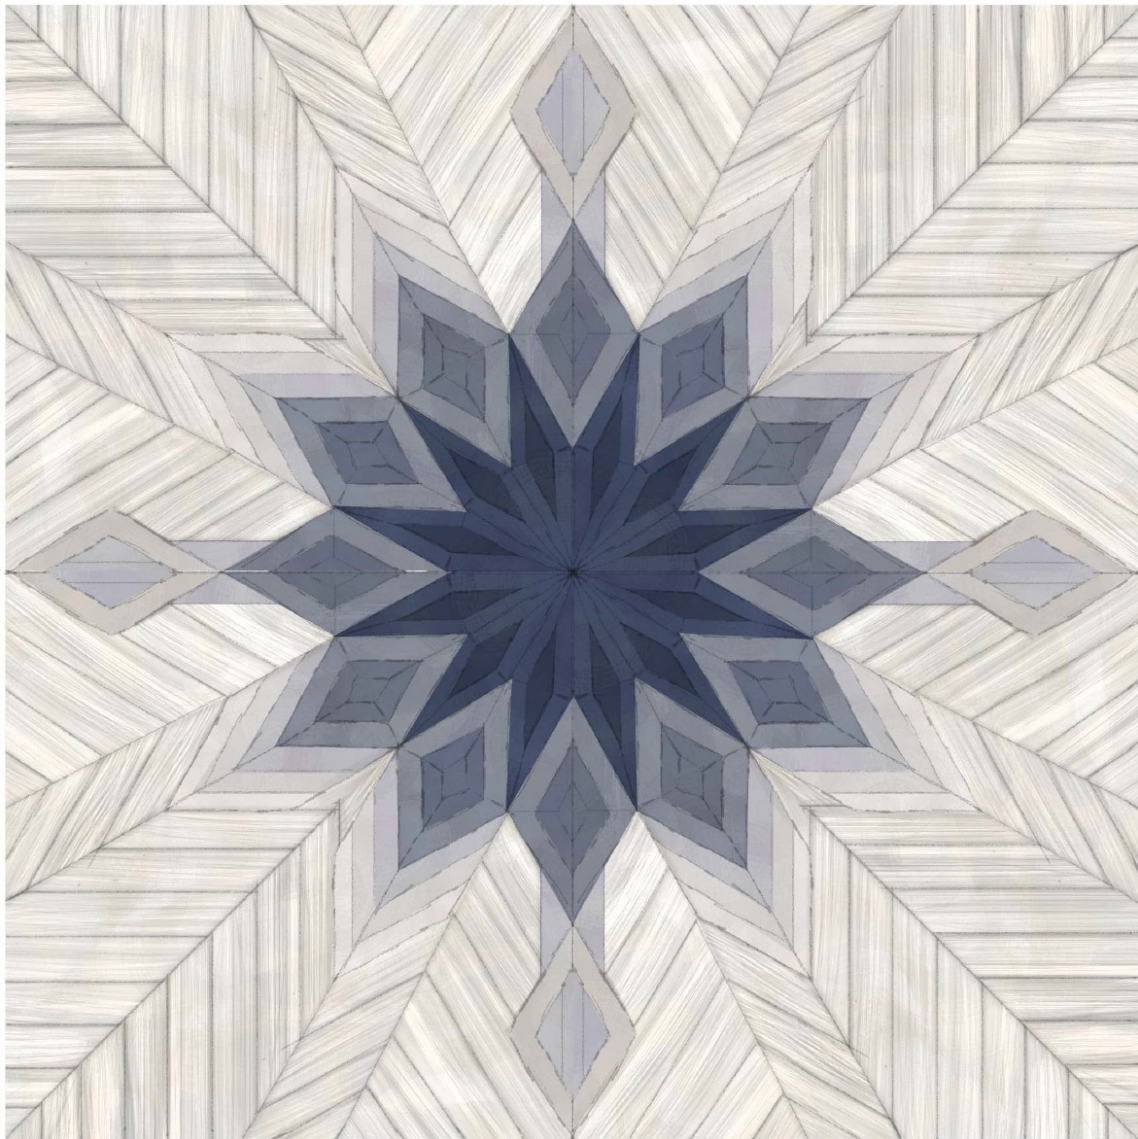


iceworks
design

ICEWORKS DESIGN PTY. LTD.
5747 Fairfield Rd, Yeerongpilly, QLD. 4105
PO Box 624, Fairfield Gardens, QLD. 4103
T: + 617 3352 4511
www.iceworksdesign.com



THESE DRAWINGS ARE CONCEPT & DESIGN ONLY.
FURTHER CONSTRUCTION & DETAIL DRAWINGS
MAY BE REQUIRED.

These drawings are © copyright 2025 ICEWORKS DESIGN.
Drawings, illustrations & 3D Renders are not to be used,
reproduced or copied without permission from ICEWORKS DESIGN.
All dimensions are to be checked on site prior to commencing any
construction, if in doubt please contact ICEWORKS DESIGN. Do
not scale from
drawings. Any building work is to comply with the building act,
BCA and standard regulations where applicable.

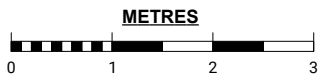

DESIGN APPROVAL

sign:.....

print name:.....

APPROVED / REVISE [circle]

comments:.....

date:..... /..... /.....

CLIENT: STODDART ENTERTAINMENT GROUP

PROJECT: FROZEN

DESIGNER: HARRY GILL

VENUE: CIVIC THEATRE

ADDRESS: 375 HUNTER ST
NEWCASTLE, NSW 2300

JOB No: 26150

DRAWING NAME: **ITEM A - SHOW FLOOR DETAILS**

DRAWN BY: GAVIN HAMPSTEAD

ISSUE: DATE DESCRIPTION

22/07/26	ISSUE FOR COSTING & CLIENT REVIEW
23/07/26	REVISED. ISSUE FOR CLIENT APPROVAL FOR CONSTRUCTION
24/07/26	FEATHER EDGE ADDED. ISSUE FOR CLIENT APPROVAL
00/00/00	XXXX
00/00/00	XXXX
00/00/00	XXXX

SCALE: AS SHOWN @ A3

DWG No: **D02**

SHEET No: **3 / 3**