

SHEET#	DWG#	DRAWING NAME
1	CP	COVER PAGE
2	D01	RENDERED VIEWS
3	D02	ASSEMBLED VIEWS
4	D03	ITEM C.1 - D/S PILLARS
5	D04	ITEM C.2 - D/S HEADER
6	D05	ITEM C.3 - D/S ARCH
7	D06	ITEM C.1-C.3 - CNC FILES



FROZEN

ITEM C.1-C.3 - DOWNSTAGE PILLARS & ARCH
CONSTRUCTION DESIGN
PLAN SET V1
29/07/26

 ICEWORKS DESIGN PTY. LTD. 5/747 Fairfield Rd, Yeerongpilly, QLD. 4105 PO Box 624, Fairfield Gardens, QLD. 4103 T: + 617 3352 4511 www.iceworksdesign.com		THESE DRAWINGS ARE CONCEPT & DESIGN ONLY. FURTHER CONSTRUCTION & DETAIL DRAWINGS MAY BE REQUIRED. These drawings are © copyright 2025 ICEWORKS DESIGN. Drawings, illustrations & 3D Renders are not to be used, reproduced or copied without permission from ICEWORKS DESIGN. All dimensions are to be checked on site prior to commencing any construction, if in doubt please contact ICEWORKS DESIGN. Do not scale from drawings. Any building work is to comply with the building act, BCA and standard regulations where applicable.	<u>DESIGN APPROVAL</u> sign:..... print name:..... APPROVED / REVISE [circle] comments..... date:..... /..... /.....	CLIENT:	STODDART ENTERTAINMENT GROUP	DRAWING NAME:	COVER PAGE	SCALE:	N/A @ A3
				PROJECT	FROZEN	DRAWN BY:	GAVIN HAMPSTEAD	DWG No:	CP
				DESIGNER:	HARRY GILL	ISSUE:	DATE	DESCRIPTION	SHEET No:
				VENUE:	CIVIC THEATRE		29/07/26	ISSUE FOR COSTING & CLIENT REVIEW	
				ADDRESS:	375 HUNTER ST NEWCASTLE, NSW 2300		00/00/00	XXXX	
				JOB No:	26150		00/00/00	XXXX	


C.1-C.3

3D FRONT VIEW
NA@A3



C.1-C.3

3D REAR VIEW
NA@A3

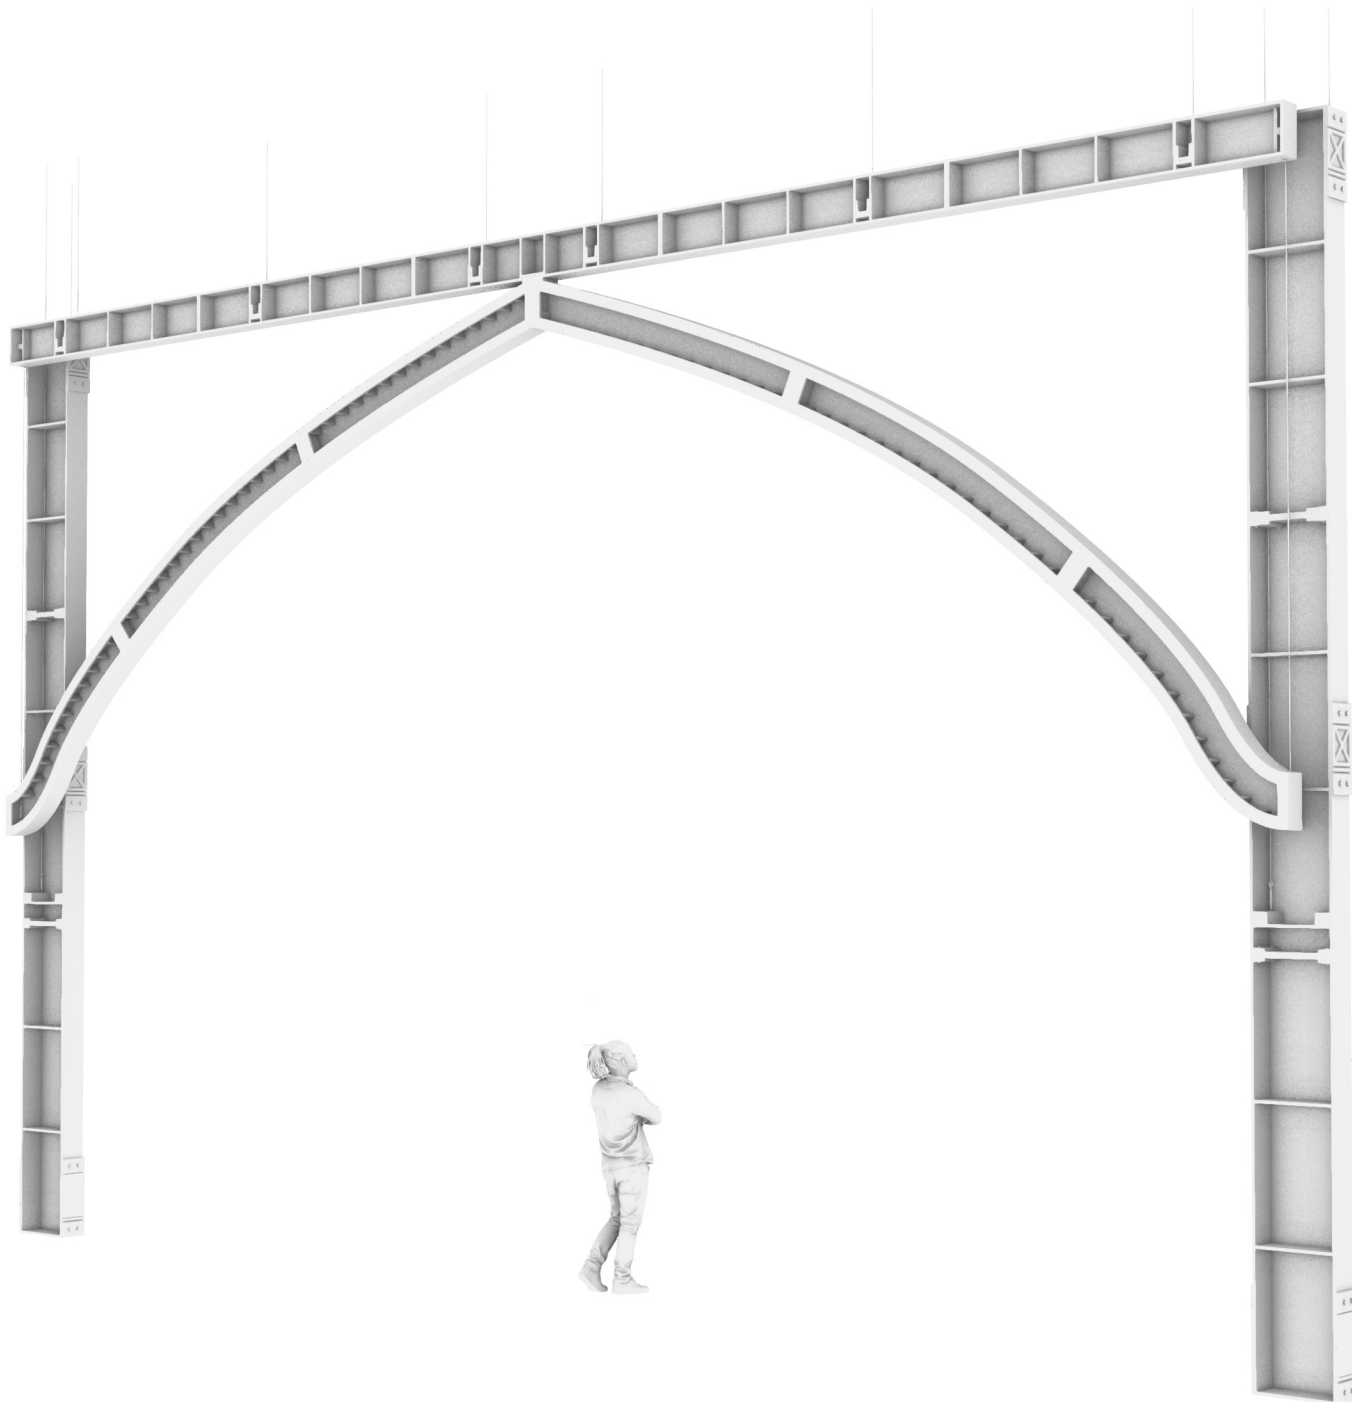

iceworks
design

ICEWORKS DESIGN PTY. LTD.
5/747 Fairfield Rd, Yeerongpilly, QLD. 4105
PO Box 624, Fairfield Gardens, QLD. 4103
T: + 617 3352 4511
www.iceworksdesign.com



THESE DRAWINGS ARE CONCEPT & DESIGN ONLY.
FURTHER CONSTRUCTION & DETAIL DRAWINGS
MAY BE REQUIRED.

These drawings are © copyright 2025 ICEWORKS DESIGN.
Drawings, illustrations & 3D Renders are not to be used,
reproduced or copied without permission from ICEWORKS DESIGN.
All dimensions are to be checked on site prior to commencing any
construction, if in doubt please contact ICEWORKS DESIGN. Do
not scale from
drawings. Any building work is to comply with the building act,
BCA and standard regulations where applicable.

DESIGN APPROVAL

sign:.....

print name:.....

APPROVED / REVISE [circle]

comments.....

date:..... /..... /.....

CLIENT: STODDART ENTERTAINMENT GROUP

PROJECT: FROZEN

DESIGNER: HARRY GILL

VENUE: CIVIC THEATRE

ADDRESS: 375 HUNTER ST
NEWCASTLE, NSW 2300

JOB No: 26150

DRAWING
NAME:

RENDERED VIEWS

DRAWN BY: GAVIN HAMPSTEAD

ISSUE:

DATE DESCRIPTION

29/07/26	ISSUE FOR COSTING & CLIENT REVIEW
00/00/00	XXXX
00/00/00	XXXX
00/00/00	XXXX
00/00/00	XXXX
00/00/00	XXXX

SCALE:

NA@ A3

DWG
No:


D01

SHEET
No:


2 / 7

FROZEN


C.1-C.3
PLAN VIEW
1:50@A3

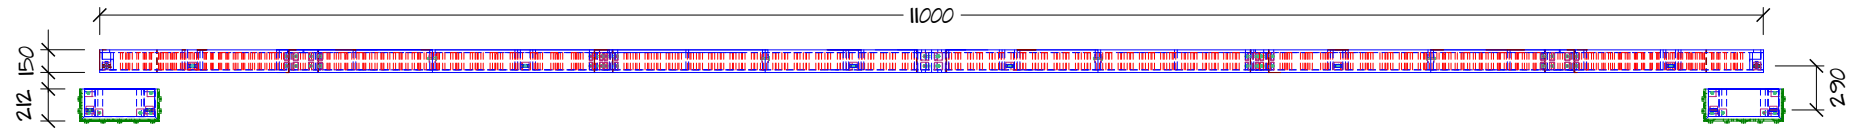

C.1-C.3
FRONT VIEW
1:50@A3

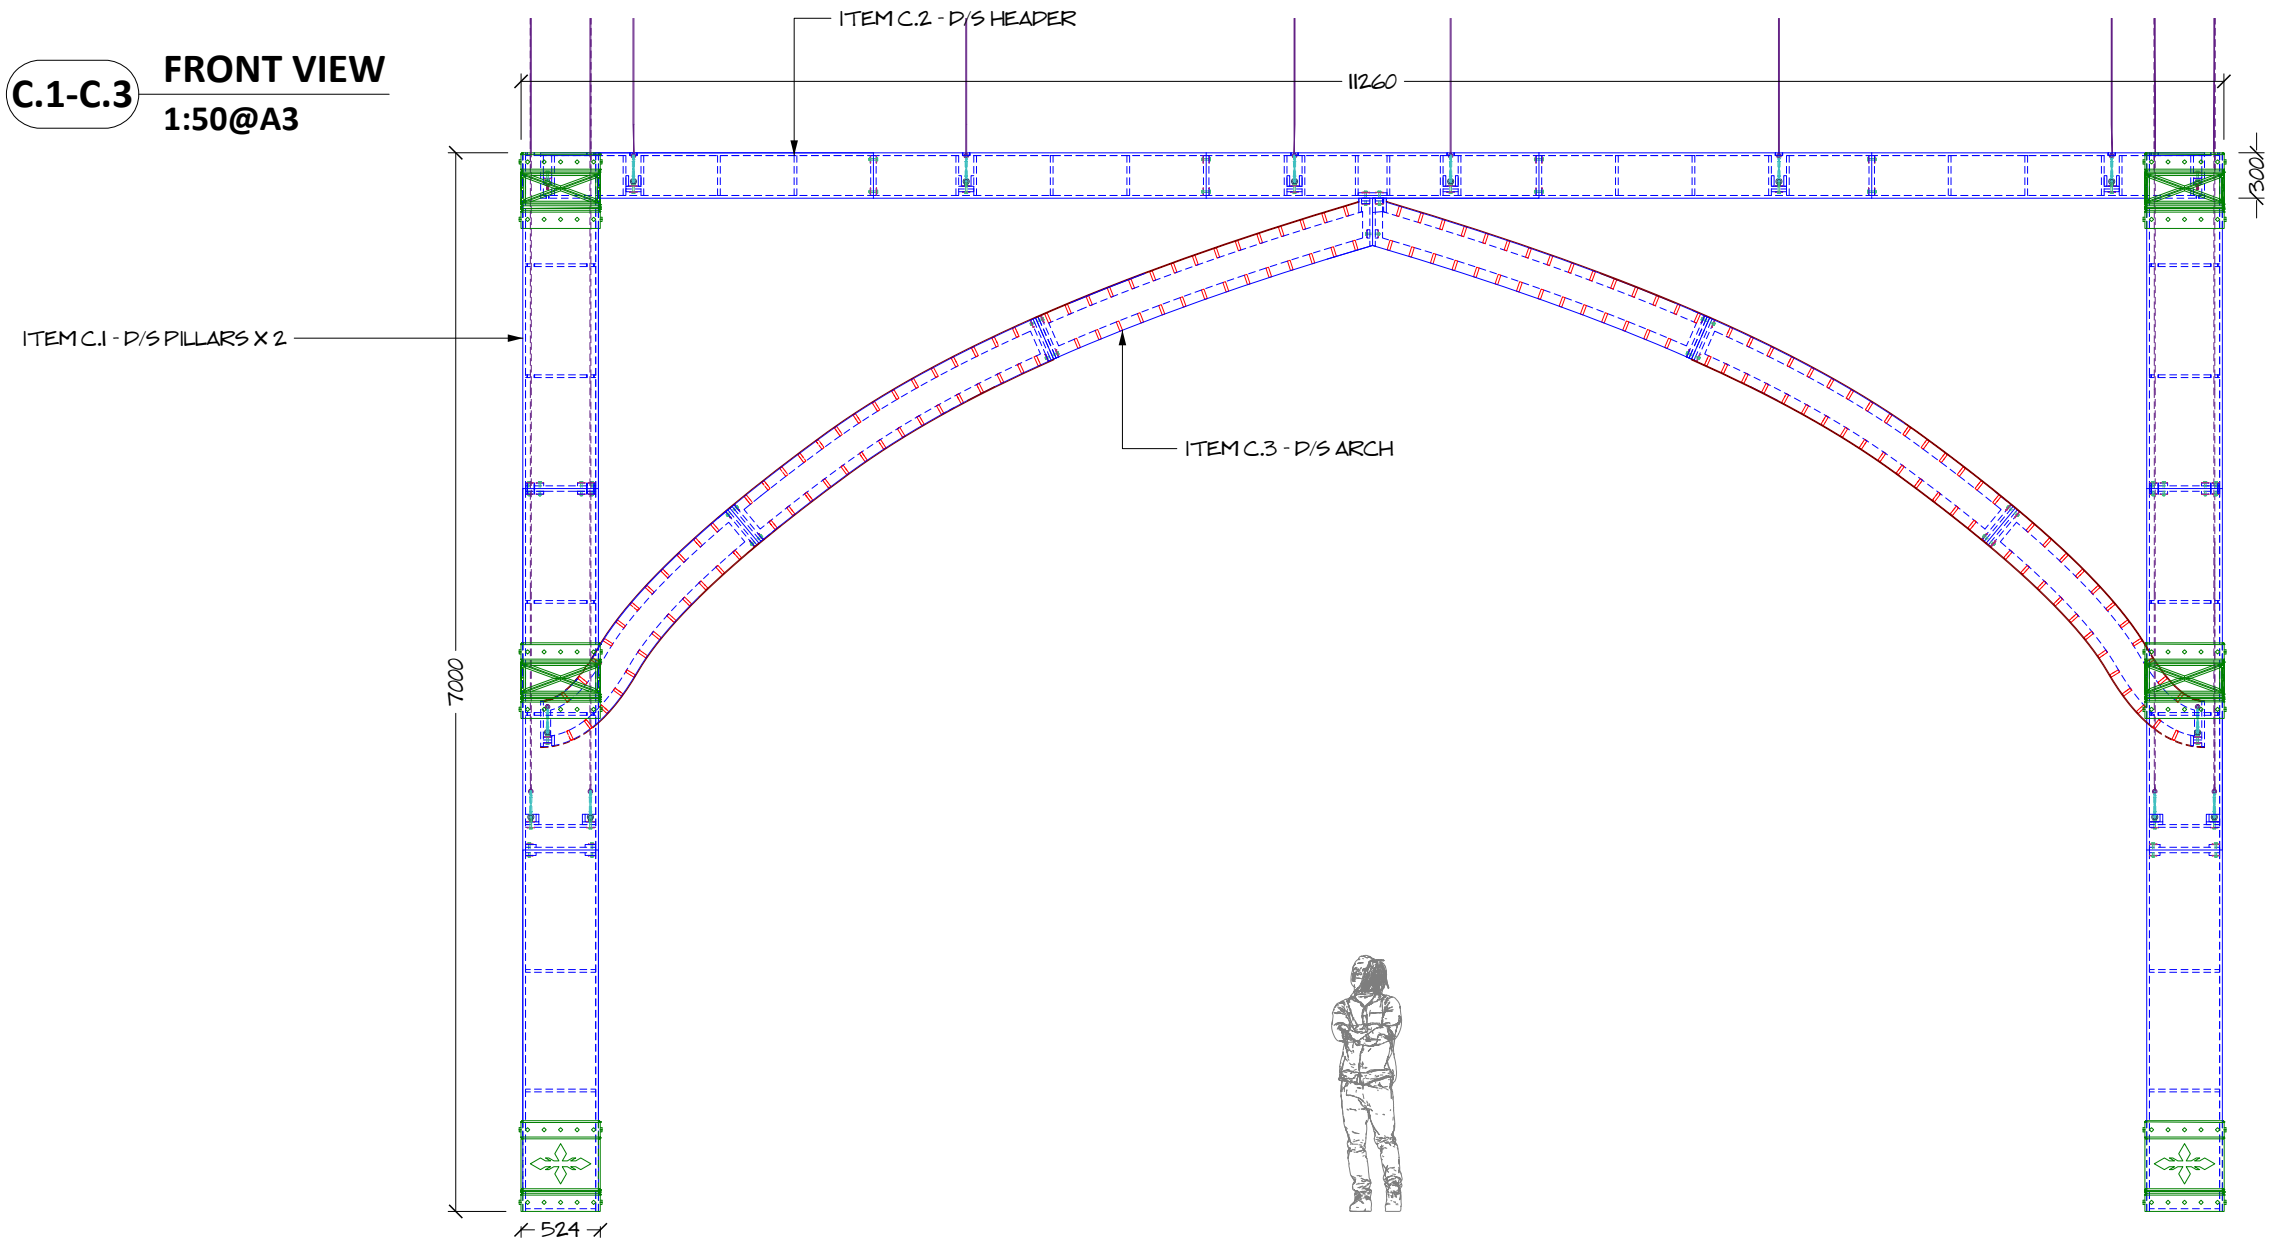

C.1-C.3
END VIEW
1:50@A3

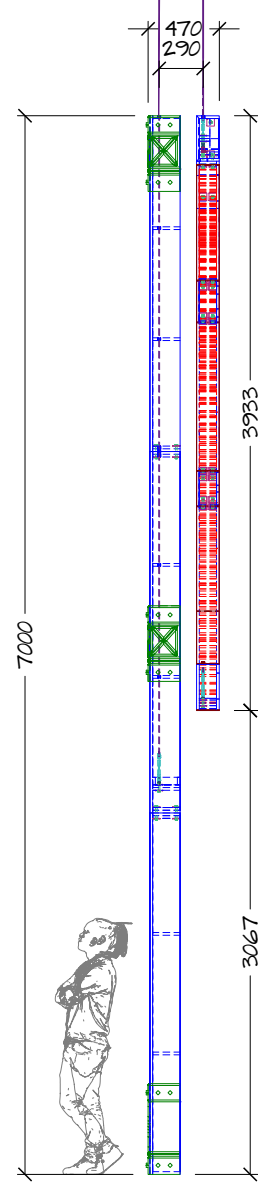


ICEWORKS DESIGN PTY. LTD.
5/747 Fairfield Rd, Yeerongpilly, QLD. 4105
PO Box 624, Fairfield Gardens, QLD. 4103
T: + 617 3352 4511
www.iceworksdesign.com



THESE DRAWINGS ARE CONCEPT & DESIGN ONLY.
FURTHER CONSTRUCTION & DETAIL DRAWINGS
MAY BE REQUIRED.

These drawings are © copyright 2025 ICEWORKS DESIGN.
Drawings, illustrations & 3D Renders are not to be used,
reproduced or copied without permission from ICEWORKS DESIGN.
All dimensions are to be checked on site prior to commencing any
construction, if in doubt please contact ICEWORKS DESIGN. Do
not scale from
drawings. Any building work is to comply with the building act,
BCA and standard regulations where applicable.

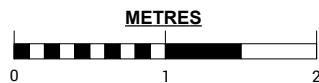

DESIGN APPROVAL

sign:.....
print name:.....
APPROVED / REVISE [circle]
comments.....
date:..... /..... /.....


CLIENT:	STODDART ENTERTAINMENT GROUP
PROJECT	FROZEN
DESIGNER:	HARRY GILL
VENUE:	CIVIC THEATRE
ADDRESS:	375 HUNTER ST NEWCASTLE, NSW 2300
JOB No:	26150

DRAWING NAME:	ASSEMBLED VIEWS	
DRAWN BY:	GAVIN HAMPSTEAD	
ISSUE:	DATE	DESCRIPTION
	29/07/26	ISSUE FOR COSTING & CLIENT REVIEW
	00/00/00	XXXX
	00/00/00	XXXX
	00/00/00	XXXX
	00/00/00	XXXX
	00/00/00	XXXX

SCALE:	1:100 @ A3
DWG No:	D02
SHEET No:	3 / 7

QTY X 2


C.1 PLAN VIEW
1:5@A3

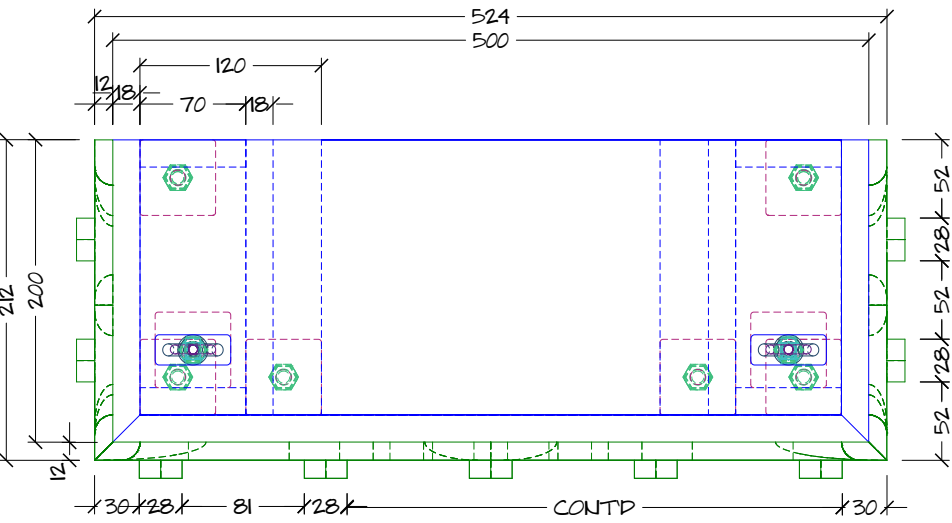


C.1 3D VIEW
NA@A3

RIGGING EYENLIT
WITH TURNBUCKLE
& STEEL WIRE DROPPER


M10 BOLT FIXINGS JOINS

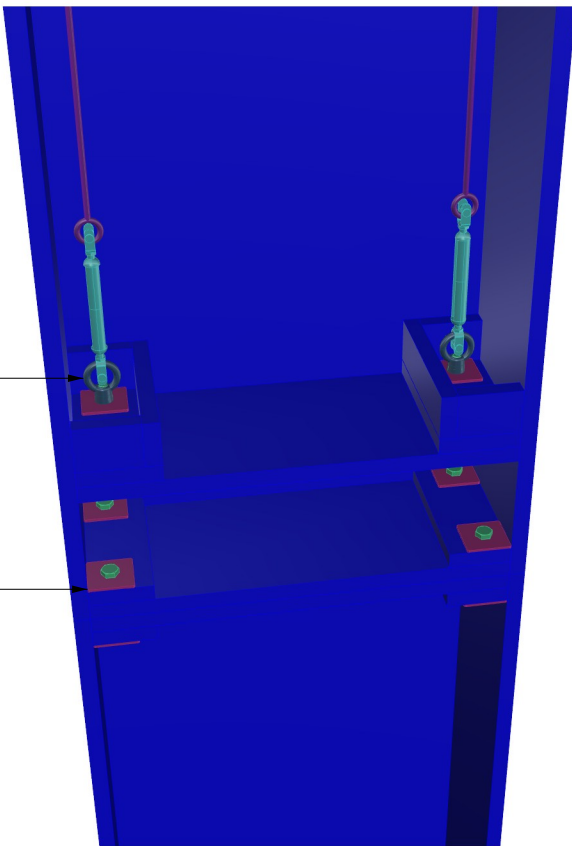


C.1 PLAN VIEW
1:50A3

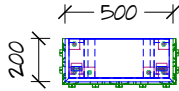

C.1 FRONT VIEW
1:50A3

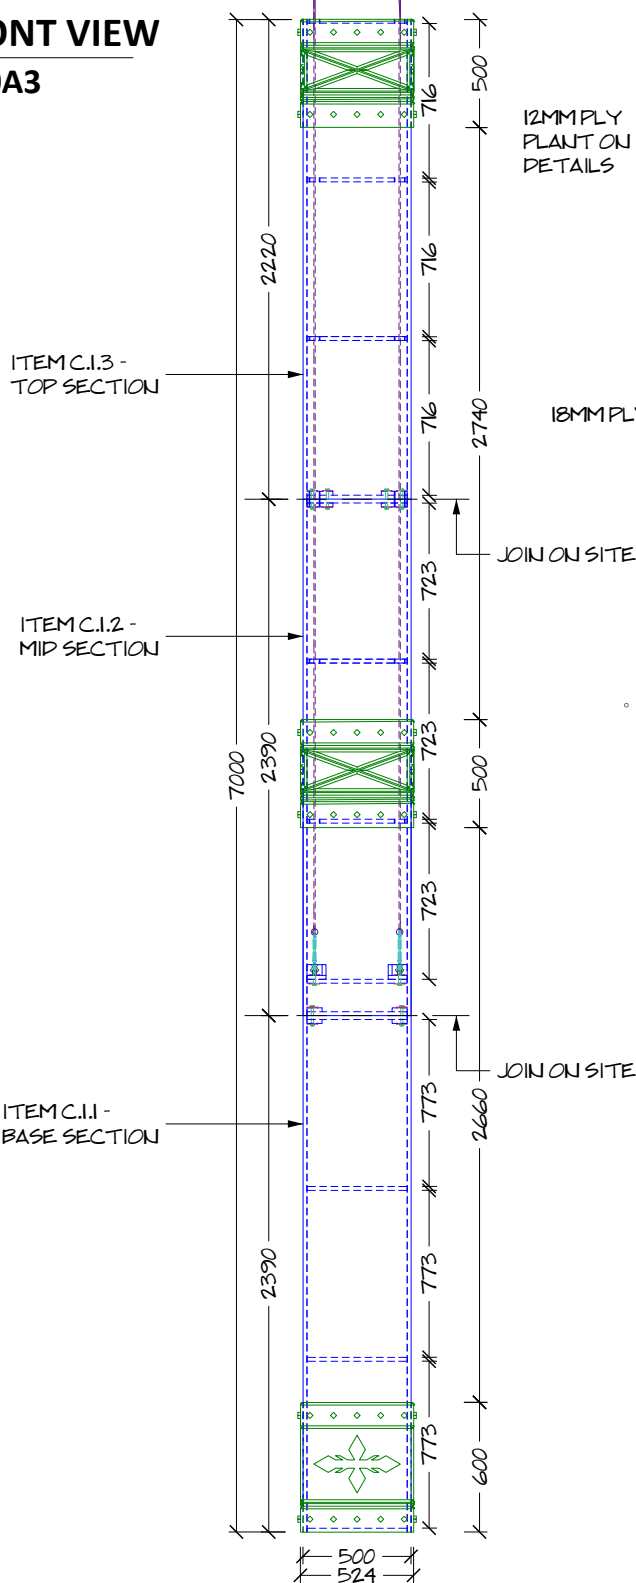

C.1 3D VIEWS
NA@A3

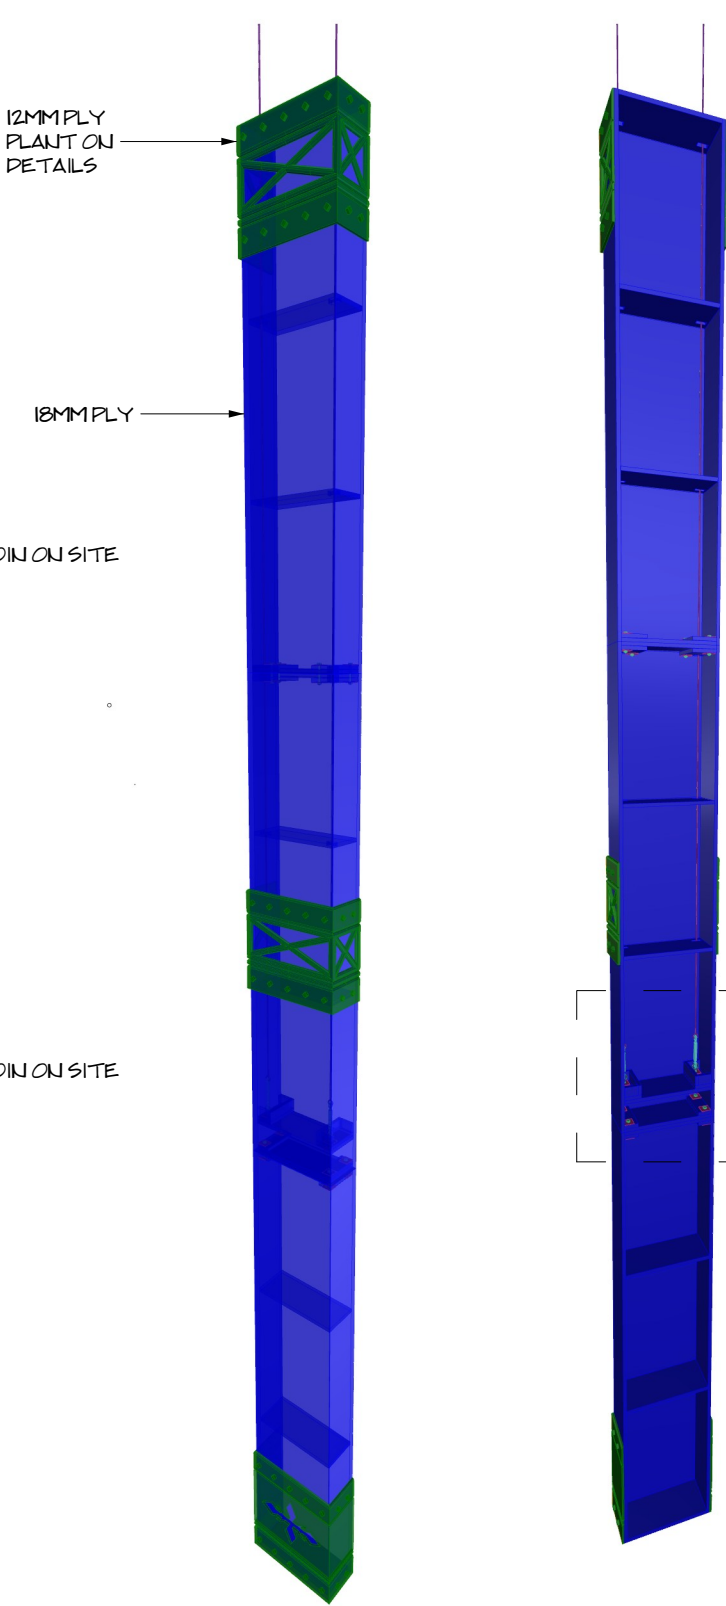

CONSTRUCTION DETAILS
MAKE 2 X ITEMS AS SHOWN.


CONSTRUCTED FROM 18MM SELEX PLY
CNC CUT TO SHAPE.
PLANT ON DETAILS CONSTRUCTED FROM
12MM SELEX PLY CNC CUT TO SHAPE. PVA
GLUE, BRAD NAIL & SCREW FIXING
ASSEMBLY.

BOLT FIX PILLAR SECTIONS TOGETHER
WITH 4 X 90MM M10 BOLTS PER JOIN.

RIGGING DETAILS - 2 X RATED M10
EYENLITS WITH M10 BOLTS TO SUIT. 2 X
JAW-JAW TURNBUCKLES WITH 2 X 5M LONG
6MM BLACK STEEL WIRE DROPPERS WITH
RATED SHACKLE. DROPPER LENGTH TBC
BY PRODUCTION MANAGER. YUPPIE
STRAPS TOP RIGGING SUPPLIED BY
PRODUCTION MANAGER.

FILL SCREW HOLES ONLY. LIGHT SAND ON
CNC PLANT ON DETAILS TO REMOVE
FURRING. UNDERCOAT AND SCENIC TOP
COAT PAINT FINISH TO MATCH SCENIC
REFERENCES SUPPLIED BY SET DESIGNER.

C.1 REAR VIEW
1:10A3

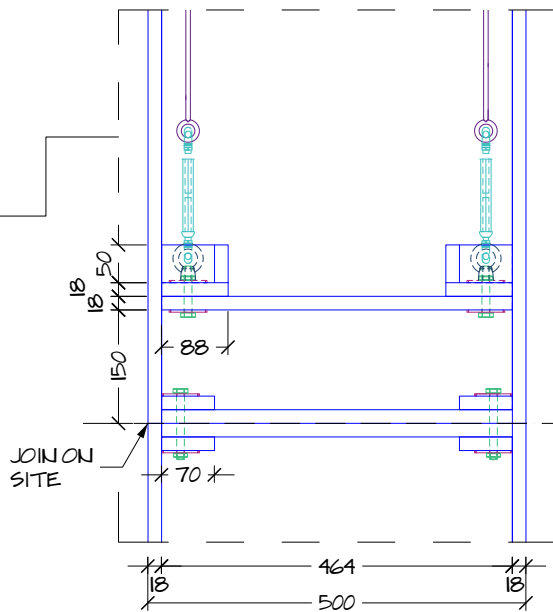

iceworks
design

ICEWORKS DESIGN PTY. LTD.
5/747 Fairfield Rd, Yeerongpilly, QLD. 4105
PO Box 624, Fairfield Gardens, QLD. 4103
T: + 617 3352 4511
www.iceworksdesign.com



THESE DRAWINGS ARE CONCEPT & DESIGN ONLY.
FURTHER CONSTRUCTION & DETAIL DRAWINGS
MAY BE REQUIRED.

These drawings are © copyright 2025 ICEWORKS DESIGN.
Drawings, illustrations & 3D Renders are not to be used,
reproduced or copied without permission from ICEWORKS DESIGN.
All dimensions are to be checked on site prior to commencing any
construction, if in doubt please contact ICEWORKS DESIGN. Do
not scale from
drawings. Any building work is to comply with the building act,
BCA and standard regulations where applicable.

DESIGN APPROVAL

sign:.....

print name:.....

APPROVED / REVISE [circle]

comments.....

date:..... /..... /.....

CLIENT:	STODDART ENTERTAINMENT GROUP
PROJECT	FROZEN
DESIGNER:	HARRY GILL
VENUE:	CIVIC THEATRE
ADDRESS:	375 HUNTER ST NEWCASTLE, NSW 2300
JOB No:	26150


DRAWING NAME:	ITEM C.1 - D/S PILLARS
DRAWN BY:	GAVIN HAMPSTEAD
ISSUE:	DATE DESCRIPTION
	29/07/26 ISSUE FOR COSTING & CLIENT REVIEW
	00/00/00 XXXX
	00/00/00 XXXX
	00/00/00 XXXX
	00/00/00 XXXX
	00/00/00 XXXX

SCALE: AS SHOWN @ A3

DWG No: D03

SHEET No: 4 / 7

C.2 3D VIEWS
NA@A3

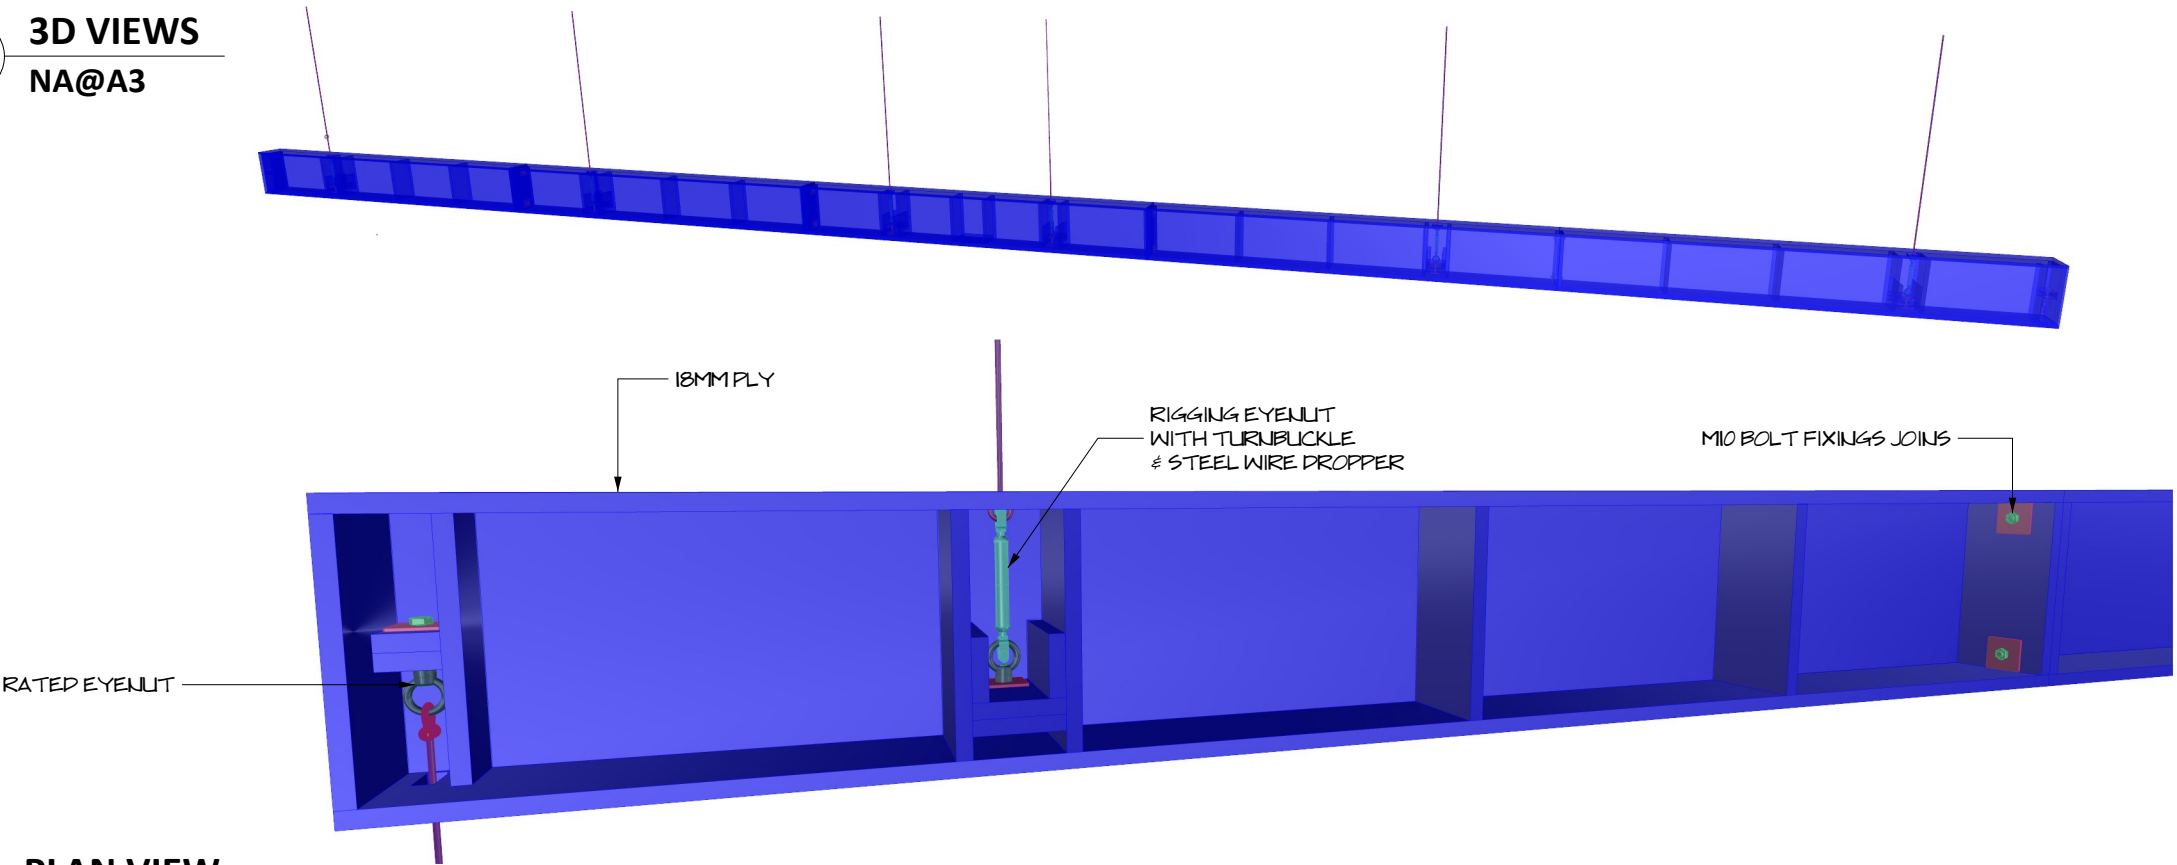

CONSTRUCTION DETAILS
MAKE 1 X ITEM AS SHOWN.


CONSTRUCTED FROM 18MM SELEX PLY
CNC CUT TO SHAPE,
PVA GLUE, BRAD NAIL & SCREW FIXING
ASSEMBLY.

BOLT FIX HEADER SECTIONS TOGETHER
WITH 2 X 50MM M10 BOLTS PER JOIN.


RIGGING DETAILS - 6 X RATED M10
EYENUTS WITH M10 BOLTS TO SUIT. 6 X
JAW-JAW TURNBUCKLES WITH 6 X 1M LONG
6MM BLACK STEEL WIRE DROPPERS WITH
RATED SHACKLE. DROPPER LENGTH TBC
BY PRODUCTION MANAGER. YUPPIE
STRAPS TOP RIGGING SUPPLIED BY
PRODUCTION MANAGER. 2 X RATED
EYENUTS TO PICK UP SUB HUNG ITEM C.3
ARCH AS SHOWN.

FILL SCREW HOLES ONLY. UNDERCOAT
AND SCENIC TOP COAT PAINT FINISH TO
MATCH SCENIC REFERENCES SUPPLIED BY
SET DESIGNER.

C.2 PLAN VIEW
1:30@A3

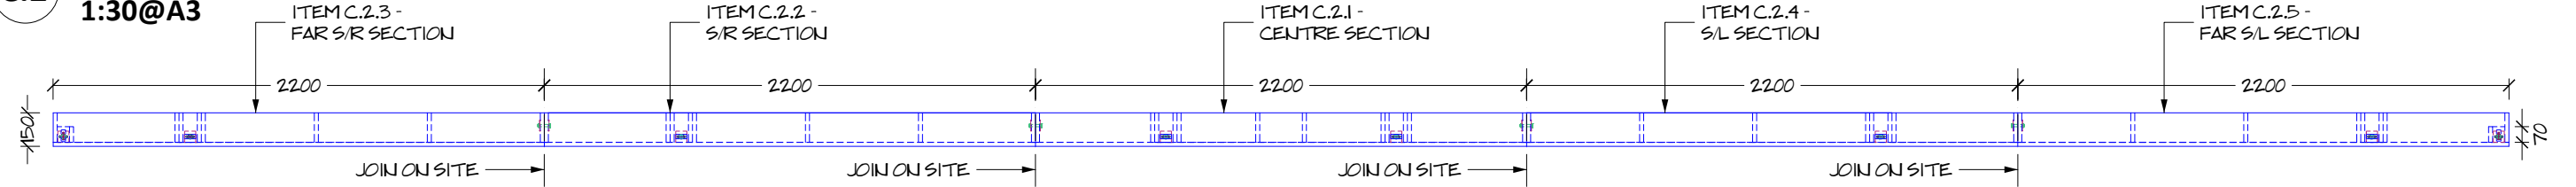

C.2 FRONT VIEW
1:30@A3

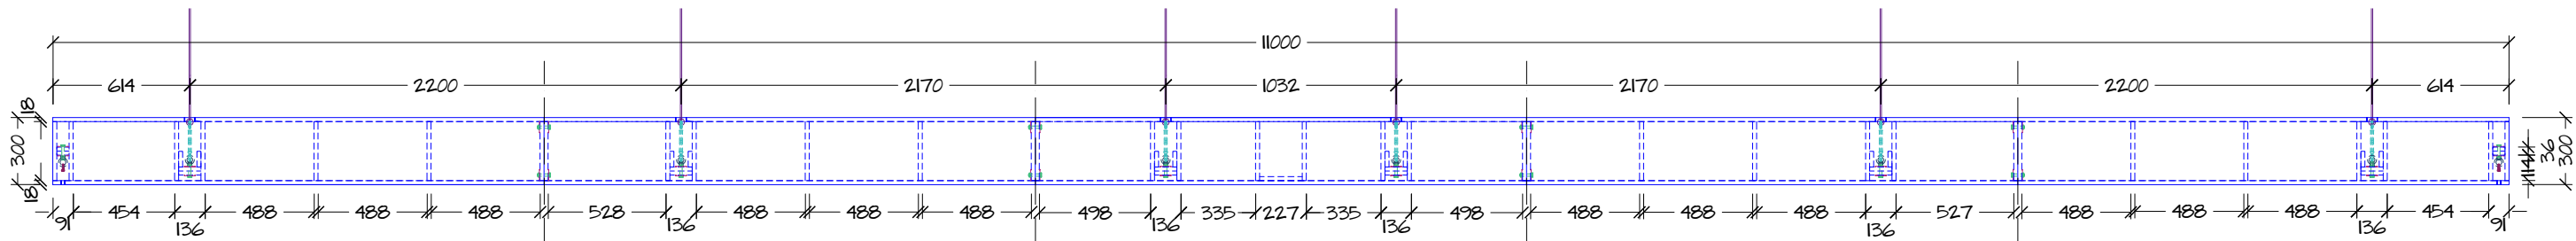

iceworks
design

ICEWORKS DESIGN PTY. LTD.
5/747 Fairfield Rd, Yeerongpilly, QLD. 4105
PO Box 624, Fairfield Gardens, QLD. 4103
T: + 617 3352 4511
www.iceworksdesign.com



THESE DRAWINGS ARE CONCEPT & DESIGN ONLY.
FURTHER CONSTRUCTION & DETAIL DRAWINGS
MAY BE REQUIRED.

These drawings are © copyright 2025 ICEWORKS DESIGN.
Drawings, illustrations & 3D Renders are not to be used,
reproduced or copied without permission from ICEWORKS DESIGN.
All dimensions are to be checked on site prior to commencing any
construction, if in doubt please contact ICEWORKS DESIGN. Do
not scale from
drawings. Any building work is to comply with the building act,
BCA and standard regulations where applicable.



DESIGN APPROVAL

sign:.....

print name:.....

APPROVED / REVISE [circle]

comments:.....

date:..... /..... /.....

CLIENT: STODDART ENTERTAINMENT GROUP

PROJECT: FROZEN

DESIGNER: HARRY GILL

VENUE: CIVIC THEATRE

ADDRESS: 375 HUNTER ST
NEWCASTLE, NSW 2300

JOB No: 26150

DRAWING
NAME:

ITEM C.2 - D/S HEADER

DRAWN BY:

GAVIN HAMPSTEAD

ISSUE:

DATE DESCRIPTION

29/07/26

00/00/00

00/00/00

00/00/00

00/00/00

00/00/00

ISSUE FOR COSTING & CLIENT REVIEW

XXXX

XXXX

XXXX

XXXX

XXXX

SCALE:

1:30 @ A3

DWG
No:

D04

SHEET
No:

5 / 7

FROZEN

C.3 3D VIEW
NA@A3

RIGGING EYEJOLT
WITH TURNBUCKLE
STEEL WIRE DROPPER

C.3 PLAN VIEW
1:35@A3

C.3 3D VIEW
NA@A3

18MM PLY
66X18 PINE

M10 BOLTS

5MM BENDY PLY

5MM BENDY PLY

CONSTRUCTION DETAILS

MAKE 1 X ITEM AS SHOWN.


CONSTRUCTED FROM 18MM SELEX PLY CNC CUT TO
SHAPE, 66X18 PINE FRAMING # 5MM BENDY PLY RETURN
SKINS.
PVA GLUE, BRAD NAIL # SCREW FIXING ASSEMBLY.

BOLT FIX ARCH SECTIONS TOGETHER WITH 4 X 50MM M10
BOLTS PER JOIN.

RIGGING DETAILS - 2 X RATED M10 EYEJOLTS WITH M10
BOLTS TO SUIT. 2 X JAW-JAW TURNBUCKLES WITH 2 X
3.2M LONG 6MM BLACK STEEL WIRE DROPPERS WITH
RATED SHACKLE. DROPPER LENGTH TBC BY DESIGNER
WITH TURNBUCKLE SPECIFIED BY RIGGER IS CONFIRMED.
YUPPIE STRAPS TOP RIGGING SUPPLIED BY
PRODUCTION MANAGER.

FILL SCREW HOLES ONLY. UNDERCOAT AND SCENIC TOP
COAT PAINT FINISH TO MATCH SCENIC REFERENCES
SUPPLIED BY SET DESIGNER.

C.3 FRONT VIEW
1:35@A3

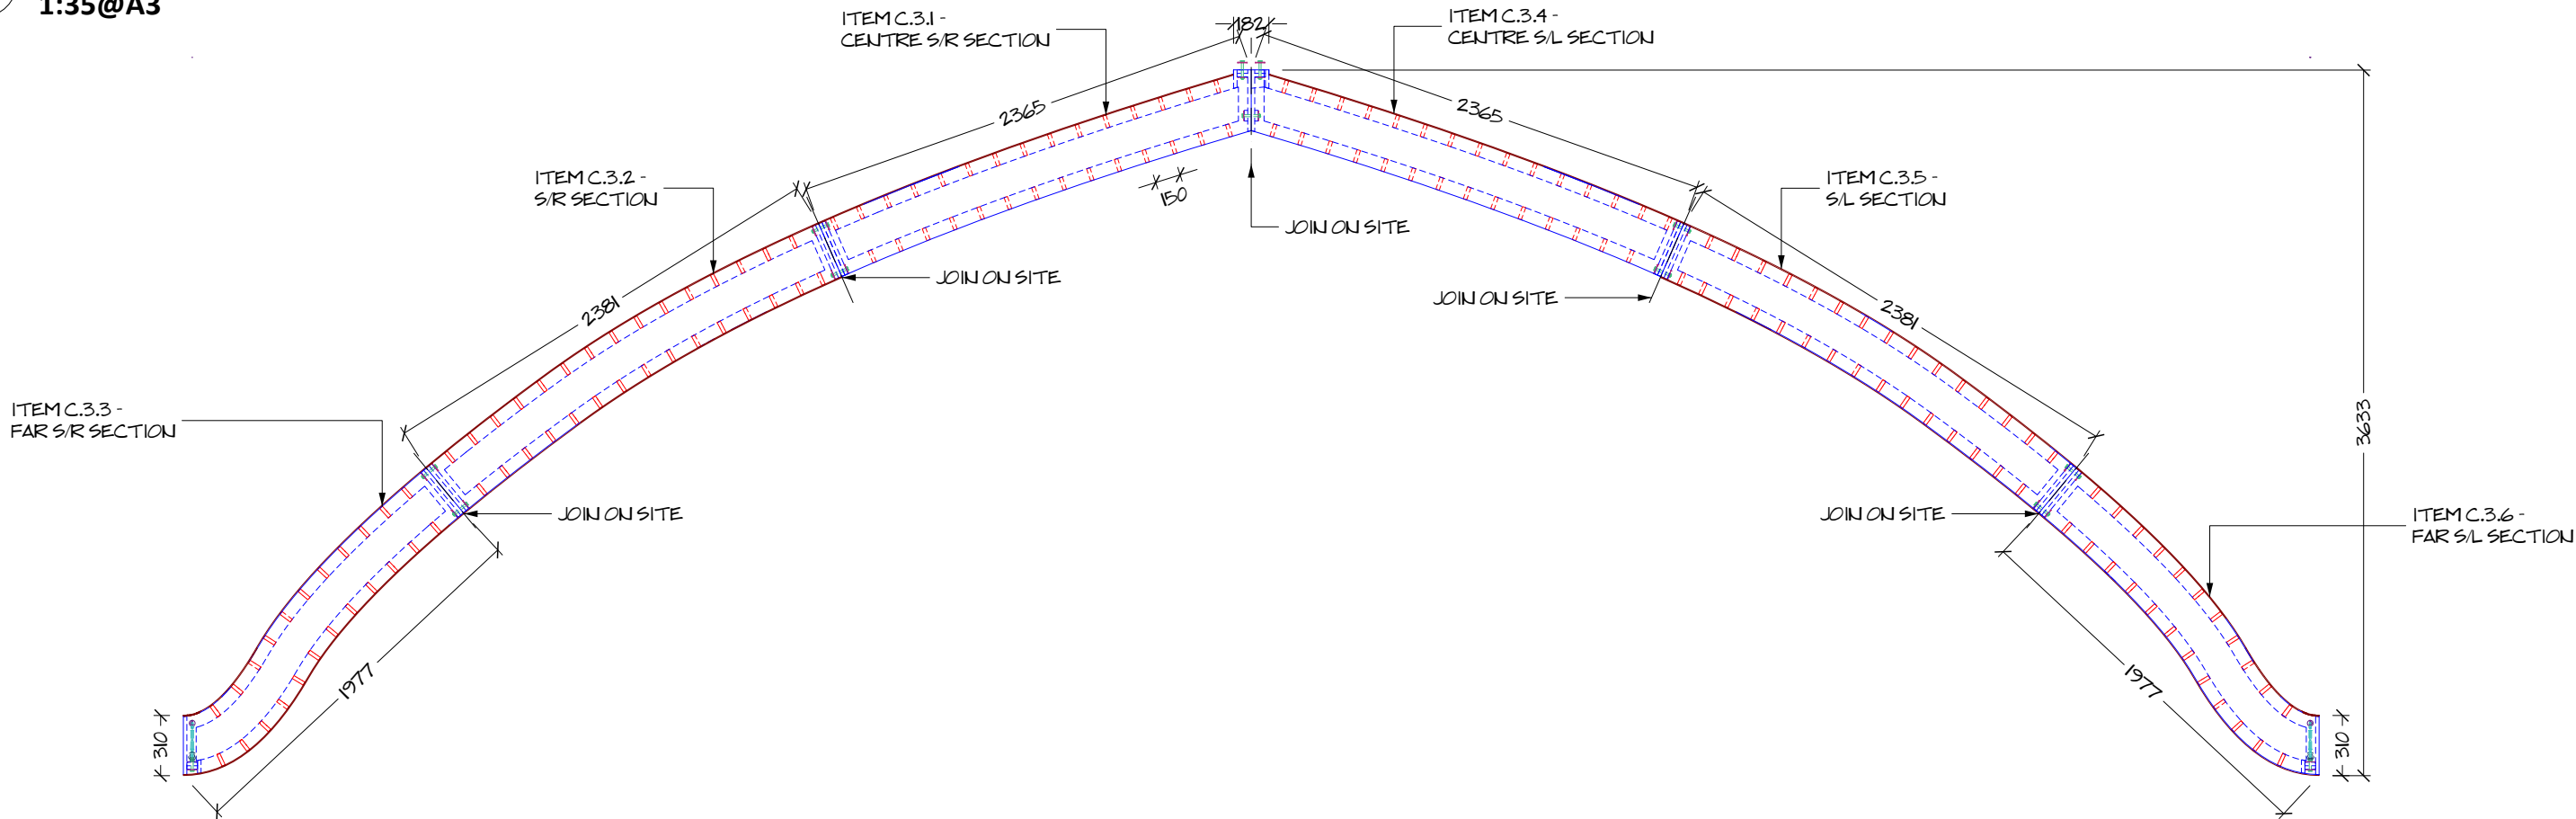


iceworks
design

ICEWORKS DESIGN PTY. LTD.
5/747 Fairfield Rd, Yeerongpilly, QLD. 4105
PO Box 624, Fairfield Gardens, QLD. 4103
T: + 617 3352 4511
www.iceworksdesign.com



THESE DRAWINGS ARE CONCEPT & DESIGN ONLY.
FURTHER CONSTRUCTION & DETAIL DRAWINGS
MAY BE REQUIRED.

These drawings are © copyright 2025 ICEWORKS DESIGN.
Drawings, illustrations & 3D Renders are not to be used,
reproduced or copied without permission from ICEWORKS DESIGN.
All dimensions are to be checked on site prior to commencing any
construction, if in doubt please contact ICEWORKS DESIGN. Do
not scale from
drawings. Any building work is to comply with the building act,
BCA and standard regulations where applicable.

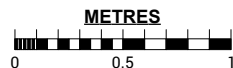

DESIGN APPROVAL

sign:.....

print name:.....

APPROVED / REVISE [circle]

comments.....

date:..... /..... /.....

CLIENT: STODDART ENTERTAINMENT GROUP

PROJECT: FROZEN

DESIGNER: HARRY GILL

VENUE: CIVIC THEATRE

ADDRESS: 375 HUNTER ST
NEWCASTLE, NSW 2300

JOB No: 26150

DRAWING
NAME:

ITEM C.3 - D/S ARCH

DRAWN BY:

GAVIN HAMPSTEAD

ISSUE:

DATE DESCRIPTION

29/07/26 ISSUE FOR COSTING & CLIENT REVIEW

00/00/00 XXXX

00/00/00 XXXX

00/00/00 XXXX

00/00/00 XXXX

SCALE: 1:35 @ A3

DWG
No:

D05

SHEET
No:

6 / 7

