

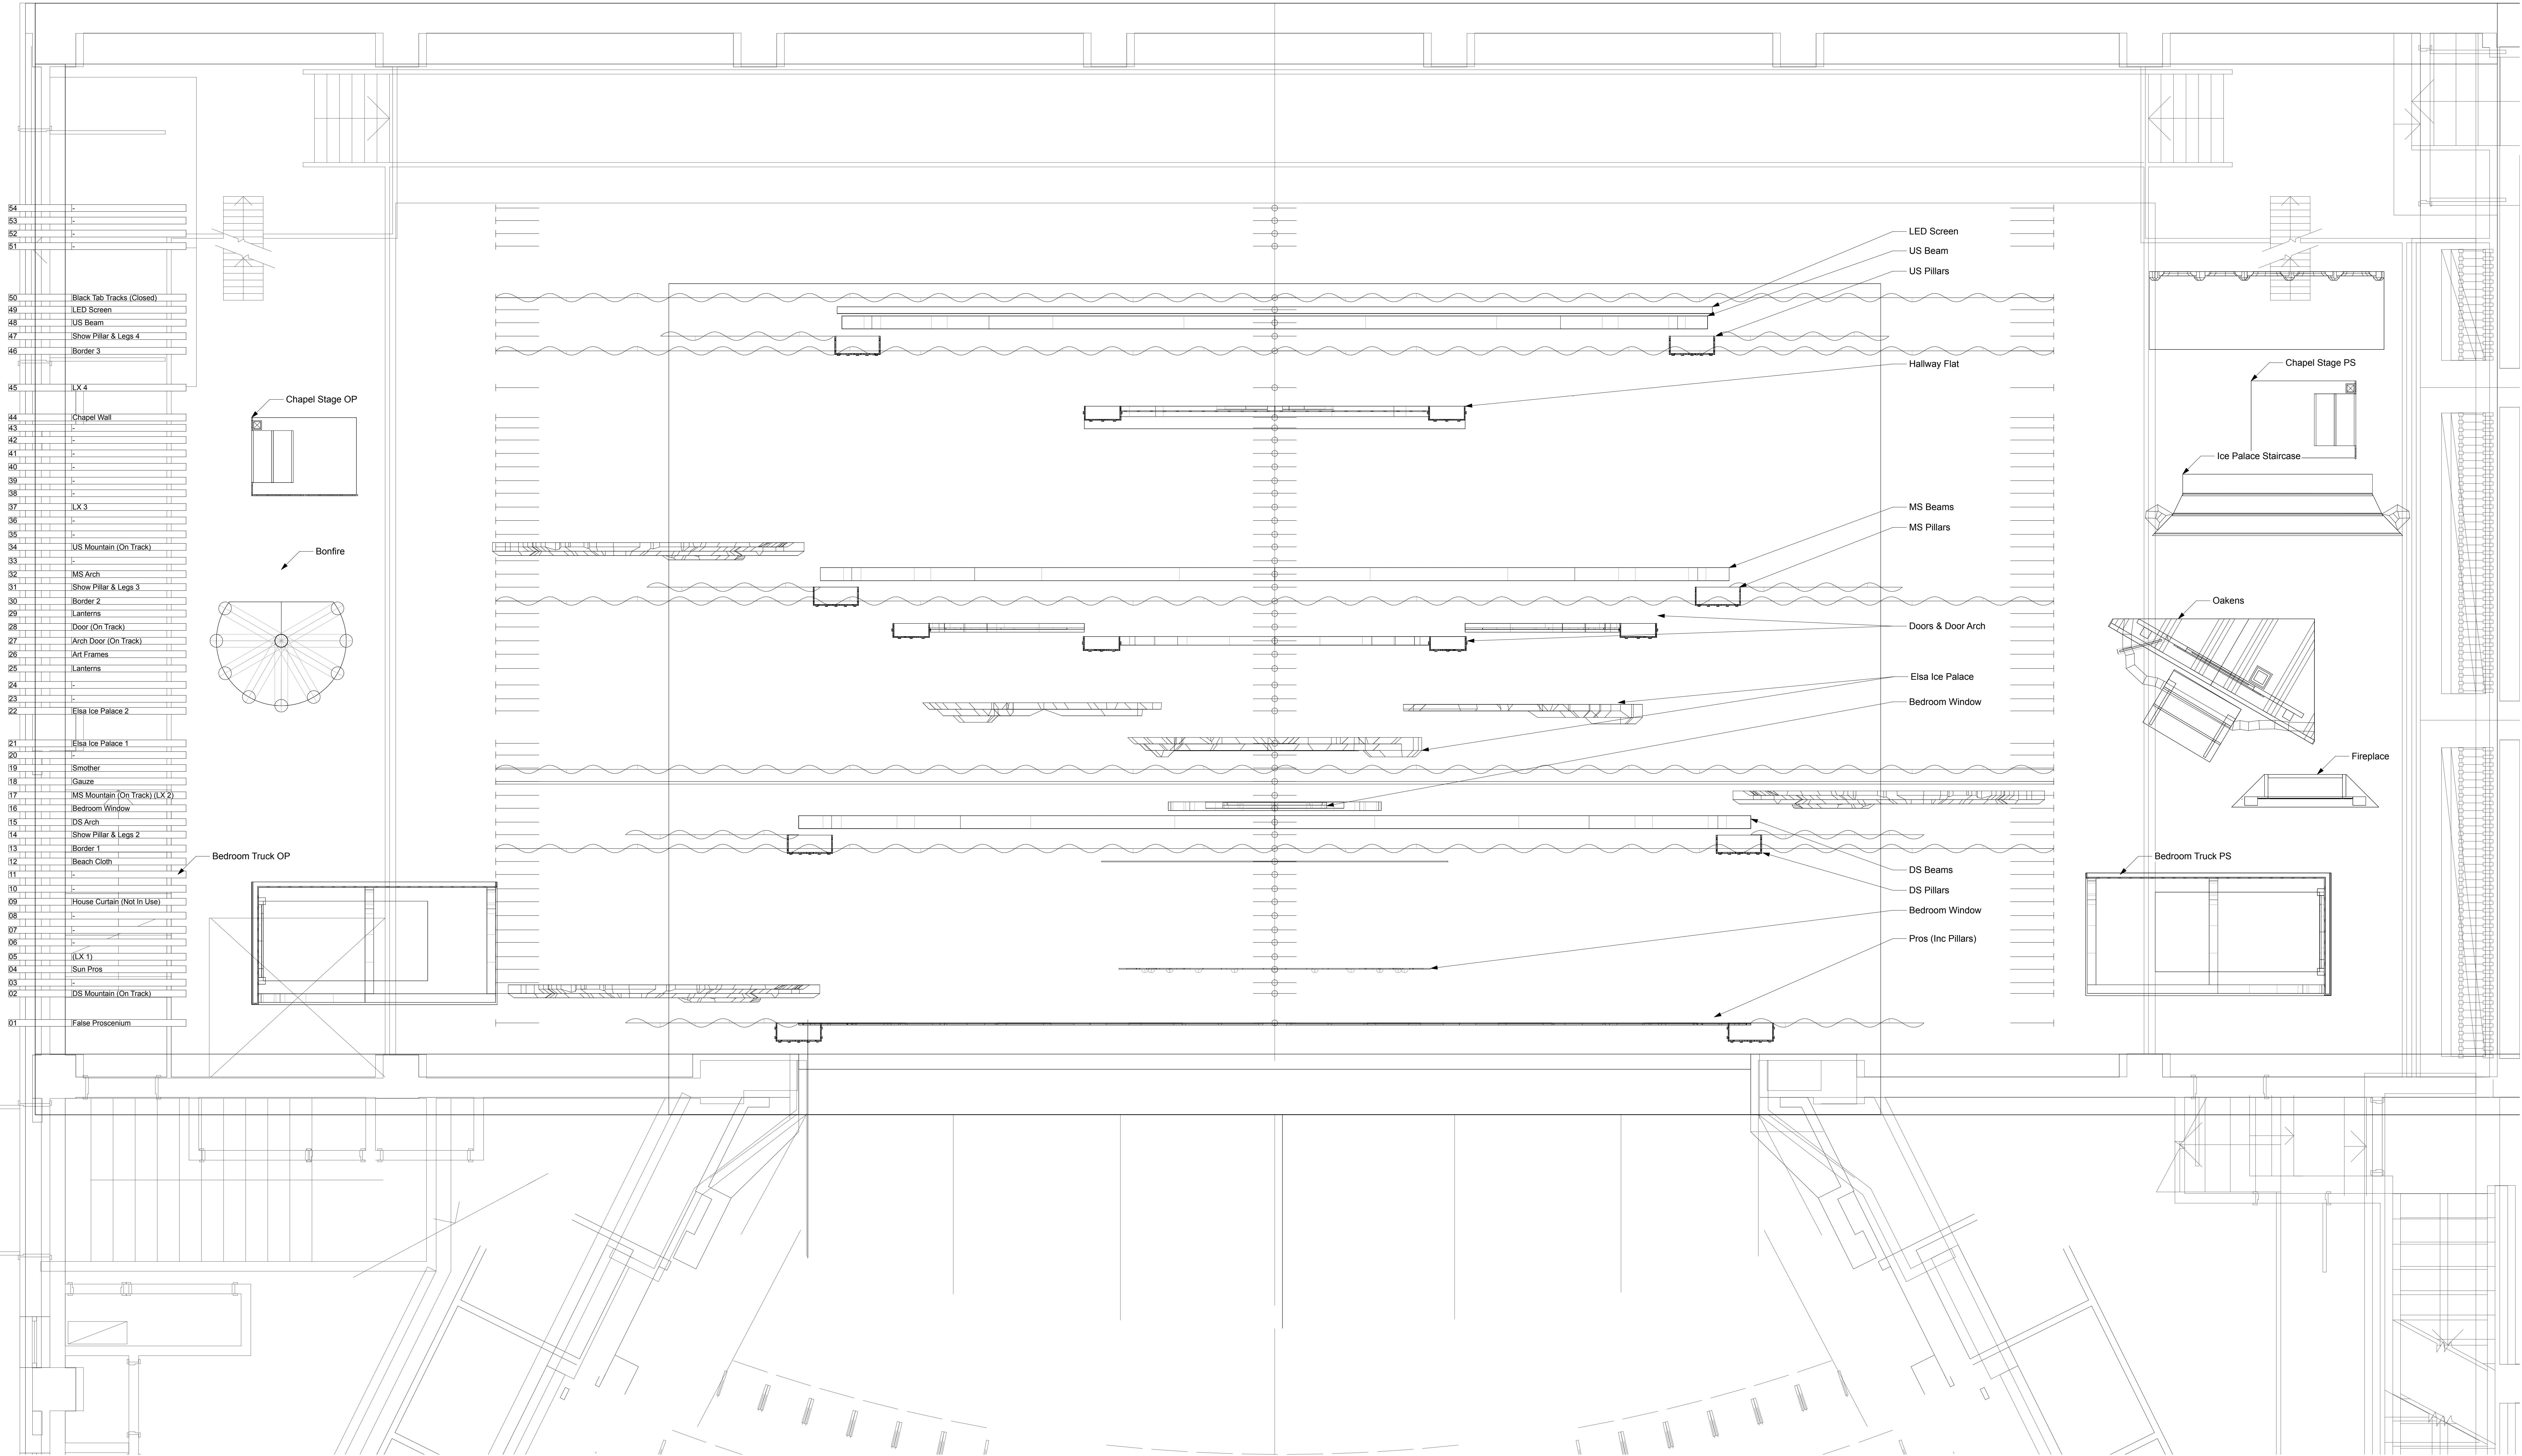


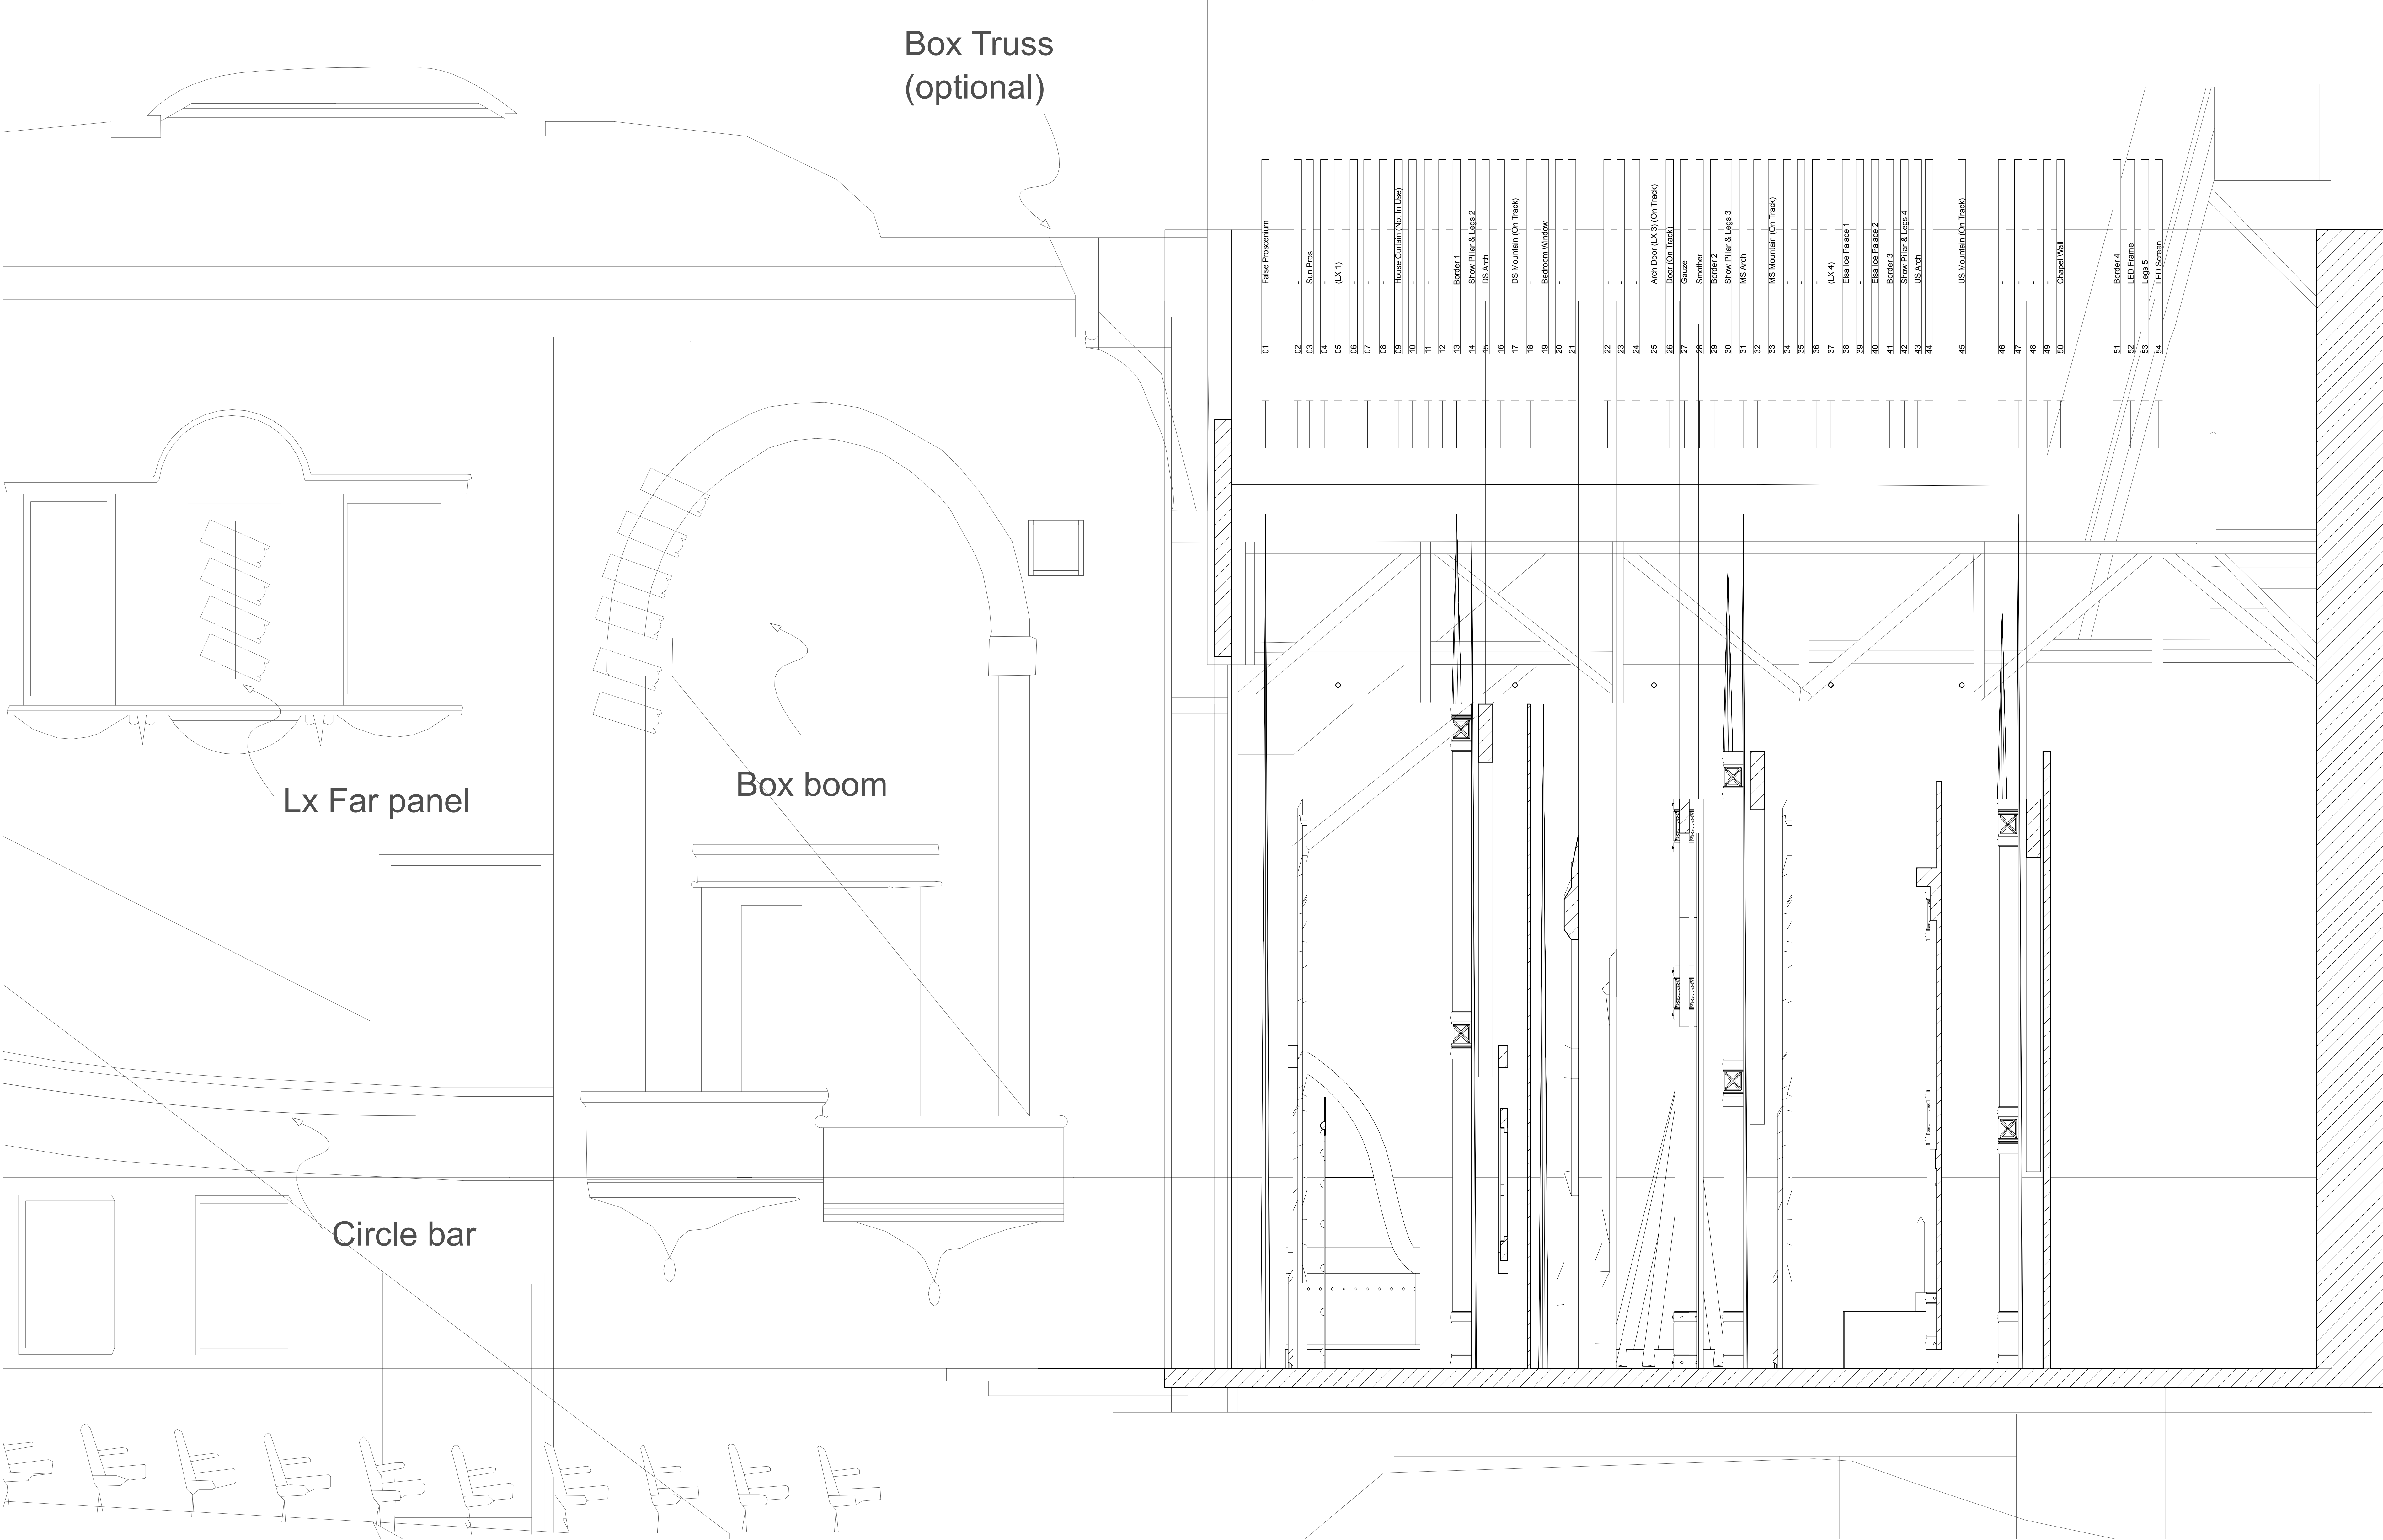

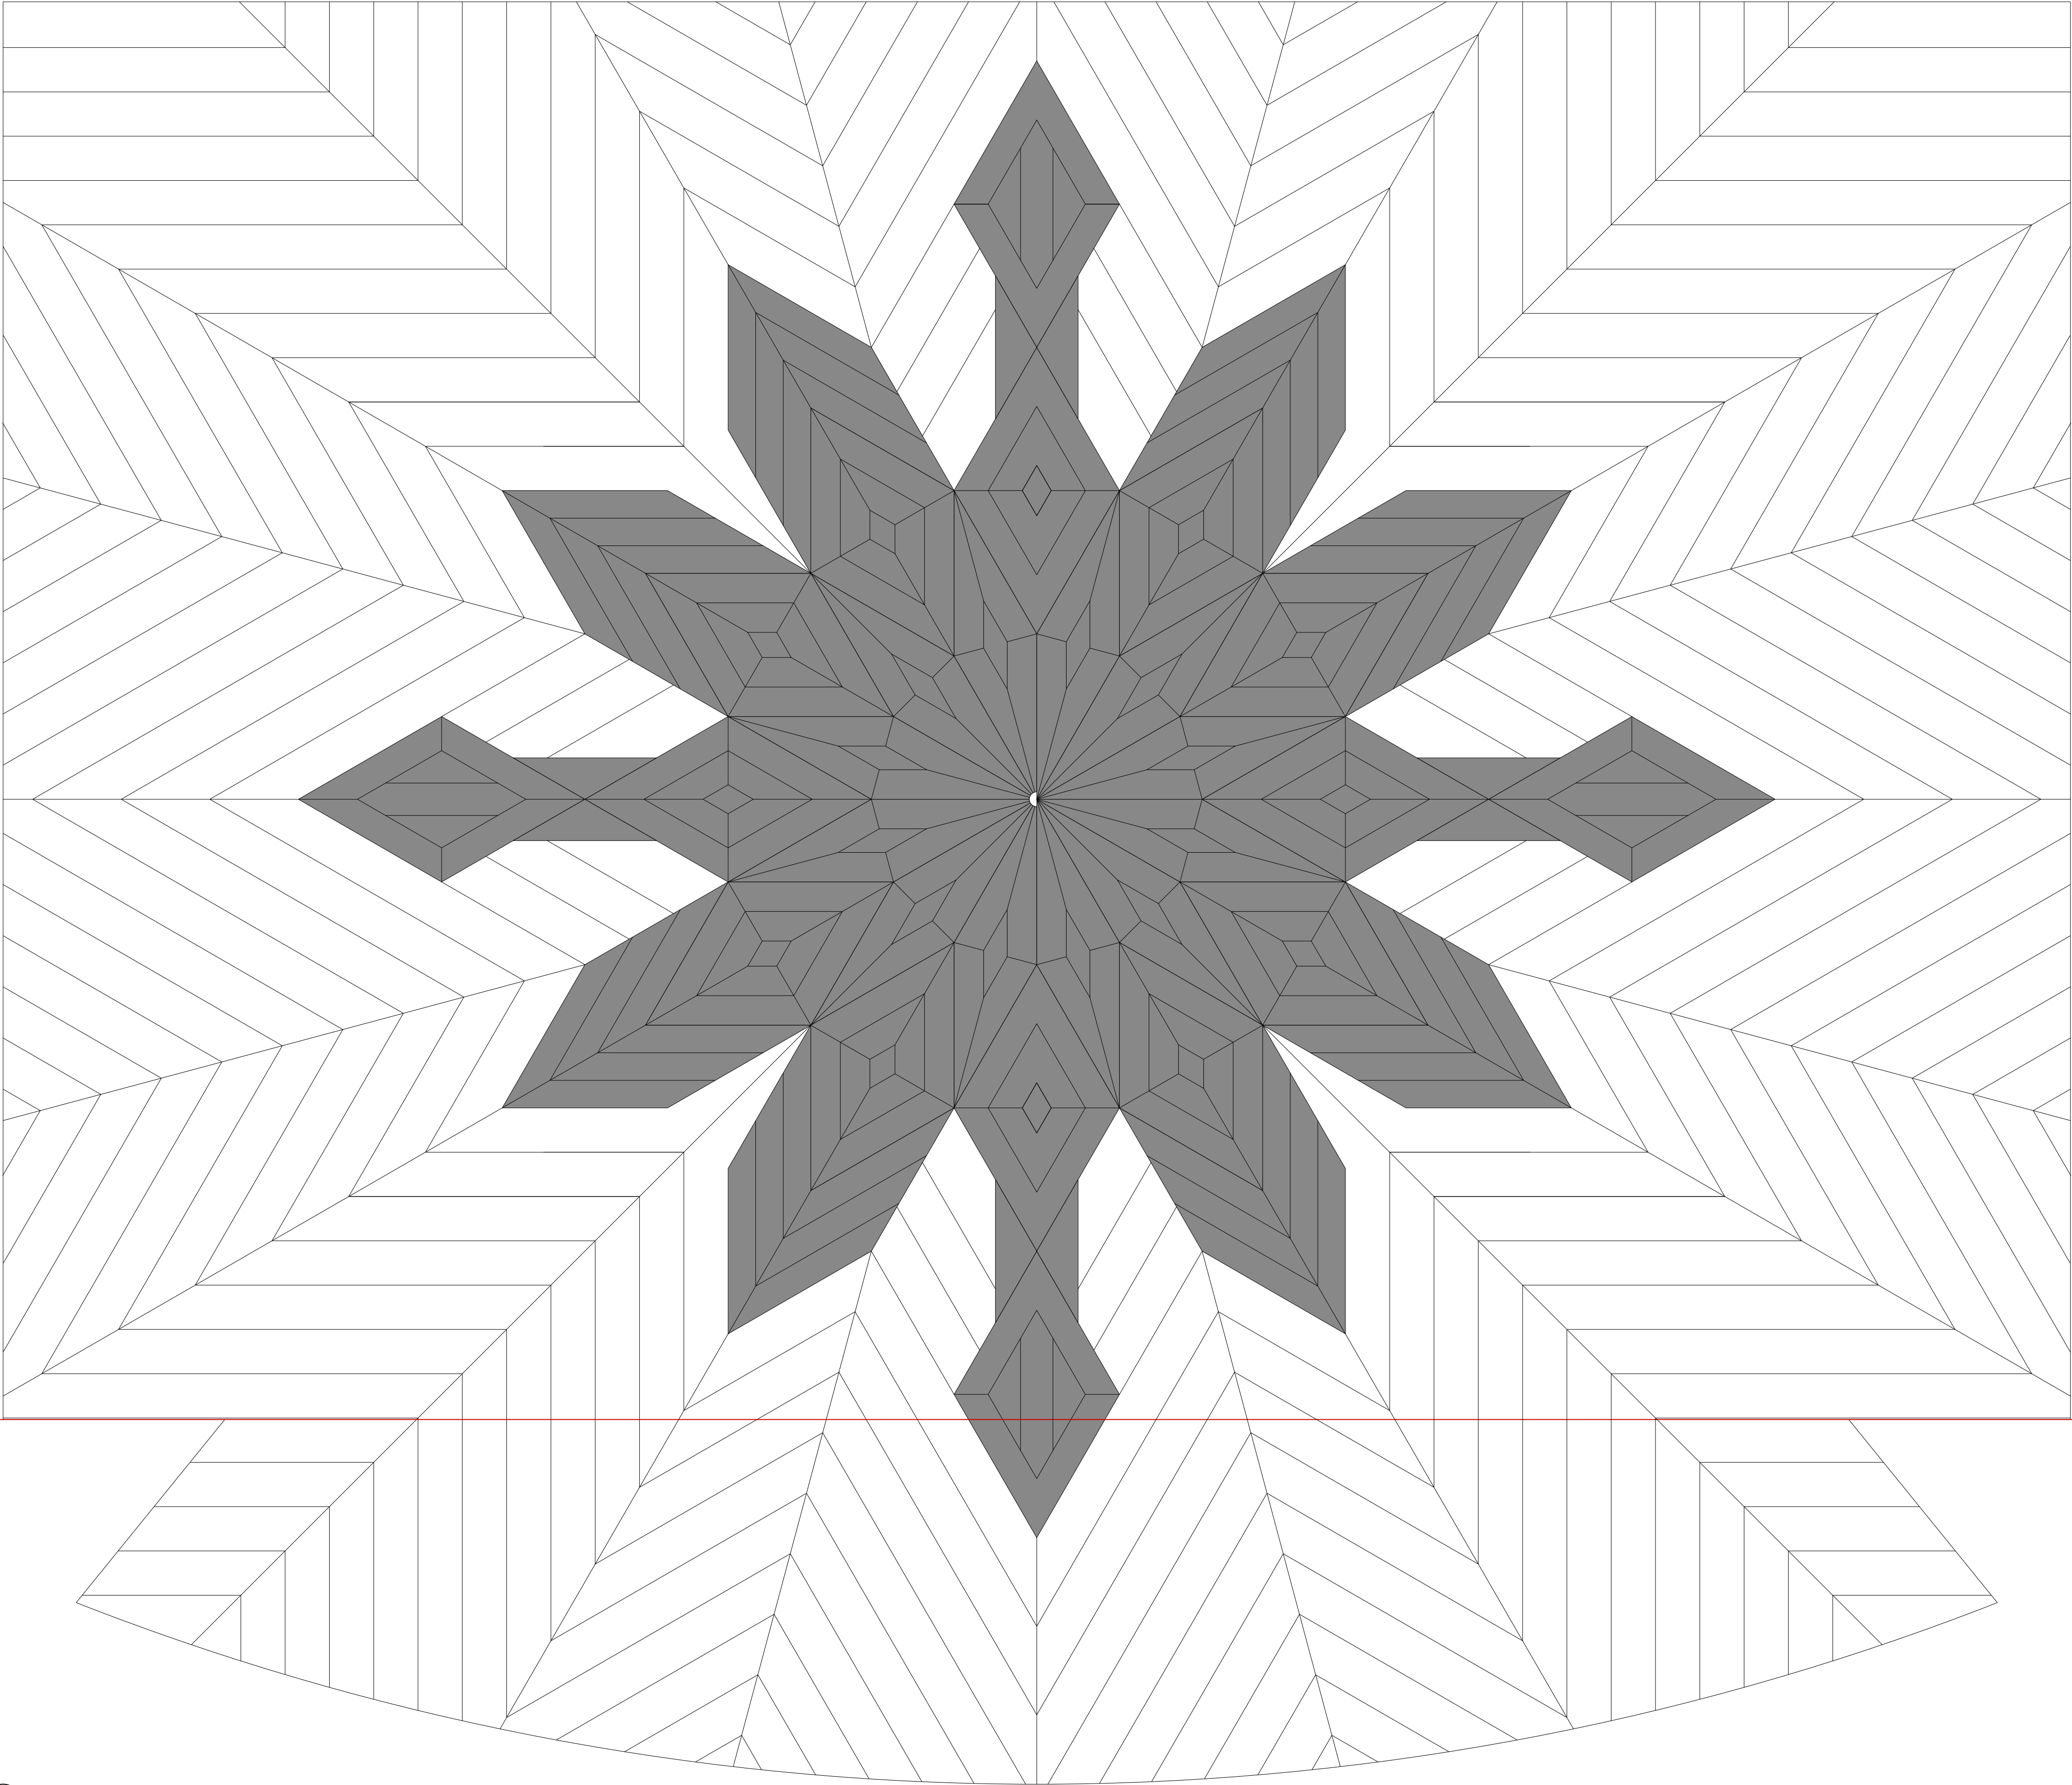


SETTING LINE

Grey area treatment different to white area.
See scenic elevation for more info.

10800x14000 total floor area required

Floor now to include the apron. Detail
pending accurate drawings from venue.

Frozen	
CentreStage	
Civic Theatre Newcastle	
Floor Detail	
Architect	Vectorworks
Client	CentreStage
Project Name	Frozen
Scale	1:25 @ A1
Date	12/07/2026
Drawn By	03 of 26
Checked By	
Project Manager	
Project Number	
Project Name	
Project Address	
Project Phone	
Project Email	
Project Website	
Project Social Media	
Project Logo	
Project Footer	

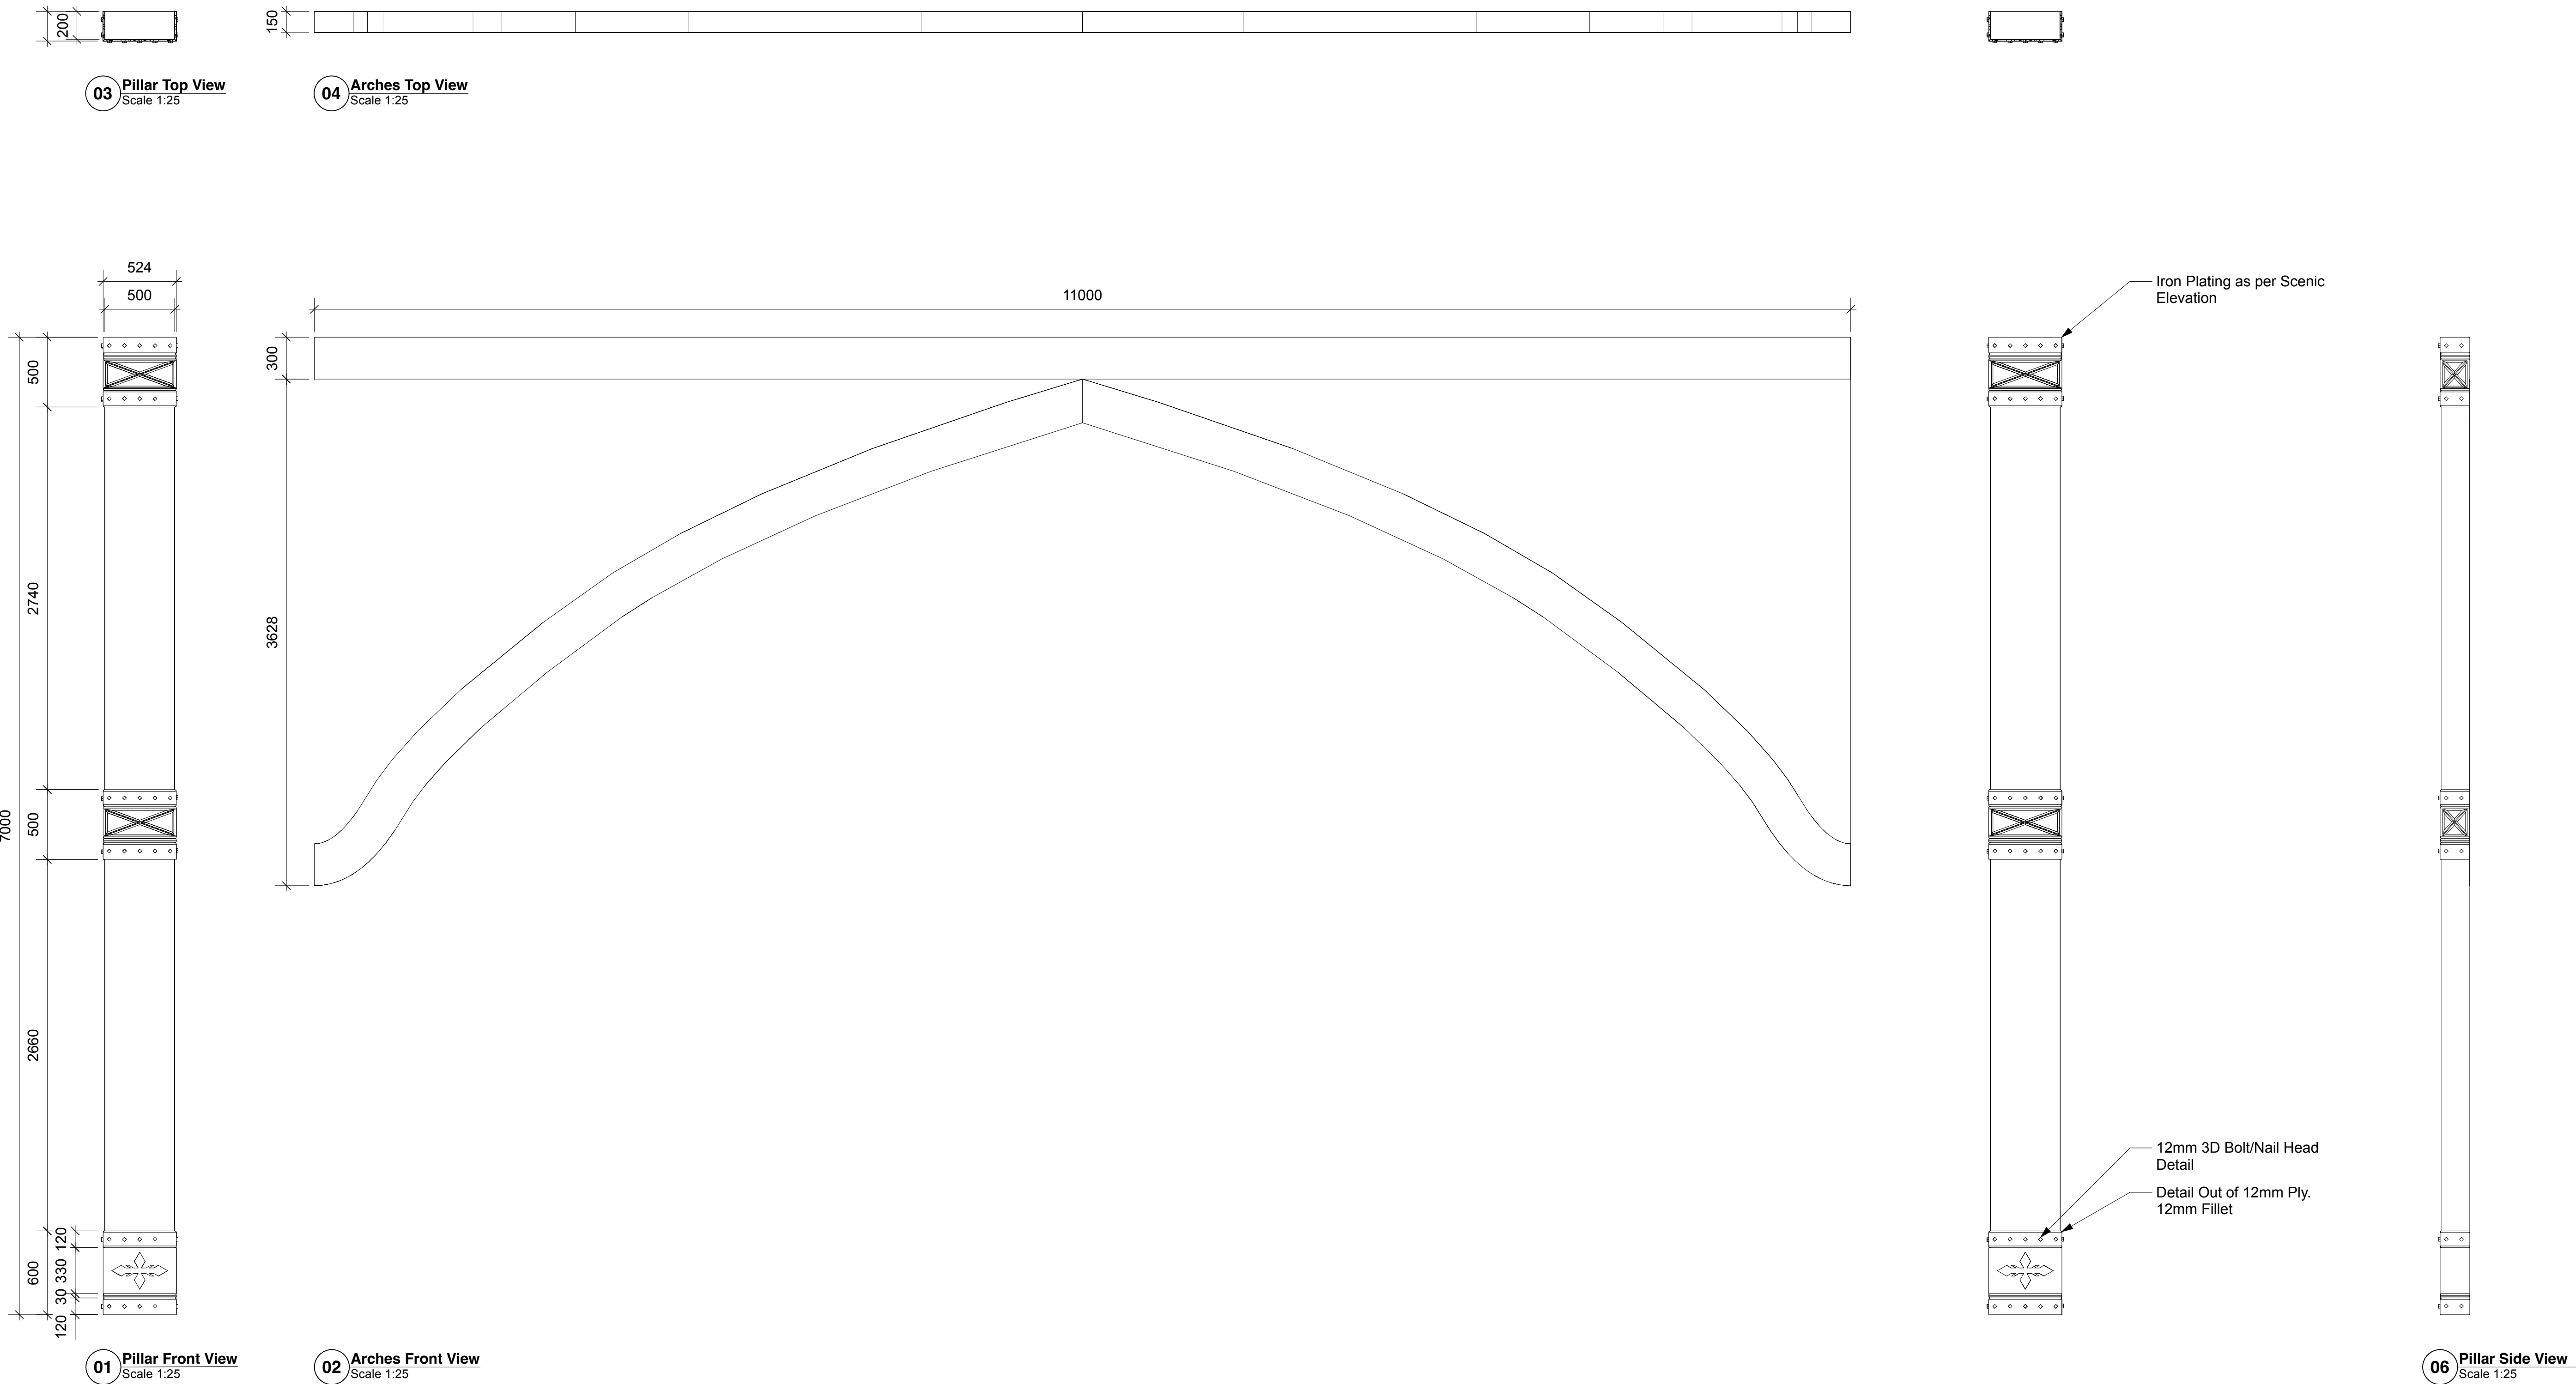



Arch and Pillars are seperate pieces.

Archs fly in and out, Pillars are stationary


Iron Plating detail only required on front and onstage side of each pillar.

Frozen	
CentreStage	
Civic Theatre Newcastle	
DS Pillars & Arches Detail	
1:25 @ A1	12/07/2026
04 of 26	
8.0	





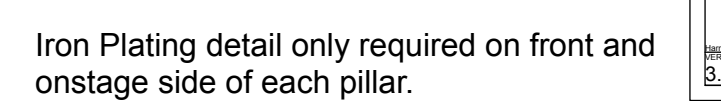


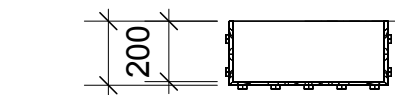

03 Pillar Top View
Scale 1:25

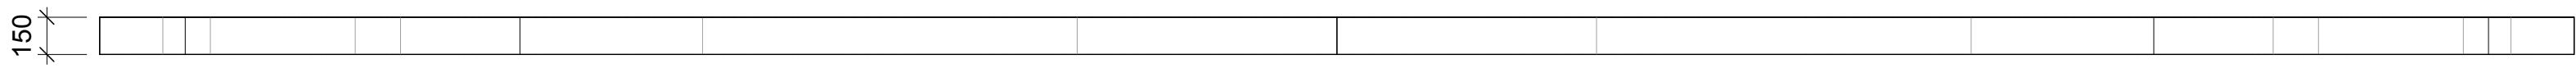

04 Arches Top View
Scale 1:25

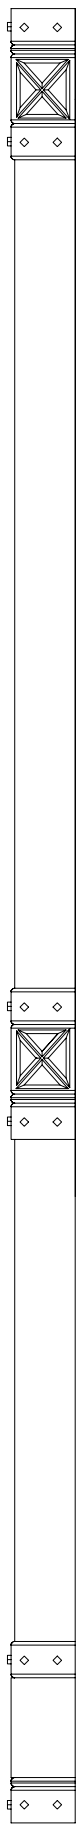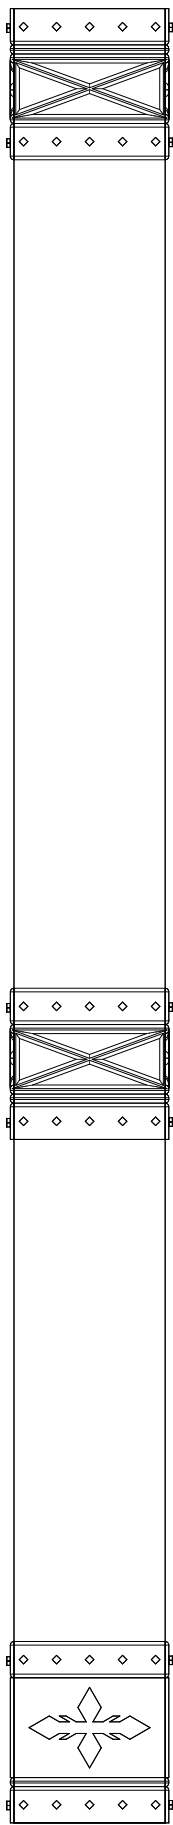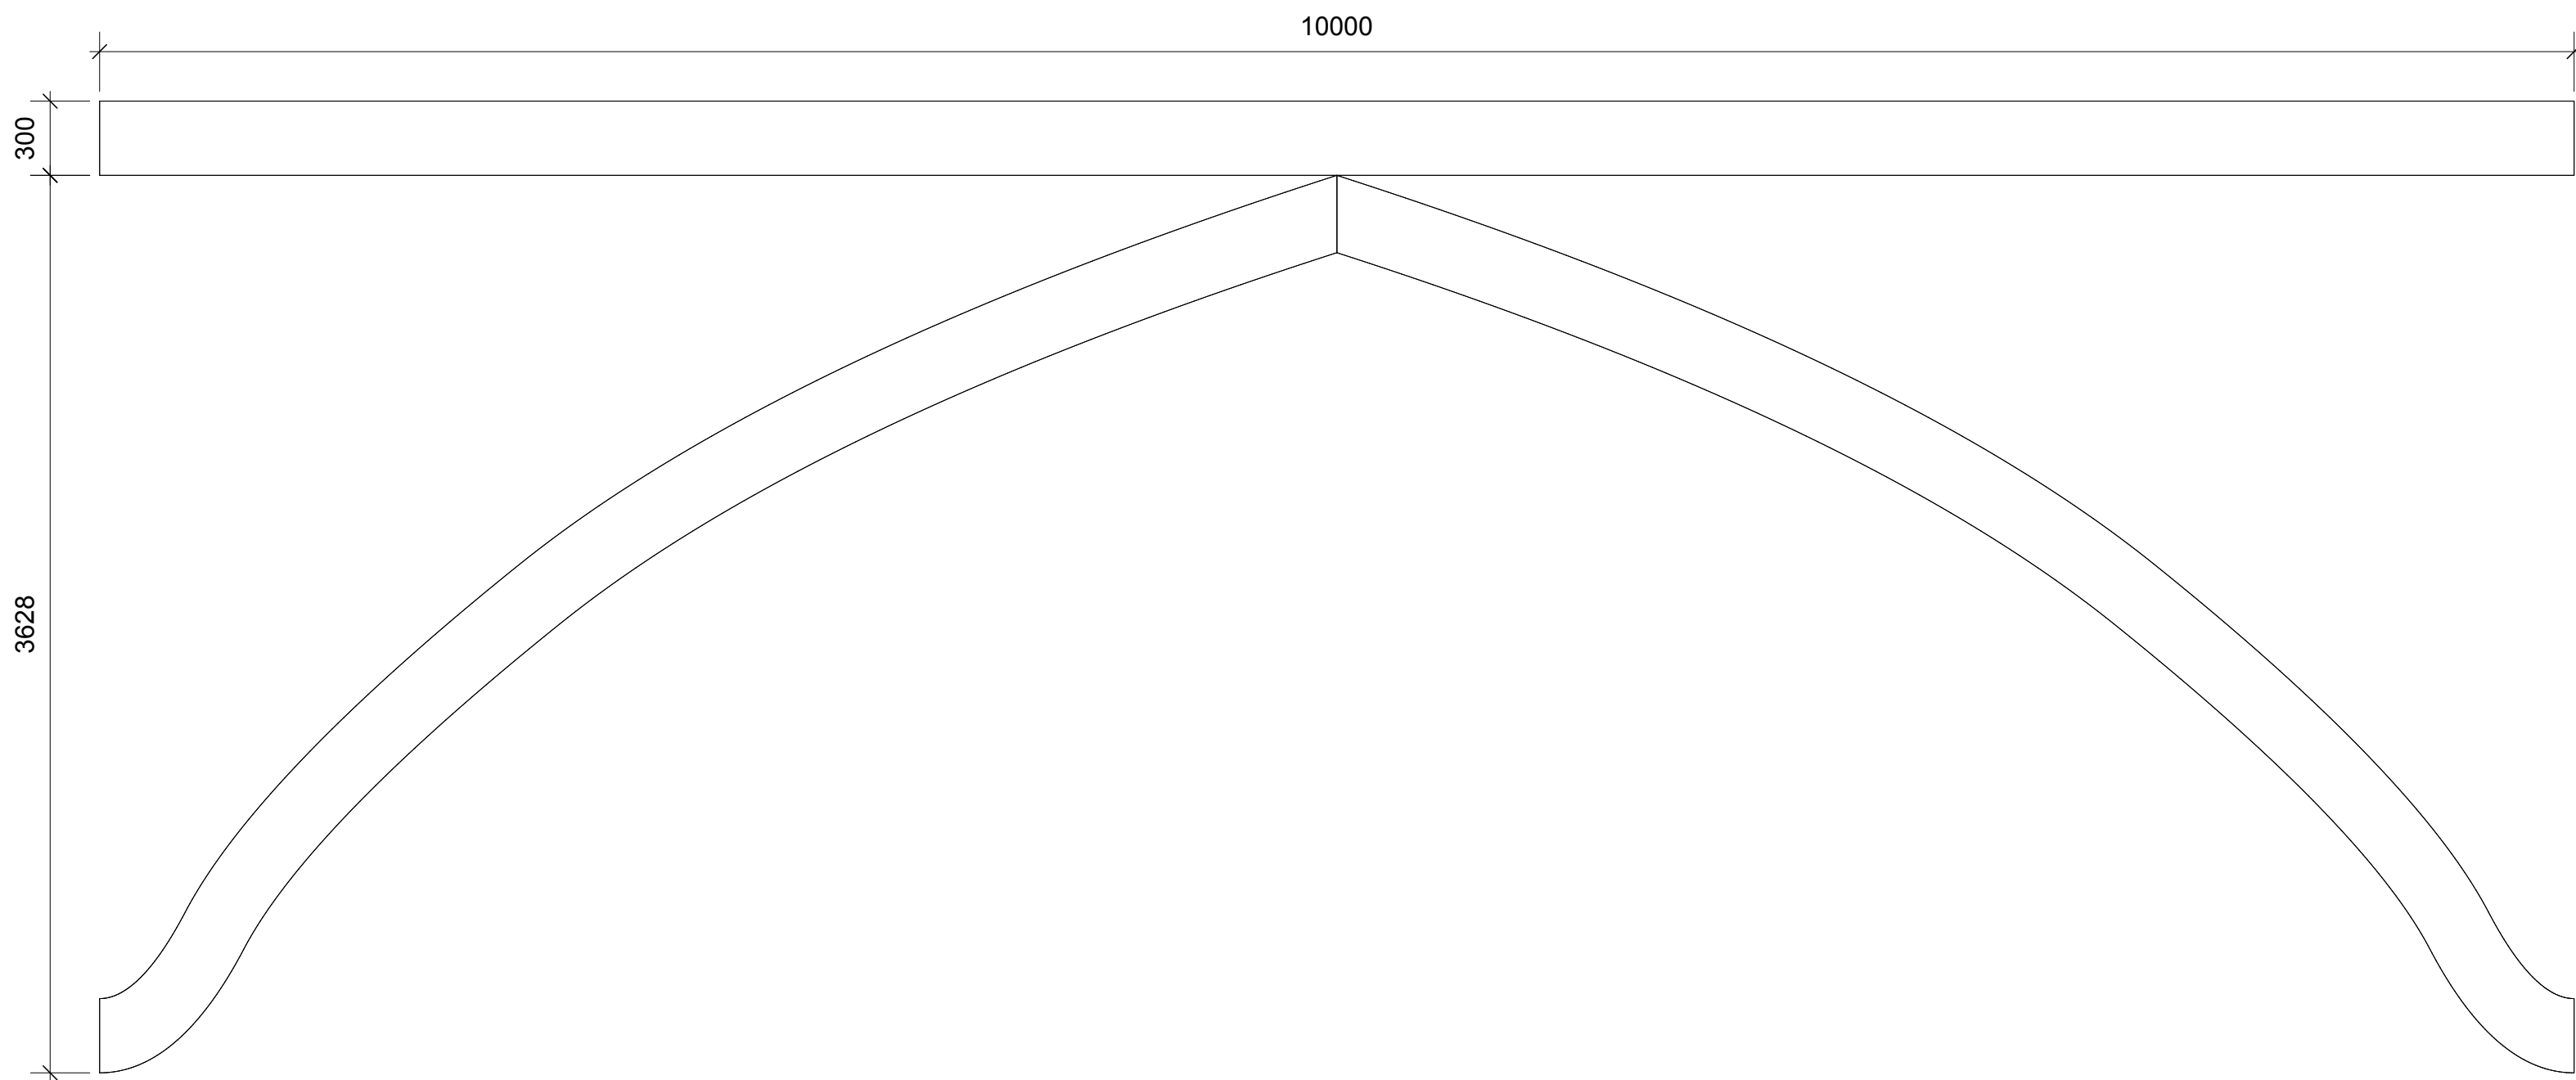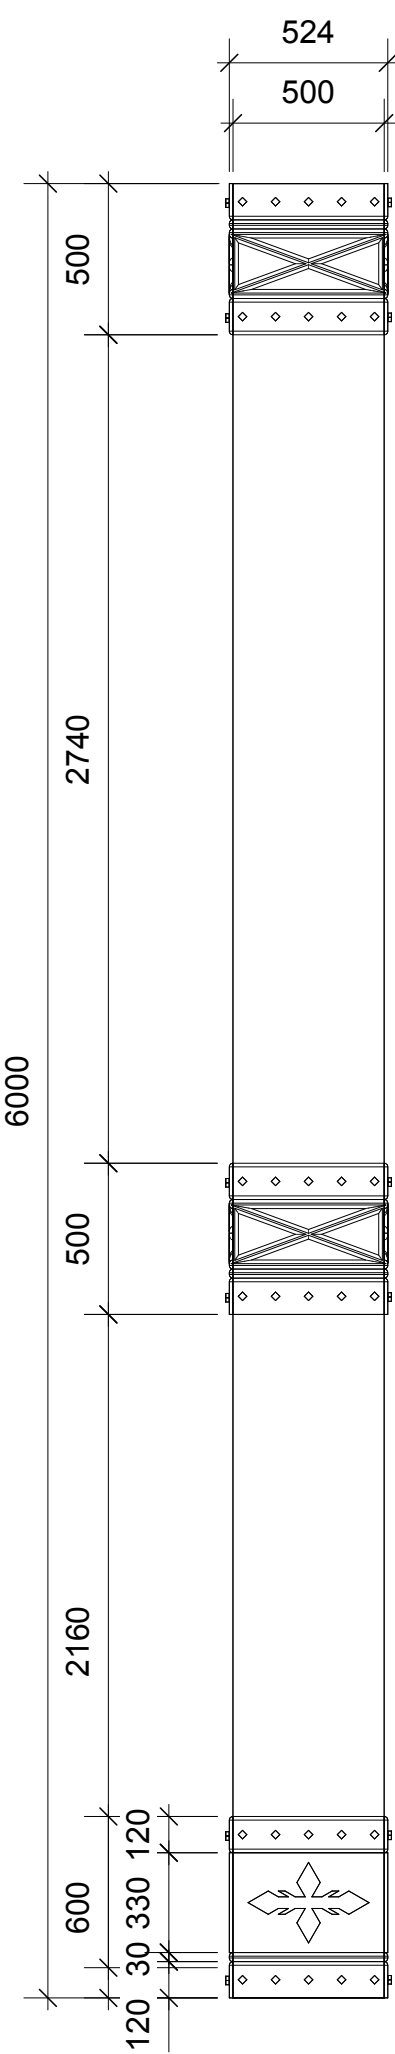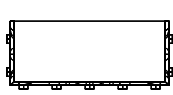


06 Pillar Side View
Scale 1:25

Arch and Pillars are seperate pieces.


Archs fly in and out, Pillars are stationary

Iron Plating detail only required on front and onstage side of each pillar.


Frozen	
CentreStage	
Civic Theatre Newcastle	
US Pilairs & Arches Detail	
DATE:	12/07/2026
BY:	12/07/2026
1:25 @ A1	12/07/2026
06 of 26	
8.0	

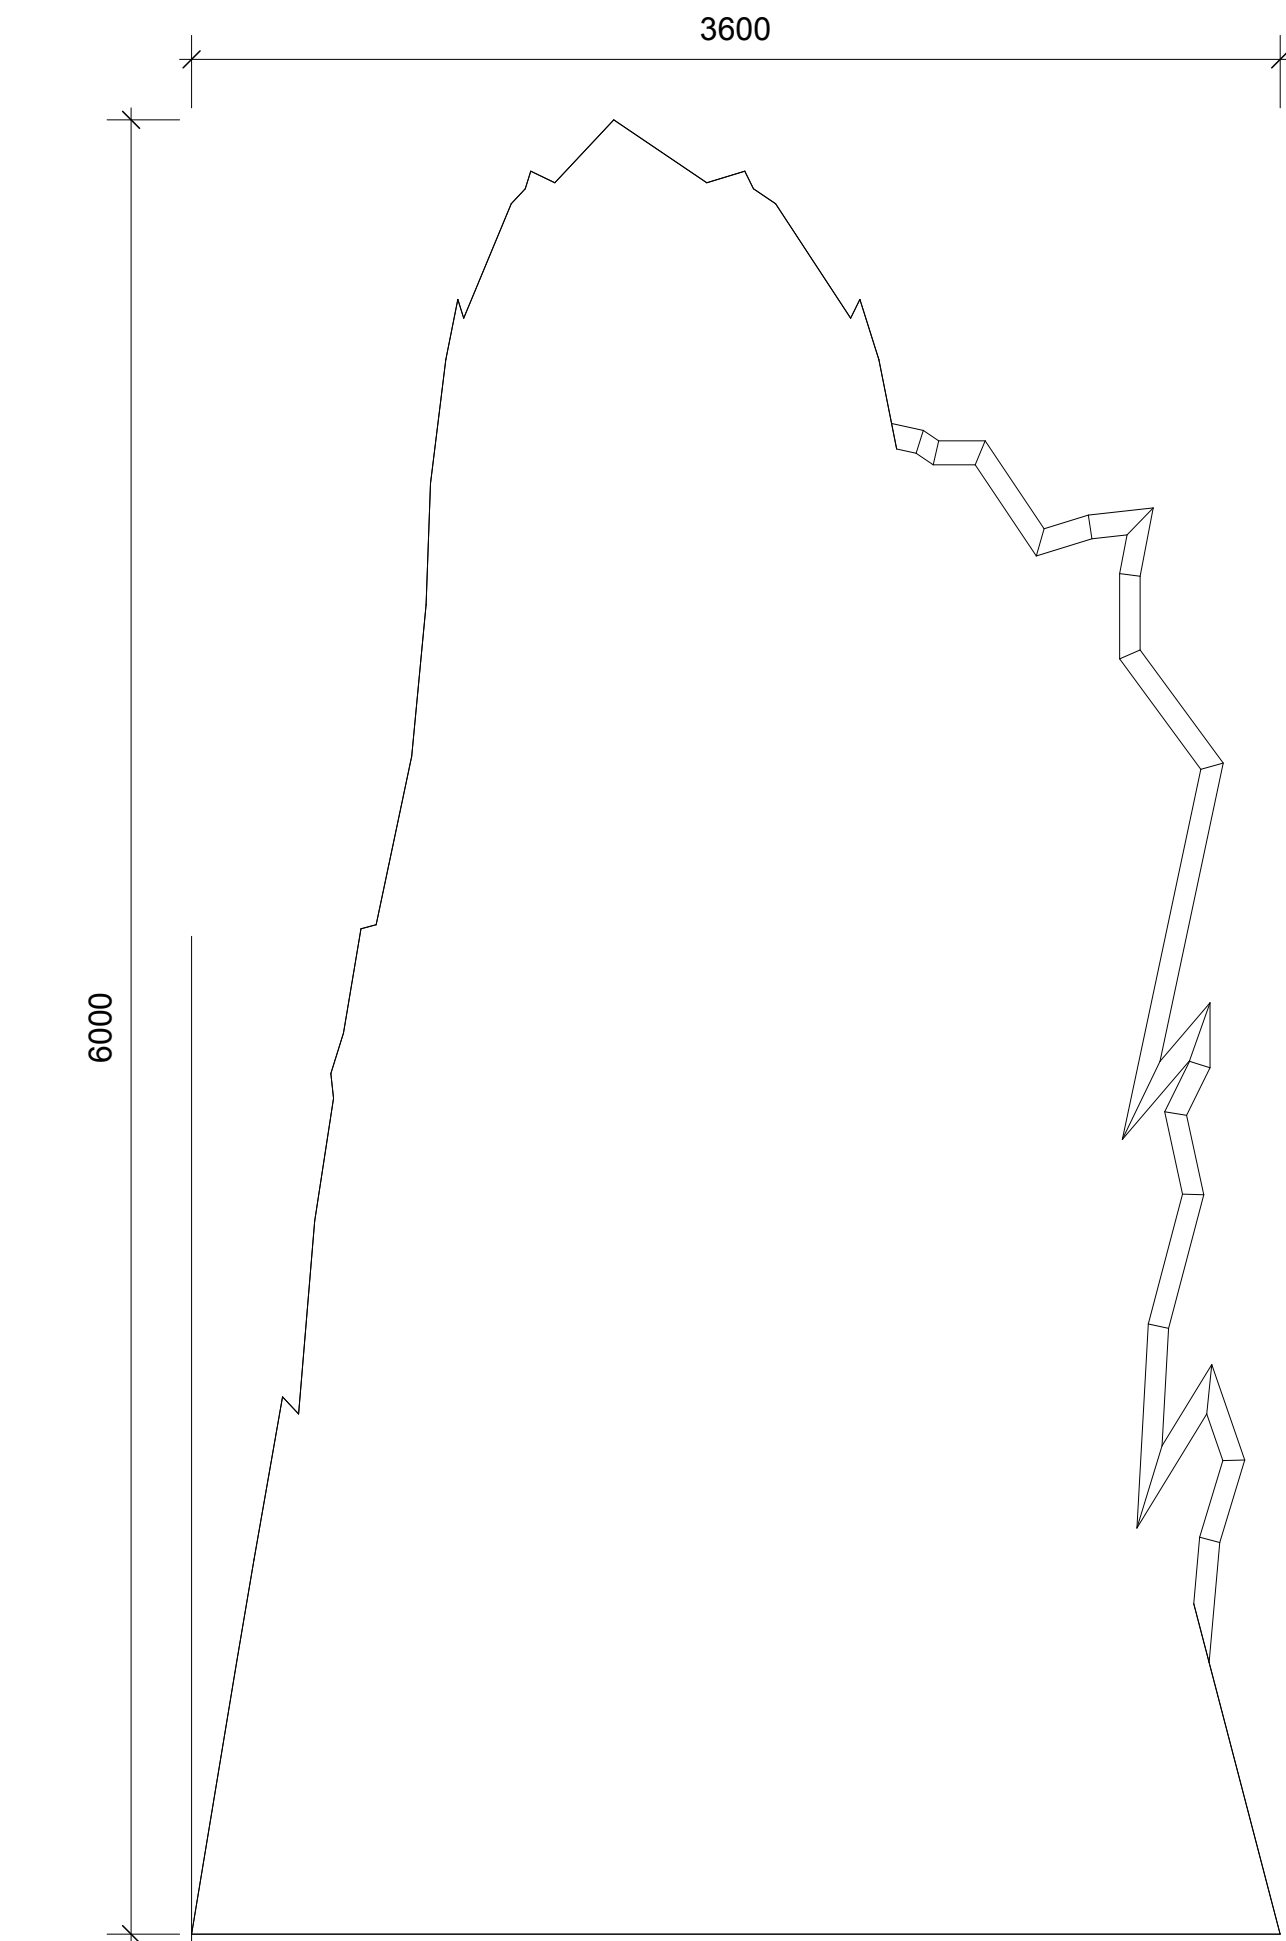


01 Mountain Layer 1
Scale 1:25

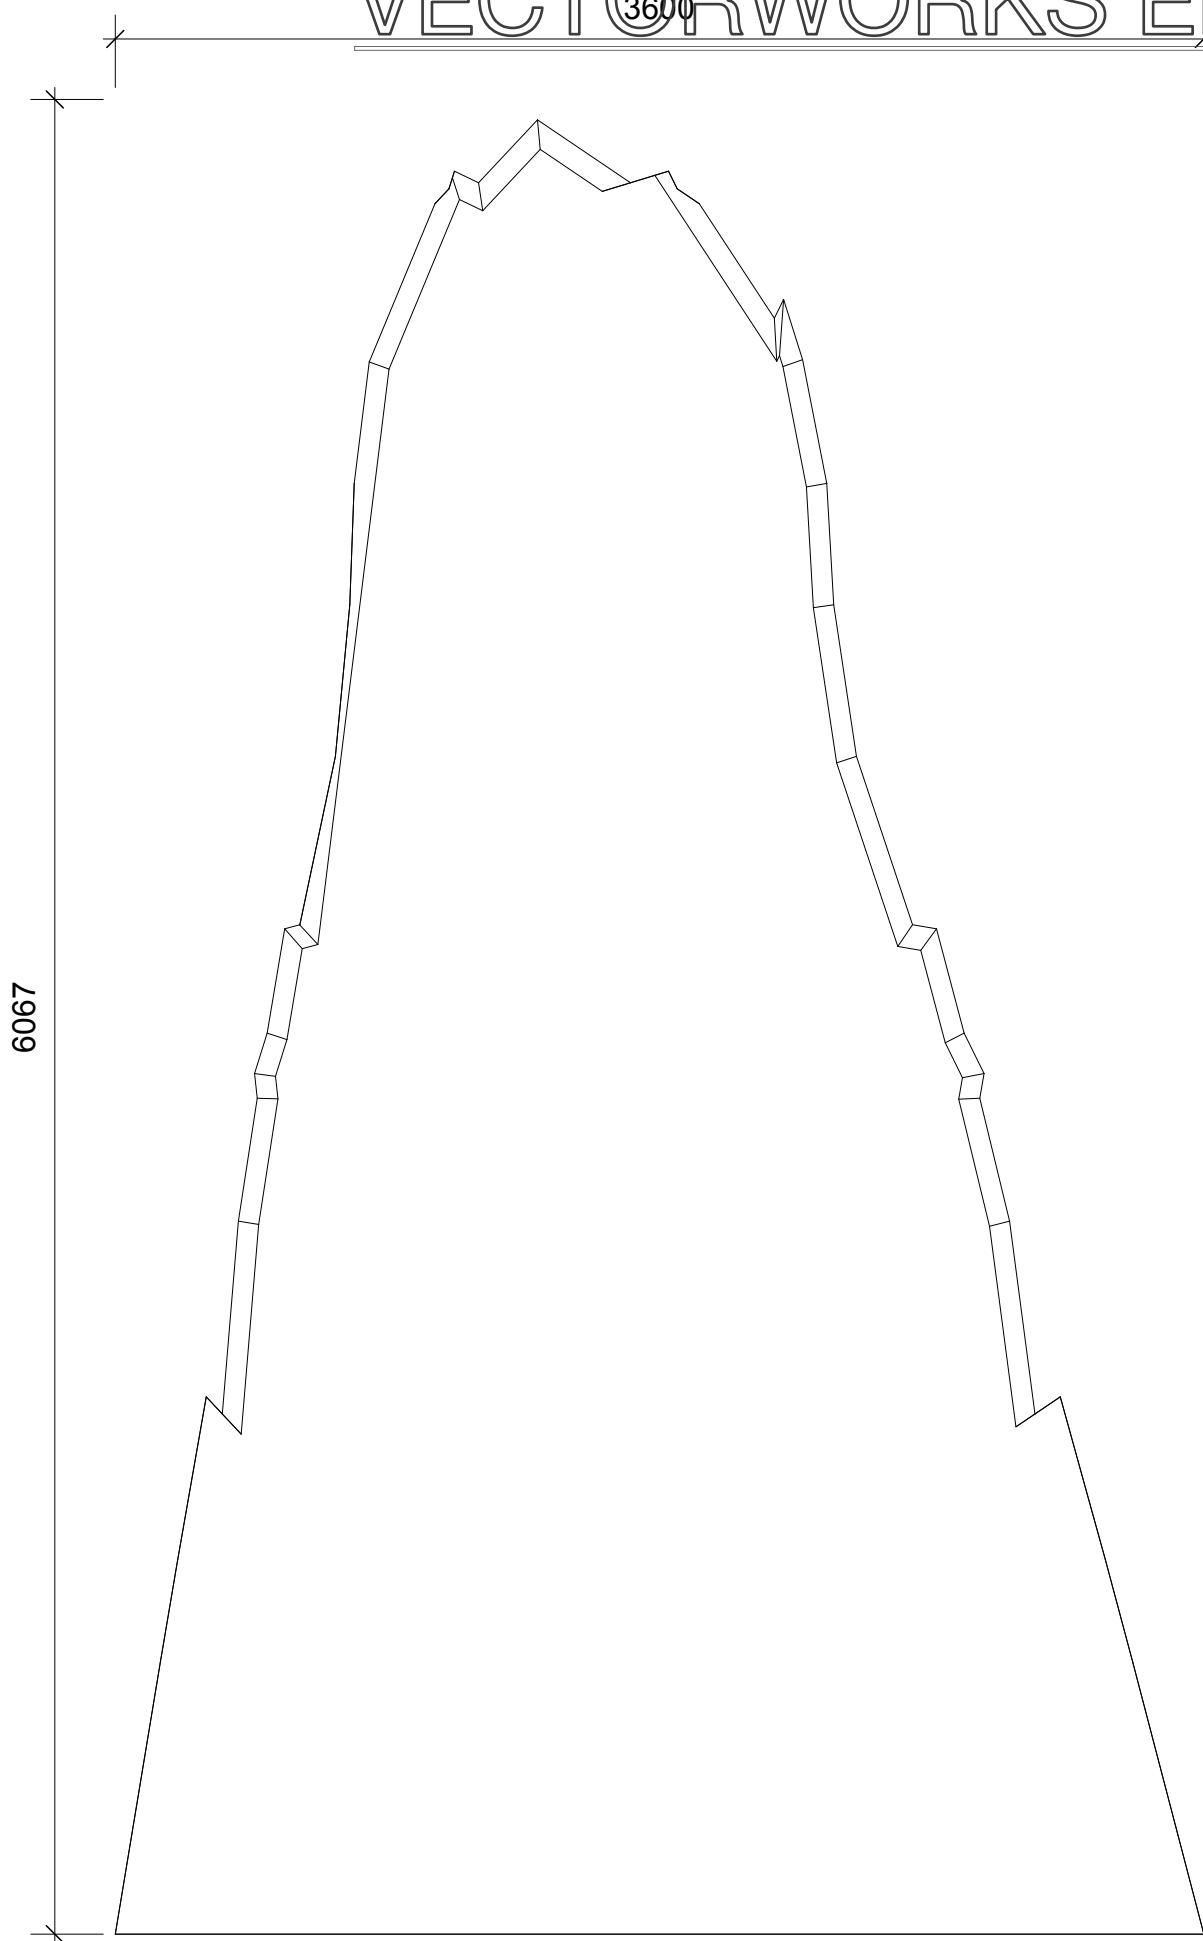


02 Mountain Layer 2
Scale 1:25

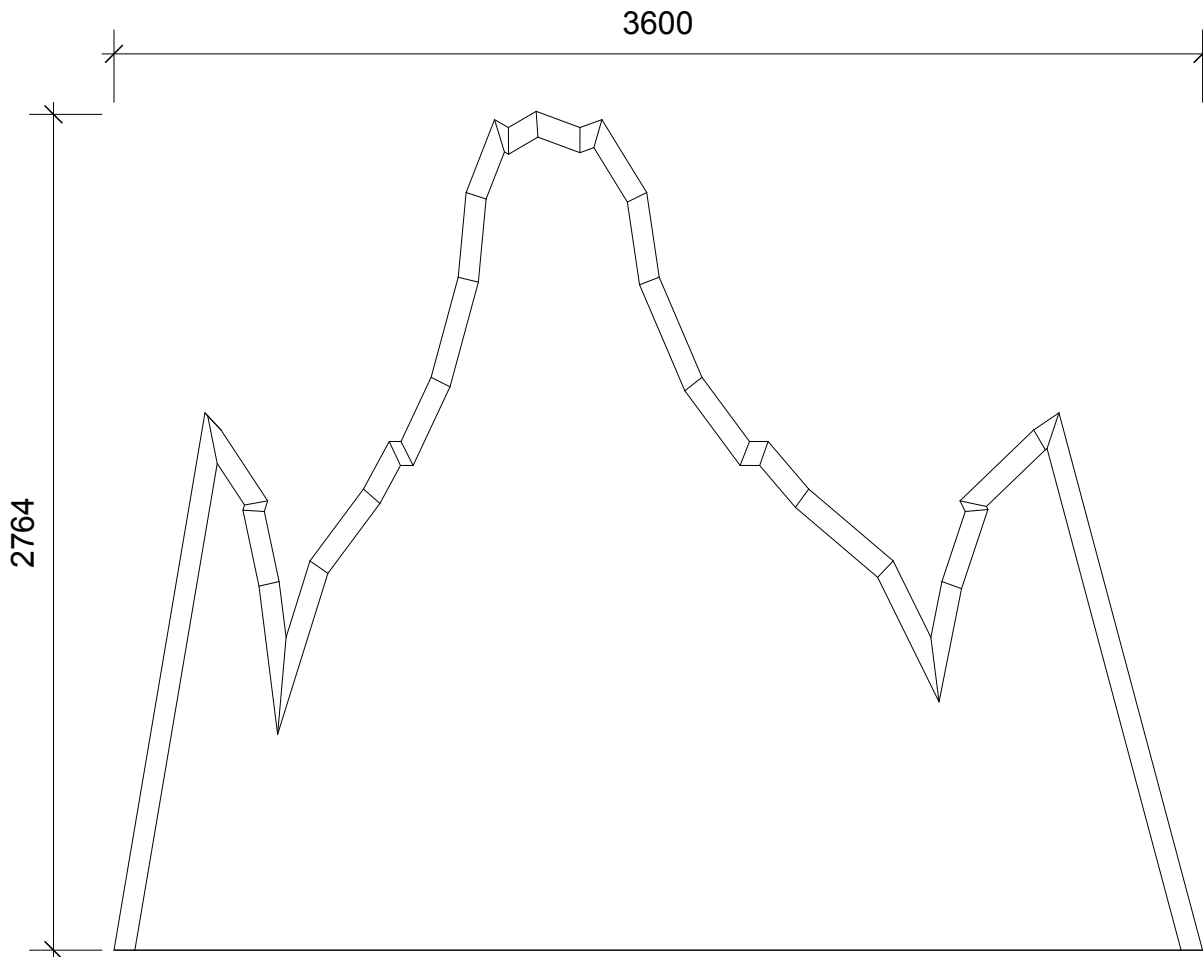


03 Mountain Layer 3
Scale 1:25

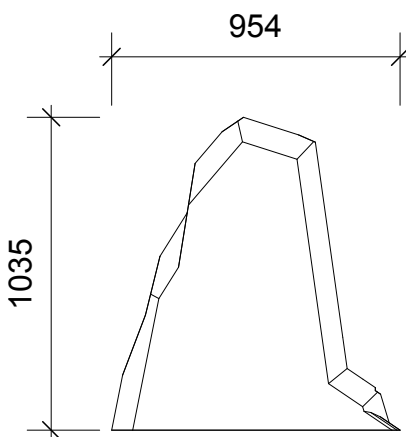


04 Mountain Layer 4
Scale 1:25

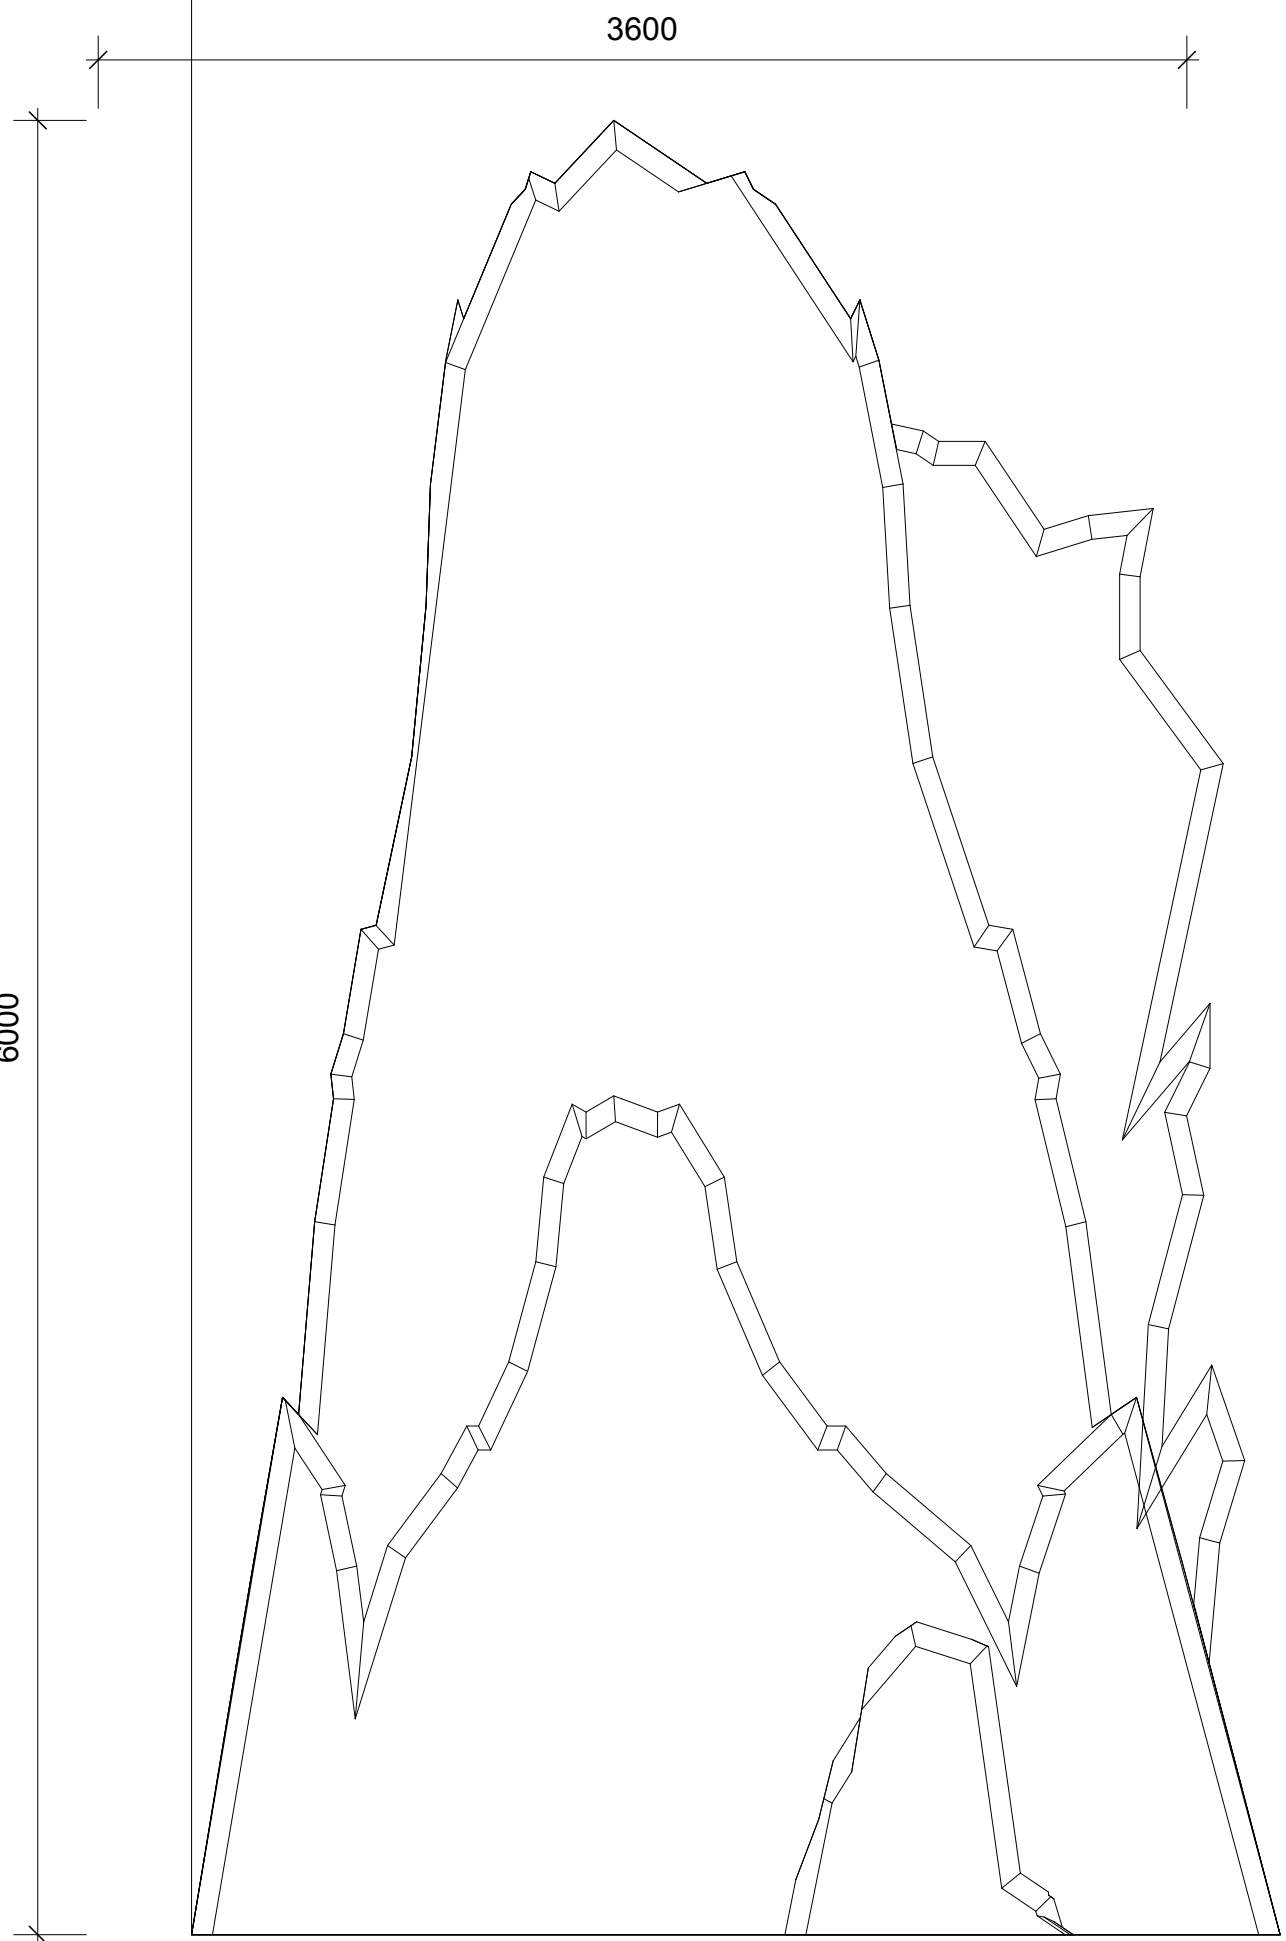


05 Mountain 1 Front
Scale 1:25

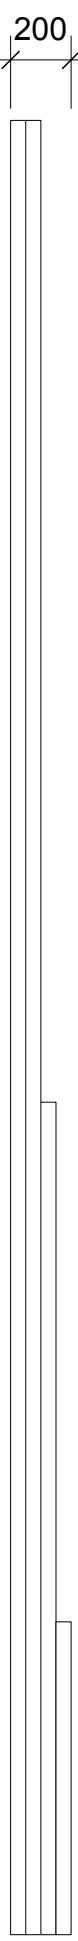

06 Mountain Side
Scale 1:25

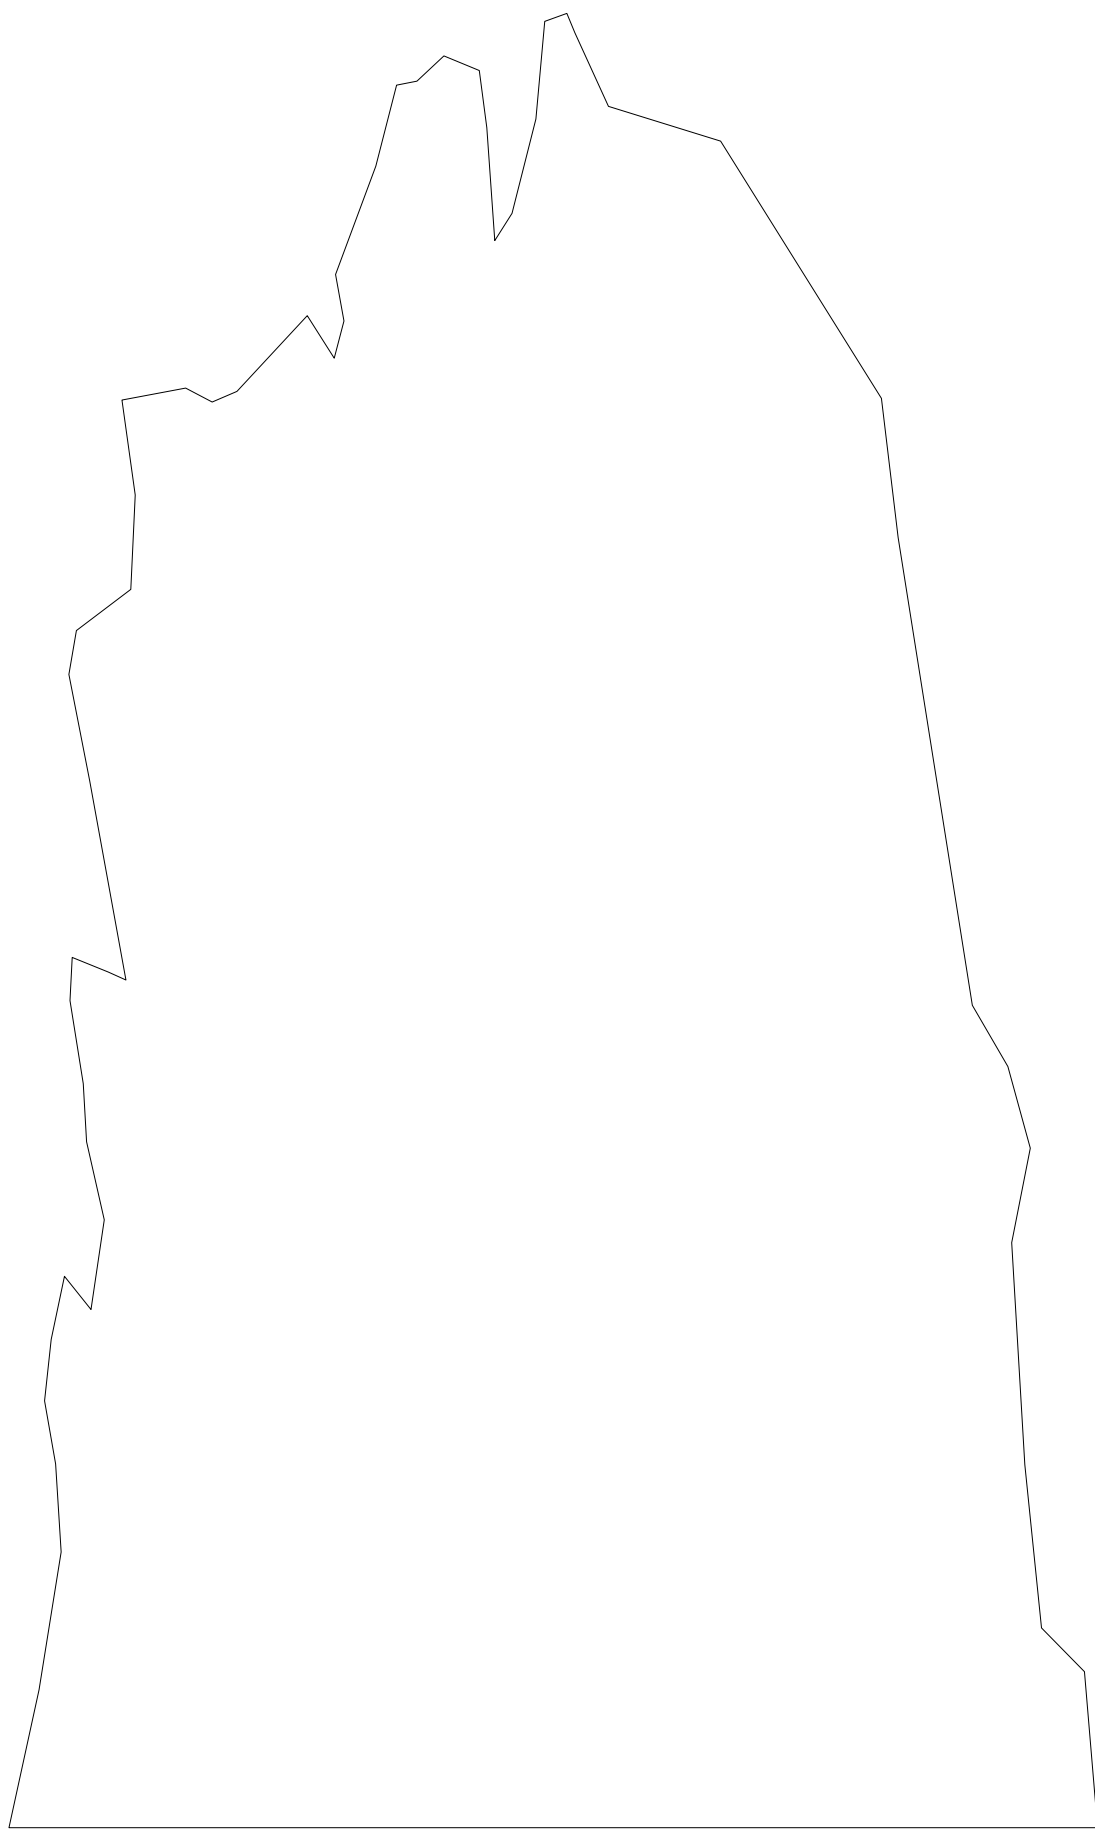

07 Mountain 2 Front Profile
Scale 1:25

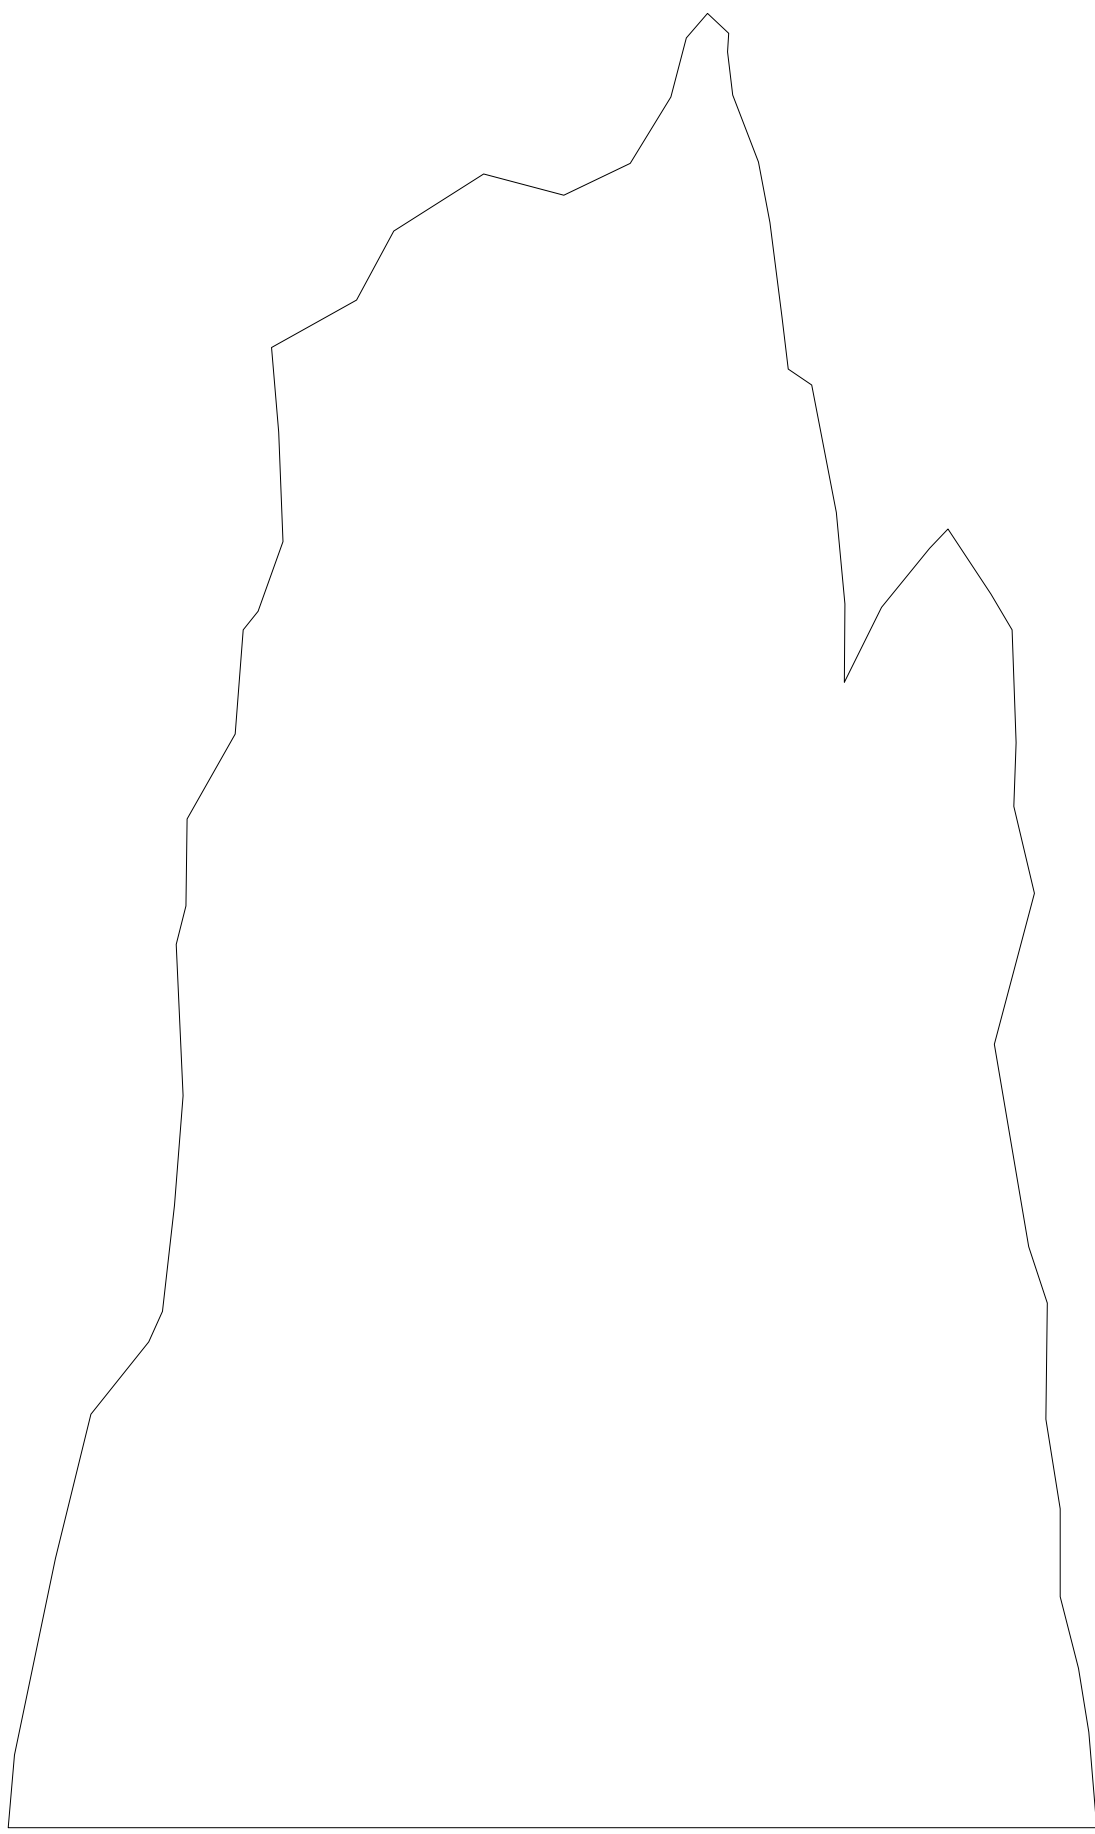


08 Mountain 3 Front Profile
Scale 1:25

Ice Mountains are made of 4x layers of a 50mm carvable material. More thickness ideal pending on cost/space in venue.


x3 Ice Mountains

All Ice Mountains to look slightly different.


Frozen	
CentreStage	
Civic Theatre Newcastle	
Project	Ice Mountains Detail
Client	CentreStage
Architect	CentreStage
Structural Engineer	CentreStage
1:25 @ A1	12/07/2026
07 of 26	
8.0	

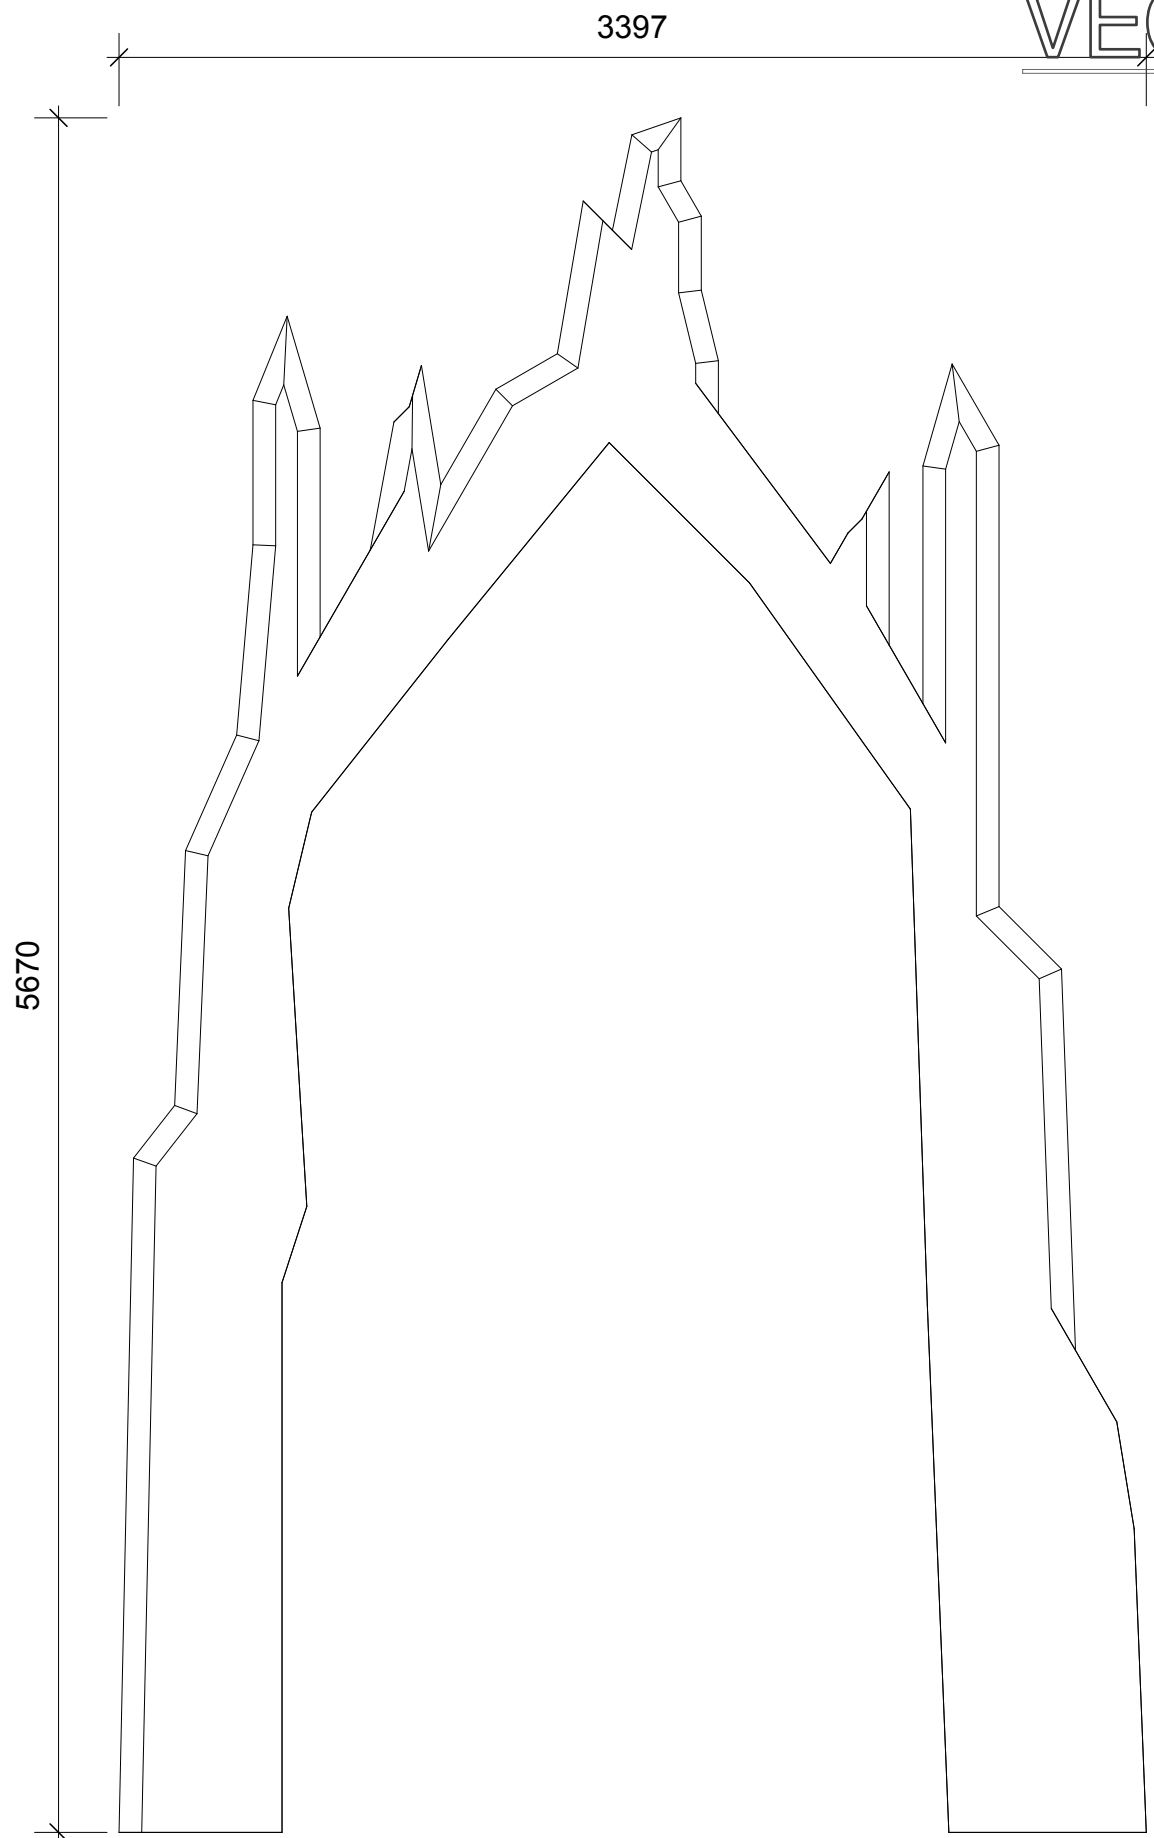



01 Ice Palace Layer 1
Scale 1:25

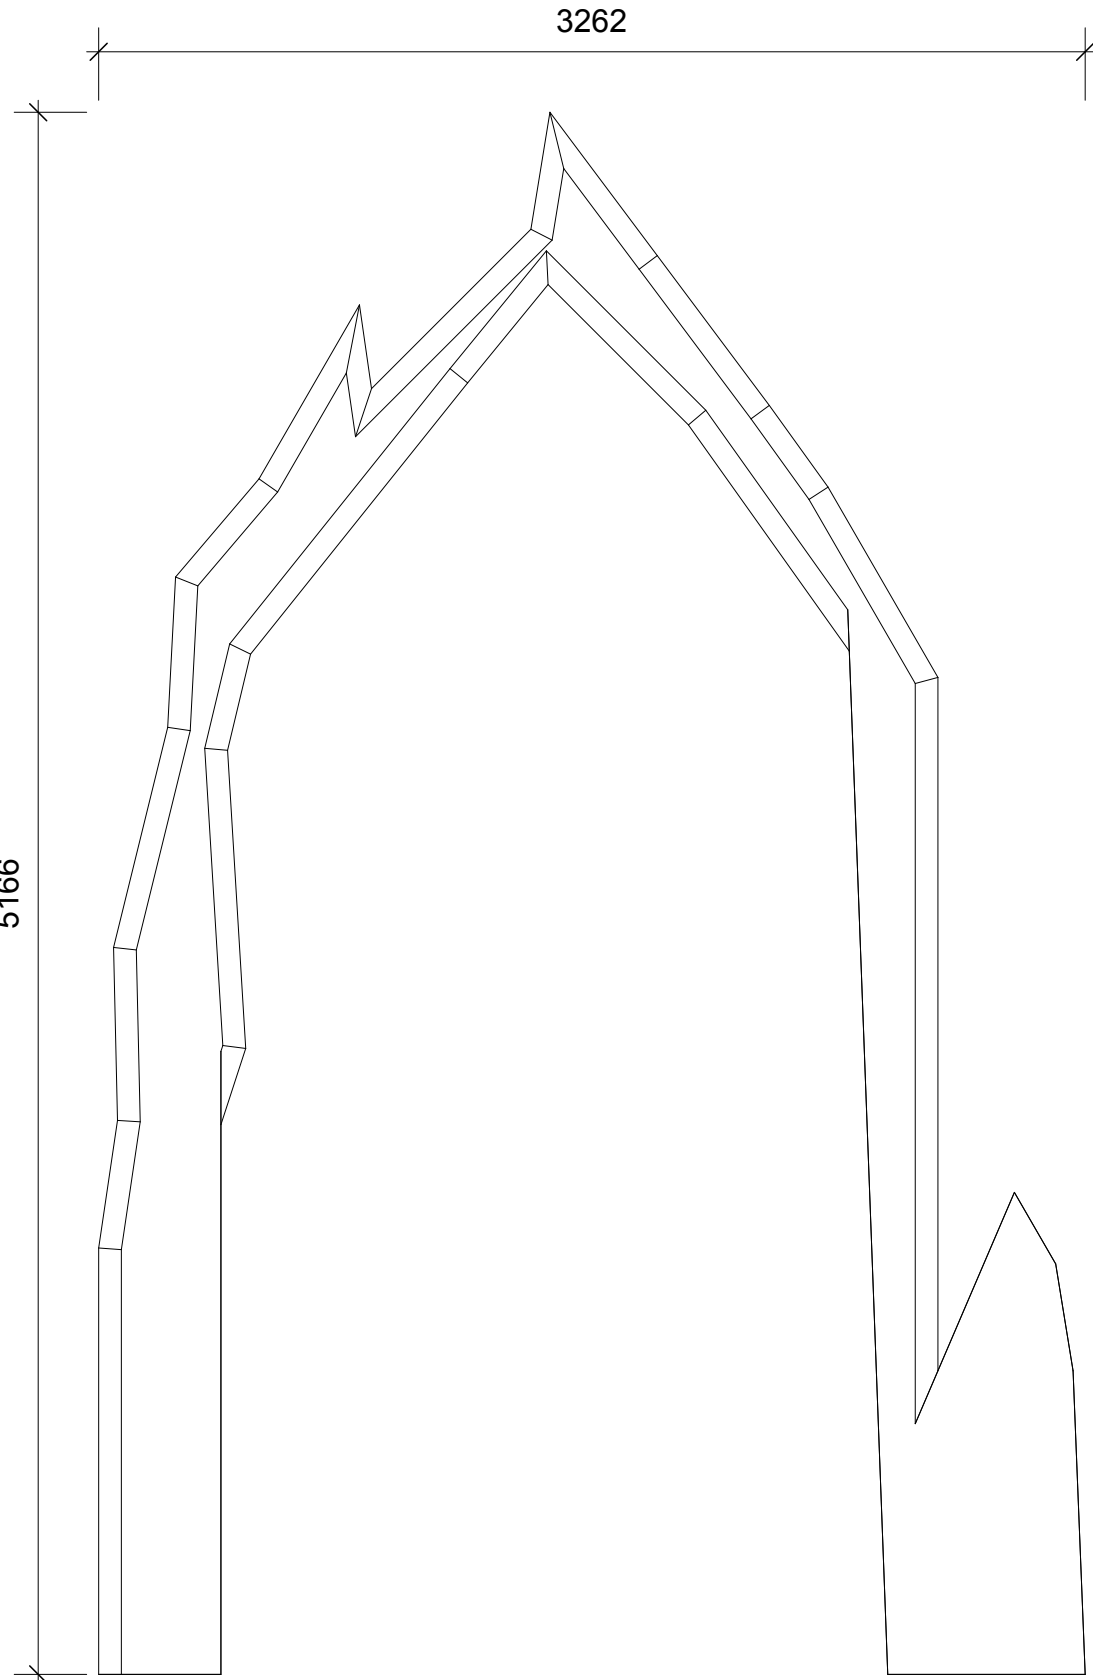


02 Ice Palace Layer 2
Scale 1:25

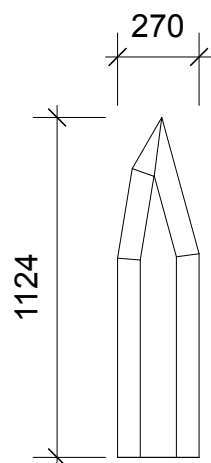

03 Ice Palace Layer 3
Scale 1:25

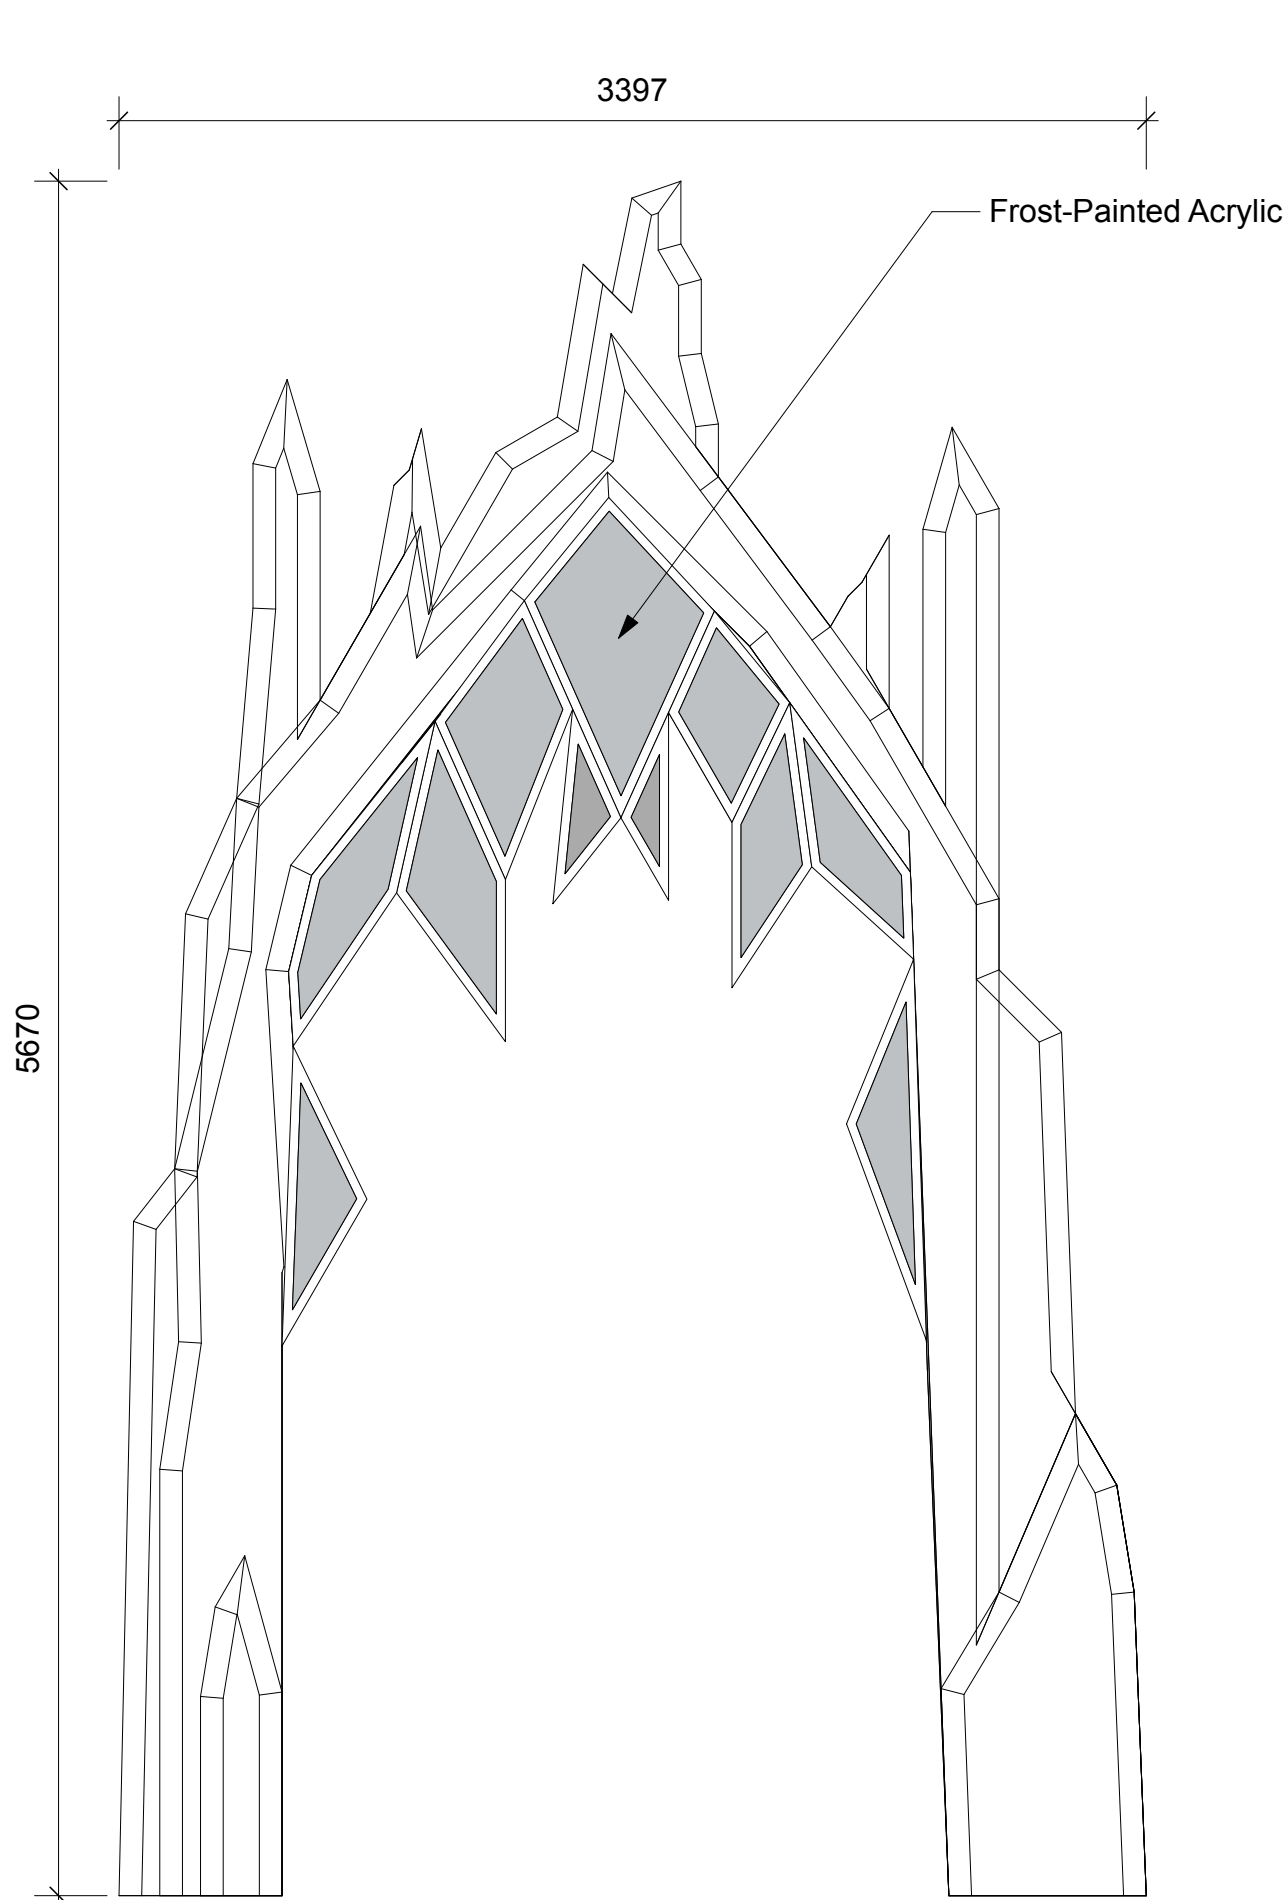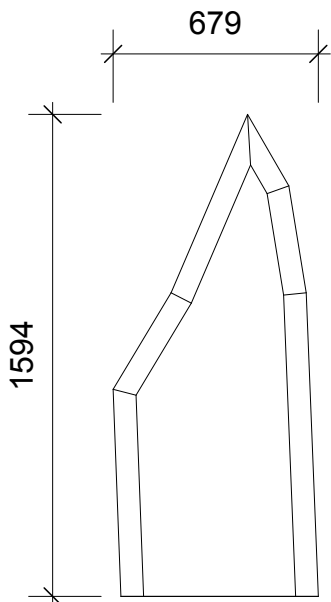

04 Ice Palace Front
Scale 1:25

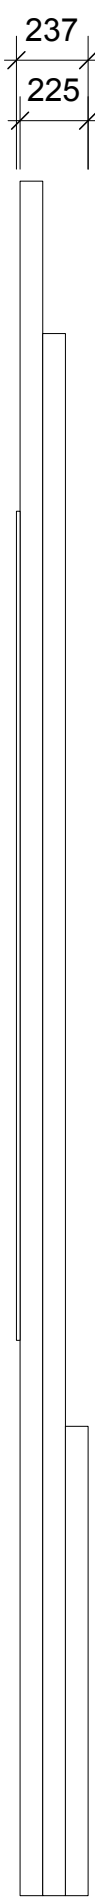


04 Ice Palace Front
Scale 1:25

Elsa's Ice Palace is made of 3x layers of 75mm thick material.


Layer thickness can change based on materials used.

Ice Stained Glass should have a more organic feel than as drawn.


Frozen	
CentreStage	
Civic Theatre Newcastle	
Elsa Ice Palace Centre Detail	
1:25 @ A1	12/06/2026
08 of 26	
8.0	

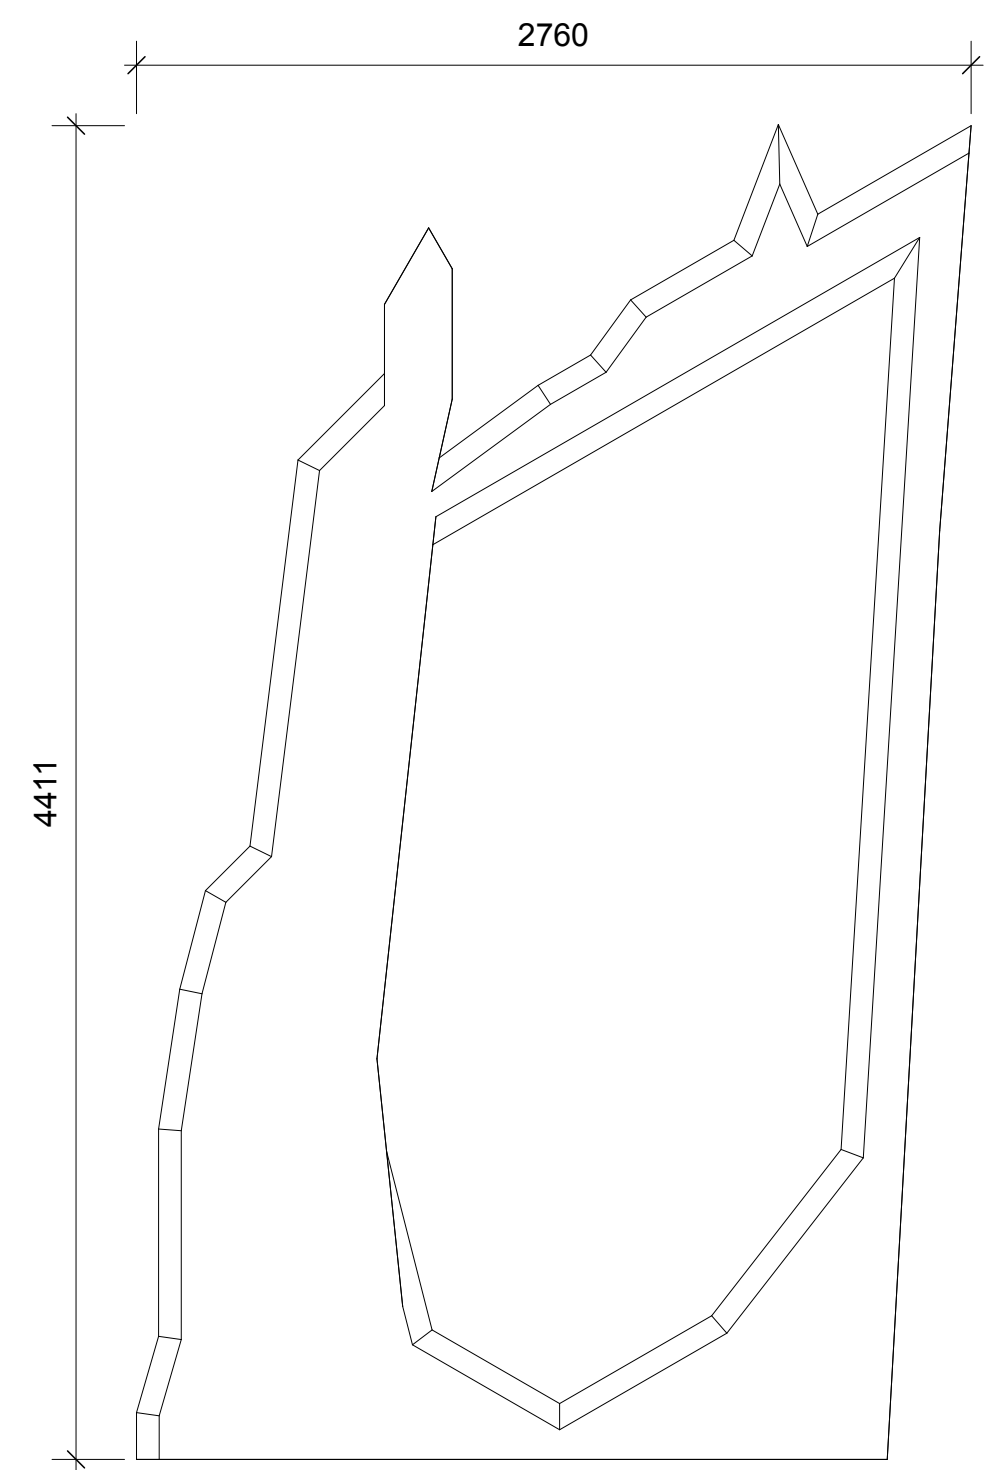


01 Ice Palace OP Layer 1
Scale 1:25

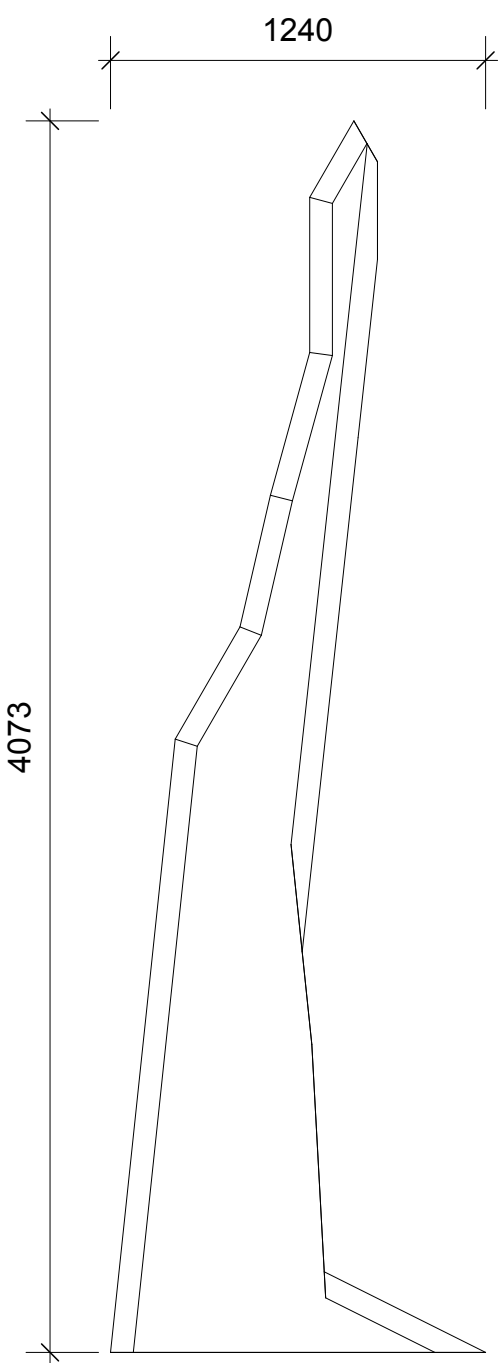


02 Ice Palace OP Layer 2
Scale 1:25

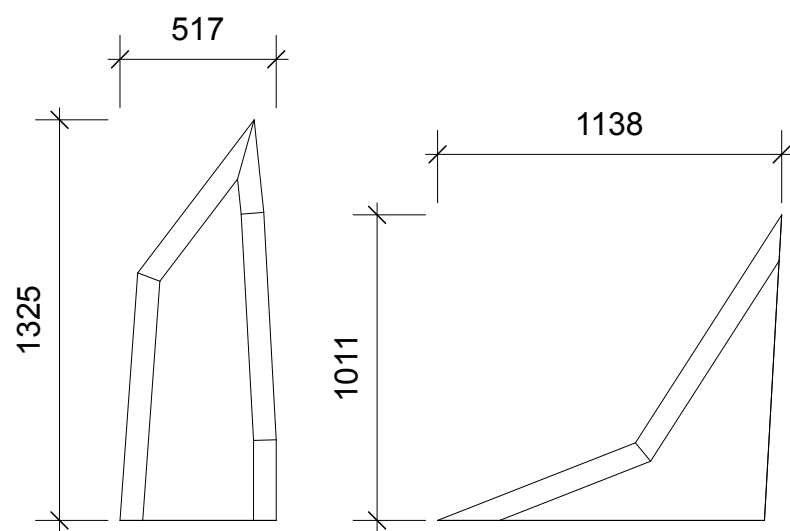


03 Ice Palace OP Layer 3
Scale 1:25

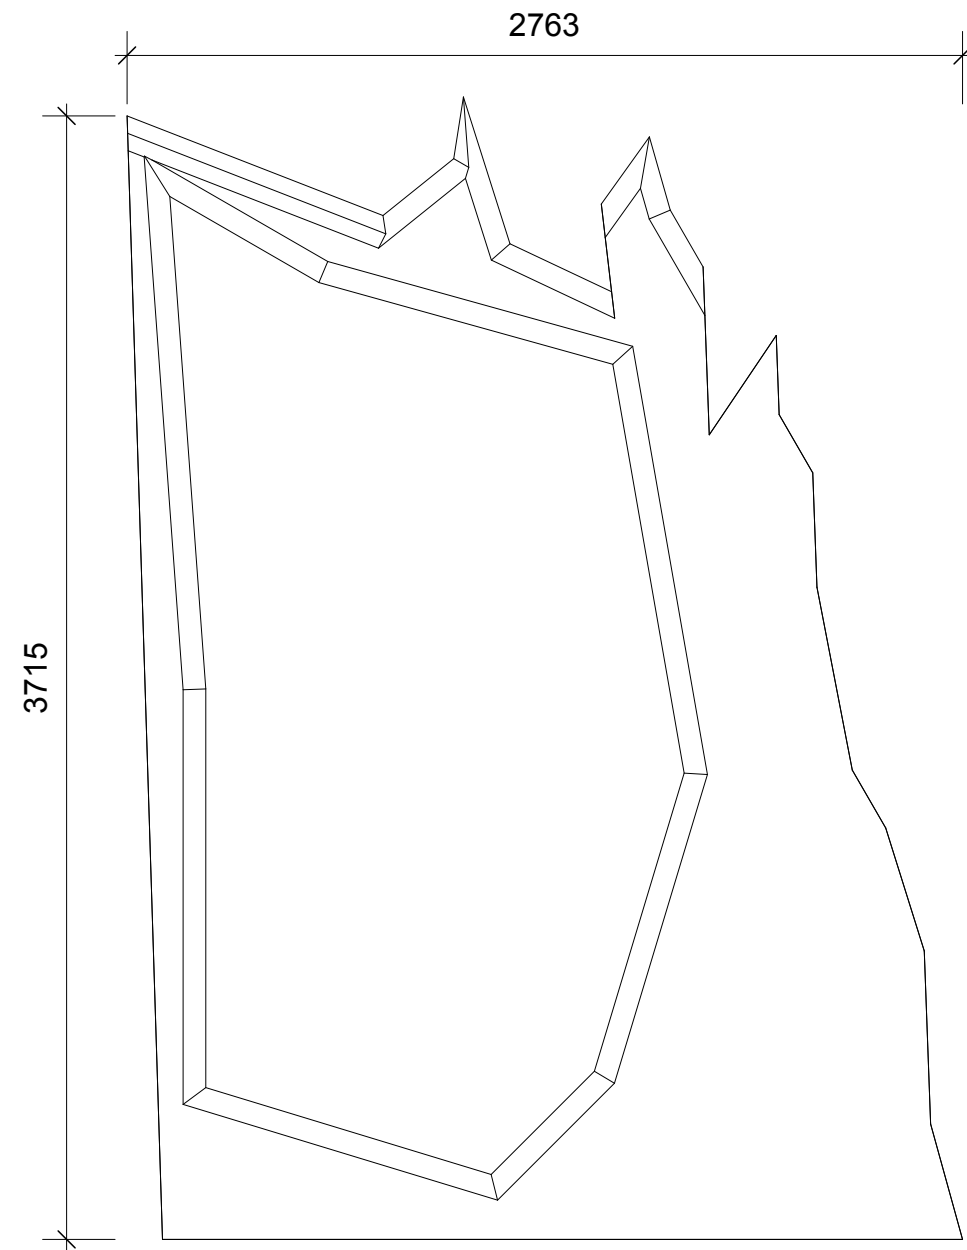


06 Ice Palace PS Layer 1
Scale 1:25

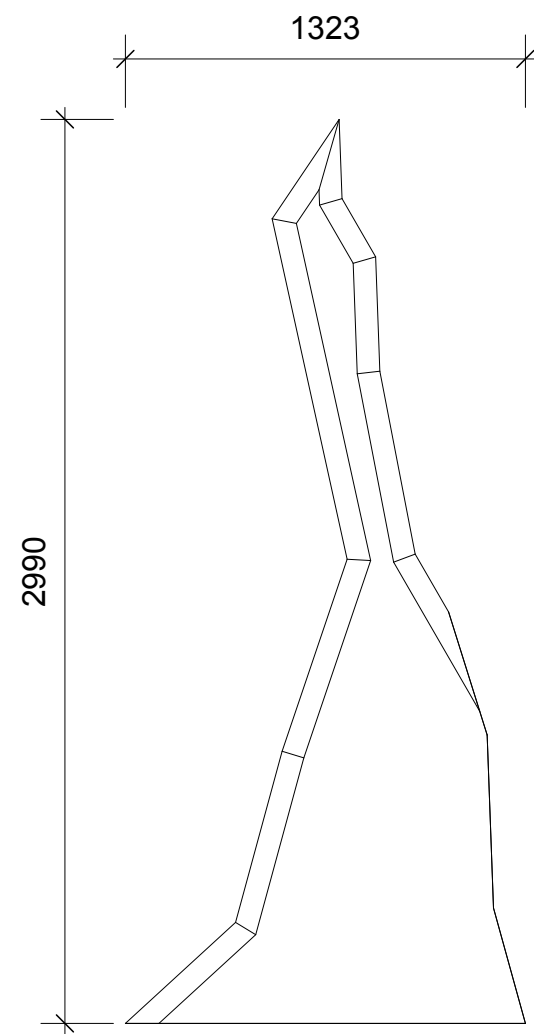


07 Ice Palace PS Layer 2
Scale 1:25

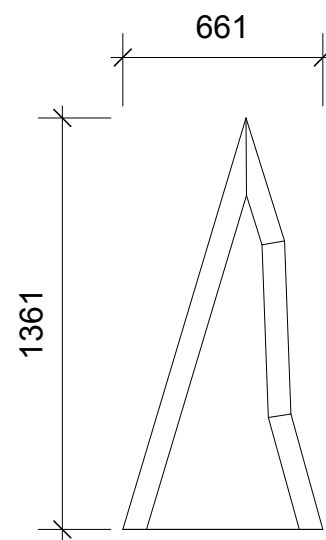


08 Ice Palace PS Layer 3
Scale 1:25

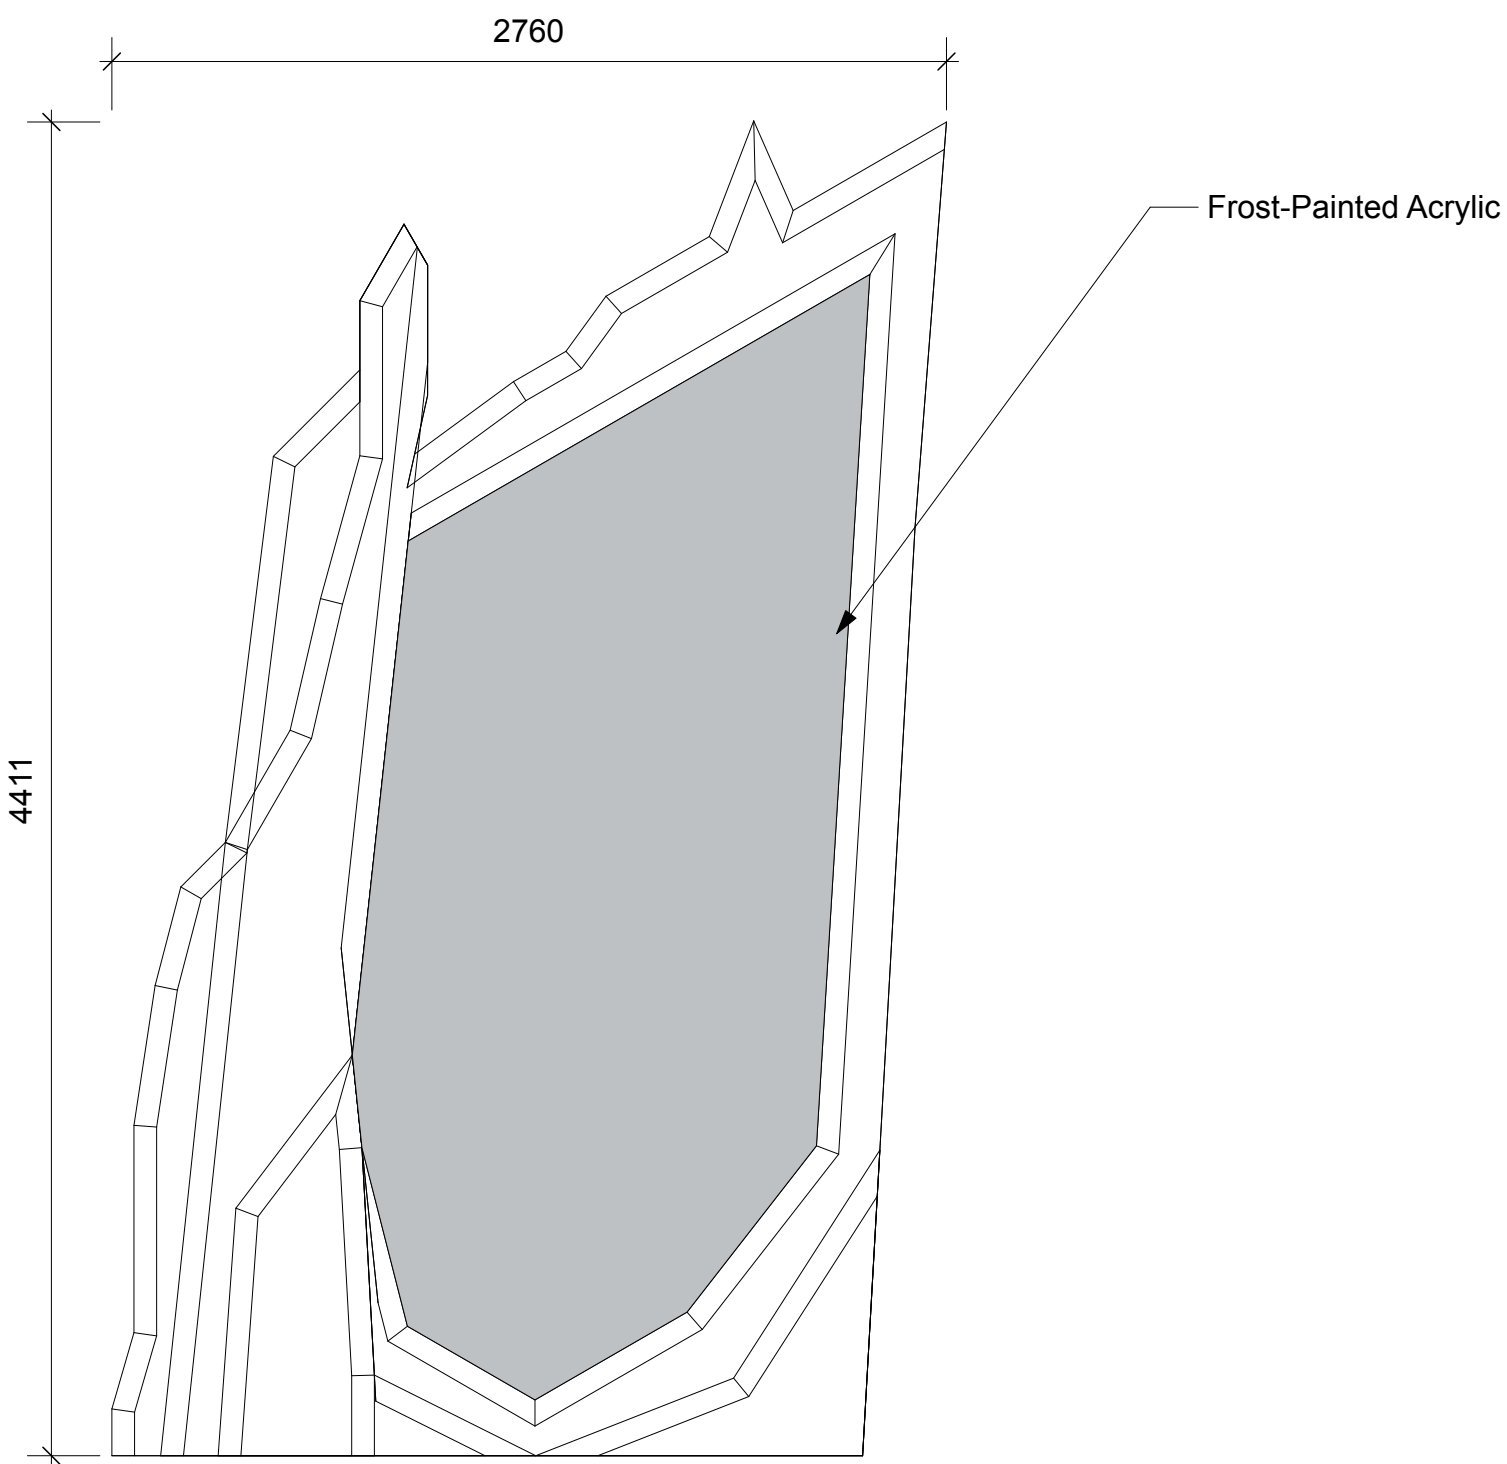


04 Ice Palace OP Front
Scale 1:25

 

05 Ice Palace OP Side
Scale 1:25

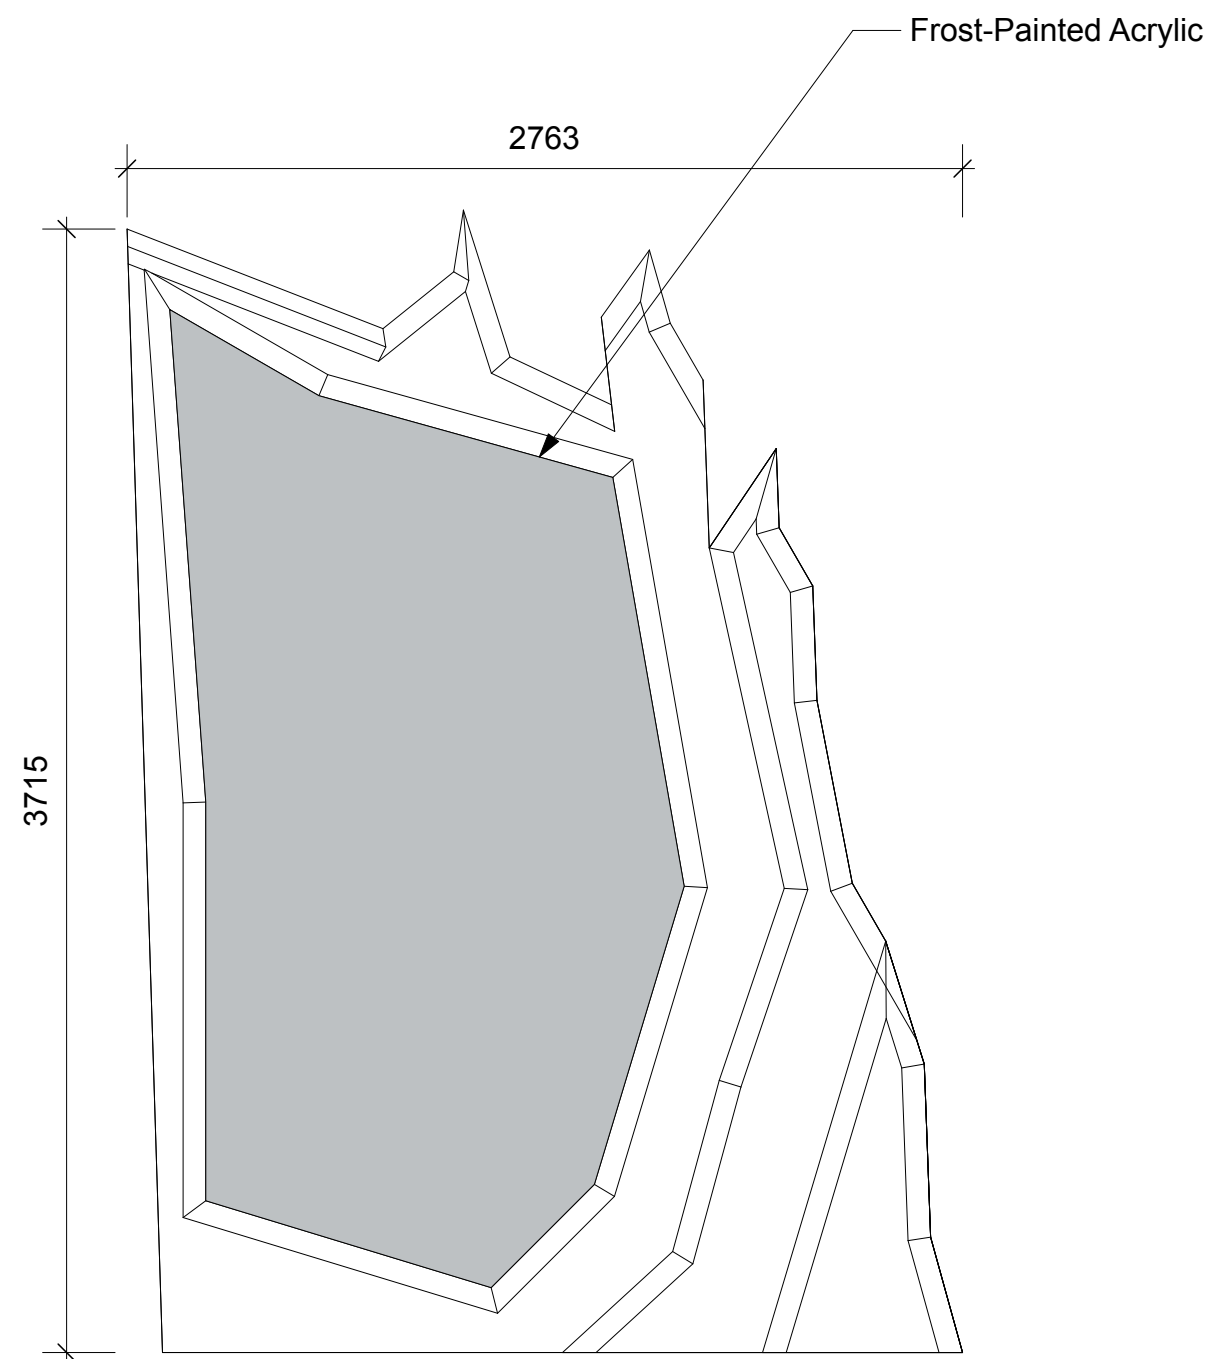

09 Ice Palace PS Front
Scale 1:25

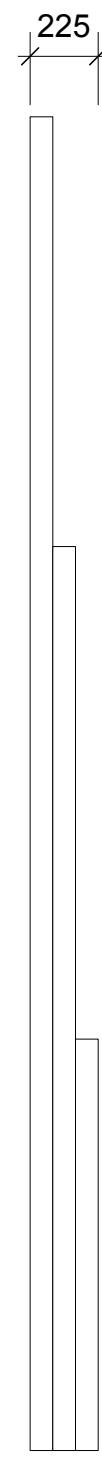


10 Ice Palace PS Side
Scale 1:25


Elsa's Ice Palace is made of 3x layers of 75mm thick material.

Layer thickness can change based on materials used.


Frozen	
CentreStage	
Civic Theatre Newcastle	
Elsa Ice Palace Sides Detail	
DATE:	12/07/2026
BY:	12/07/2026
FOR:	12/07/2026
1:25 @ A1	12/07/2026
09 of 26	
8.0	

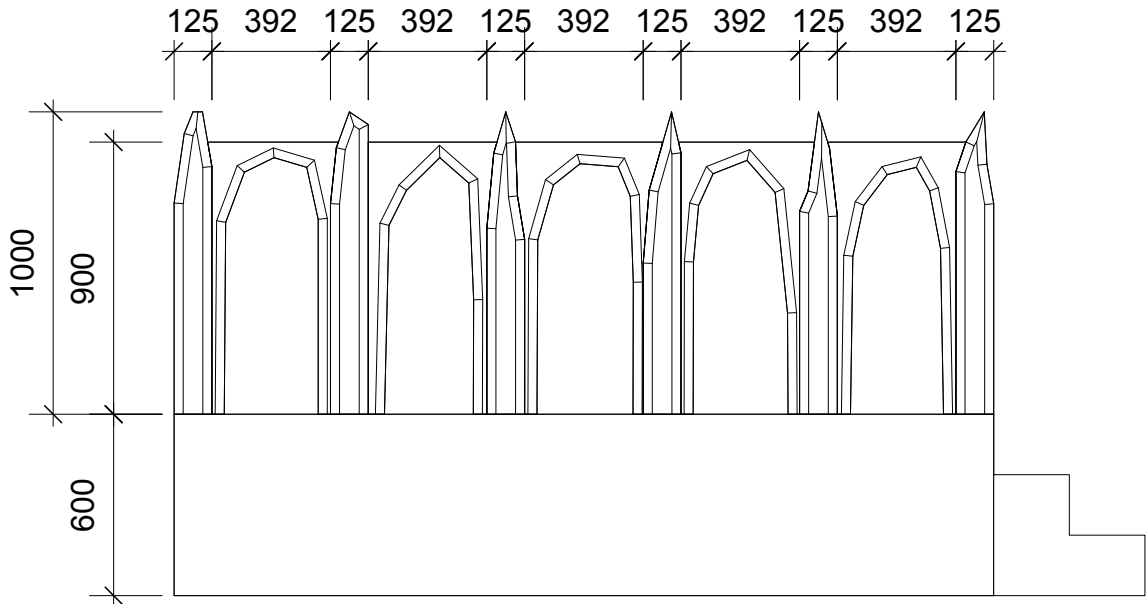


02 Staircase Piece 2 Front
Scale 1:25

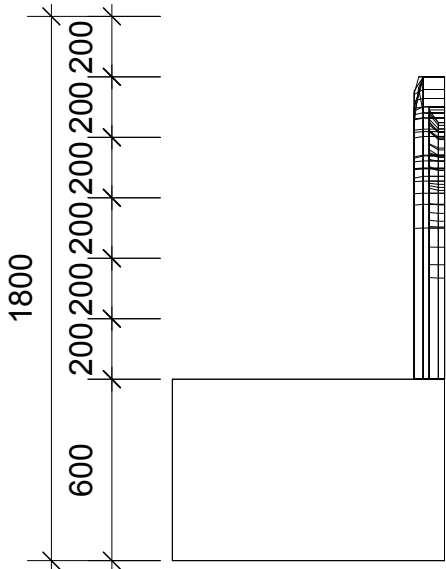


06 Staircase Piece 2 Side
Scale 1:25

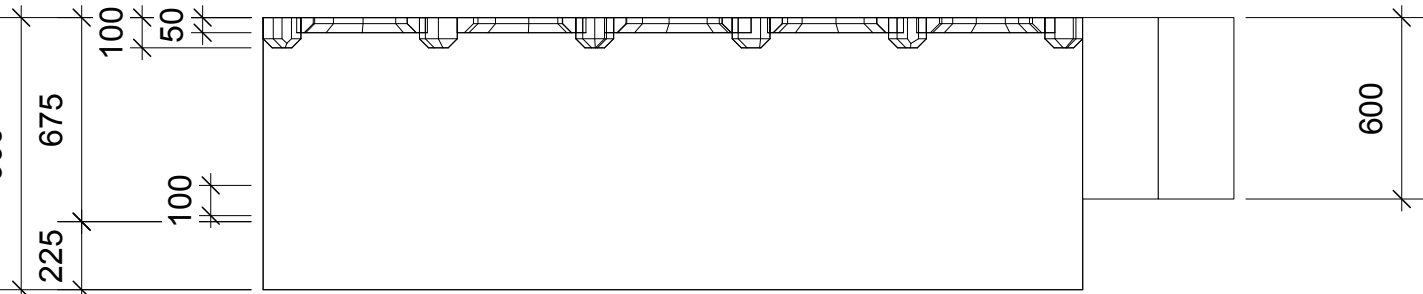


04 Staircase Piece 2 Top
Scale 1:25

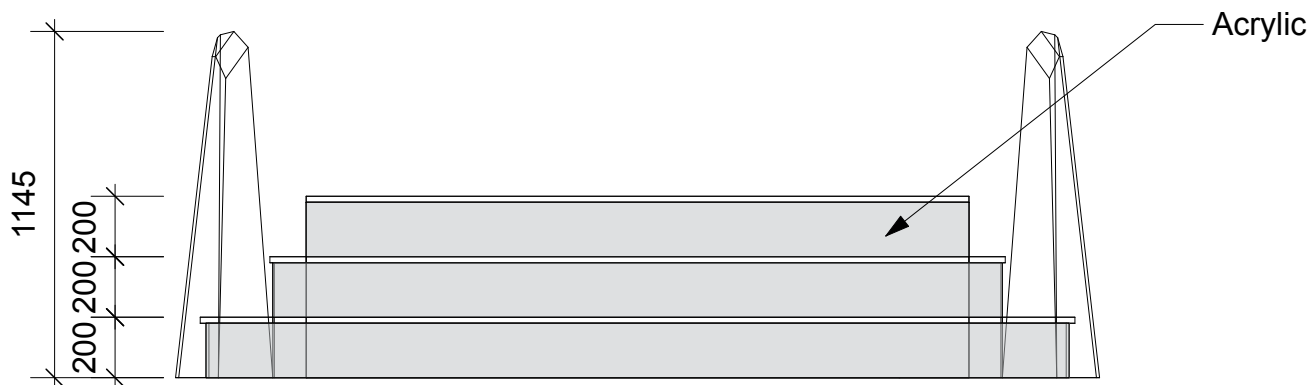


02 Staircase Piece 1 Front
Scale 1:25

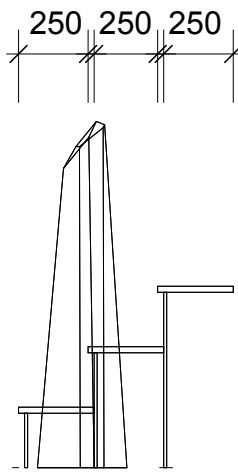

03 Staircase Piece 1 Side
Scale 1:25

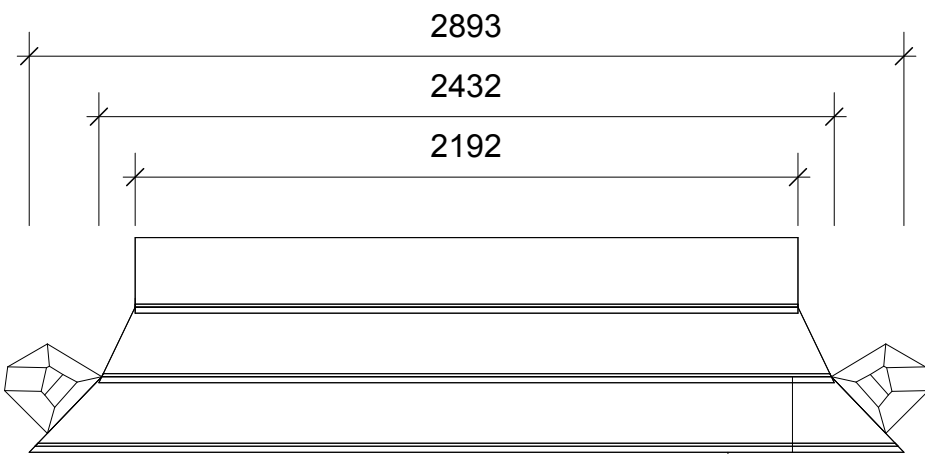

01 Staircase Piece 1 Top
Scale 1:25

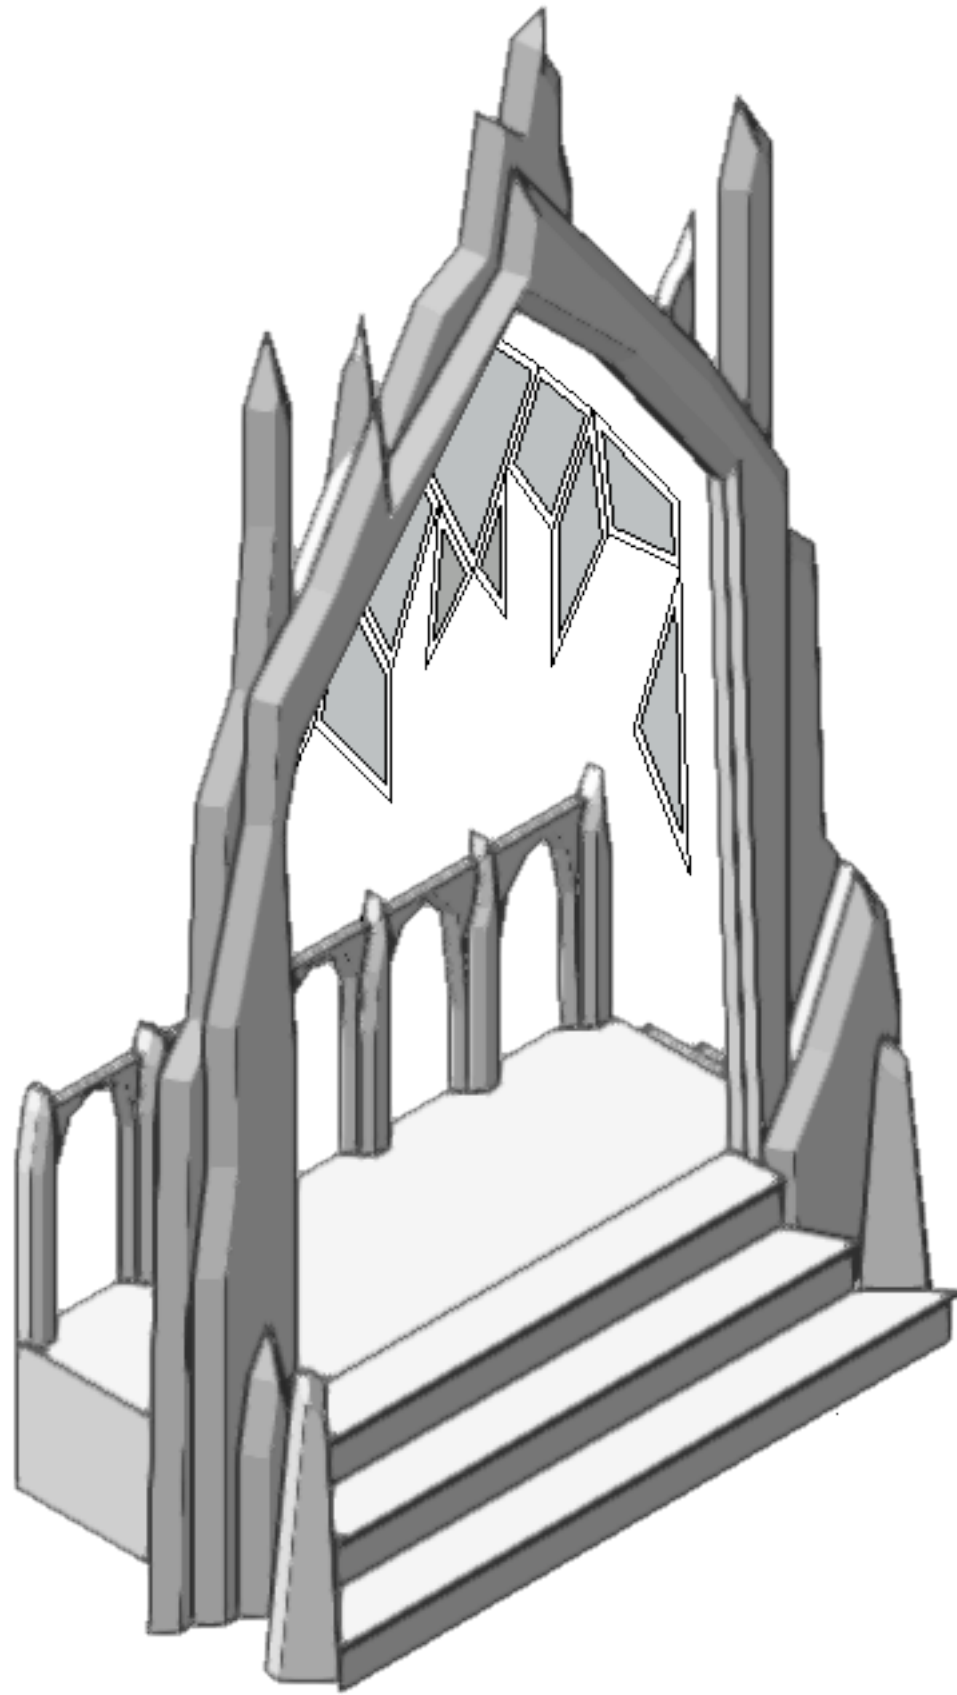


Staircase in 2 pieces.


Escape stairs required for off-stage exit/entrance.

Pieces trucked on


Frozen	
FOURWAY:	
CentreStage	
PROJECT:	
Civic Theatre Newcastle	
TITLE:	
Elsa Ice Palace Staircase Detail	
DIRECTOR:	
Mallory Trew-McGowan	
ART DESIGNER:	
Harry Gill	
LIGHTING DESIGNER:	
Zach Kruse	
SCALE:	
1:25 @ A1	
DATE:	
12/07/2026	
DRAWING NUMBER:	
10 of 26	
DESIGNED & DRAWN BY:	
CONTRACT:	
Harry Gill	
VERSION:	
3.0	

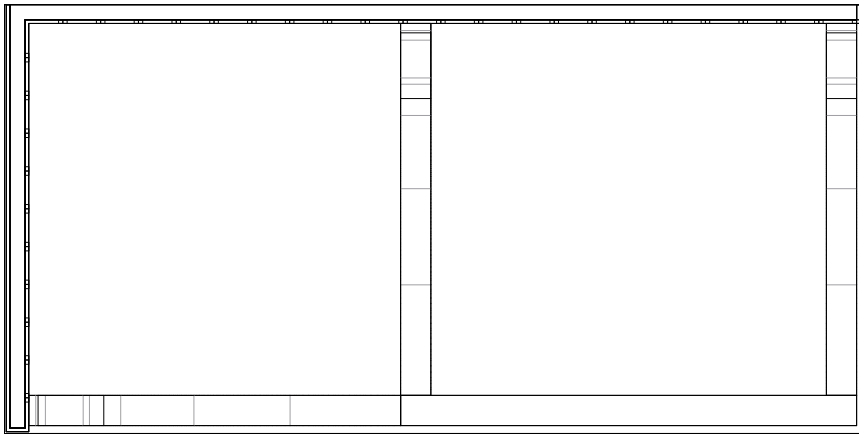


04 Bedrom Top
Scale 1:25

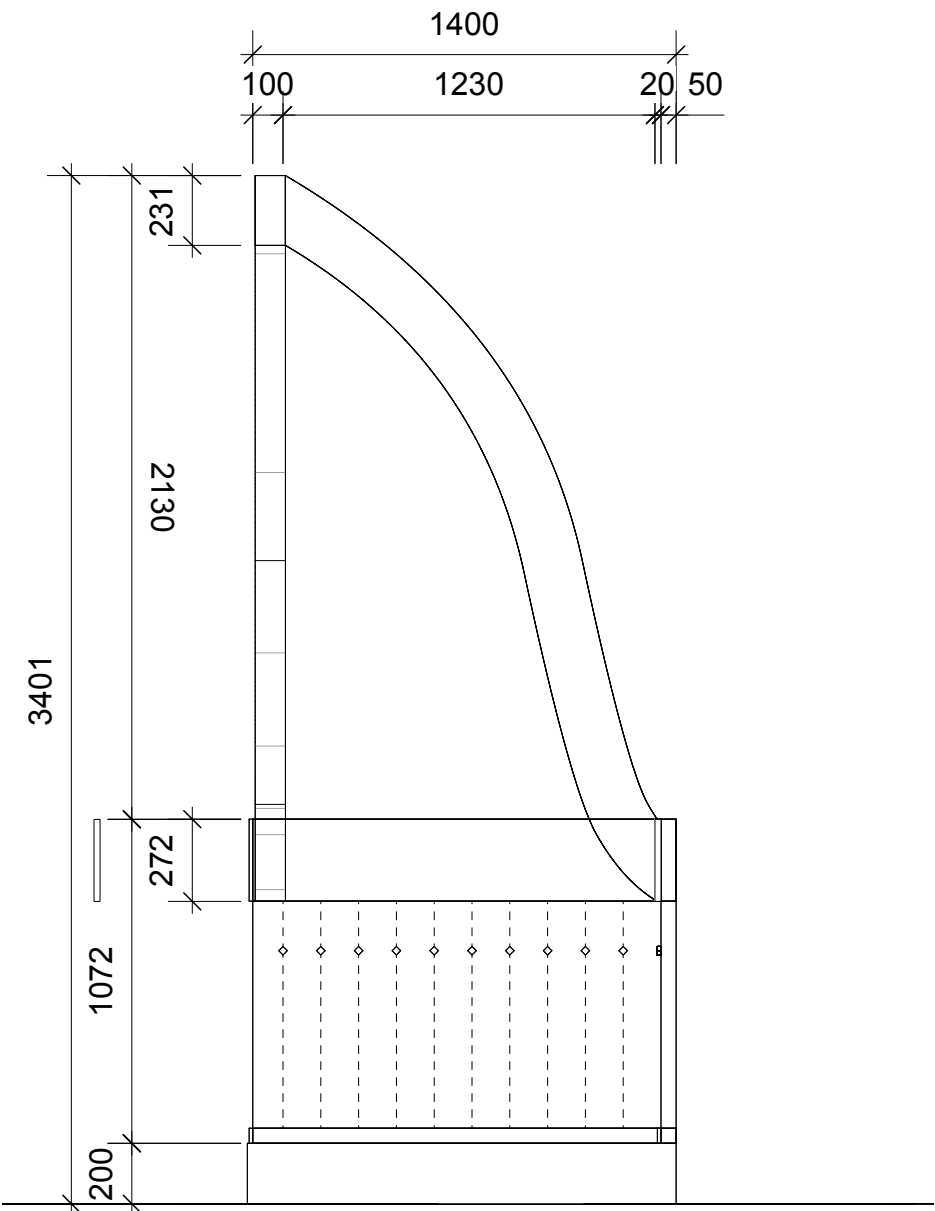

02 Bedrom Side (Internal)
Scale 1:25

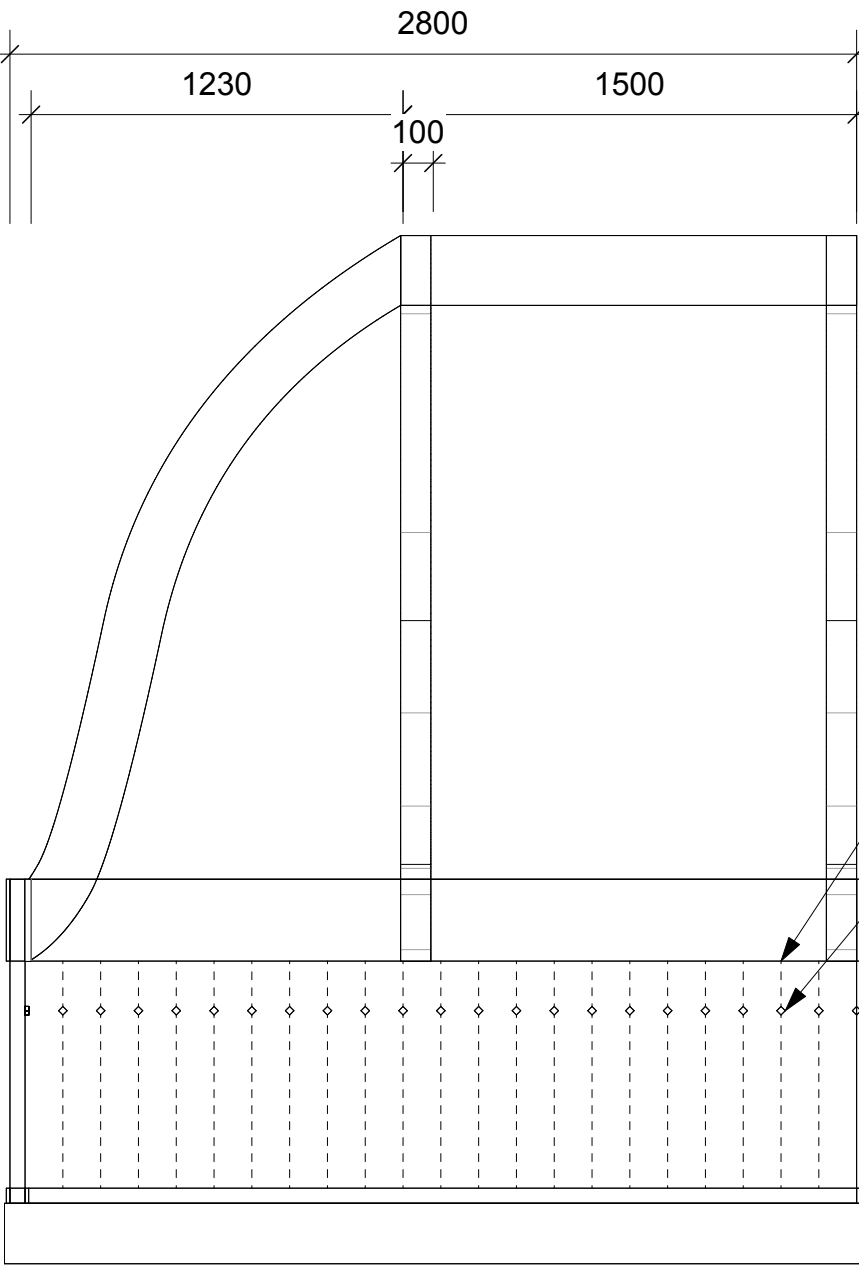

01 Bedrom Front
Scale 1:25

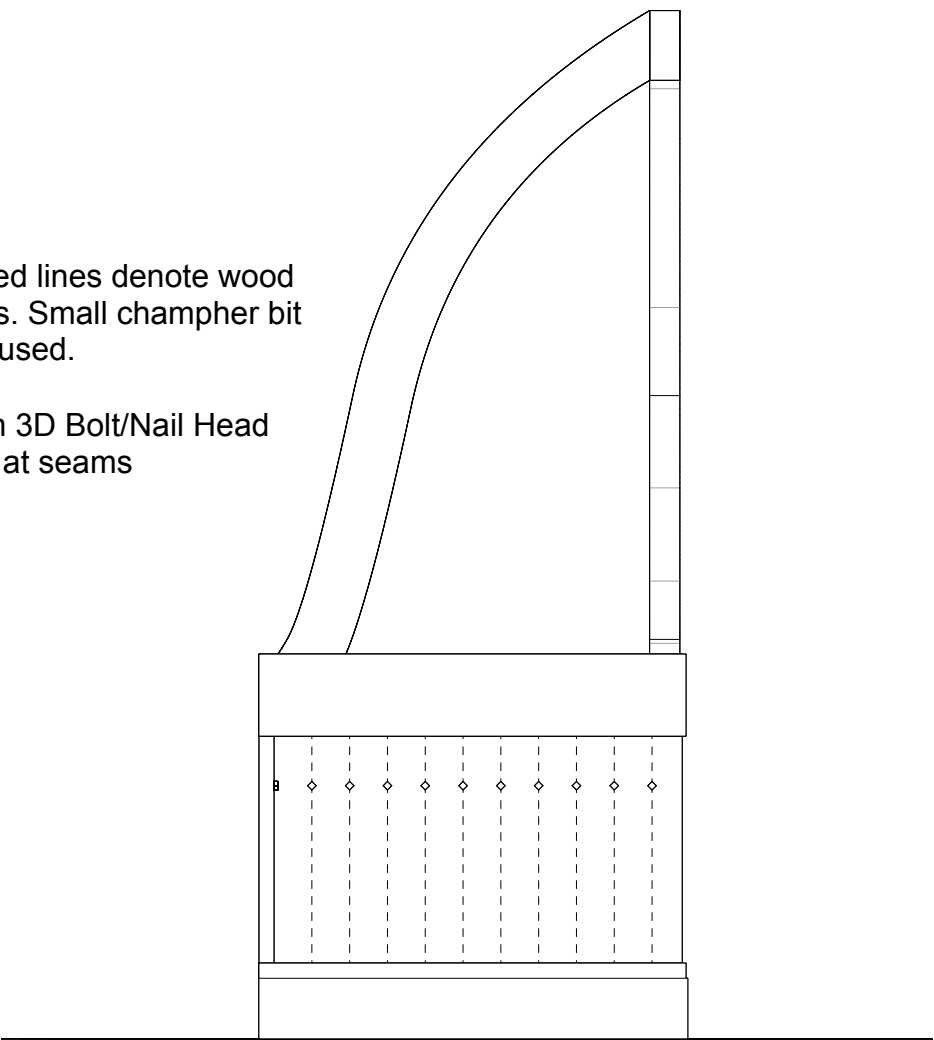

03 Bedrom Side (External)
Scale 1:25

Dashed lines denote wood planks. Small chamfer bit to be used.


12mm 3D Bolt/Nail Head detail at seams

x2 Bed Trucks Mirrored

50mm wall thickness allowed.

Both inside and outside of side wall to be finished, as will be seen as truck moves across stage.

Frozen	
DRAWN BY:	CentreStage
PROJECT:	Civic Theatre Newcastle
TITLE:	Bedroom Truck Detail
DIRECTOR:	Melissa Trew-Kayworth
SET DESIGNER:	Harry Gill
LIGHTING DESIGNER:	Zach Kraske
SCALE:	DATE:
1:25 @ A2	12/07/2026
DRAWING NUMBER:	
11 of 26	
DESIGNED & DRAWN BY:	CONTACT:
Harry Gill	harry@newstage.com
VERSION:	DATE: 12/07/2026
3.0	

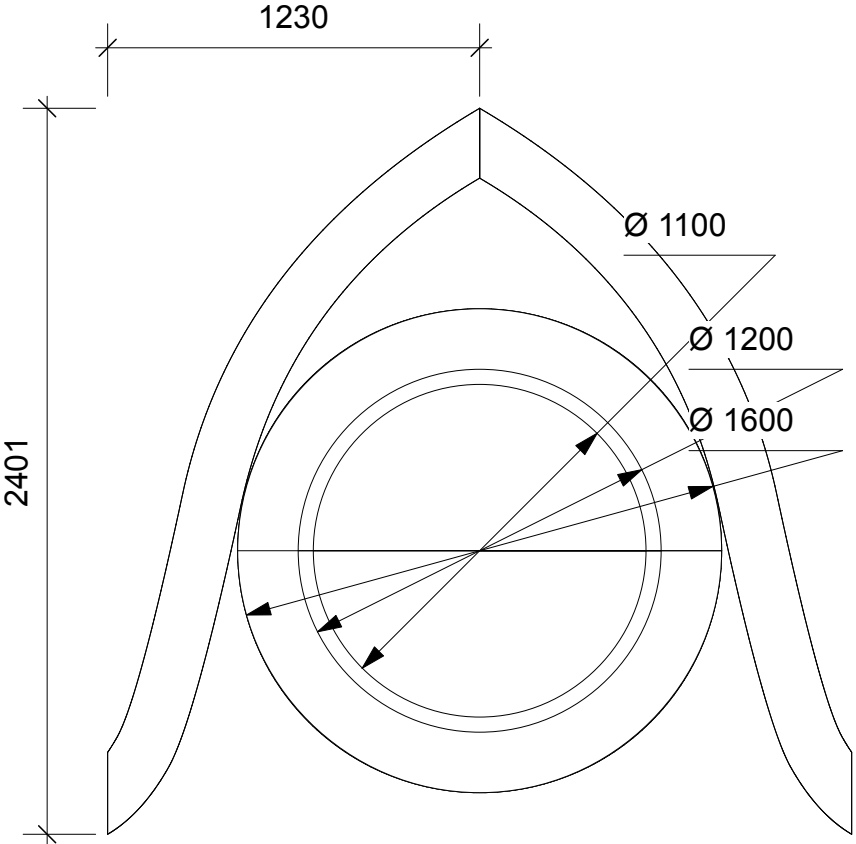

01

Bedrom Window Front

Scale 1:25



02

Bedrom Window Side

Scale 1:25

Frozen

COMPANY:
CentreStage

VENUE:
Civic Theatre Newcastle

TITLE:
Bedroom Window

DIRECTOR: Madison Thew-Keyworth

SET DESIGNER: Harry Gill

LIGHTING DESIGNER: Zach Krause

SCALE: 1:25 @ A3
DATE: 12/07/2026



DRAWING NUMBER:

12 of 26


DESIGNED & DRAWN BY: CONTACT:

Harry Gill
VERSION: 031.002.47
3.0

harry@harrygilldesigns.com

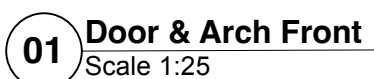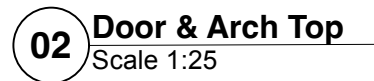


- Door In Door

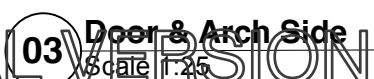


x2 of both pieces mirrored.

Frozen	
PROJECT CentreStage	
NAME Civic Theatre Newcastle	
TITLE Door & Arch Detail	
DRAWN BY Mellissa Vasey-Watson	CHECKED BY Henry Giff
DATE June 2006	SCALE 1:25 @ A2
DRAWING NUMBER: 13 of 26	
DESIGNED & DRAWN BY	CHECKED
www.creativeplanning.com Unit 102 4/17	

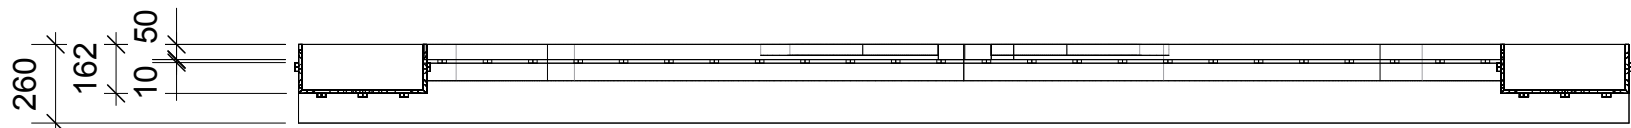


02 Chapel Wall Top
Scale 1:25

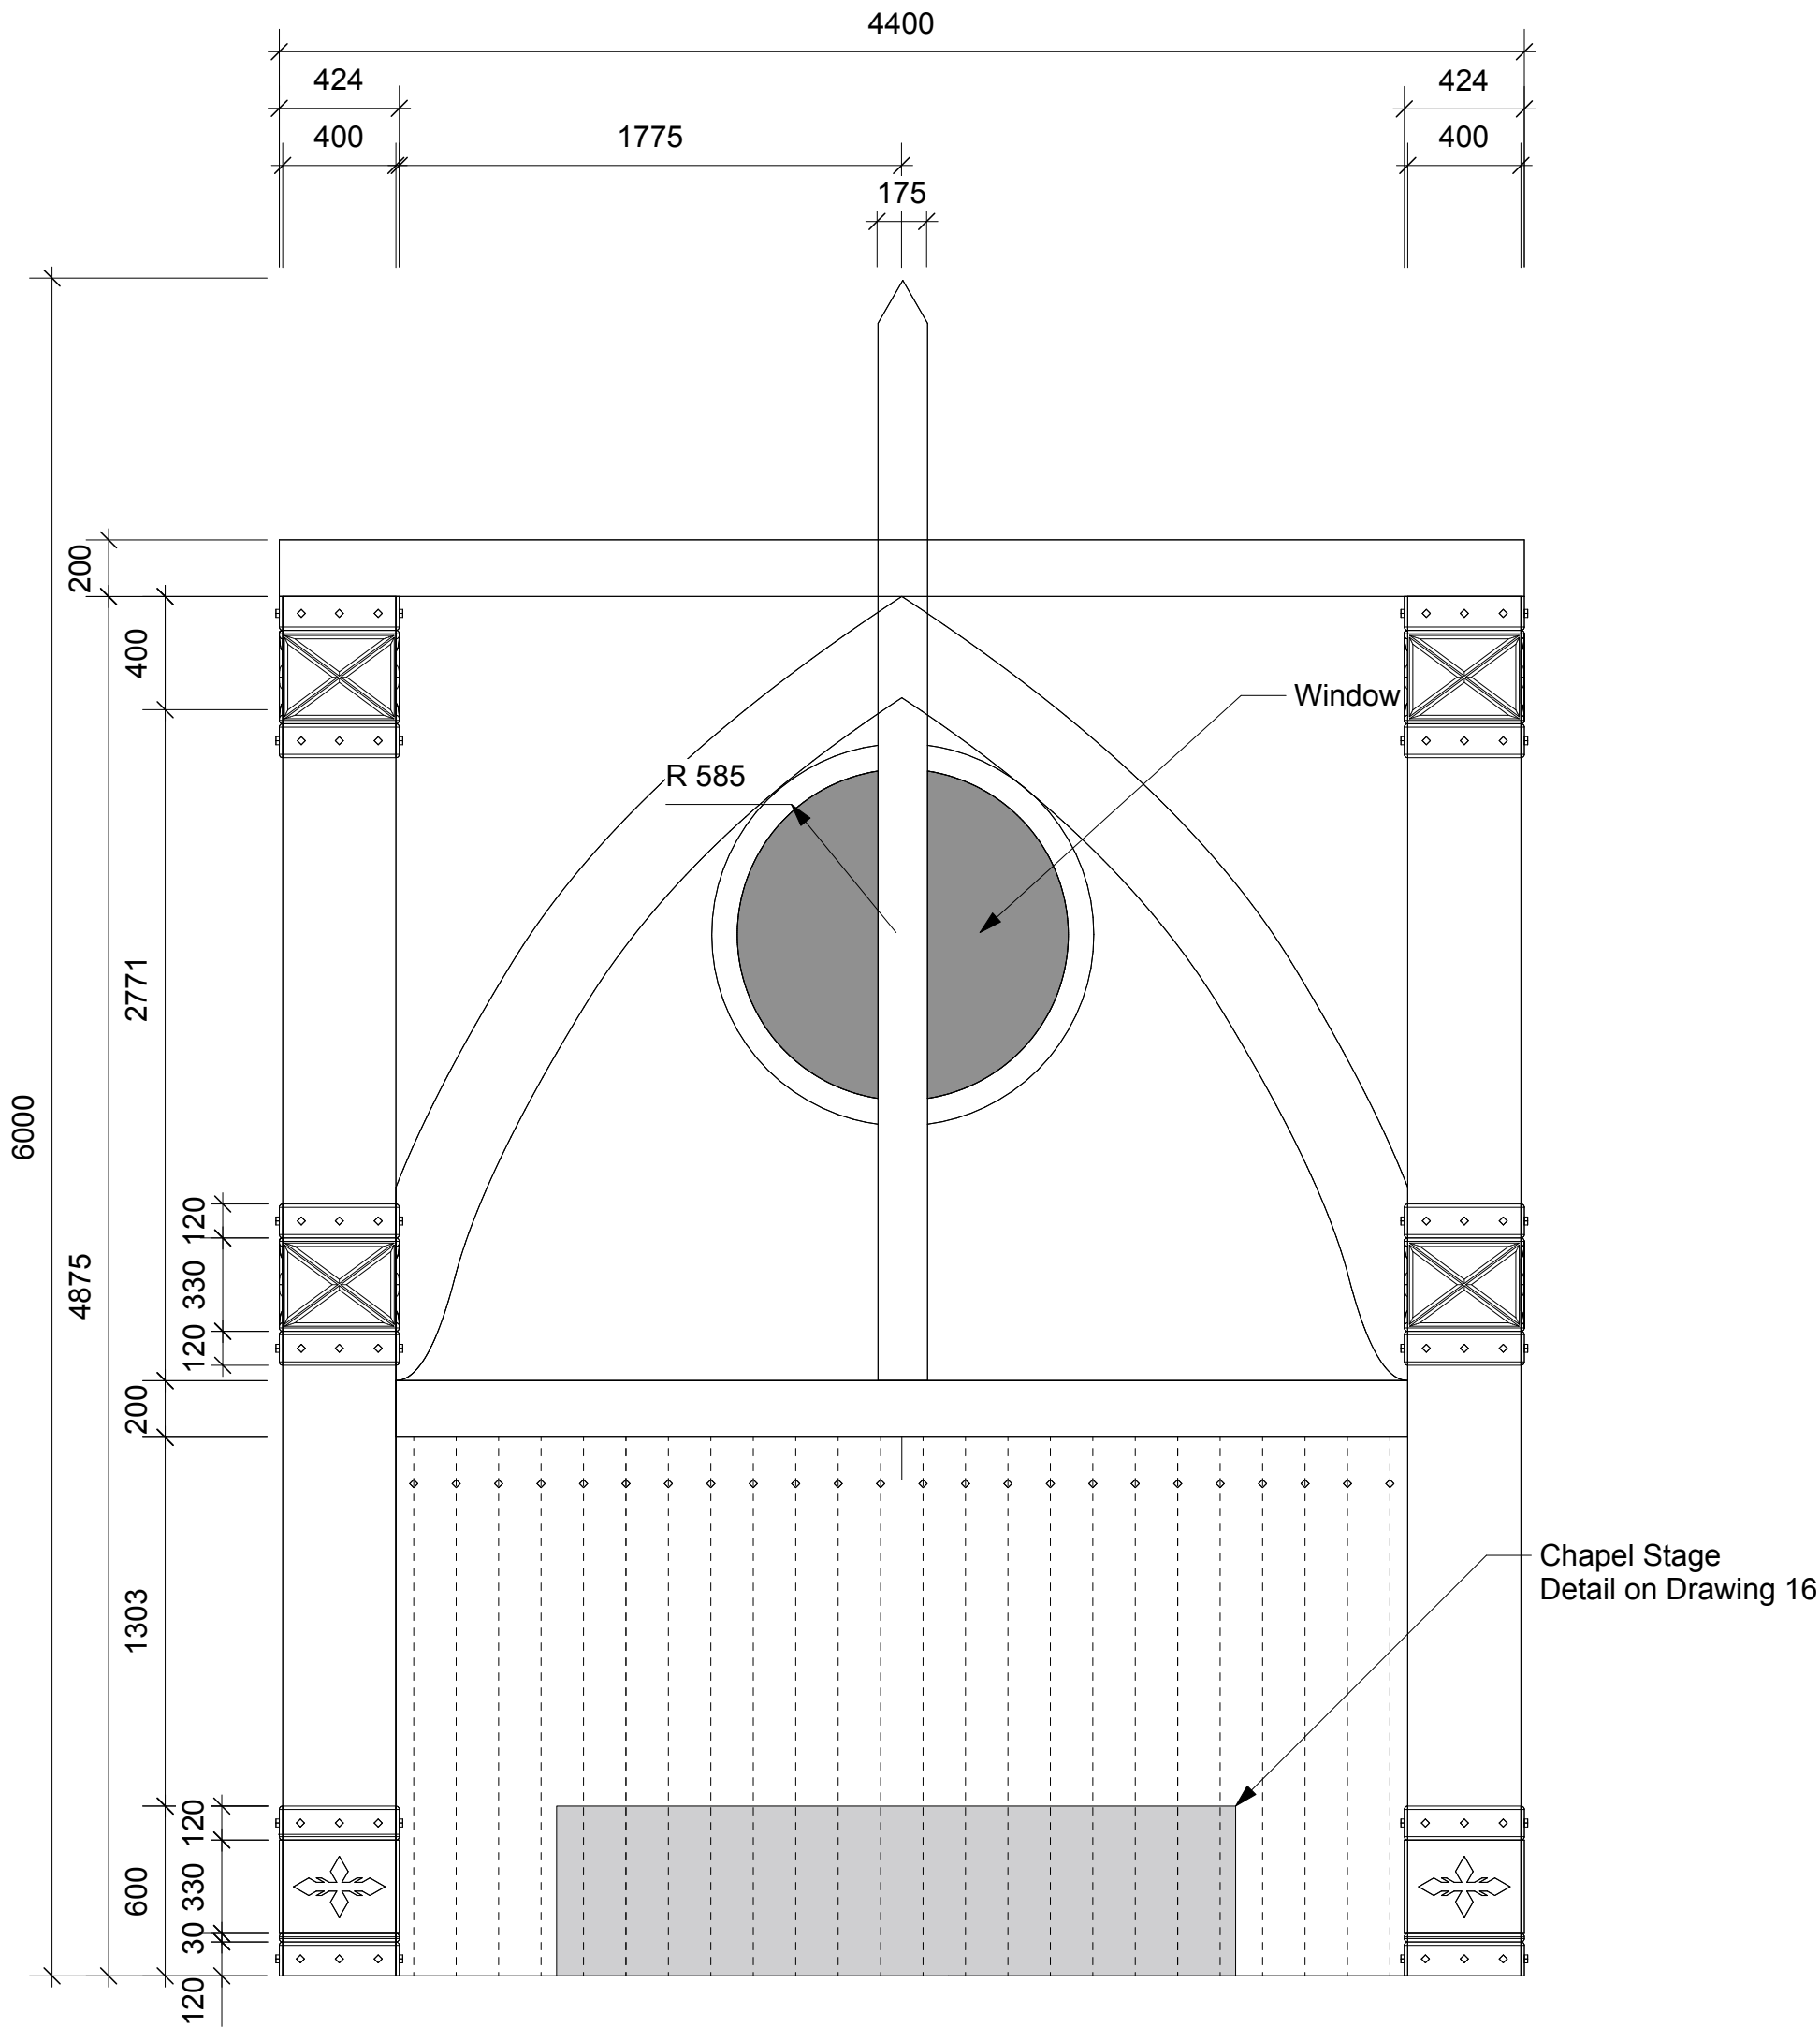

01 Chapel Wall Front
Scale 1:25




02 Chapel Wall Side
Scale 1:25

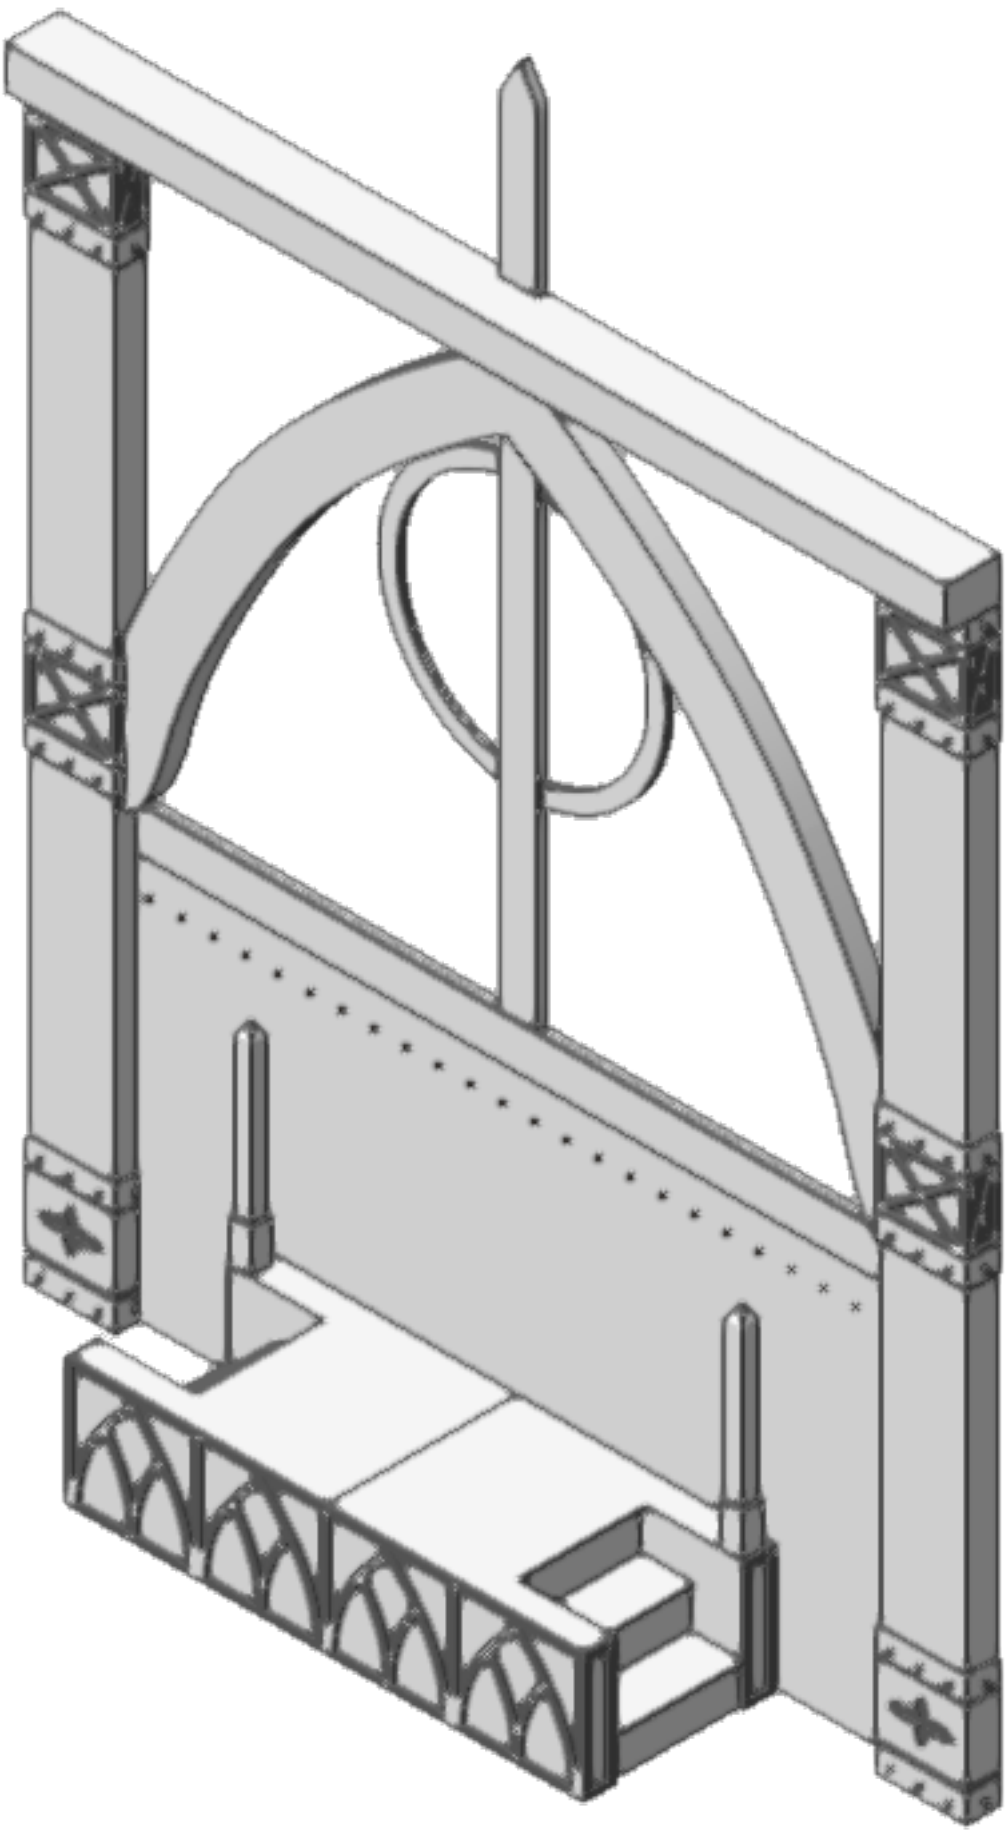


Chapel Wall flies in.

Frozen	
CentreStage	
Civic Theatre Newcastle	
Chapel Wall Detail	
DIRECTOR	Markus Tress-Kayser
SET DESIGNER	Harry Gill
LIGHTING DESIGNER	Jack Krieger
SCALE	DATE
1:25 @ A2	12/07/2026
DRAWING NUMBER:	
15 of 26	
DESIGNED & DRAWN BY	
CONTACT	
Harry Gill	
harry@harrygilldesigns.com	
3.0	

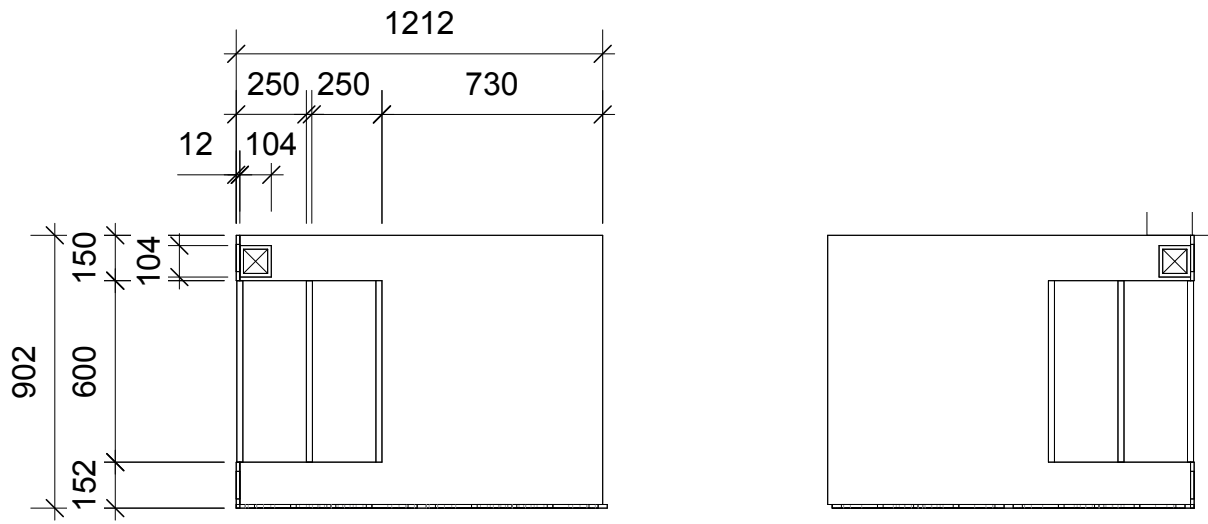


02 Chapel Stage Top
Scale 1:25

Front detail overlaps to
hide seam

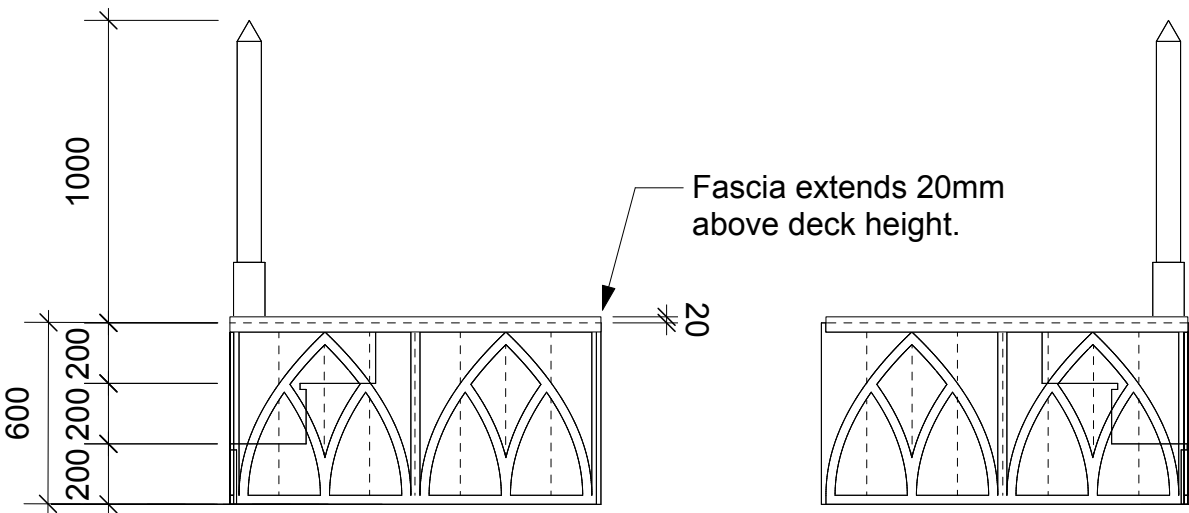

01 Chapel Stage Front
Scale 1:25

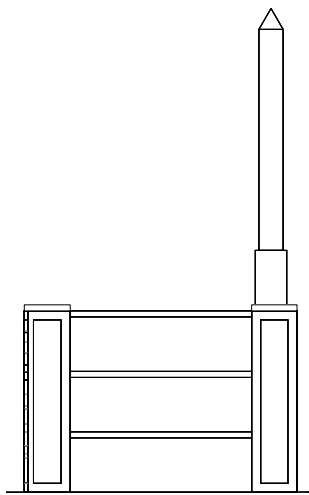

03 Chapel Stage Side
Scale 1:25

Stage trucks on on track in floor.

Inside face of trucks to have scenic finish.

Fascia extends 20mm above FFL to mask join
mechanism.

Stanchion should have enough structural
strength as is being pushed on by cast to
move truck.

Frozen

COMPANY:
CentreStage

VENUE:
Civic Theatre Newcastle

TITLE:
Chapel Stage Detail

DIRECTOR: Madison Trew-Keyworth

SET DESIGNER: Harry Gill

LIGHTING DESIGNER: Zach Krause

SCALE: 1:25 @ A3

DATE: 12/07/2026

DRAWING NUMBER:

16 of 26


DESIGNED & DRAWN BY:

CONTACT:

Harry Gill


VERSION: 0431 192 447

3.0

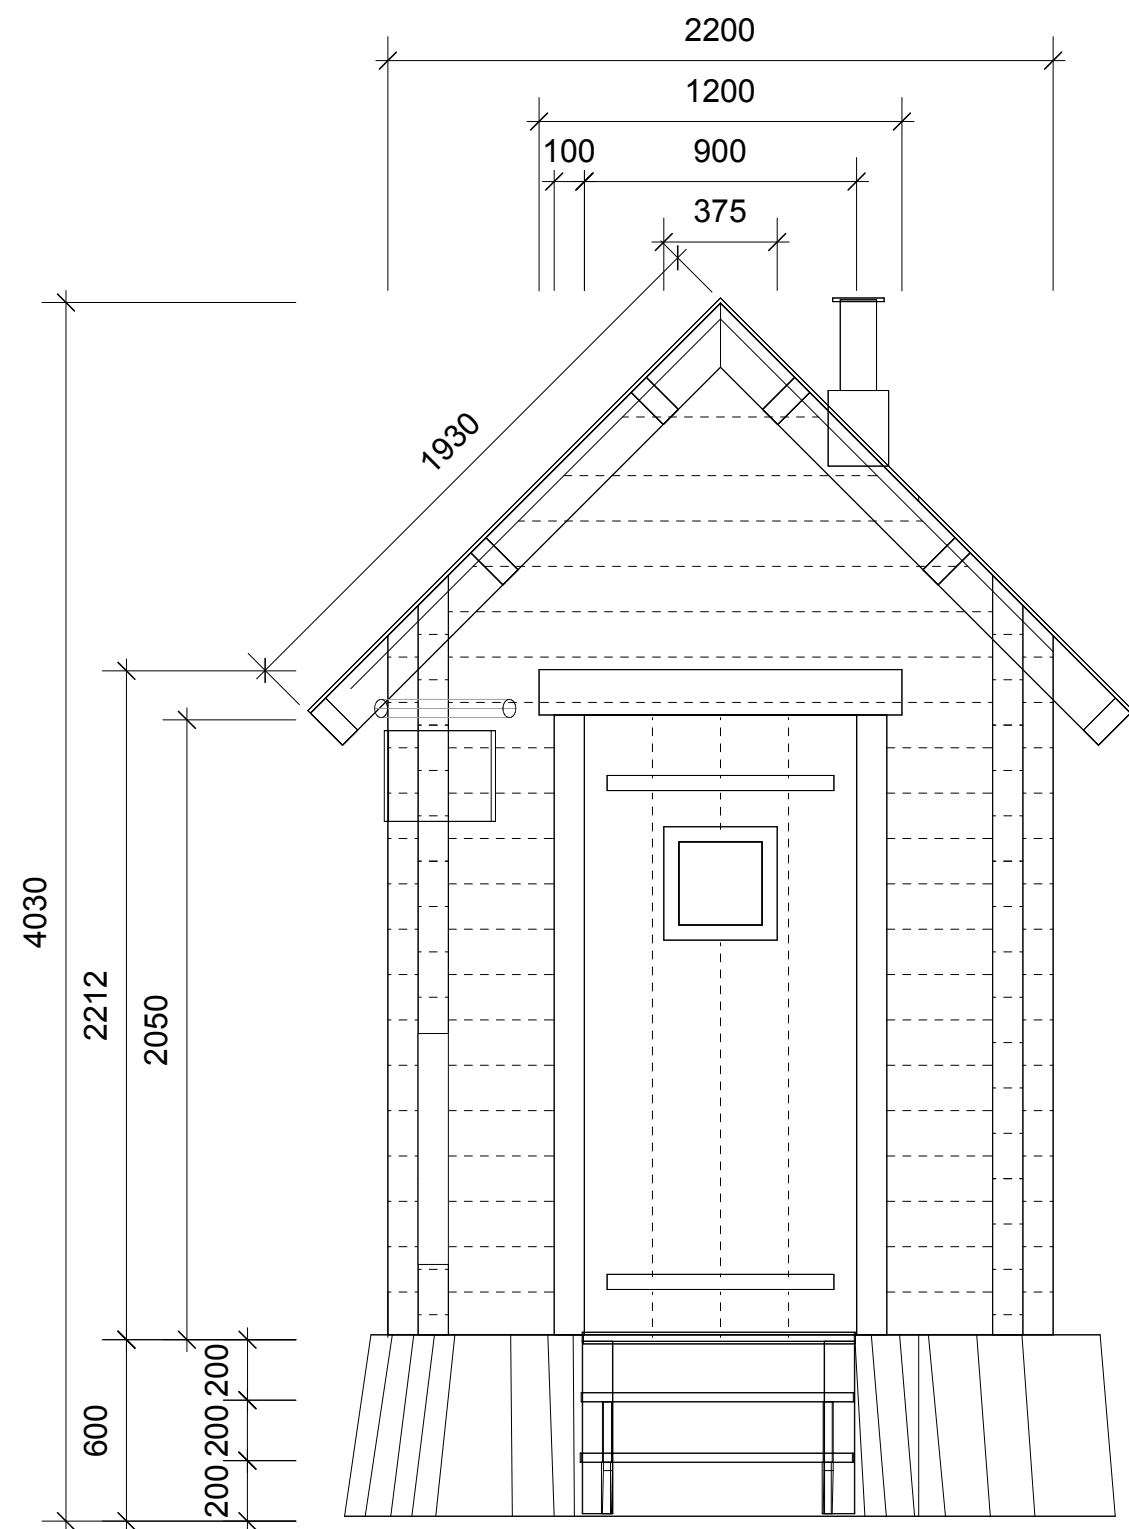


02 Oaken Sauna View 1
Scale 1:25

Dashed line denotes
seperate wooden planks.
This should look like
intersecting wooden at the
corners like a log cabin.
See model & scenic
elevation for futher detail

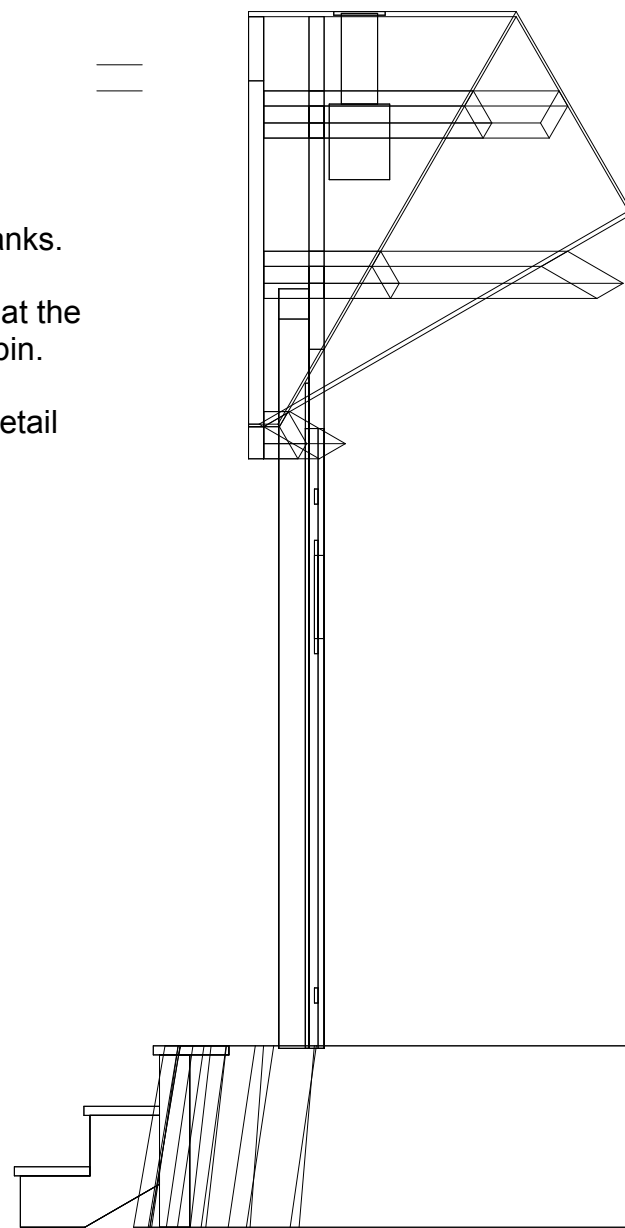

03 Oaken Sauna View 2
Scale 1:25

Hanging Sign

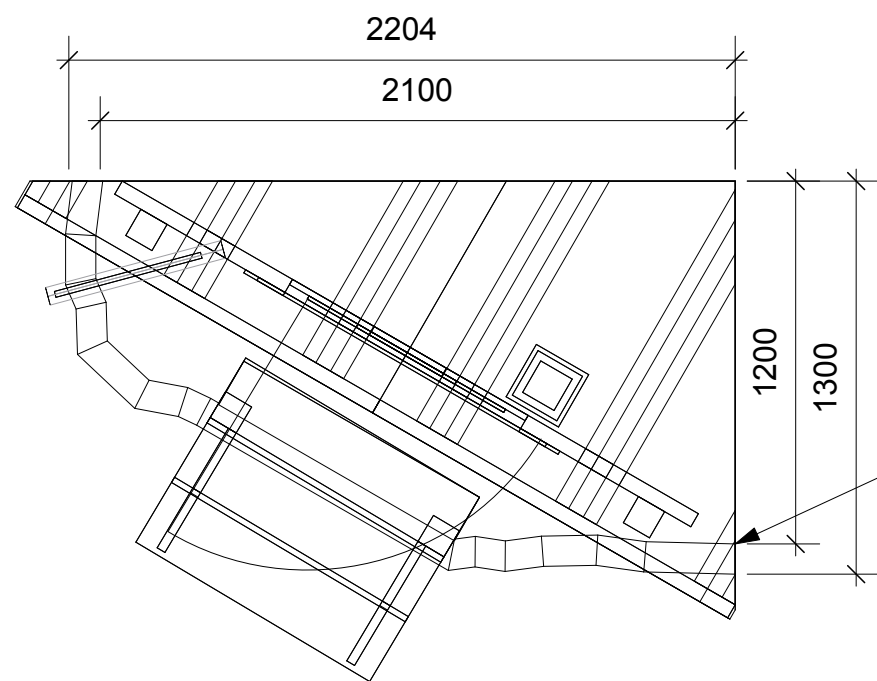

01 Oaken Sauna Top
Scale 1:25

Rocky Carving


Oaken Sauna On a Truck

100mm allowed for rocky carving

Refer to scenic elevations for rocky carving
detail.

Snow on roof. refer to scenic elevation &
model for further detail.

Frozen	
FORWARD:	CentreStage
PROJECT:	Civic Theatre Newcastle
TITLE:	Oaken Sauna Detail
DIRECTOR:	Matthew Trew-Kayworth
SET DESIGNER:	Harry Gil
LIGHTING DESIGNER:	Zach Kruse
SCALE:	DATE:
1:25 @ A2	12/07/2026
DRAWING NUMBER:	
17 of 26	
DESIGNED & DRAWN BY:	CONTACT:
Harry Gil	harry@harrygildesigns.com
VERSION:	2024.02.02
3.0	

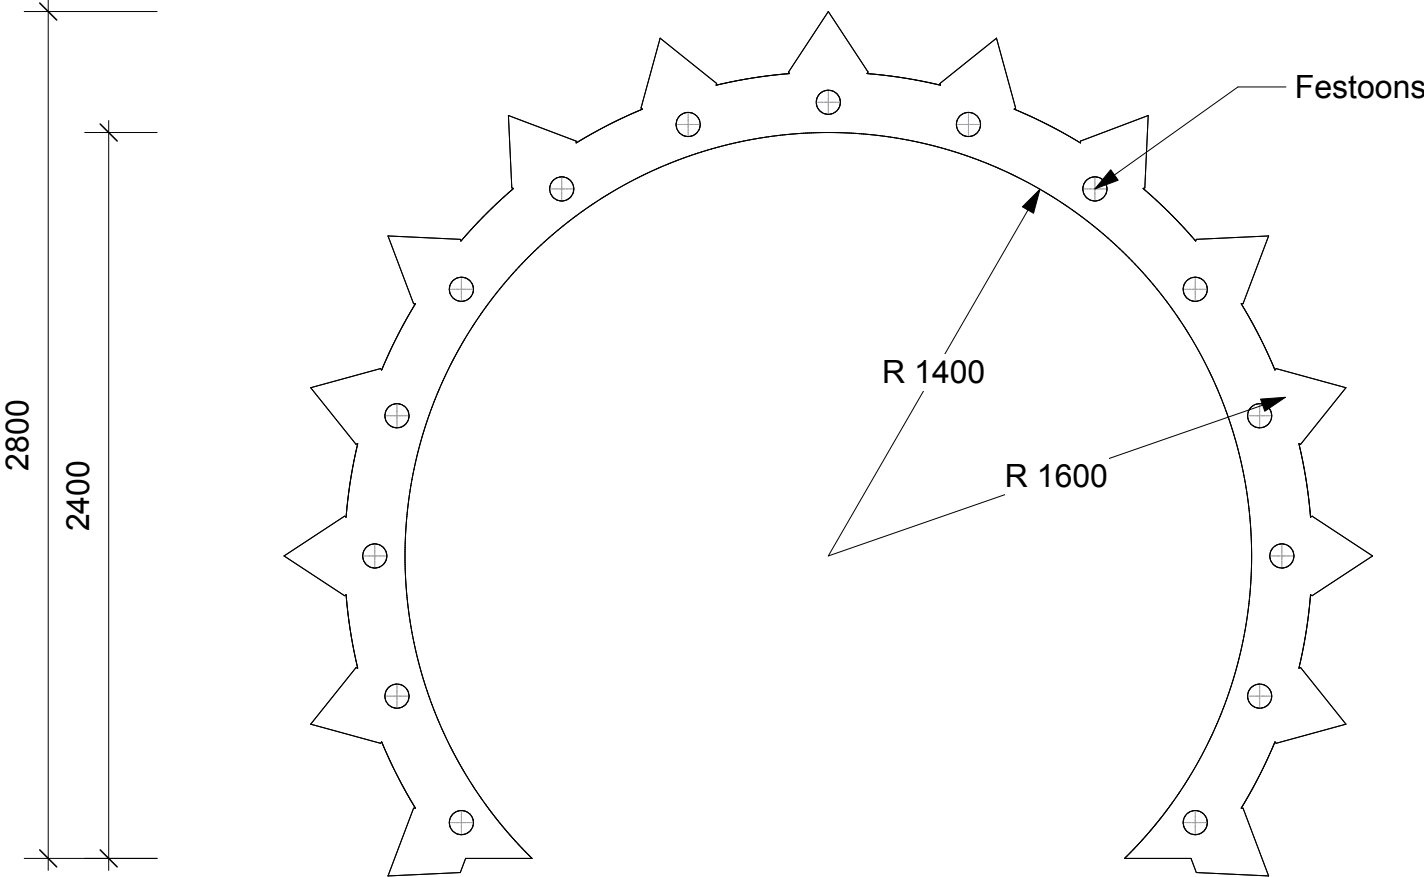

01 Sun Pros Front
Scale 1:25




02 Sun Pros Side
Scale 1:25

Flies in.


50mm nominal thickness given for frame and sun, but sun should look like a piece of paper.

Festoon ammount, spacing & hole size TBC with LD.

Frozen	
CentreStage	
Civic Theatre Newcastle	
Sun Proscenium Detail	
DIRECTOR:	Madison Trew-Keyworth
SET DESIGNER:	Harry Gill
LIGHTING DESIGNER:	Zach Krause
SCALE:	DATE:
1:25 @ A3	12/07/2026
DRAWING NUMBER:	
19 of 26	
DESIGNED & DRAWN BY:	CONTACT:
Harry Gill	harry@harrygilldesigns.com
VERSION:	0431 352 447
3.0	

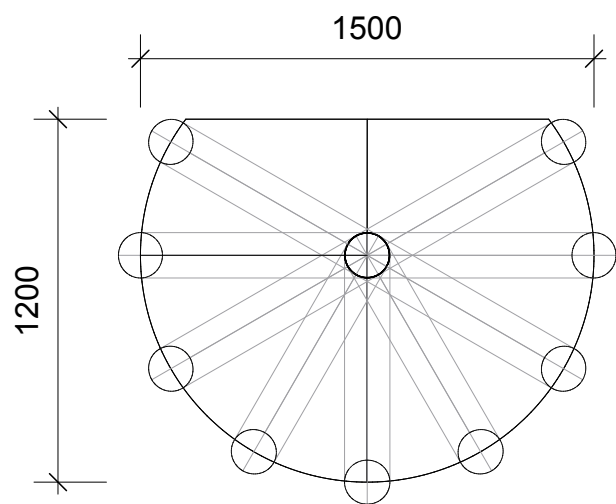

02 Bonfire Top
Scale 1:25

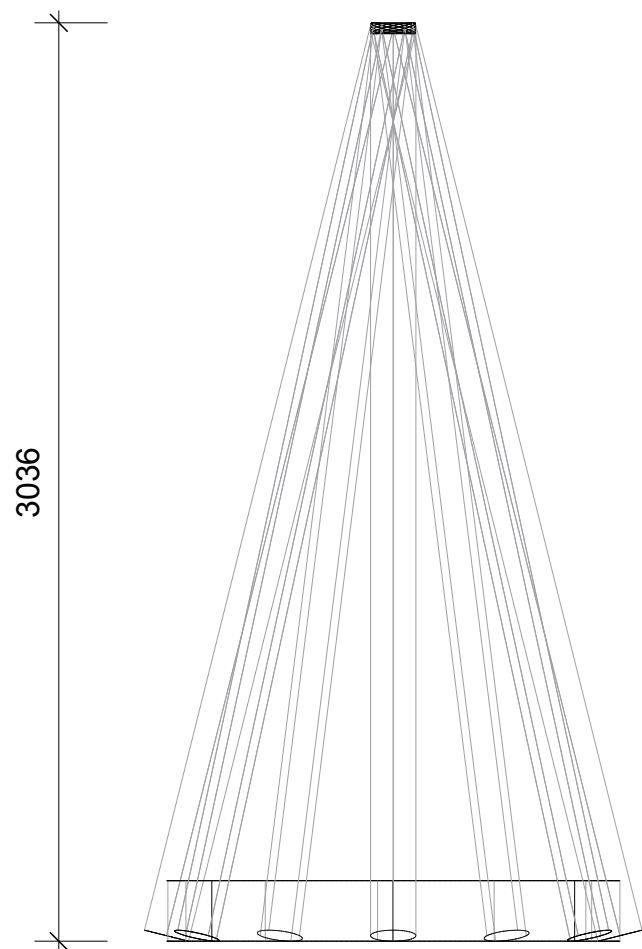


02 Bonfire Front
Scale 1:25


Bonfire made with natural looking wooden
trunks and branches

Smoke machine needed inside.


Truck disguised by branches.

Frozen	
COMPANY: CentreStage	
VENUE: Civic Theatre Newcastle	
TITLE: Bonfire Detail	
DIRECTOR:	Madison Tseu-Keyworth
SET DESIGNER:	Harry Gill
LIGHTING DESIGNER:	Zach Krause
SCALE:	DATE:
1:25 @ A3	12/07/2026
DRAWING NUMBER: 21 of 26	
DESIGNED & DRAWN BY:	CONTACT:
Harry Gill VERSION: 3.0	harry@harrygilldesigns.com 0431 592 447

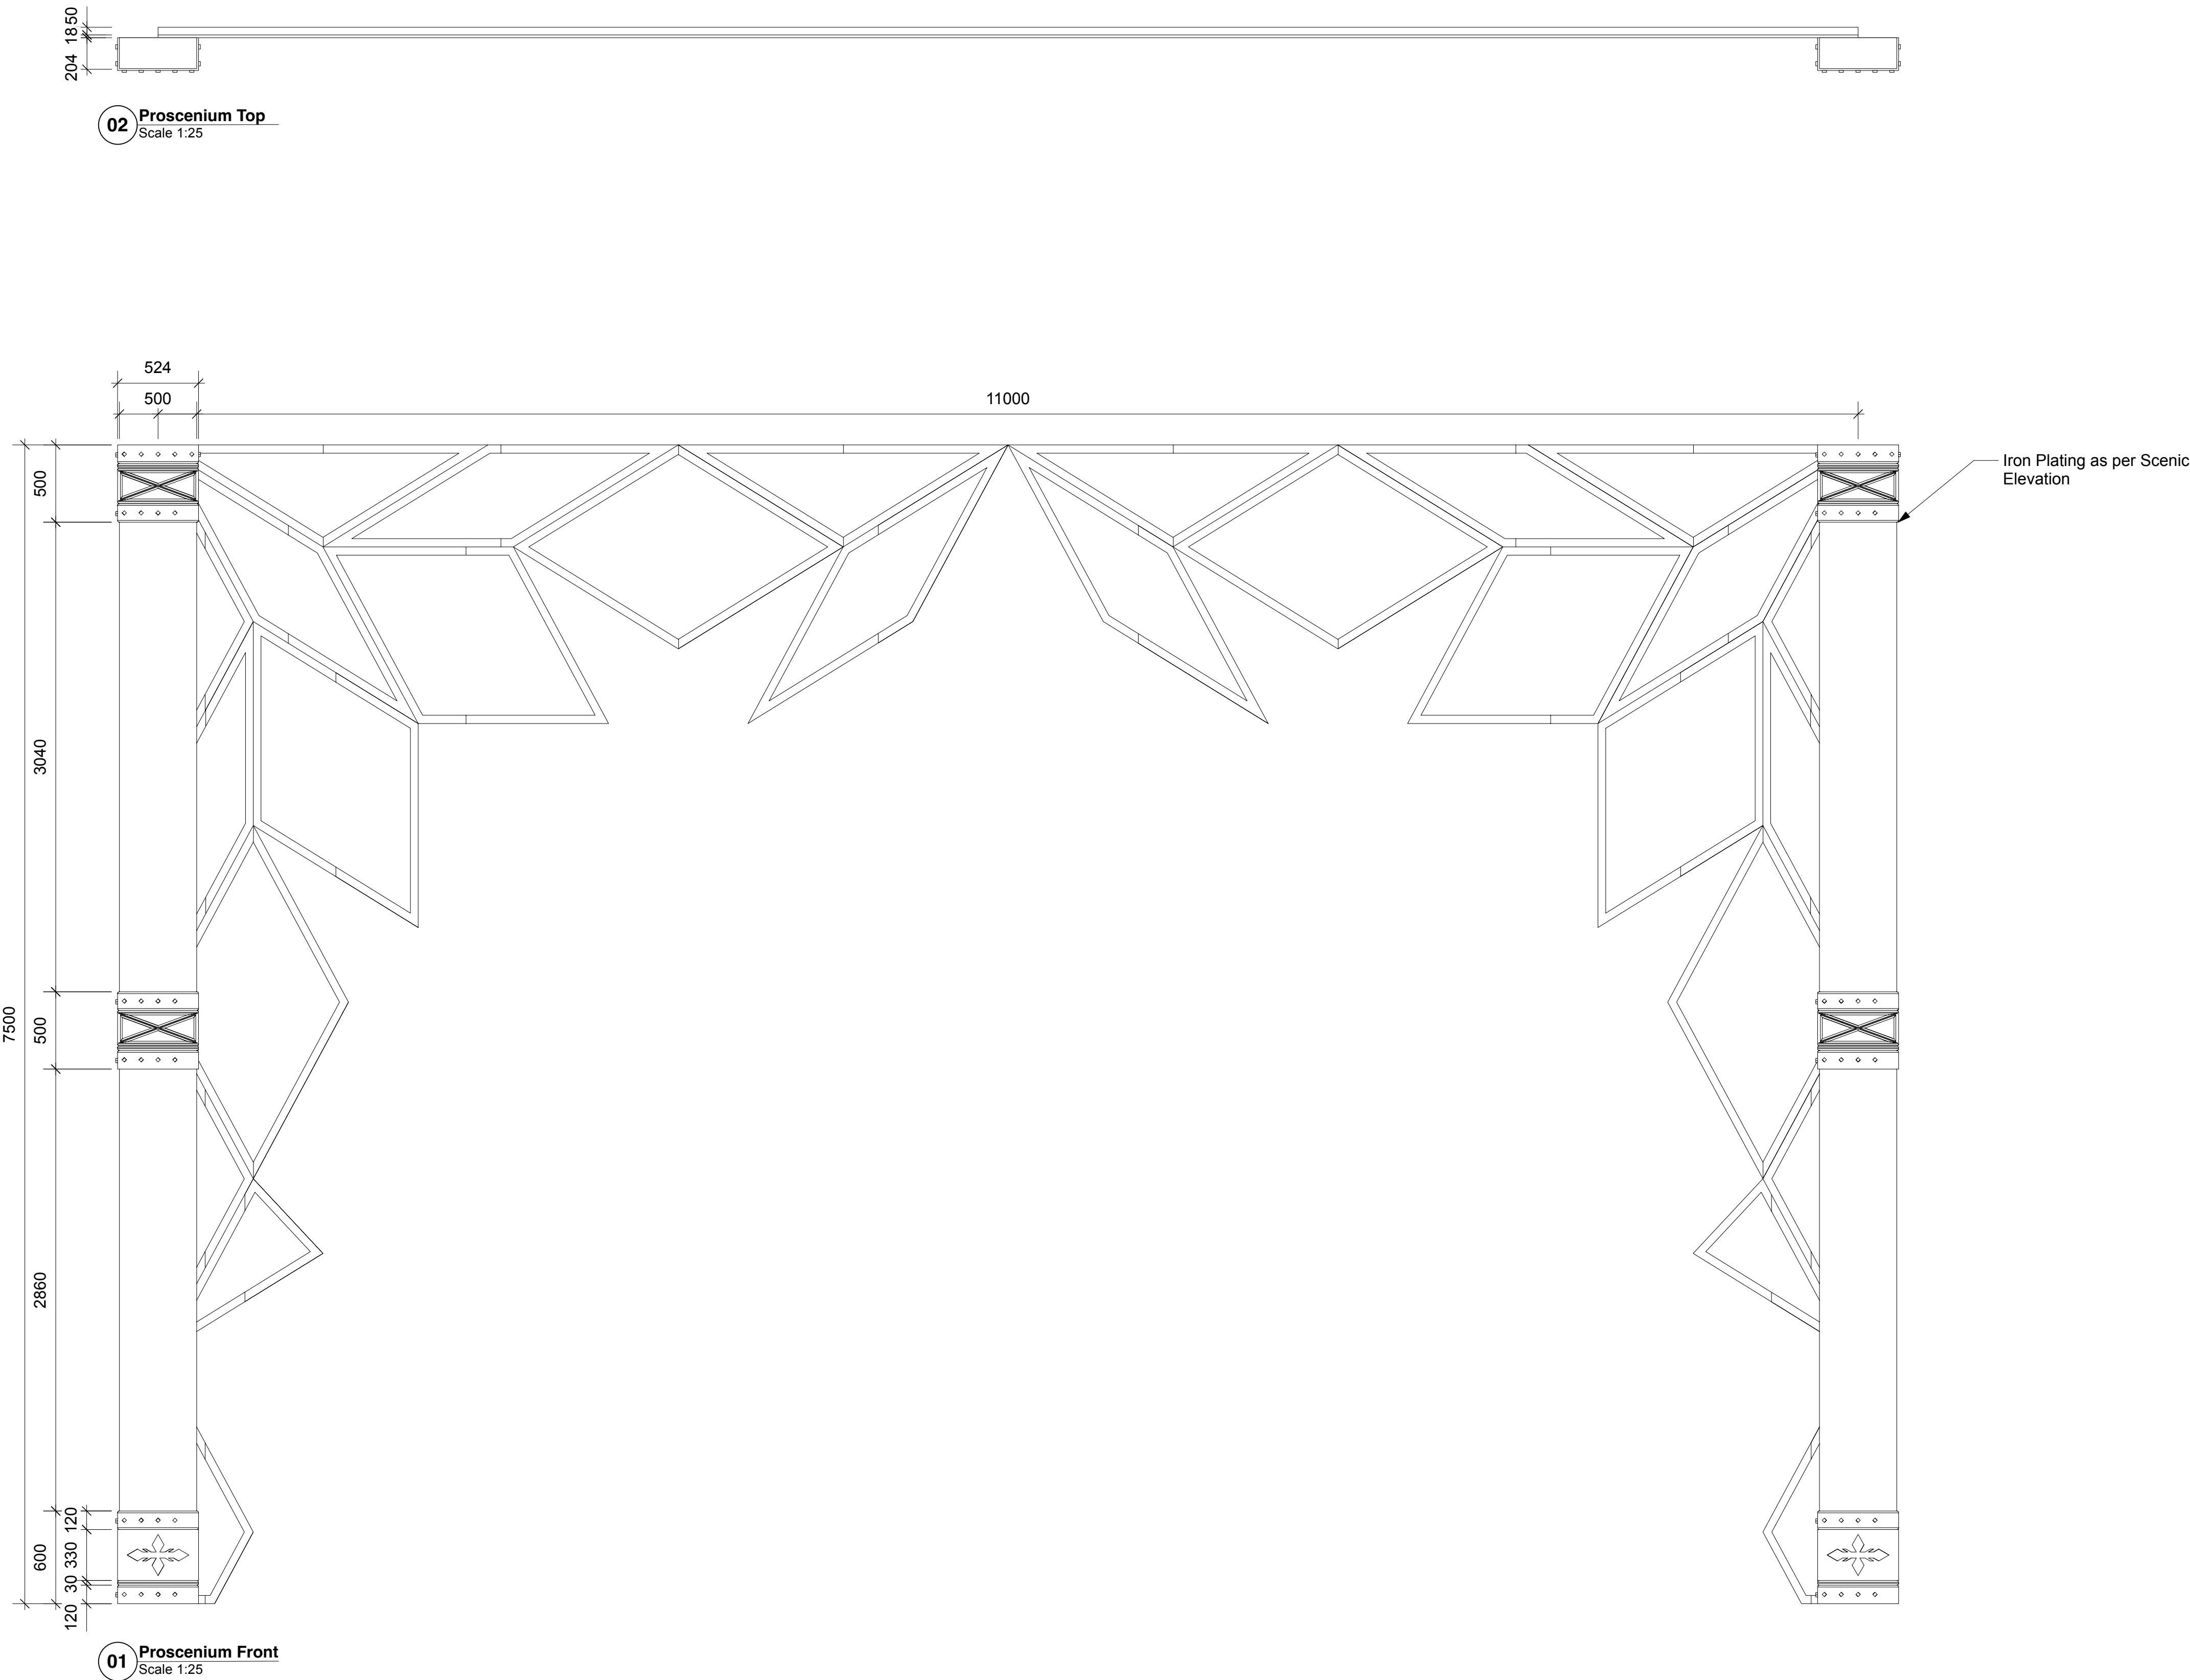


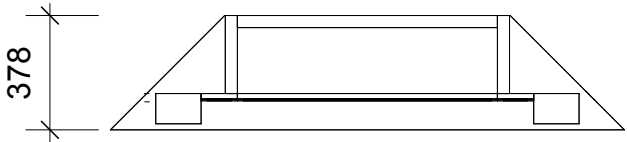


02 Fireplace Top
Scale 1:25

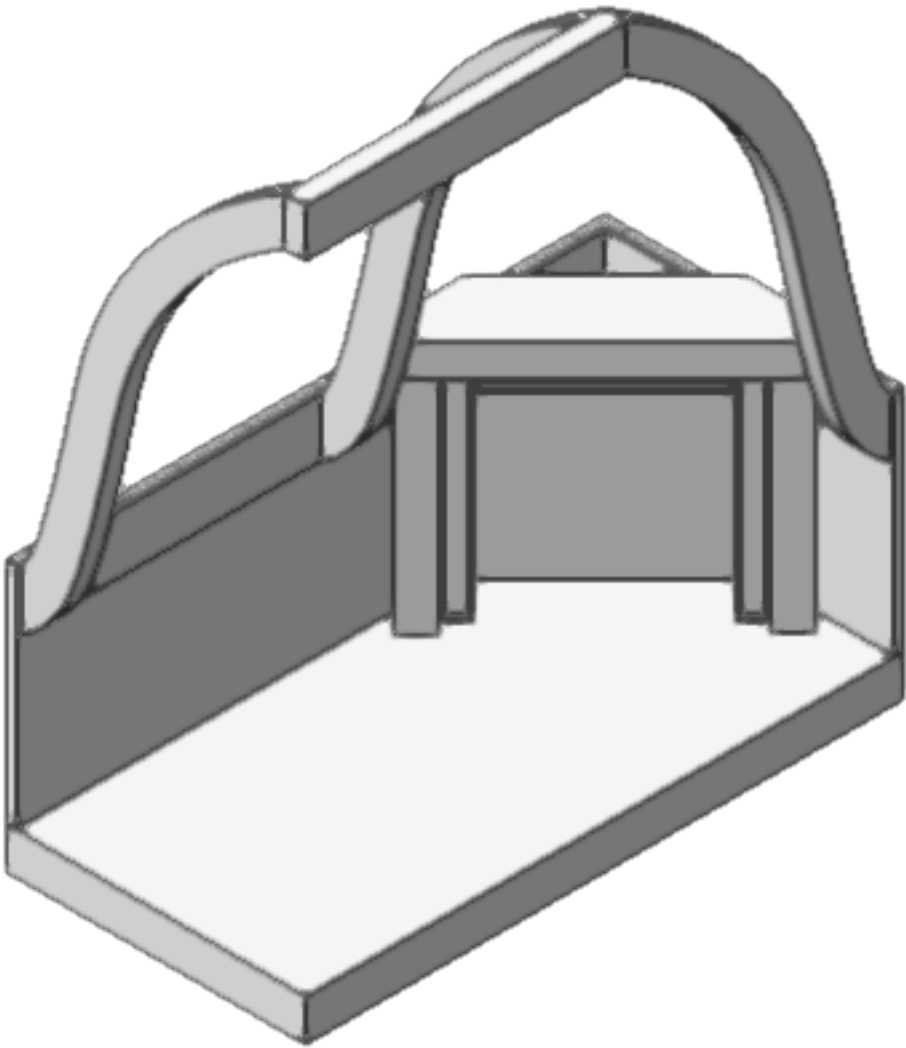

04 Fireplace Iso
Scale 1:25

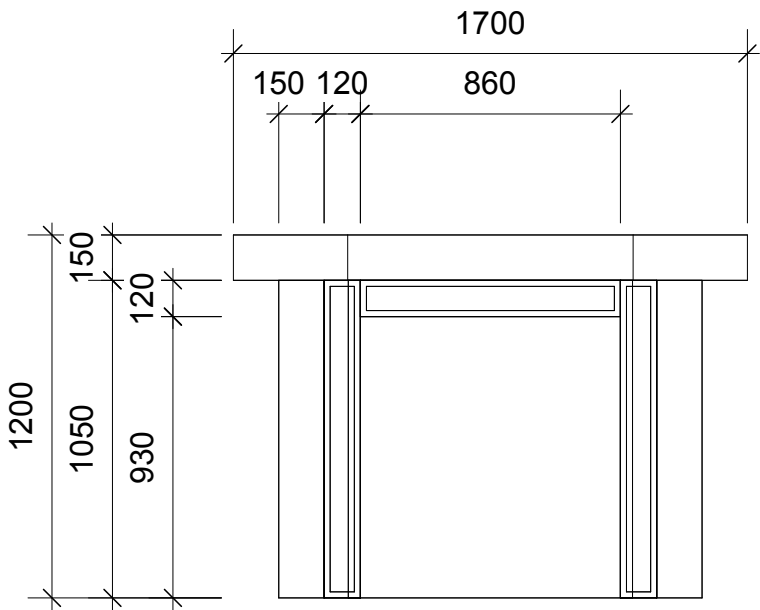


01 Fireplace Front
Scale 1:25

 


03 Fireplace Side
Scale 1:25


Frozen	
COMPANY: CentreStage	
VENUE: Civic Theatre Newcastle	
TITLE: Fireplace Detail	
DIRECTOR:	Madison Tseu-Keyworth
SET DESIGNER:	Harry Gill
LIGHTING DESIGNER:	Zach Krause
SCALE:	DATE:
1:25 @ A3	12/07/2026
DRAWING NUMBER:	
25 of 26	
DESIGNED & DRAWN BY:	CONTACT:
Harry Gill	harry@harrygilldesigns.com
VERSION:	0431 052 447
3.0	

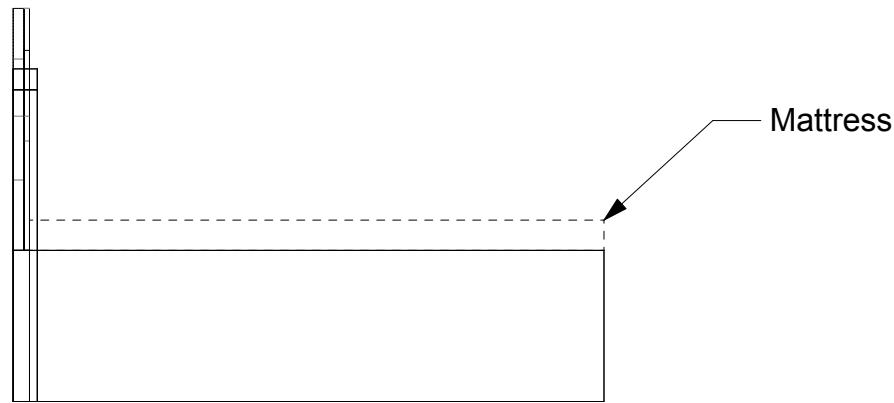

03 Bed Top
Scale 1:25

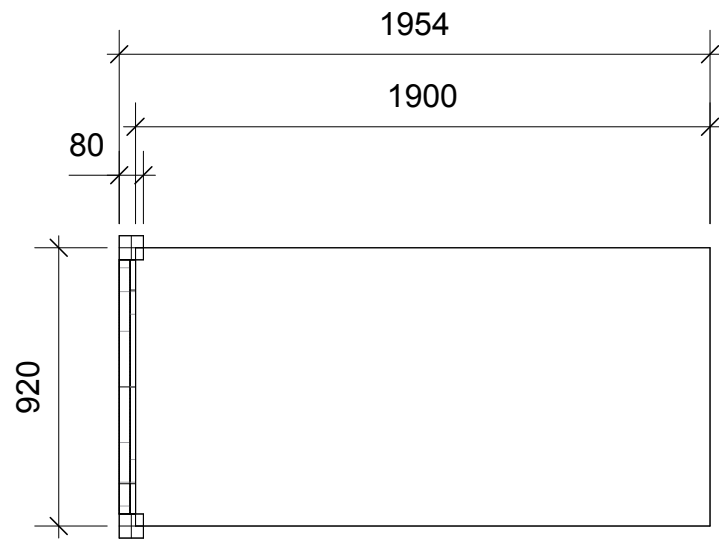

01 Bed Front
Scale 1:25

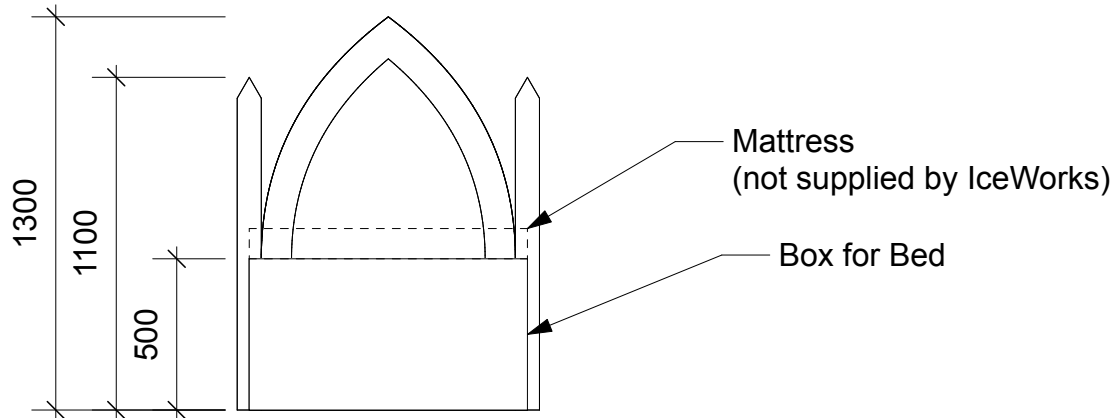

02 Bed Side
Scale 1:25

x2 Bed

Bed Box based around single bed mattress - 1900 x 920 - Access under bed needed - will be masked with valance.

Beds to be removable from bedroom truck.

Bed Box will not be visible.

Frozen	
COMPANY: CentreStage	
VENUE: Civic Theatre Newcastle	
TITLE: Beds Detail	
DIRECTOR:	Madison Trew-Keyworth
SET DESIGNER:	Harry Gill
LIGHTING DESIGNER:	Zach Krause
SCALE:	DATE:
1:25 @ A3	12/07/2026
DRAWING NUMBER: 26 of 26	
DESIGNED & DRAWN BY:	CONTACT:
Harry Gill	harry@harrygilldesigns.com
VERSION: 3.0	0431 992 447