



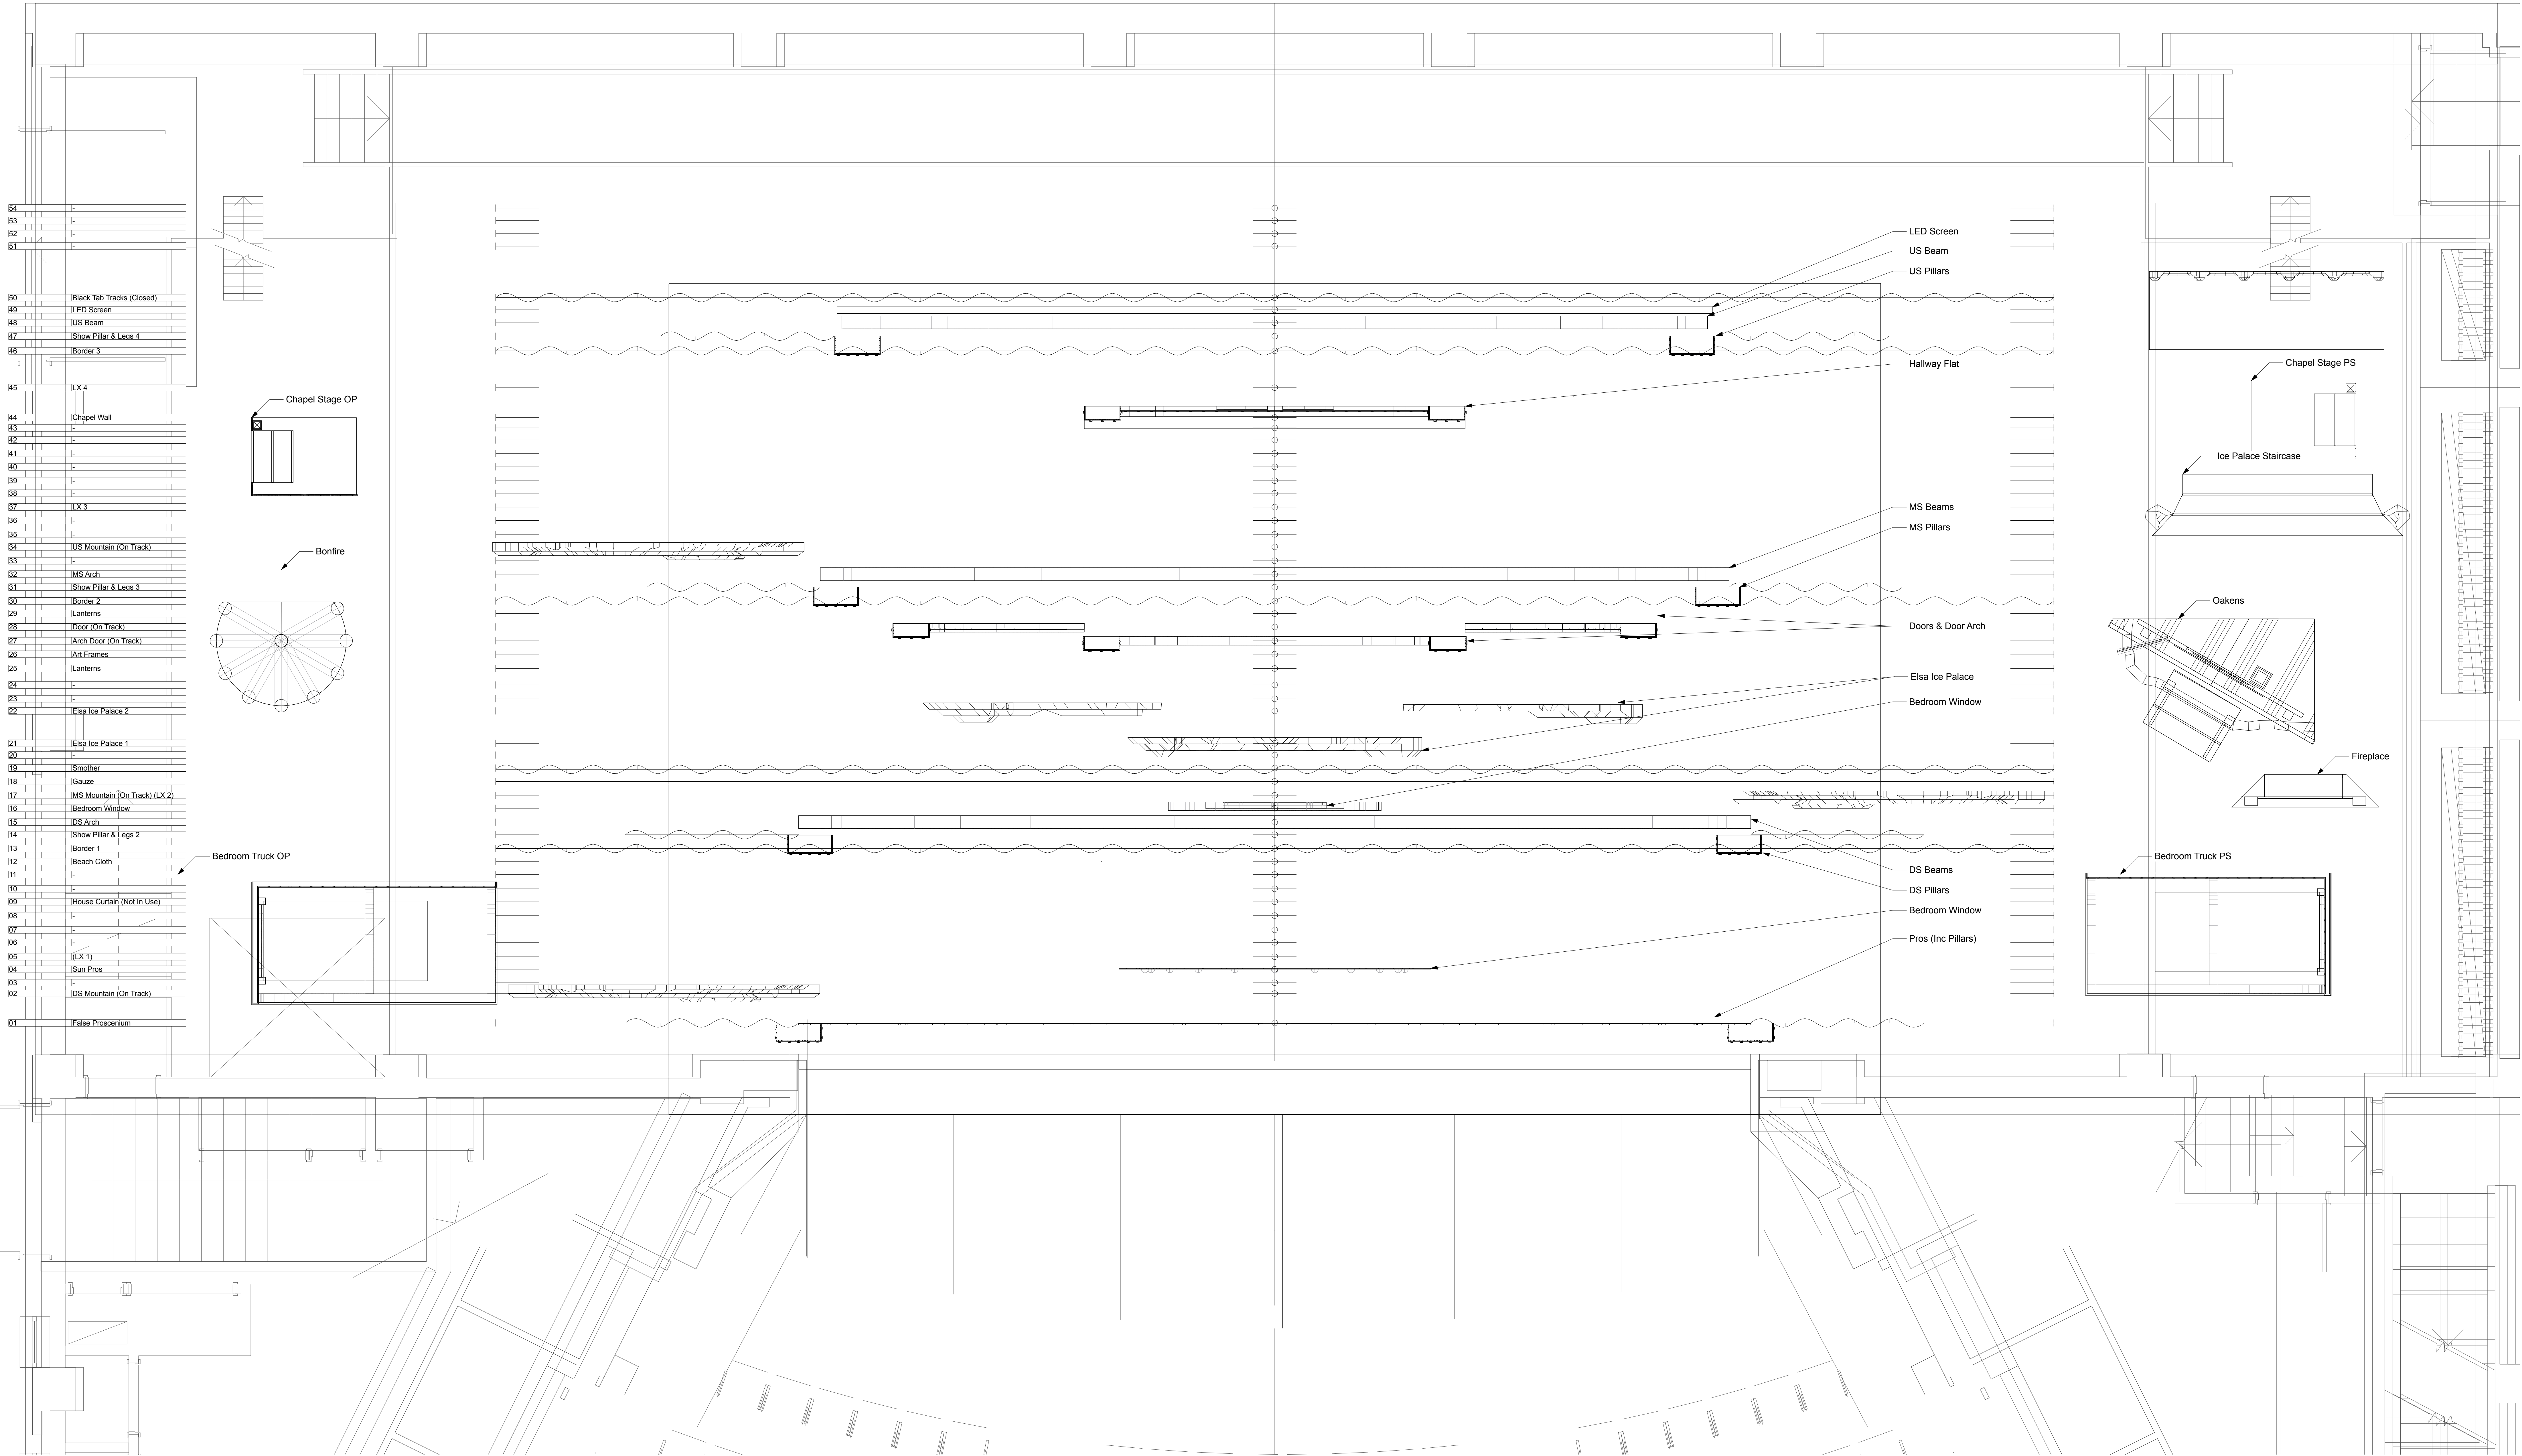

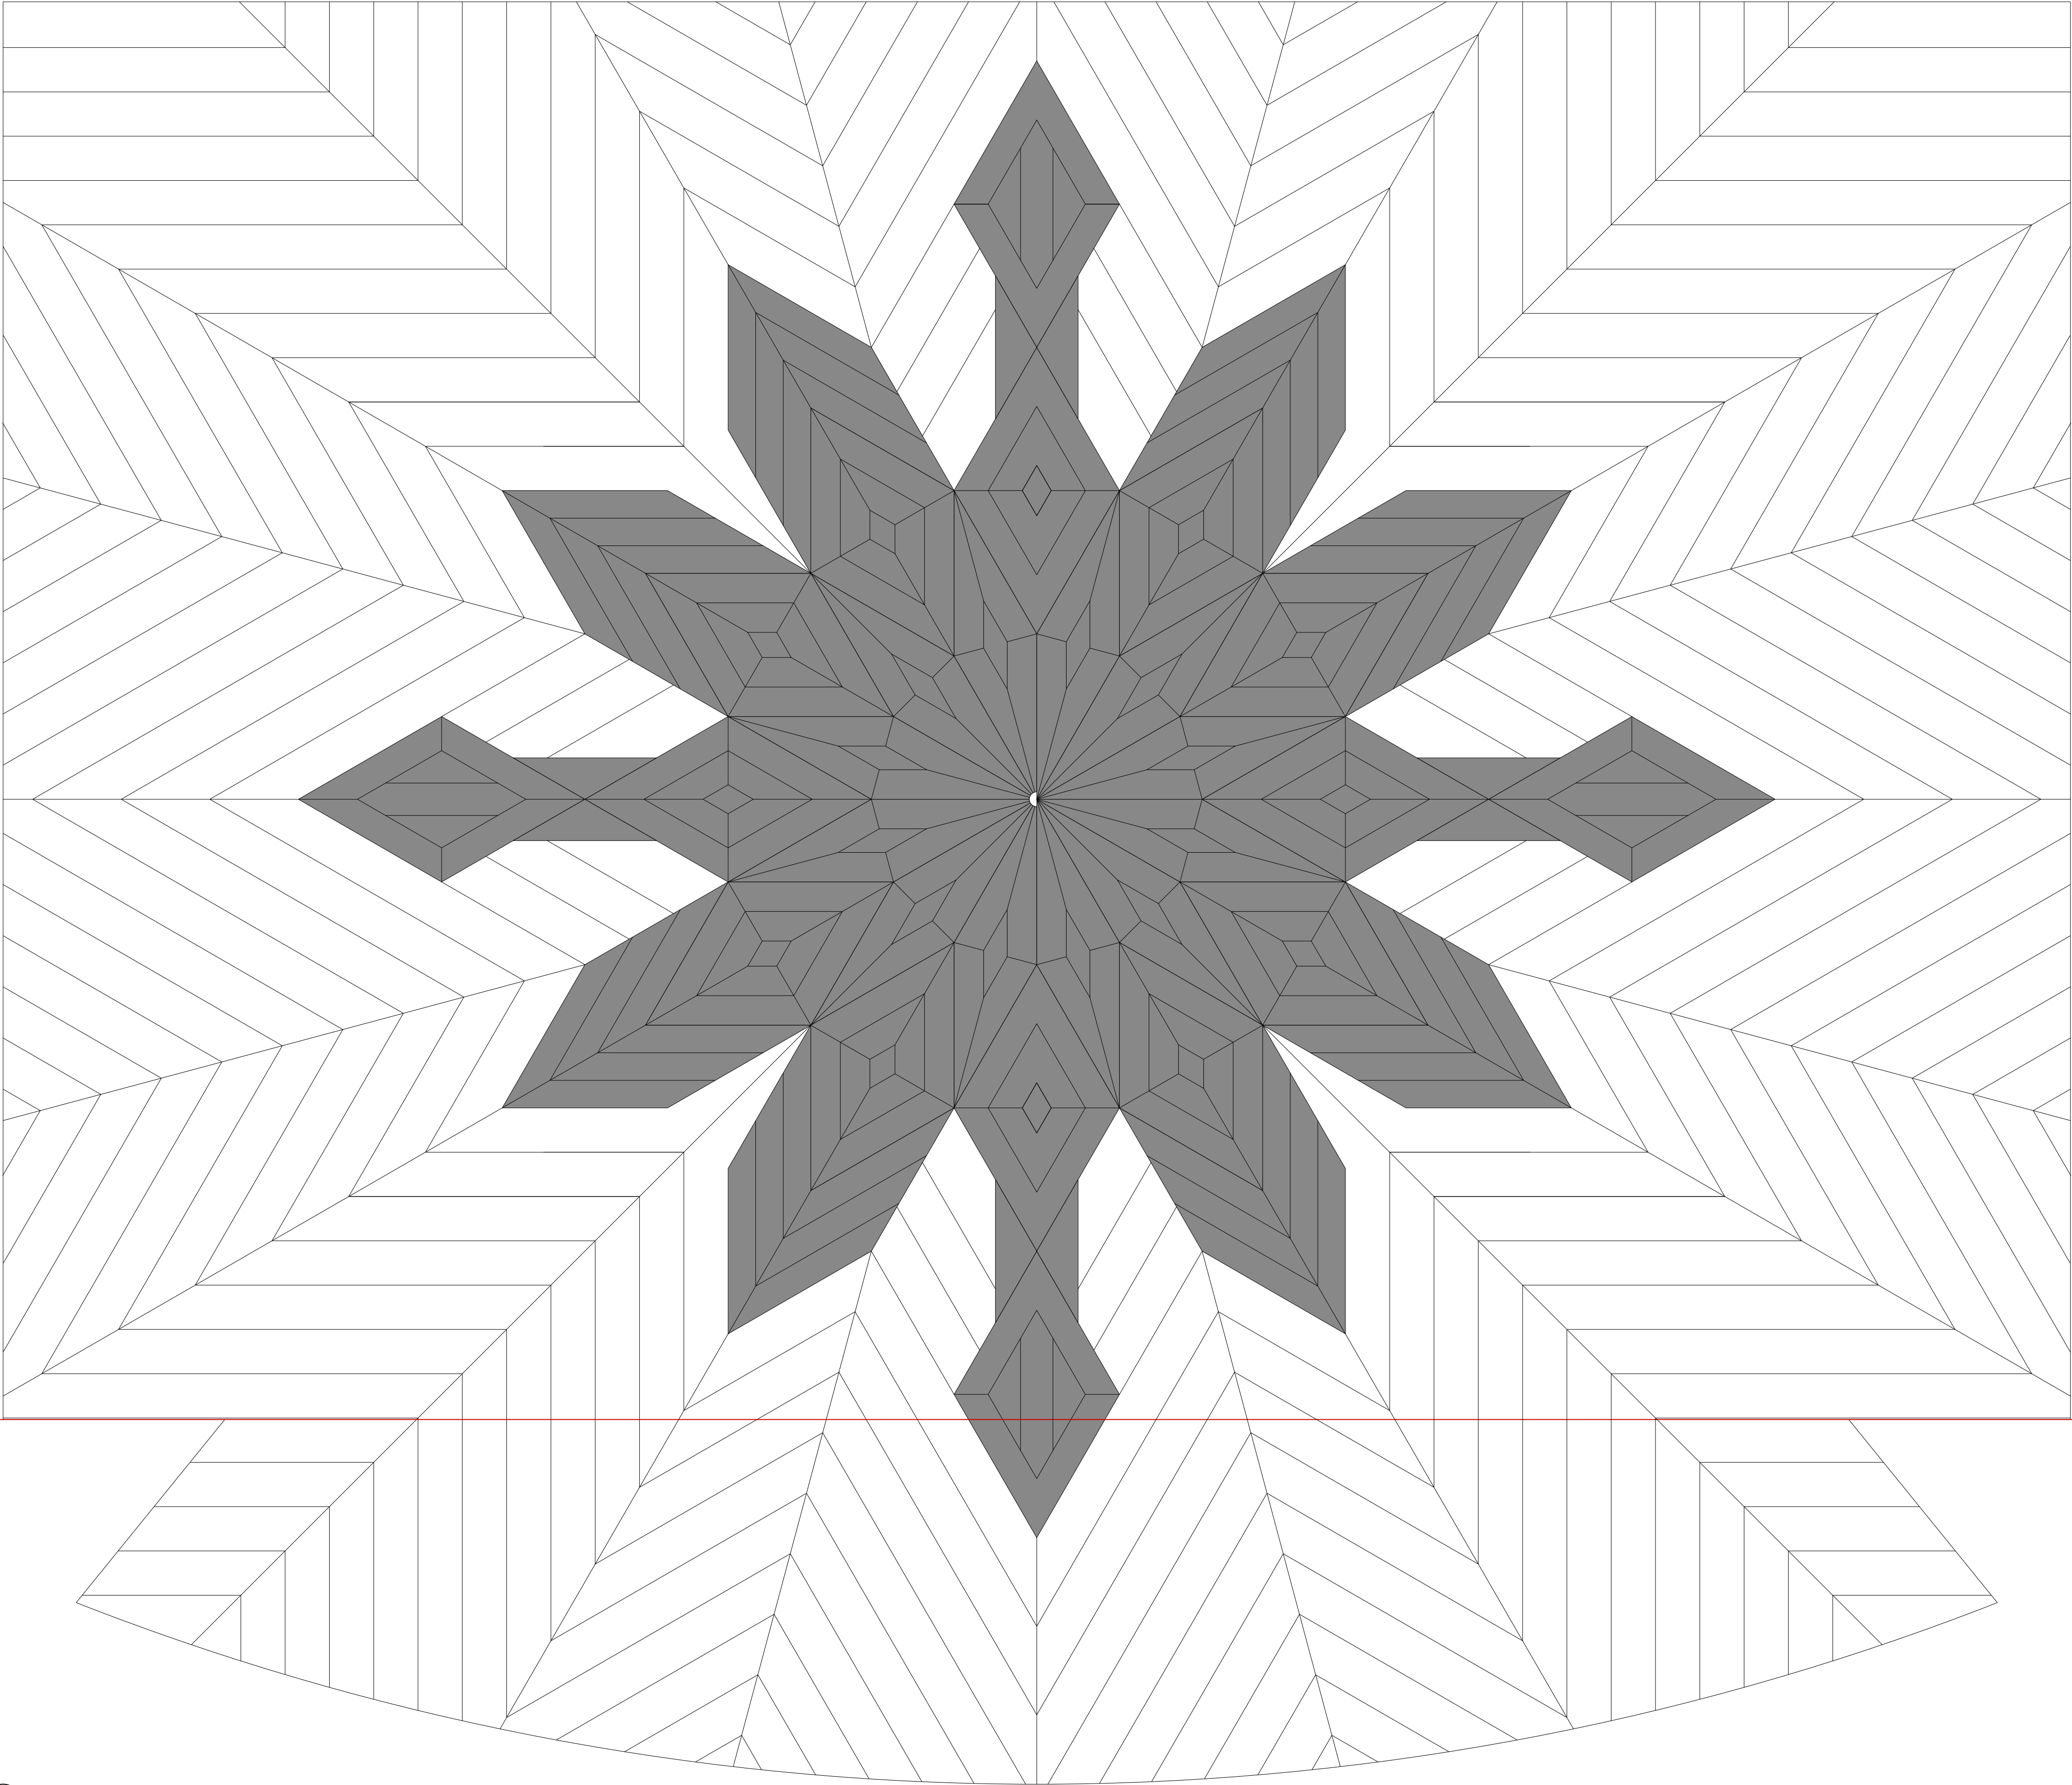

SETTING LINE


01 Floor Top View
Scale 1:25

Grey area treatment different to white area.
See scenic elevation for more info.

10800x14000 total floor area required

Floor now to include the apron. Detail
pending accurate drawings from venue.

Frozen	
Stoddart Entertainment Group	
Civic Theatre Newcastle	
Floor Detail	
DATE:	12/07/2026
BY:	12/07/2026
1:25 @ A1	12/07/2026
03 of 26	
8.0	

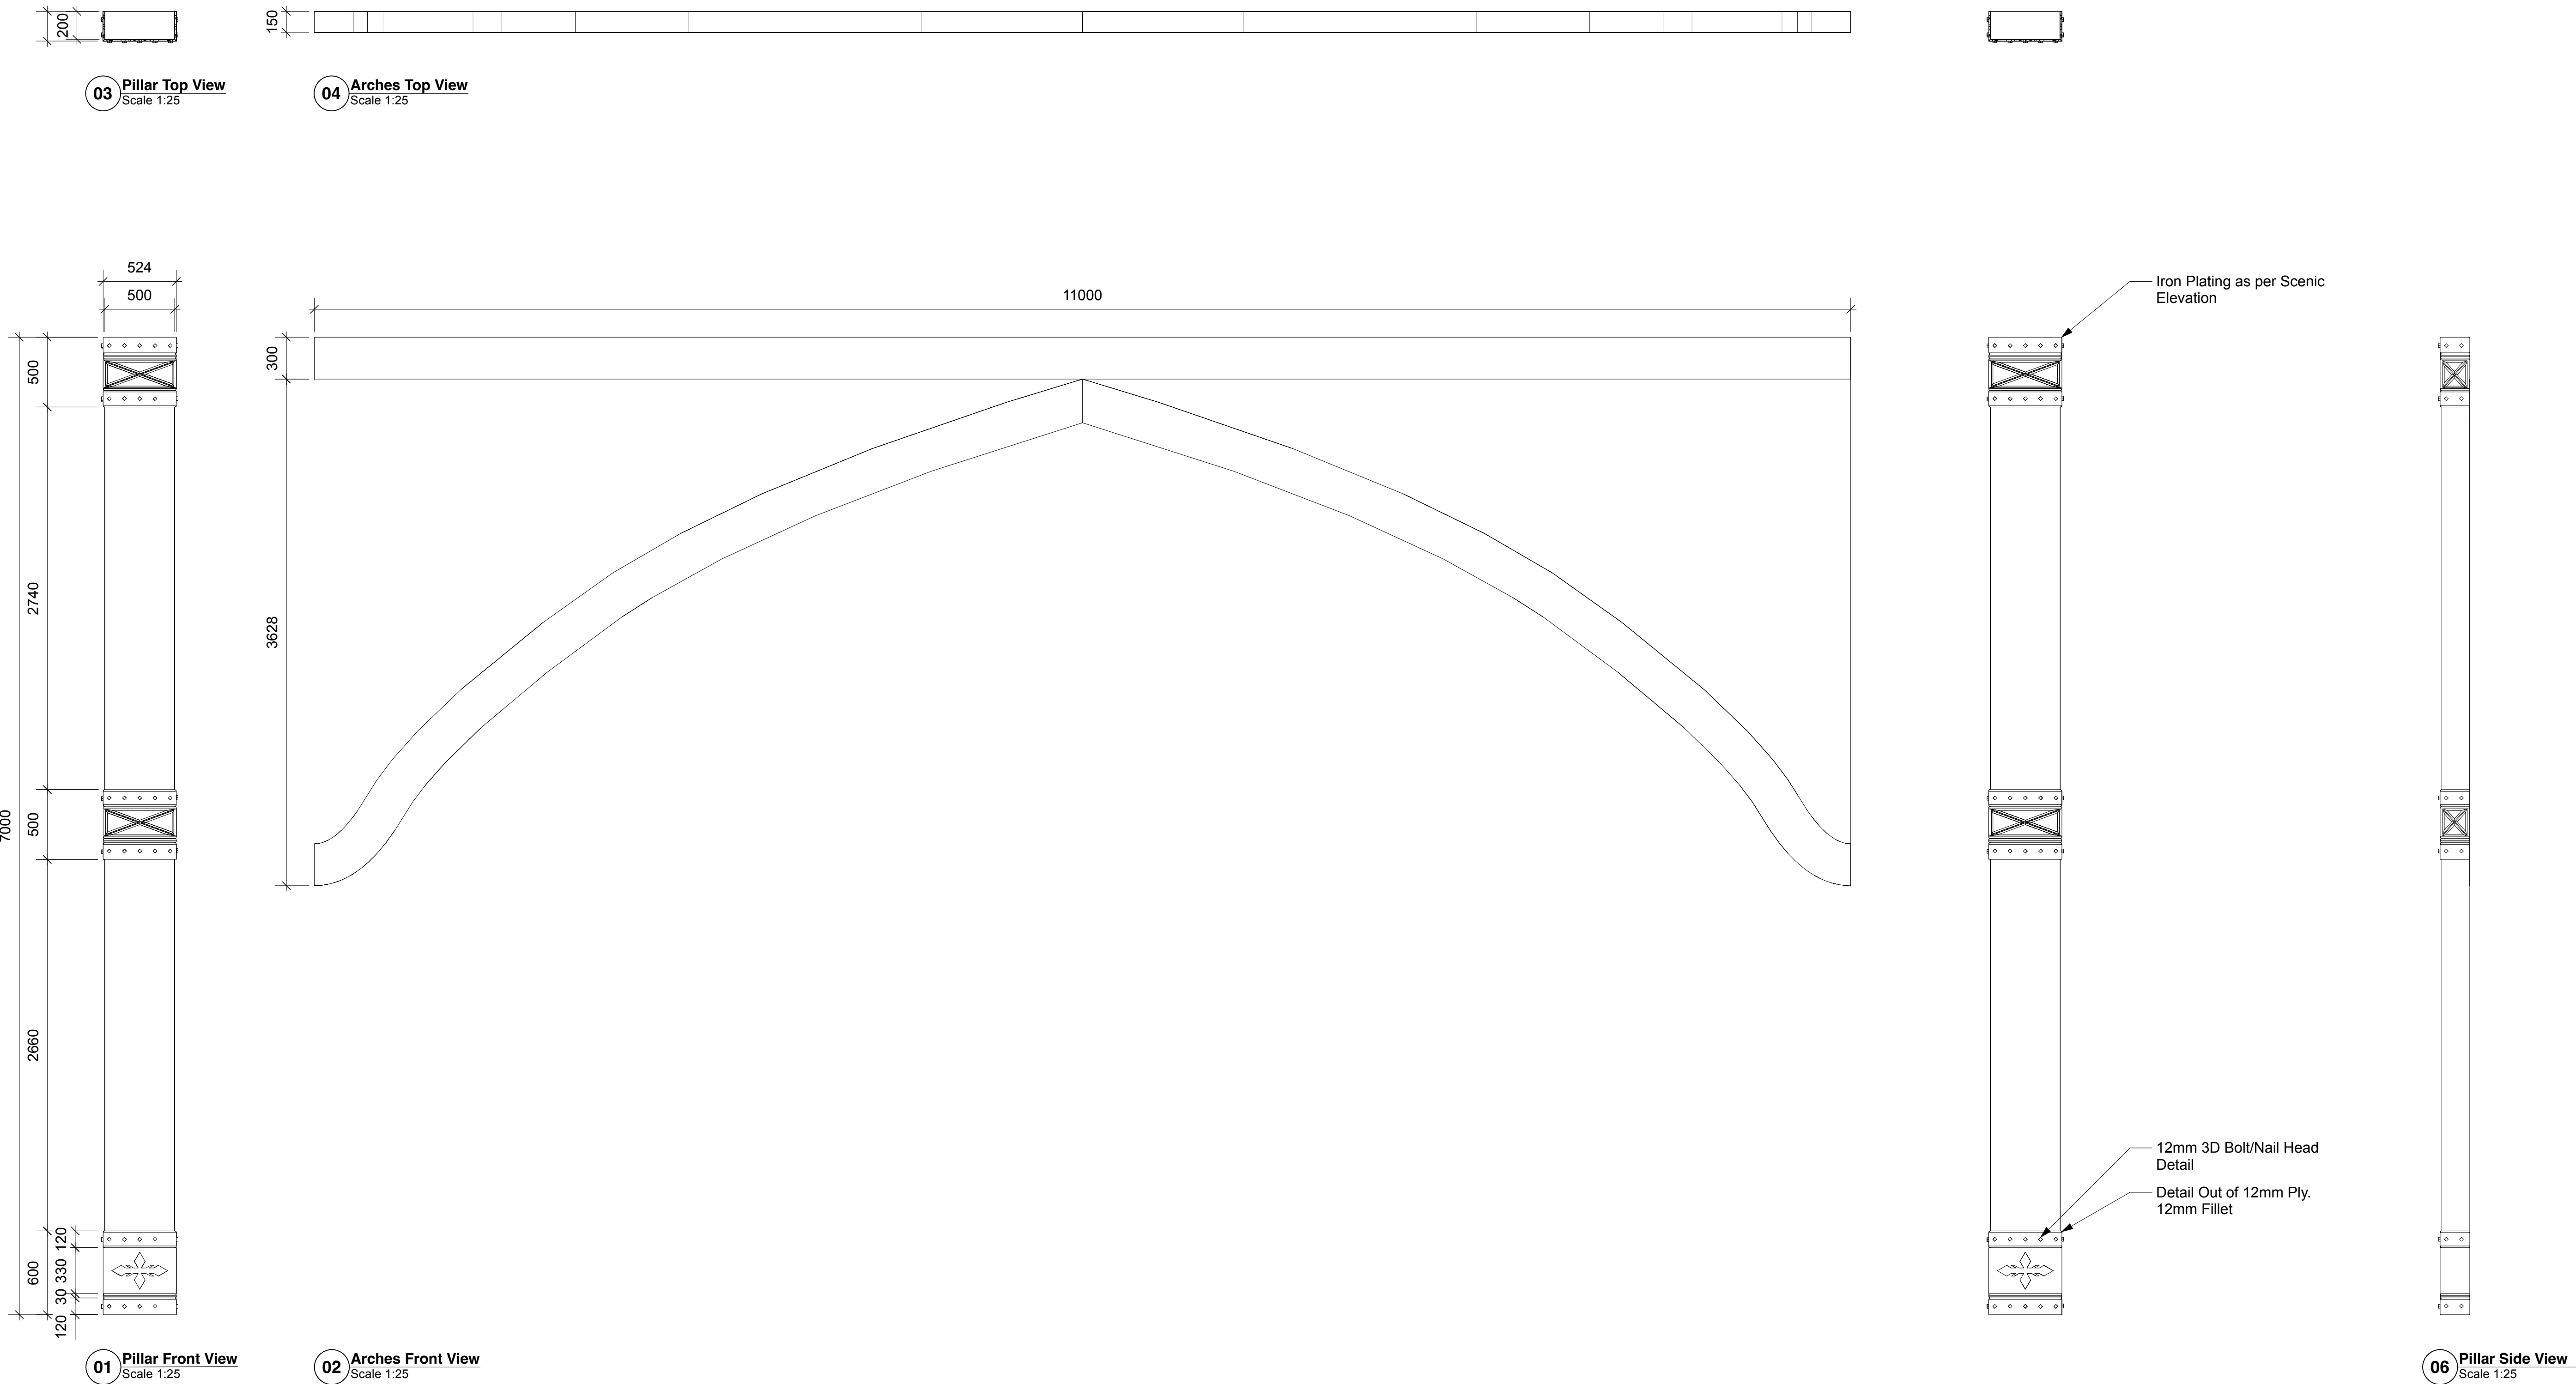



Arch and Pillars are seperate pieces.

Archs fly in and out, Pillars are stationary


Iron Plating detail only required on front and onstage side of each pillar.

Frozen	
Stoddart Entertainment Group	
Civic Theatre Newcastle	
DS Pillars & Arches Detail	
DATE:	12/07/2026
BY:	12/07/2026
1:25 @ A1	04 of 26
04 of 26	04 of 26
8.0	8.0





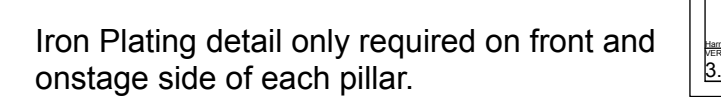


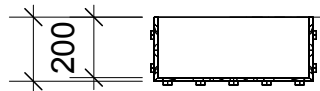

03 Pillar Top View
Scale 1:25

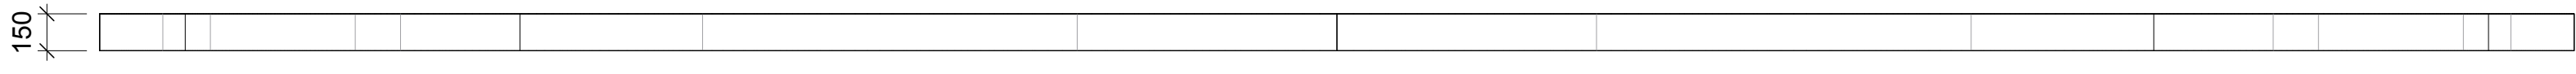

04 Arches Top View
Scale 1:25

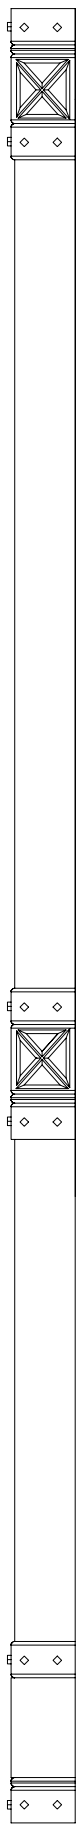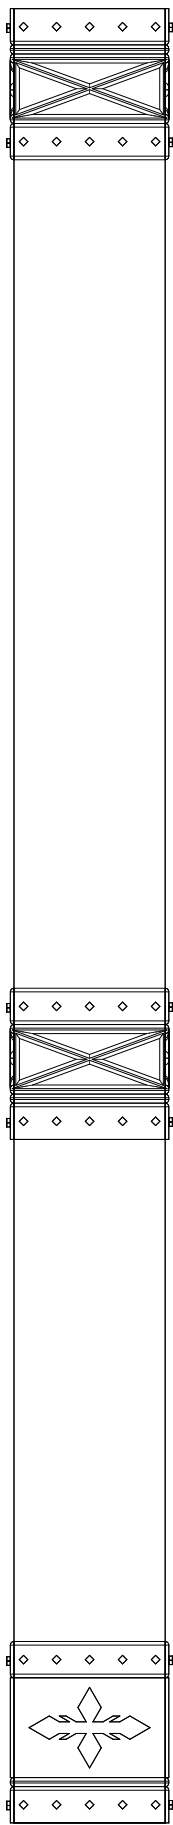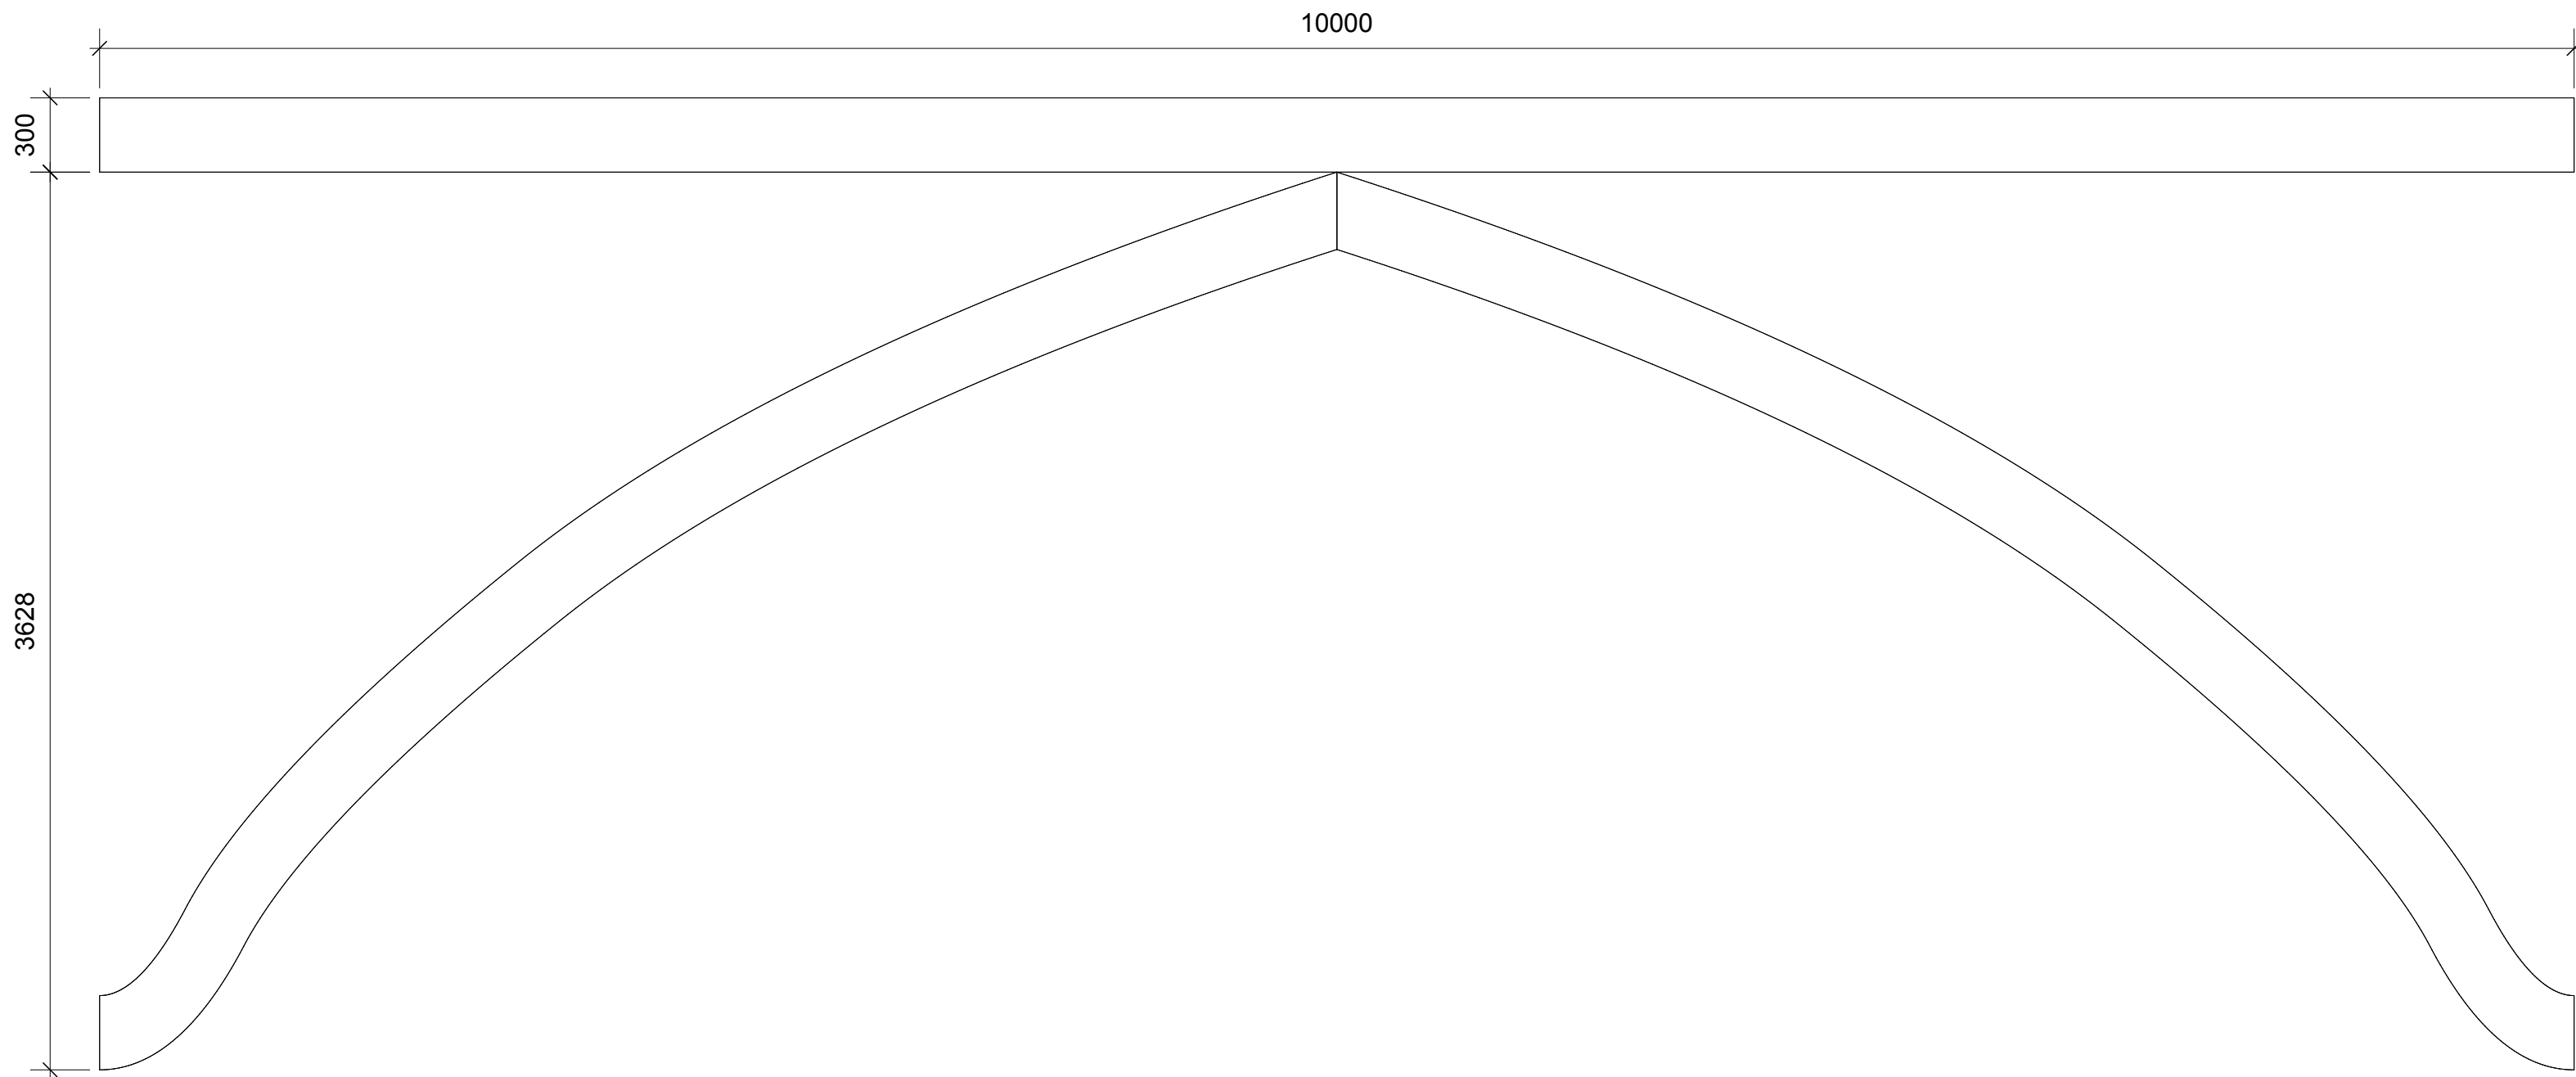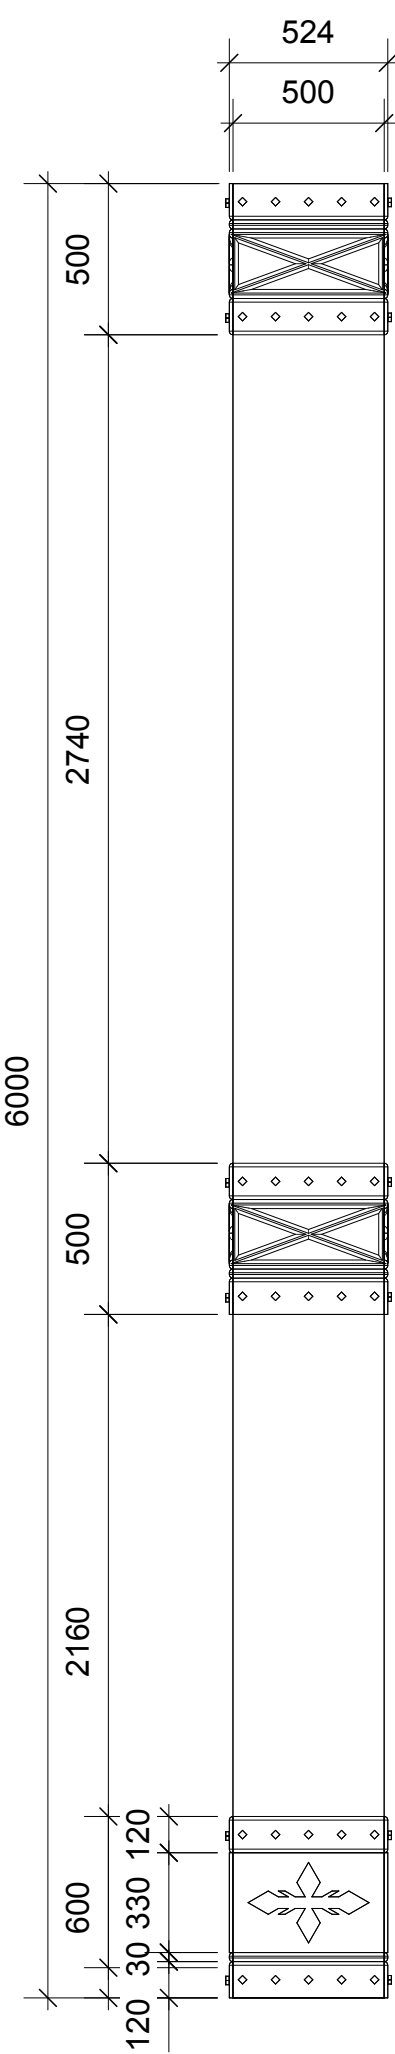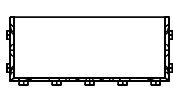


06 Pillar Side View
Scale 1:25

Arch and Pillars are seperate pieces.


Archs fly in and out, Pillars are stationary

Iron Plating detail only required on front and onstage side of each pillar.


Frozen	
Stoddart Entertainment Group	
Civic Theatre Newcastle	
US Pilairs & Arches Detail	
DATE:	12/07/2026
BY:	12/07/2026
1:25 @ A1	12/07/2026
06 of 26	
8.0	

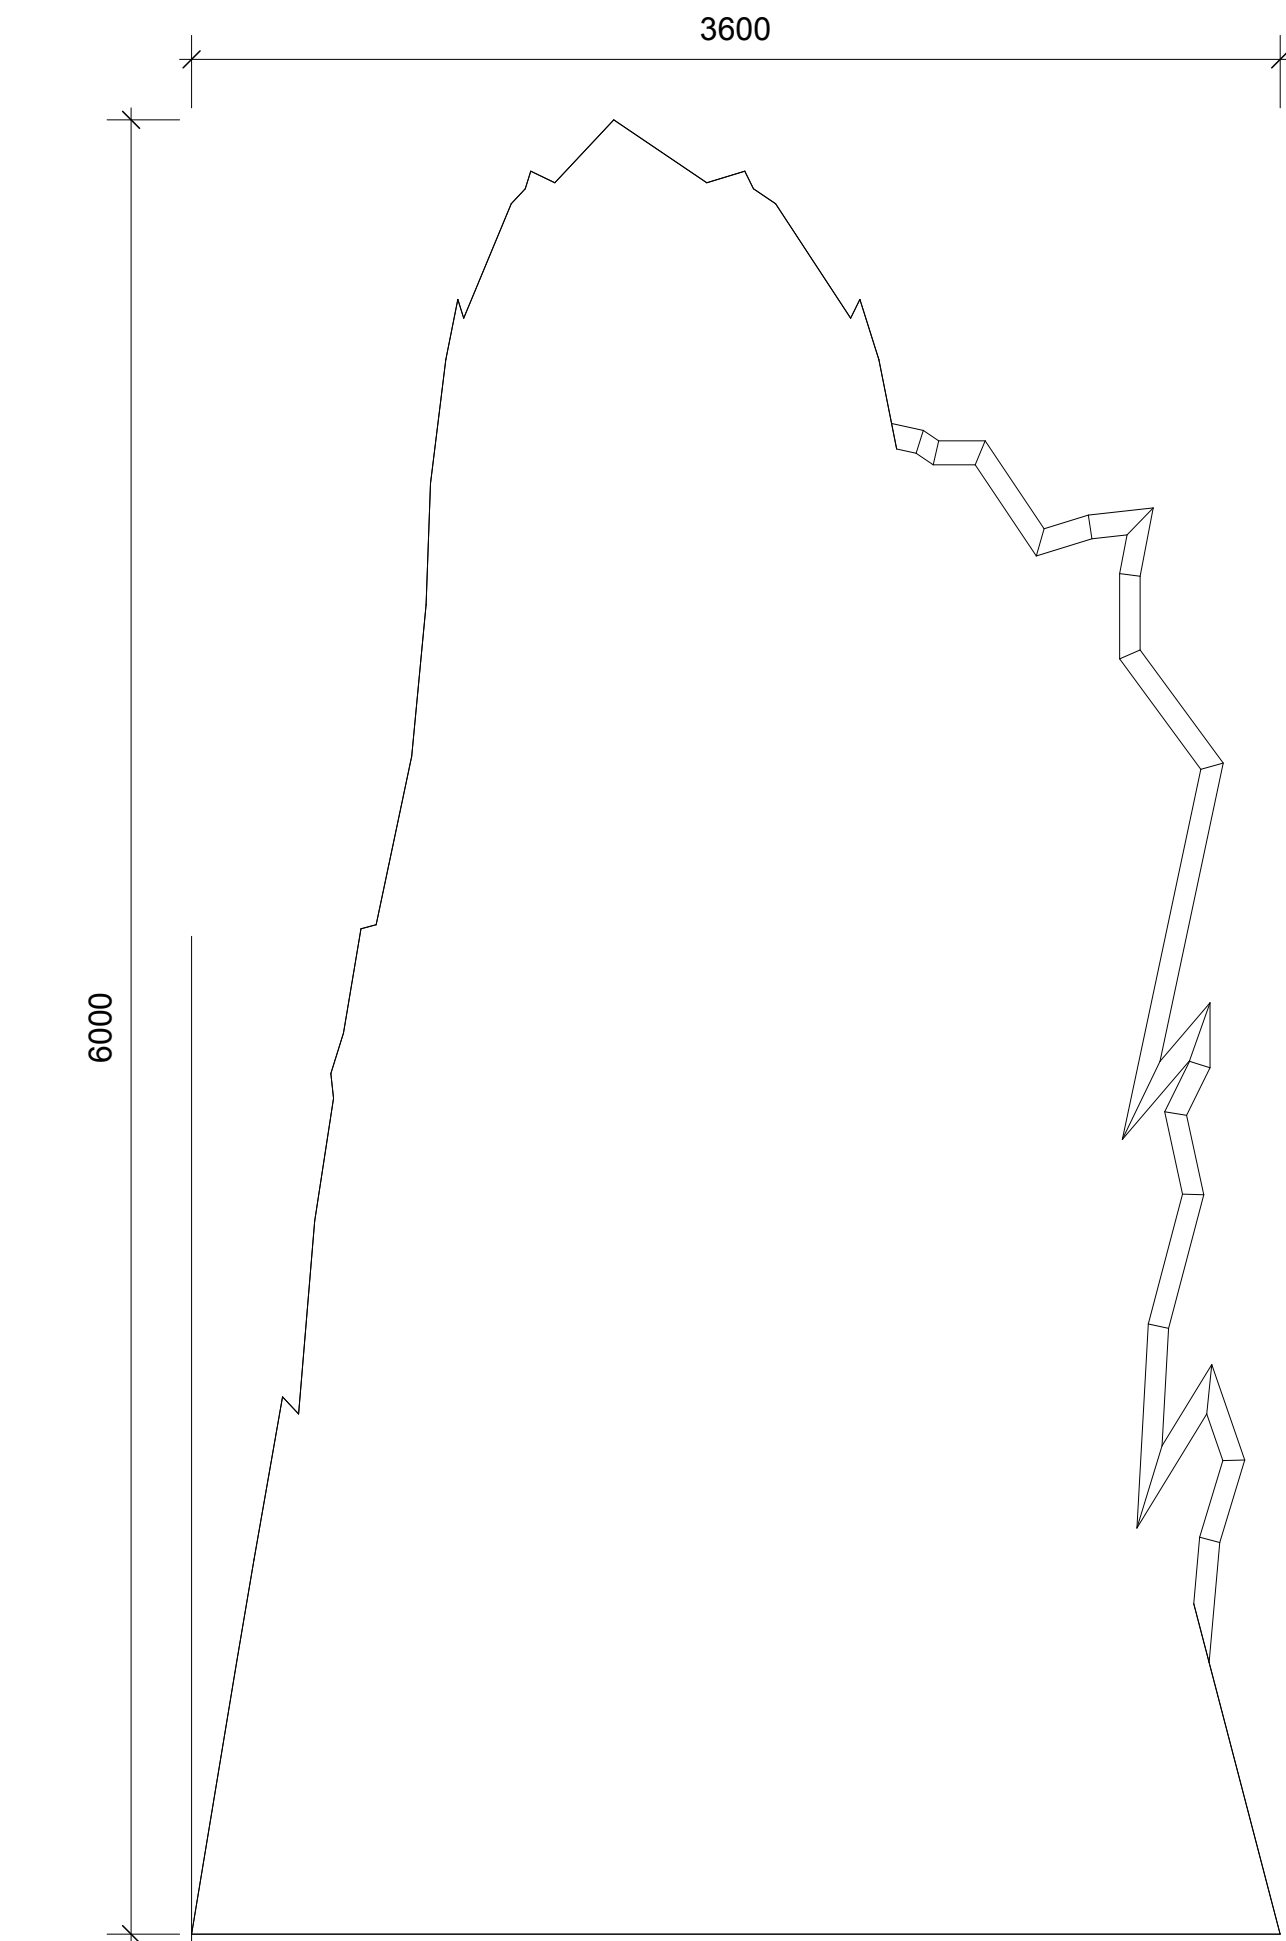


01 Mountain Layer 1
Scale 1:25

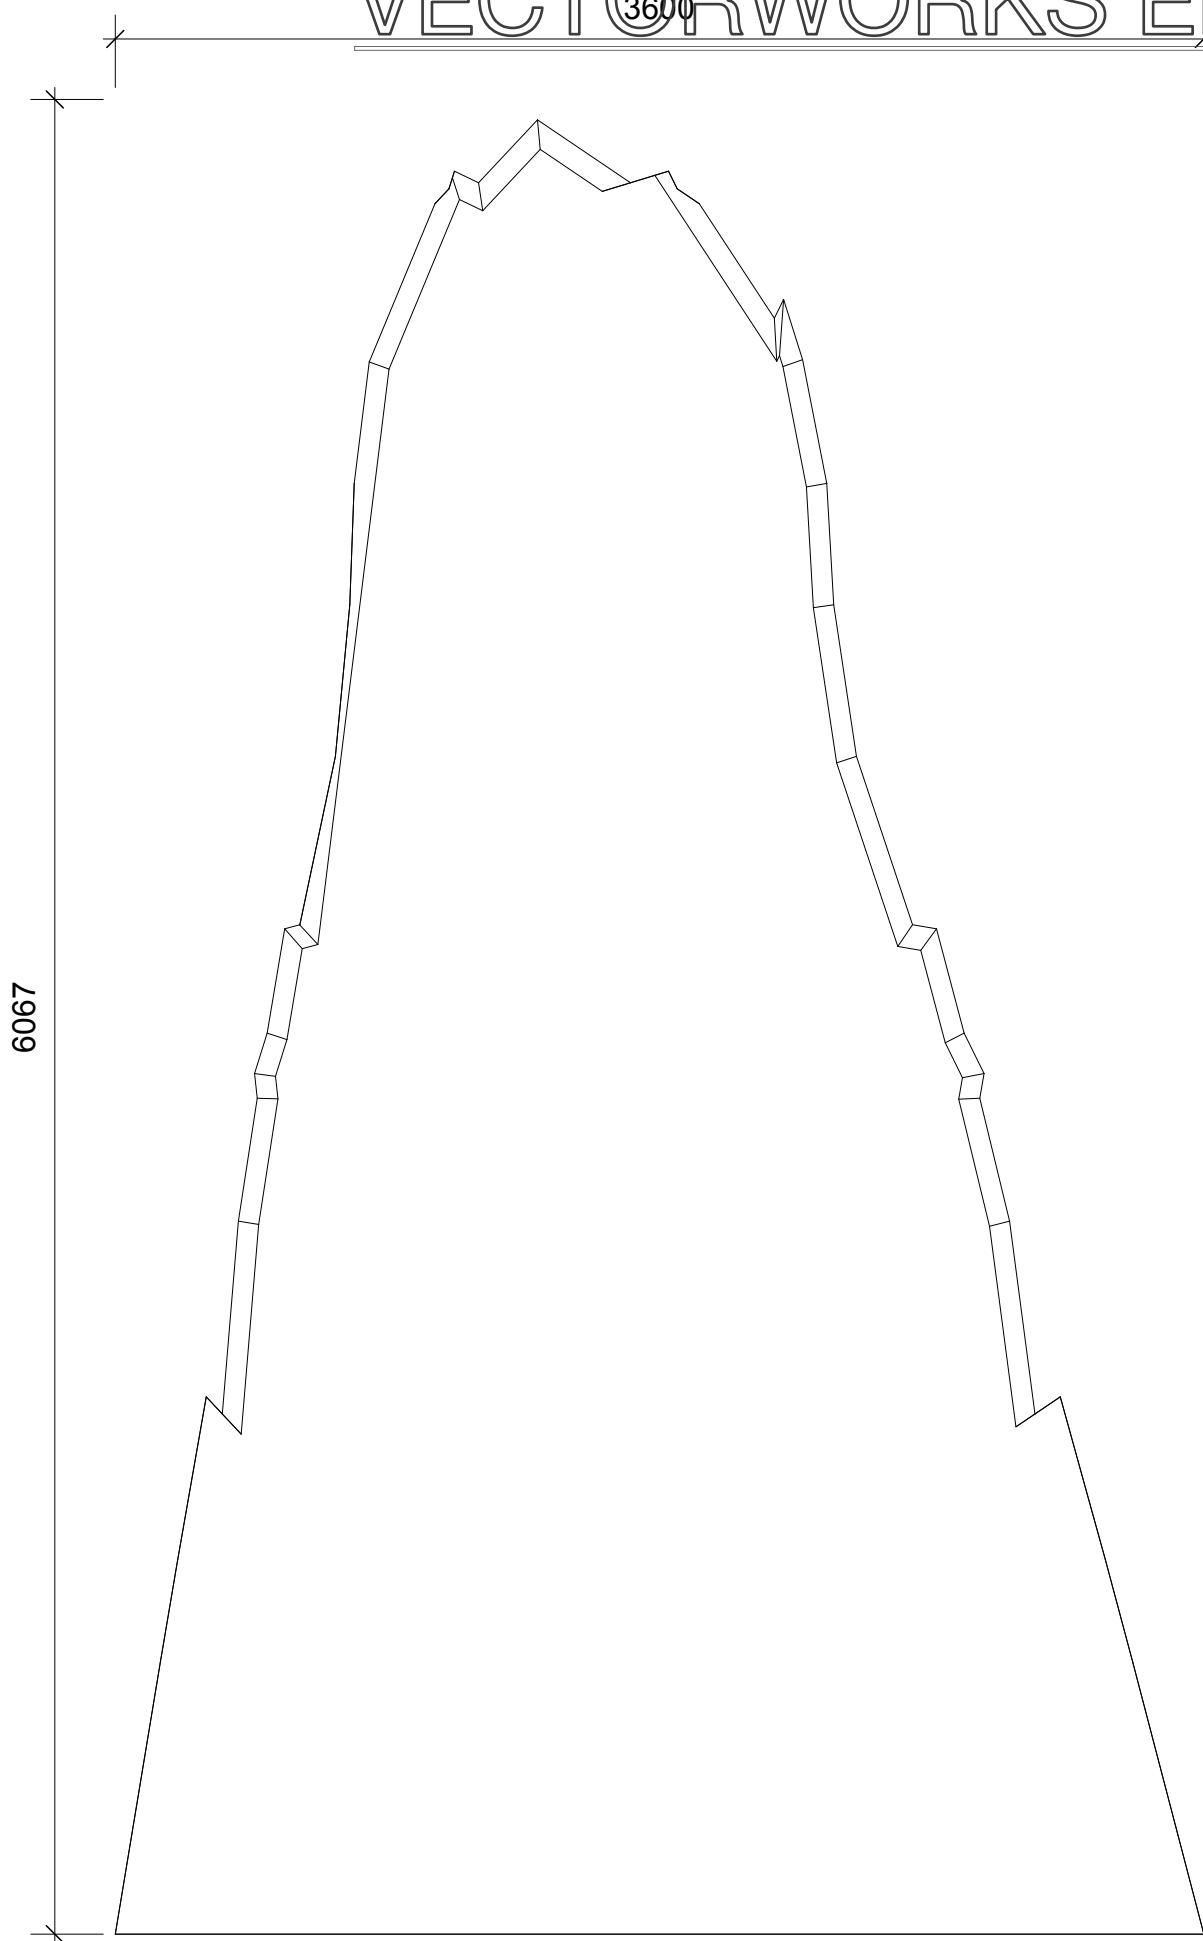


02 Mountain Layer 2
Scale 1:25

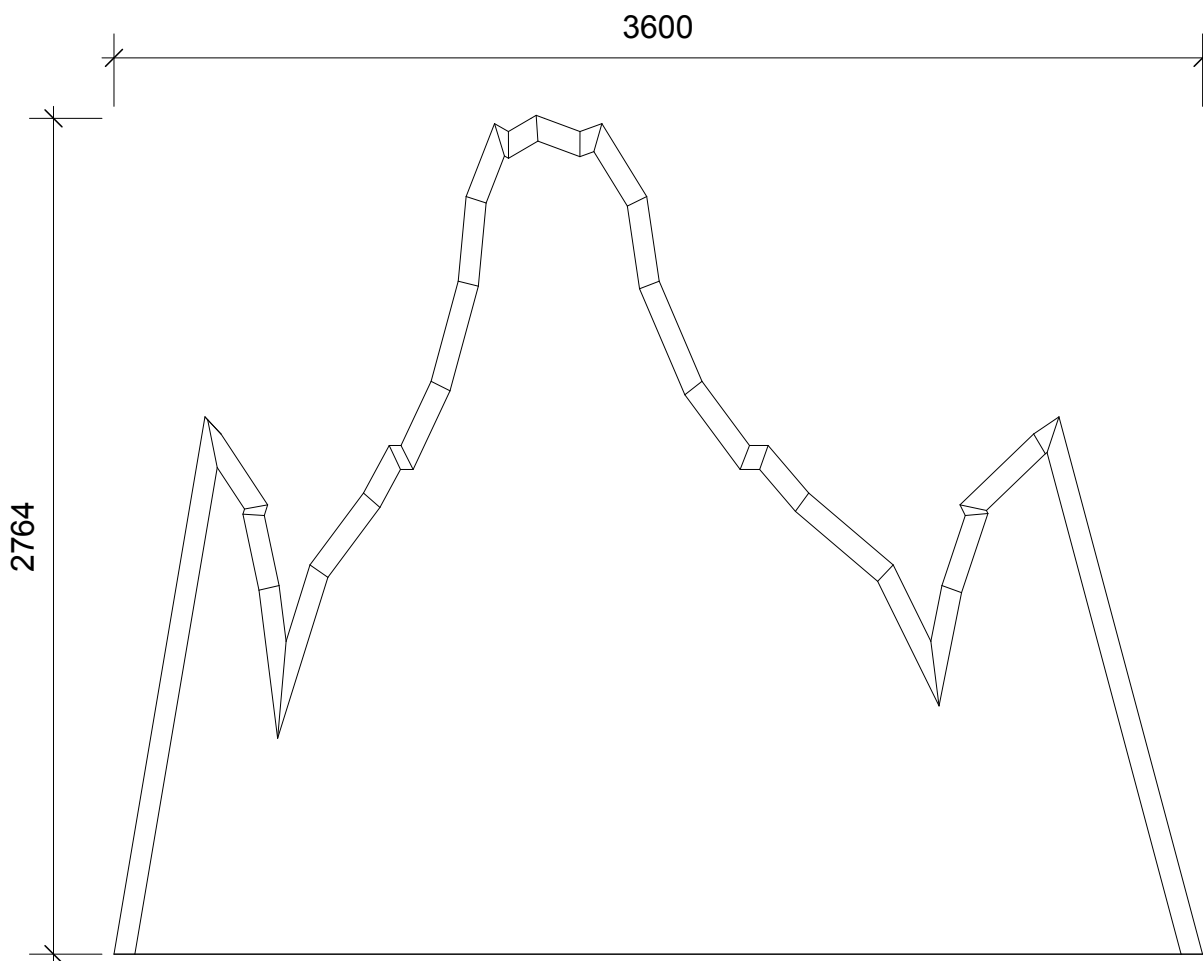


03 Mountain Layer 3
Scale 1:25

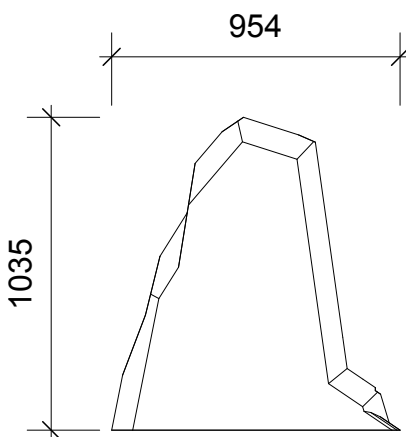


04 Mountain Layer 4
Scale 1:25

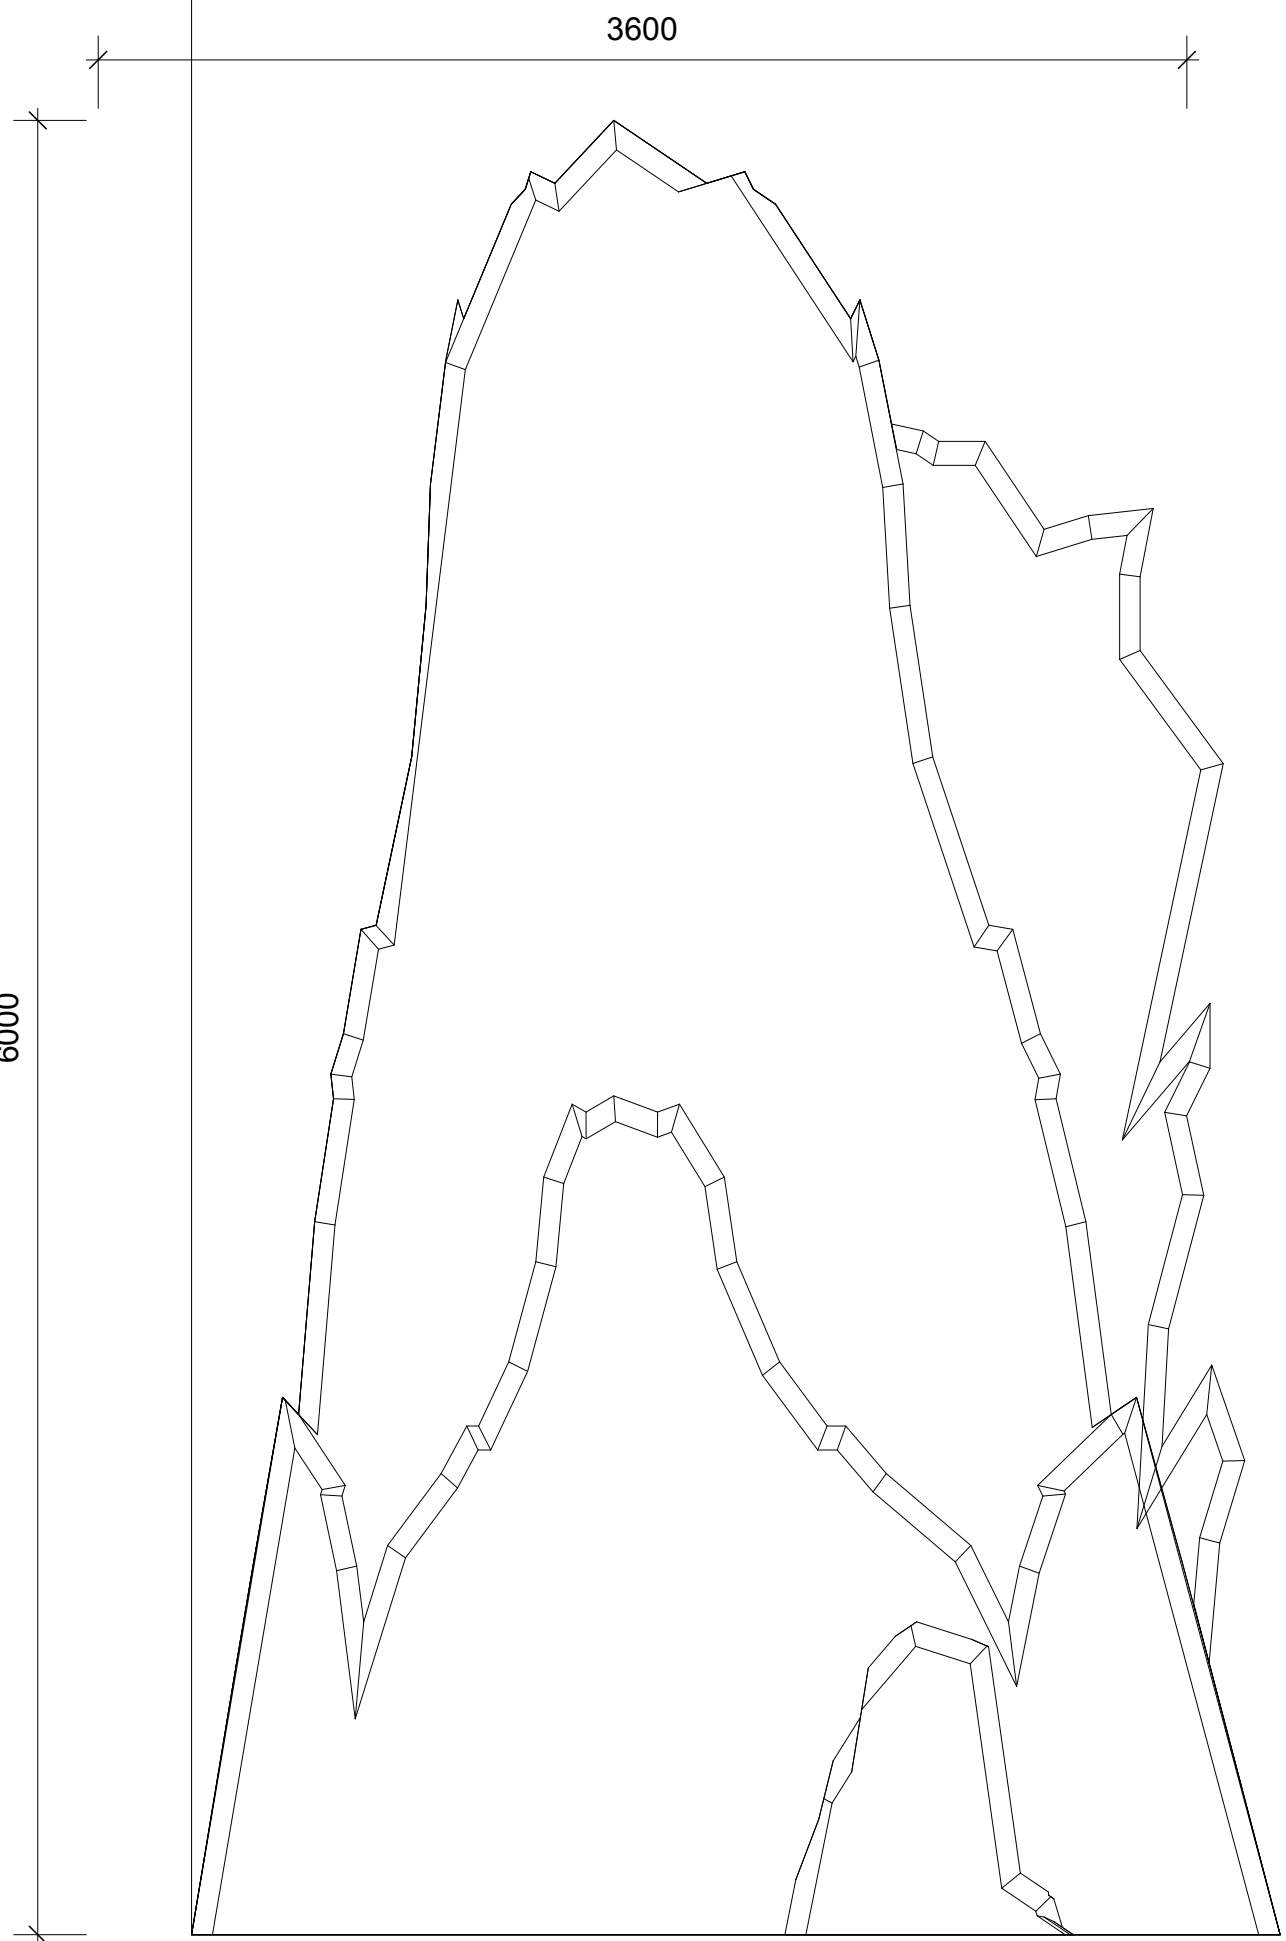


05 Mountain 1 Front
Scale 1:25

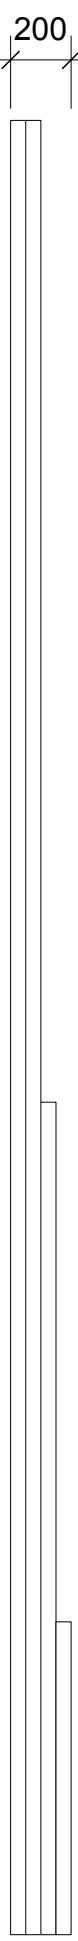

06 Mountain Side
Scale 1:25

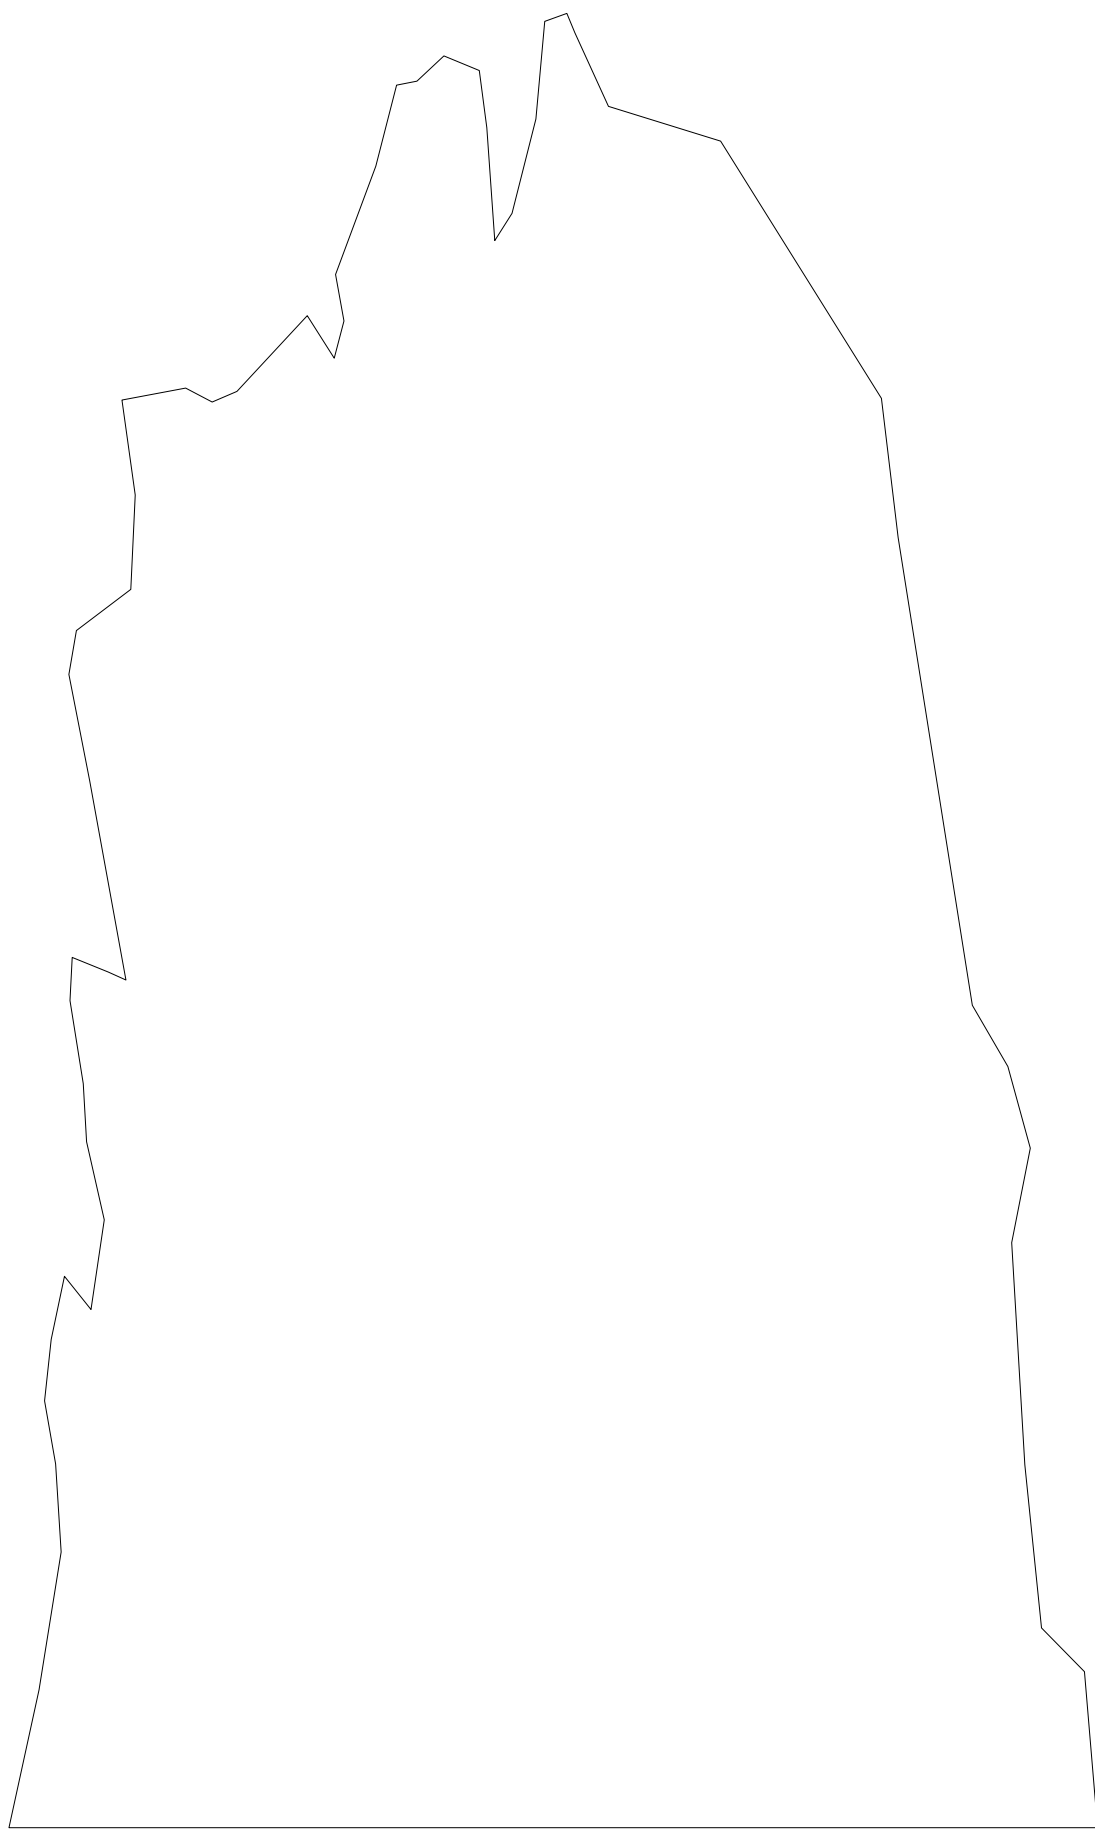

07 Mountain 2 Front Profile
Scale 1:25

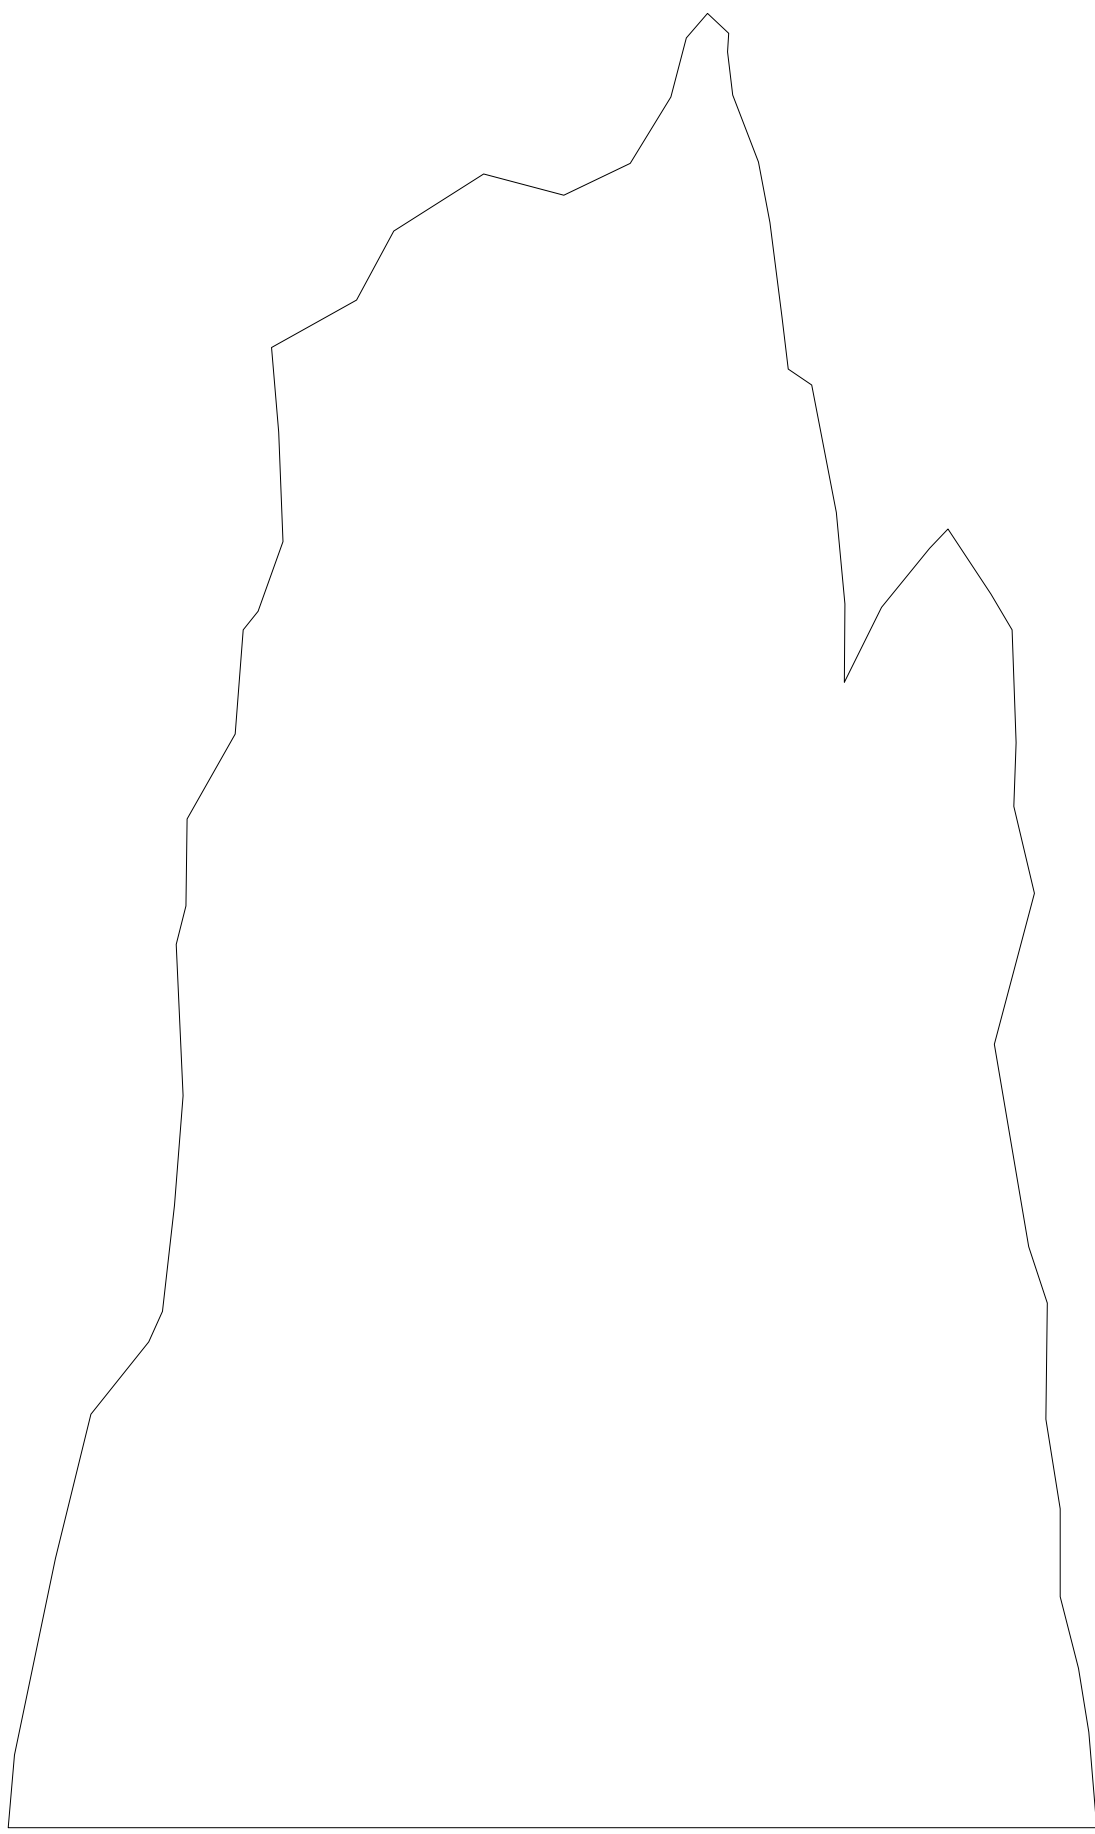


08 Mountain 3 Front Profile
Scale 1:25

Ice Mountains are made of 4x layers of a 50mm carvable material. More thickness ideal pending on cost/space in venue.


x3 Ice Mountains

All Ice Mountains to look slightly different.


Frozen	
Stoddart Entertainment Group	
Civic Theatre Newcastle	
Ice Mountains Detail	
DATE:	12/07/2026
BY:	12/07/2026
1:25 @ A1	12/07/2026
07 of 26	
8.0	

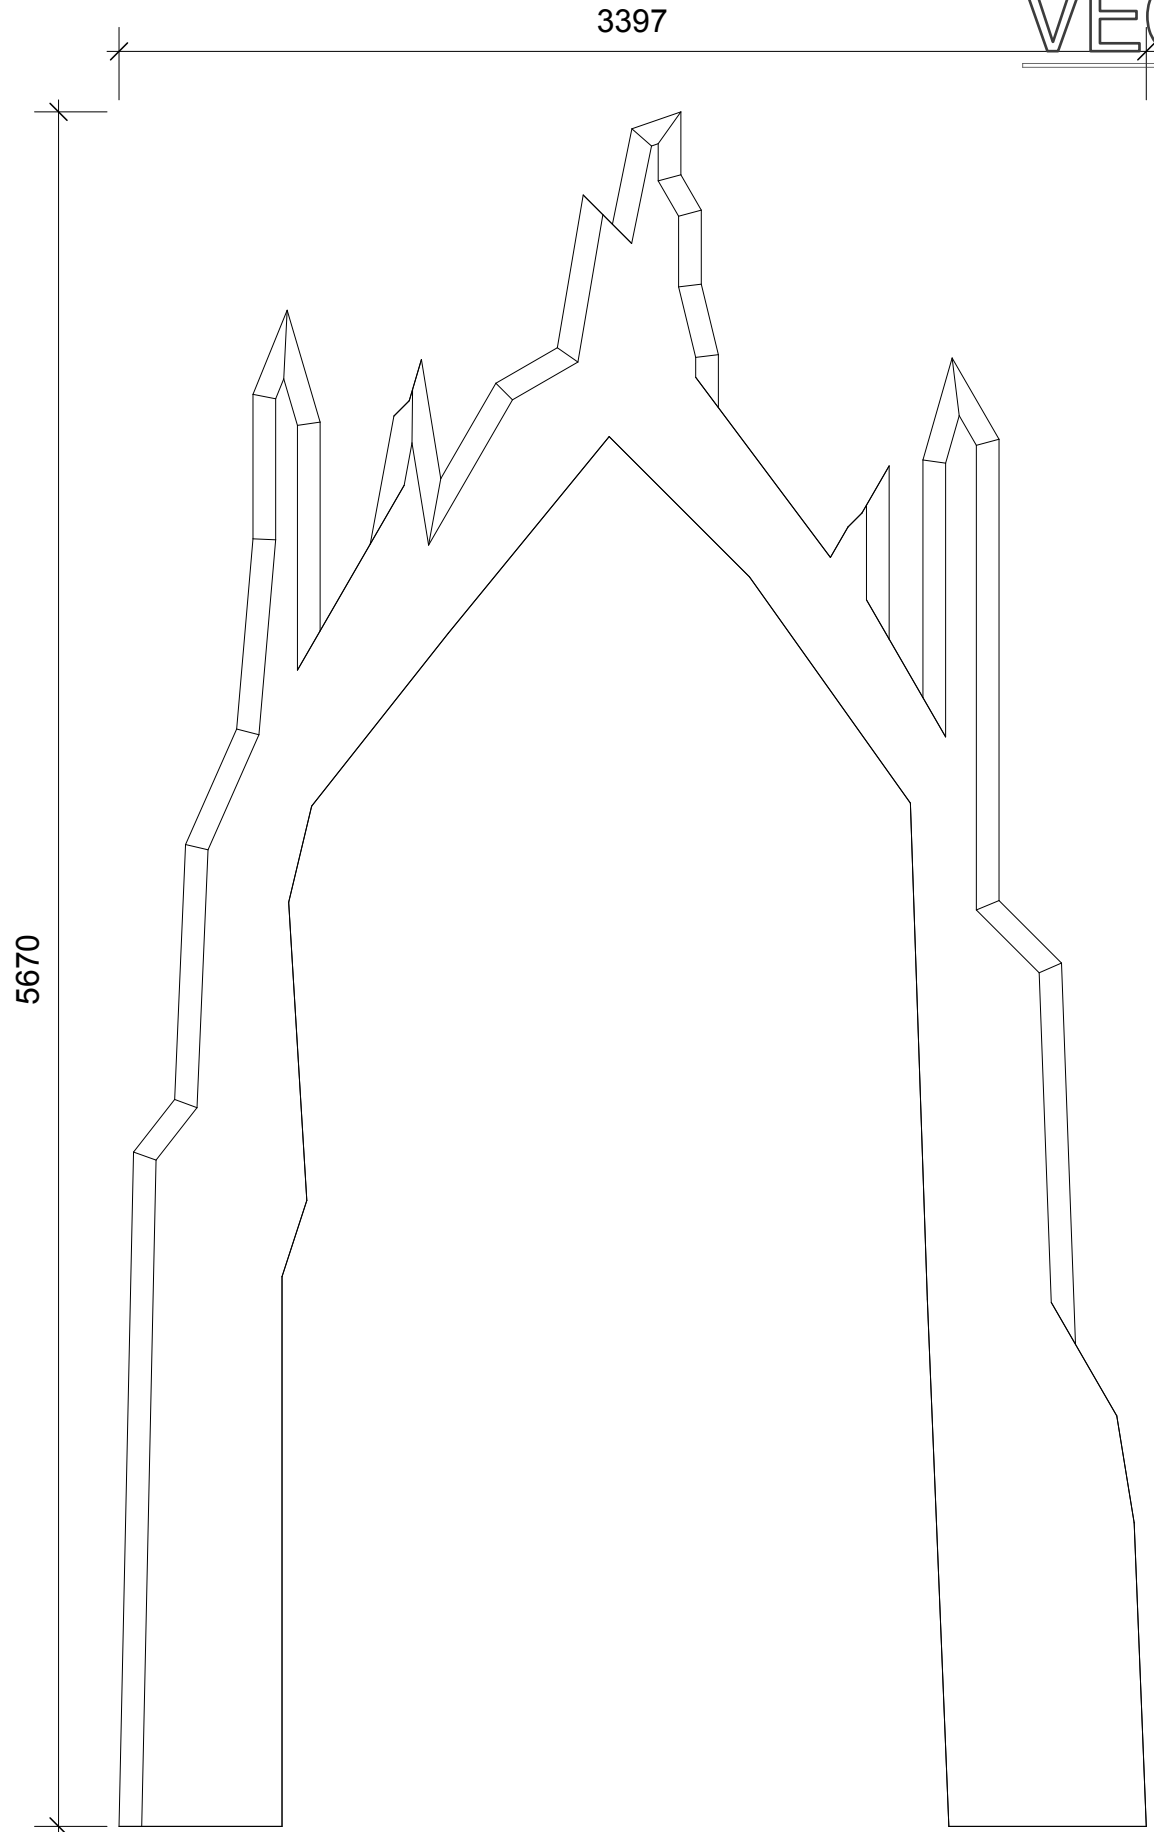



01 Ice Palace Layer 1
Scale 1:25

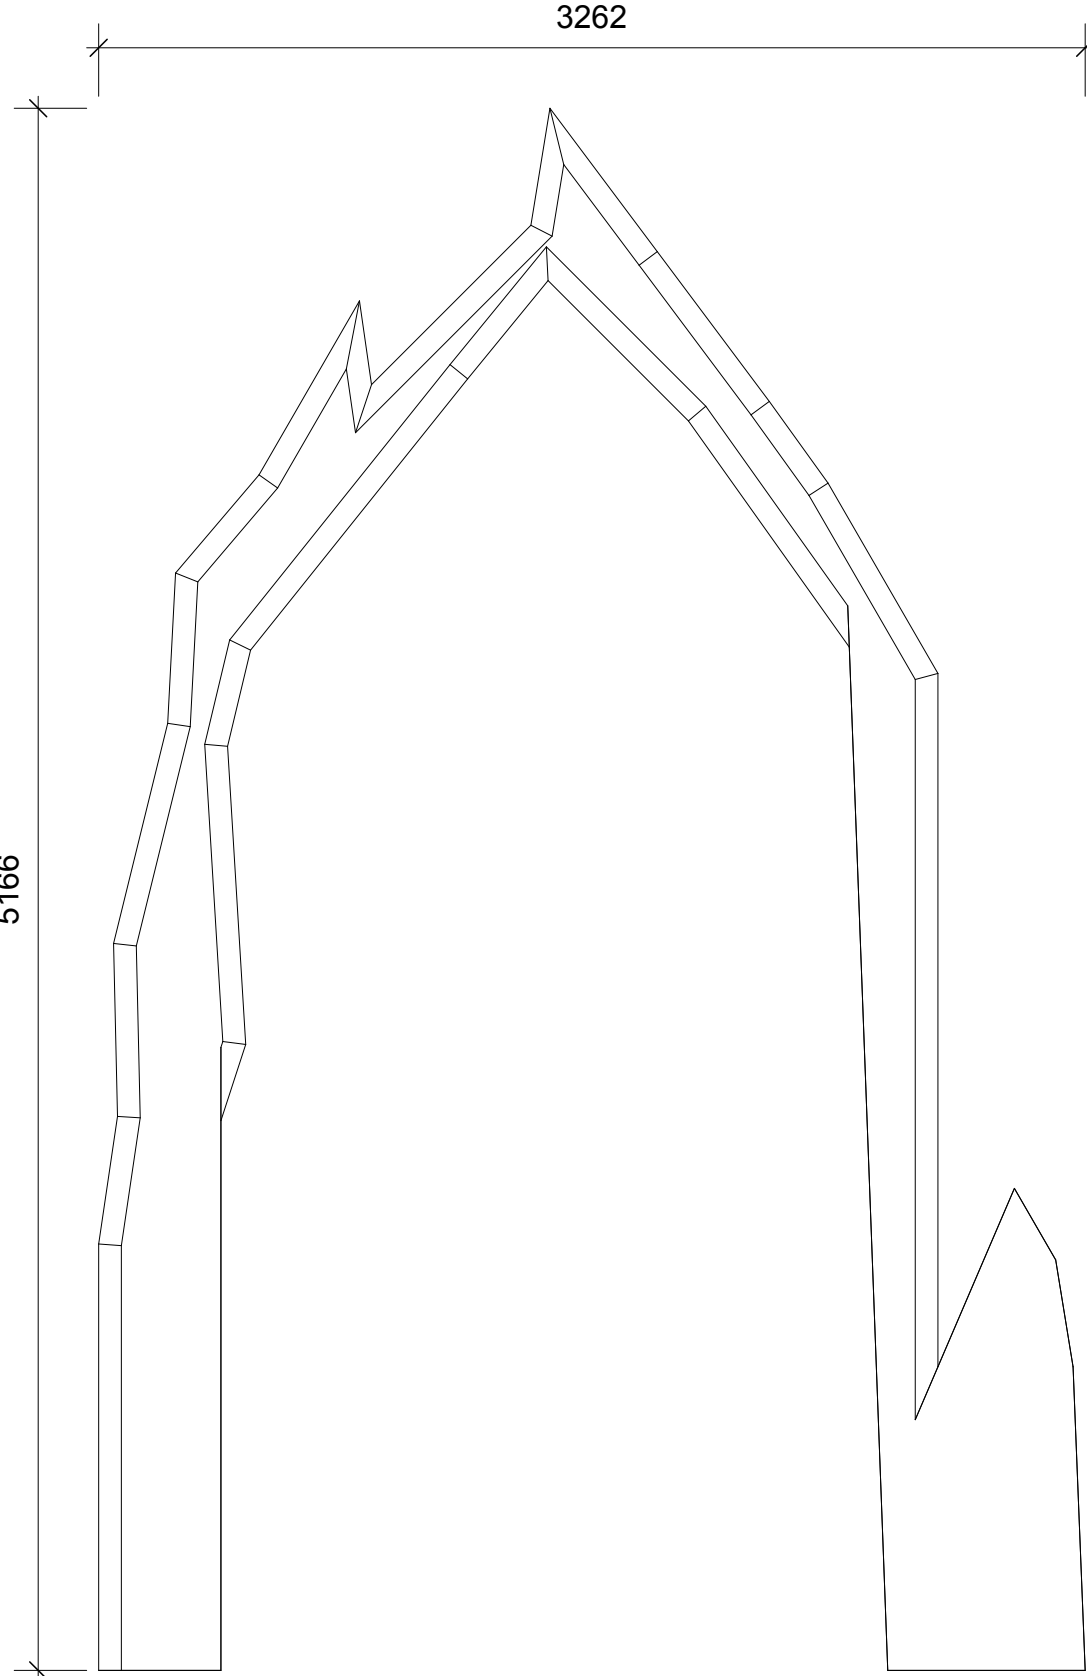


02 Ice Palace Layer 2
Scale 1:25

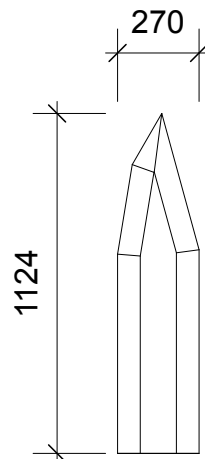

03 Ice Palace Layer 3
Scale 1:25

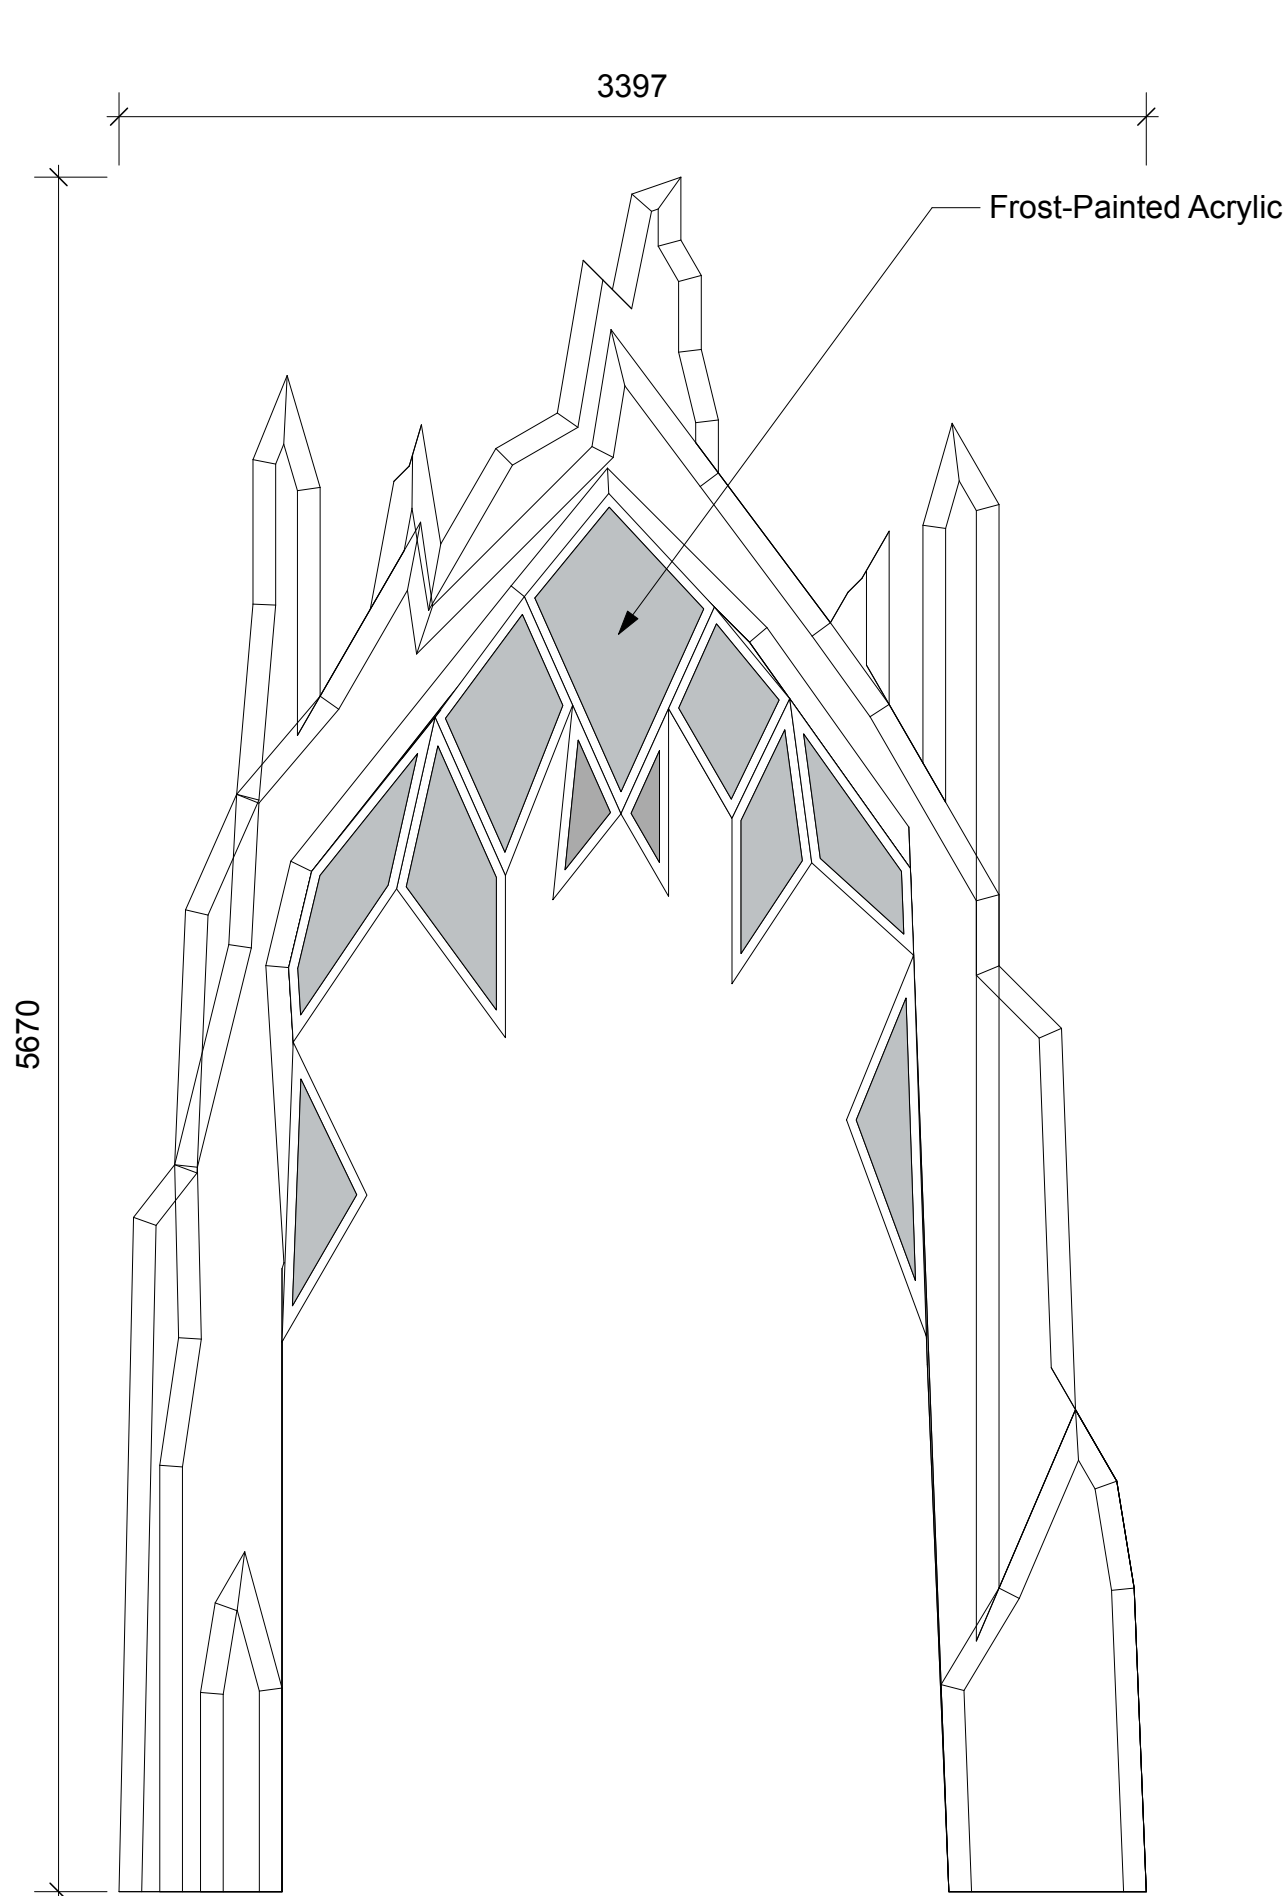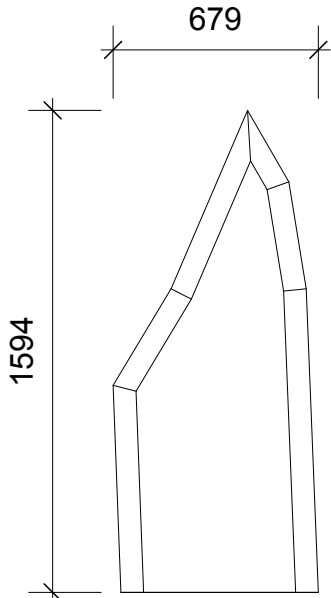

04 Ice Palace Front
Scale 1:25

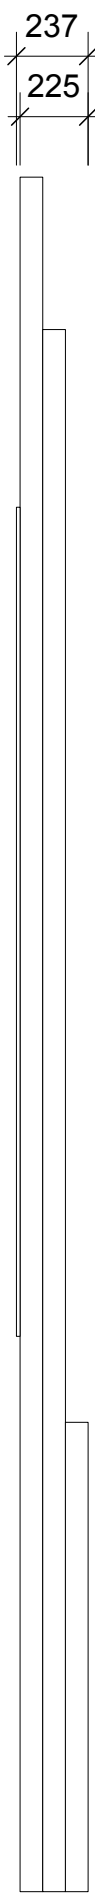


04 Ice Palace Front
Scale 1:25

Elsa's Ice Palace is made of 3x layers of 75mm thick material.


Layer thickness can change based on materials used.

Ice Stained Glass should have a more organic feel than as drawn.


Frozen	
Stoddart Entertainment Group	
Civic Theatre Newcastle	
Elsa Ice Palace Centre Detail	
DATE:	12/06/2026
BY:	12/06/2026
FOR:	12/06/2026
1:25 @ A1	12/06/2026
08 of 26	08 of 26
8.0	8.0

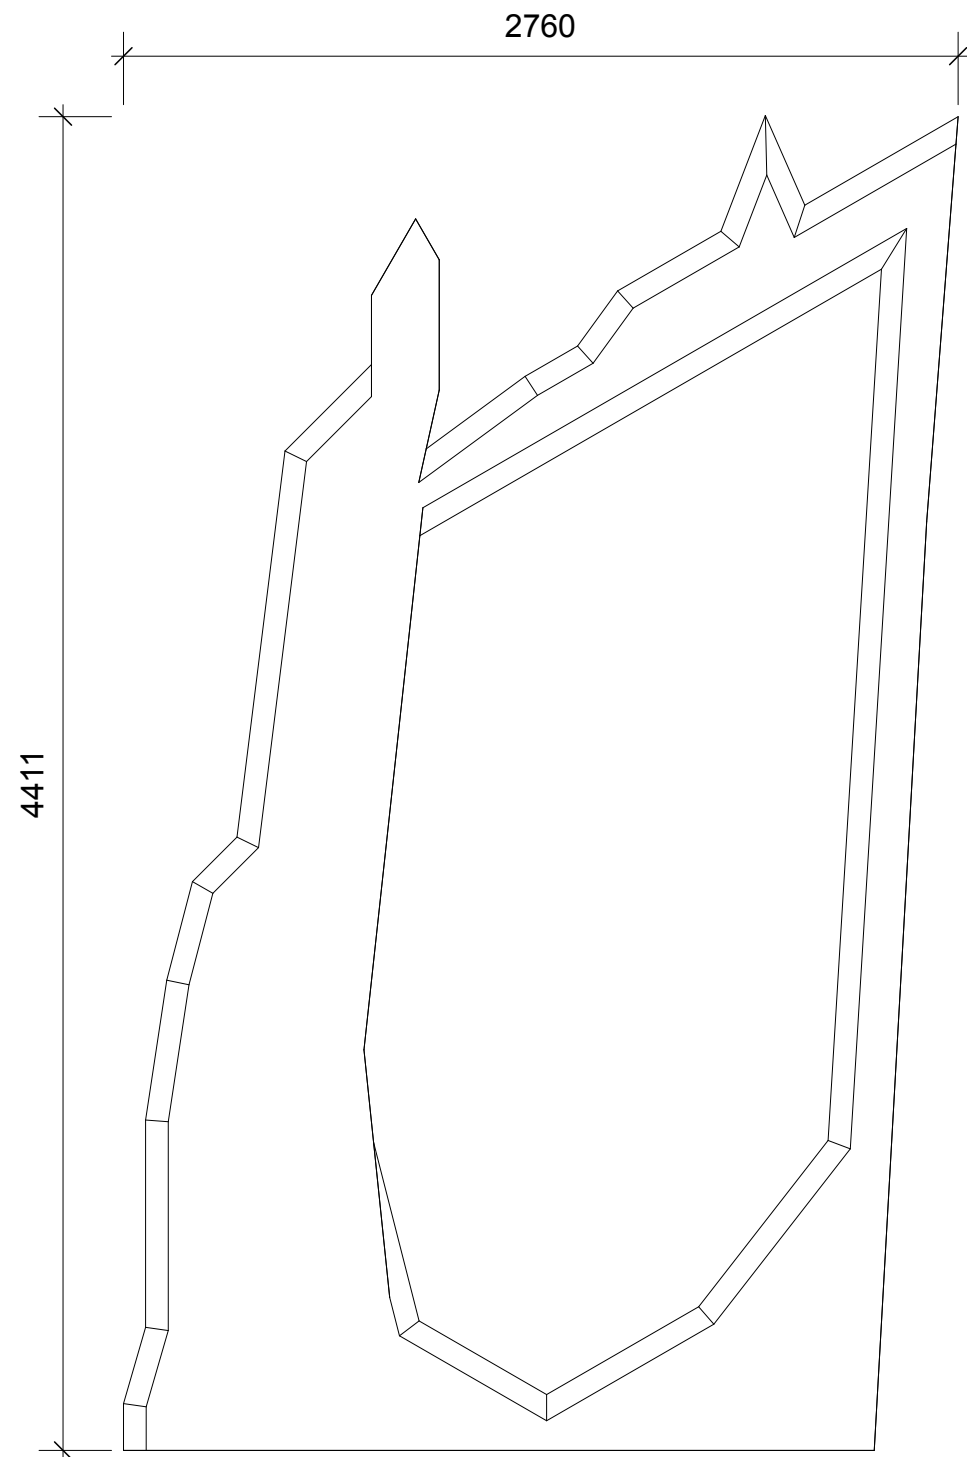


01 Ice Palace OP Layer 1
Scale 1:25

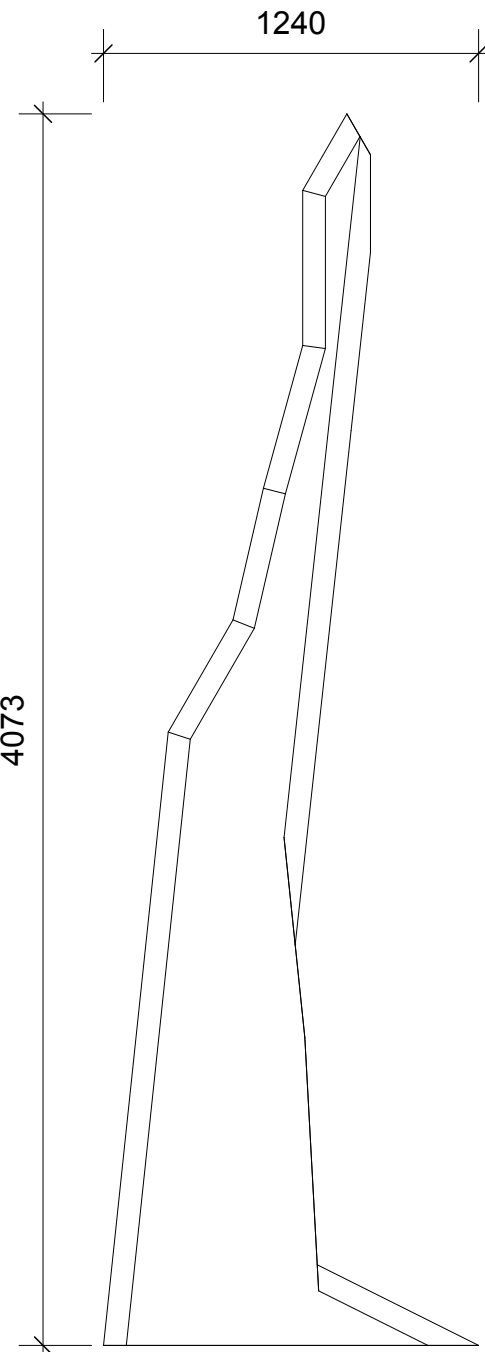


02 Ice Palace OP Layer 2
Scale 1:25

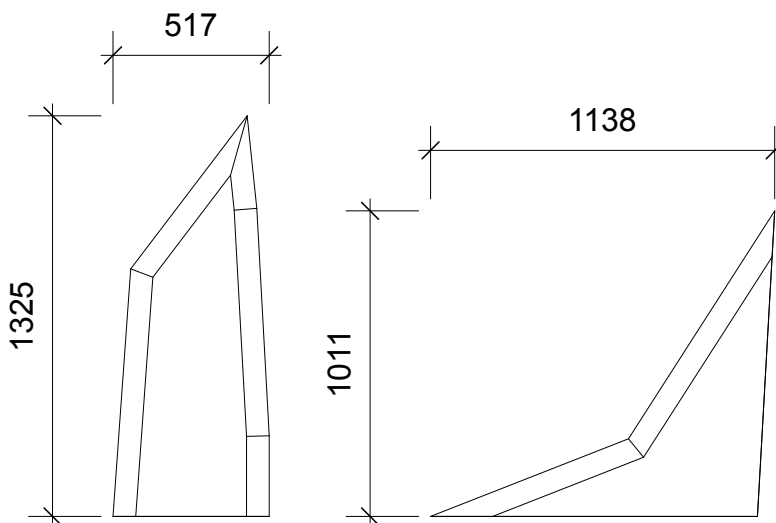


03 Ice Palace OP Layer 3
Scale 1:25

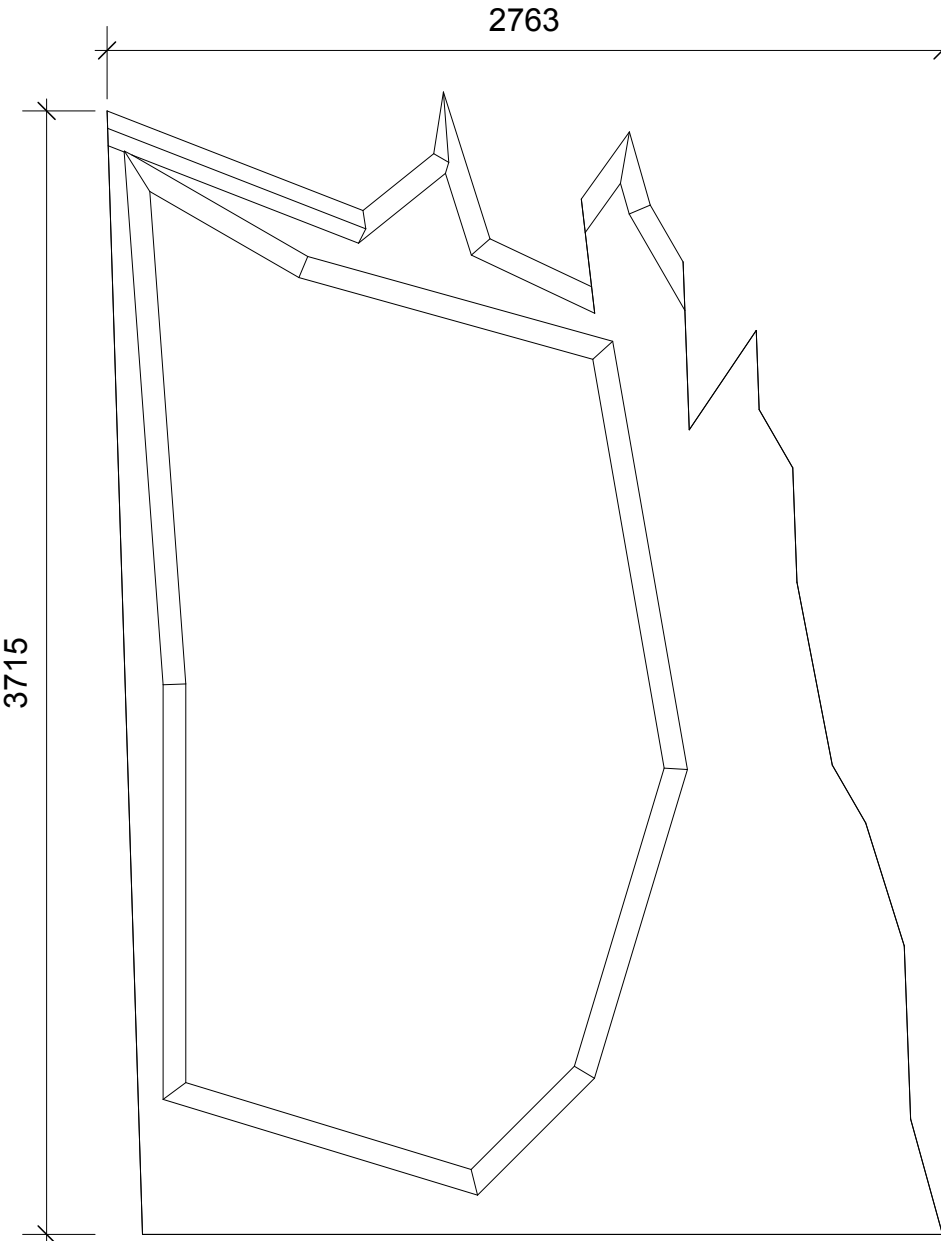


06 Ice Palace PS Layer 1
Scale 1:25

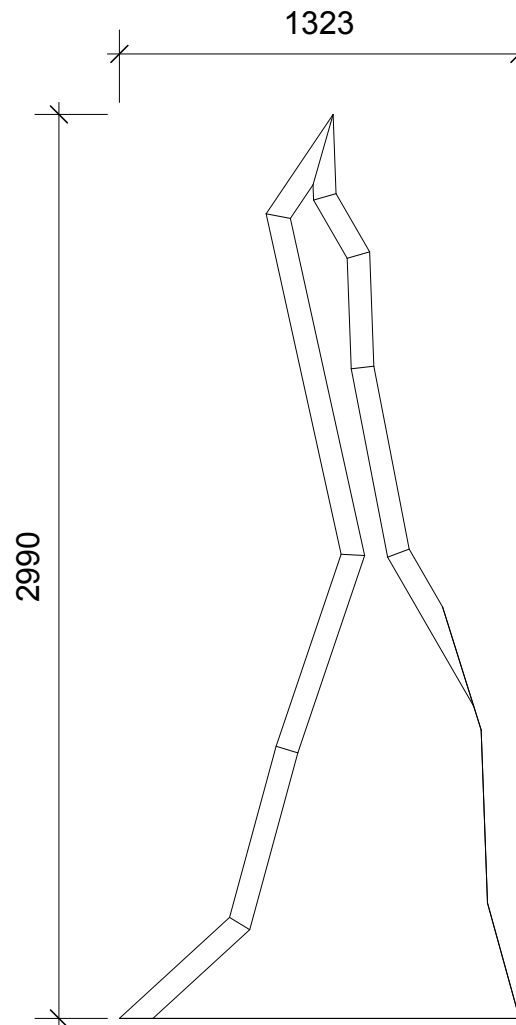


07 Ice Palace PS Layer 2
Scale 1:25

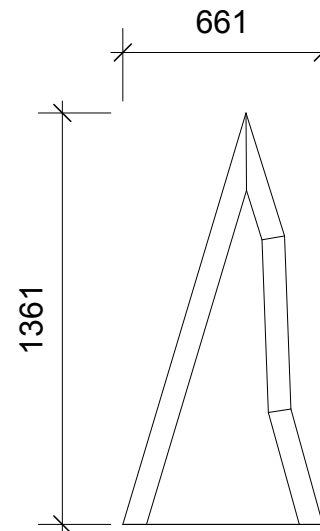


08 Ice Palace PS Layer 3
Scale 1:25

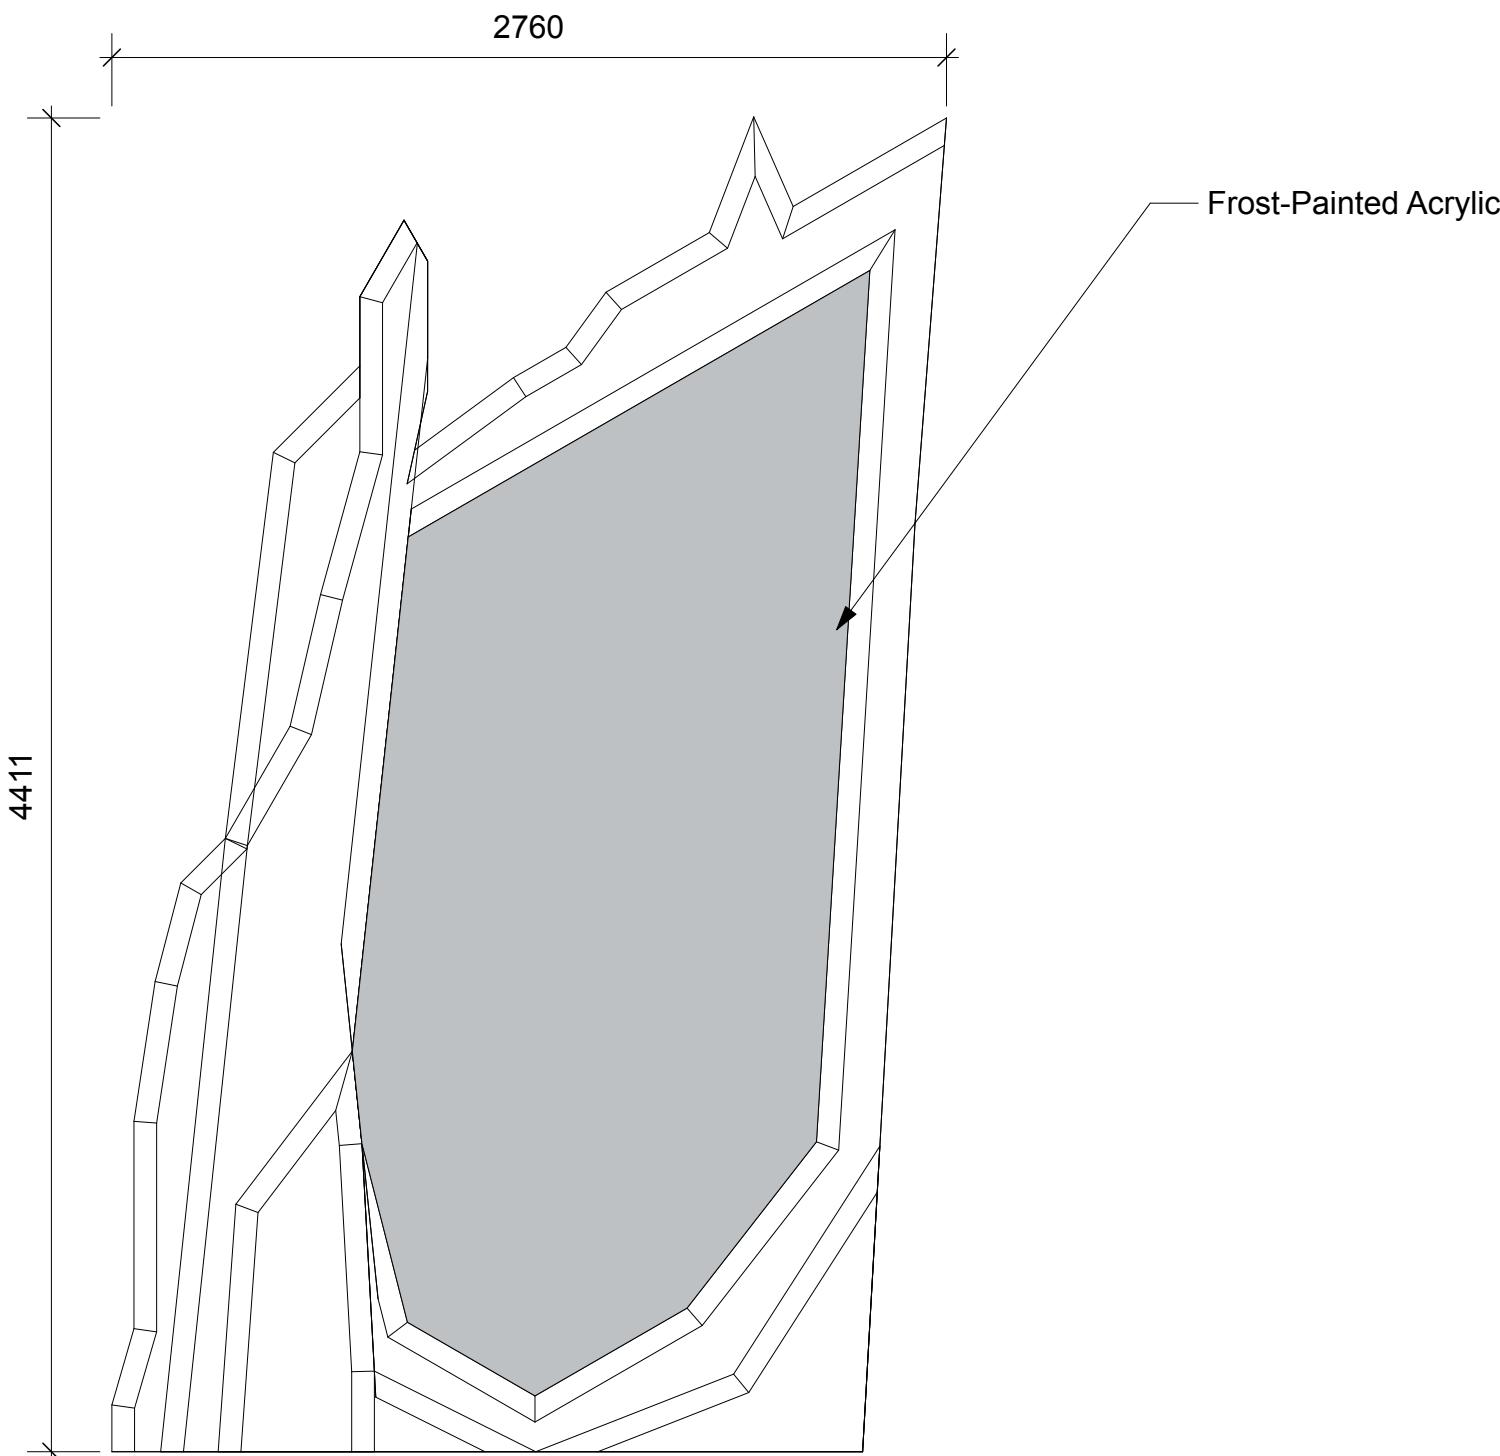


04 Ice Palace OP Front
Scale 1:25

 

05 Ice Palace OP Side
Scale 1:25

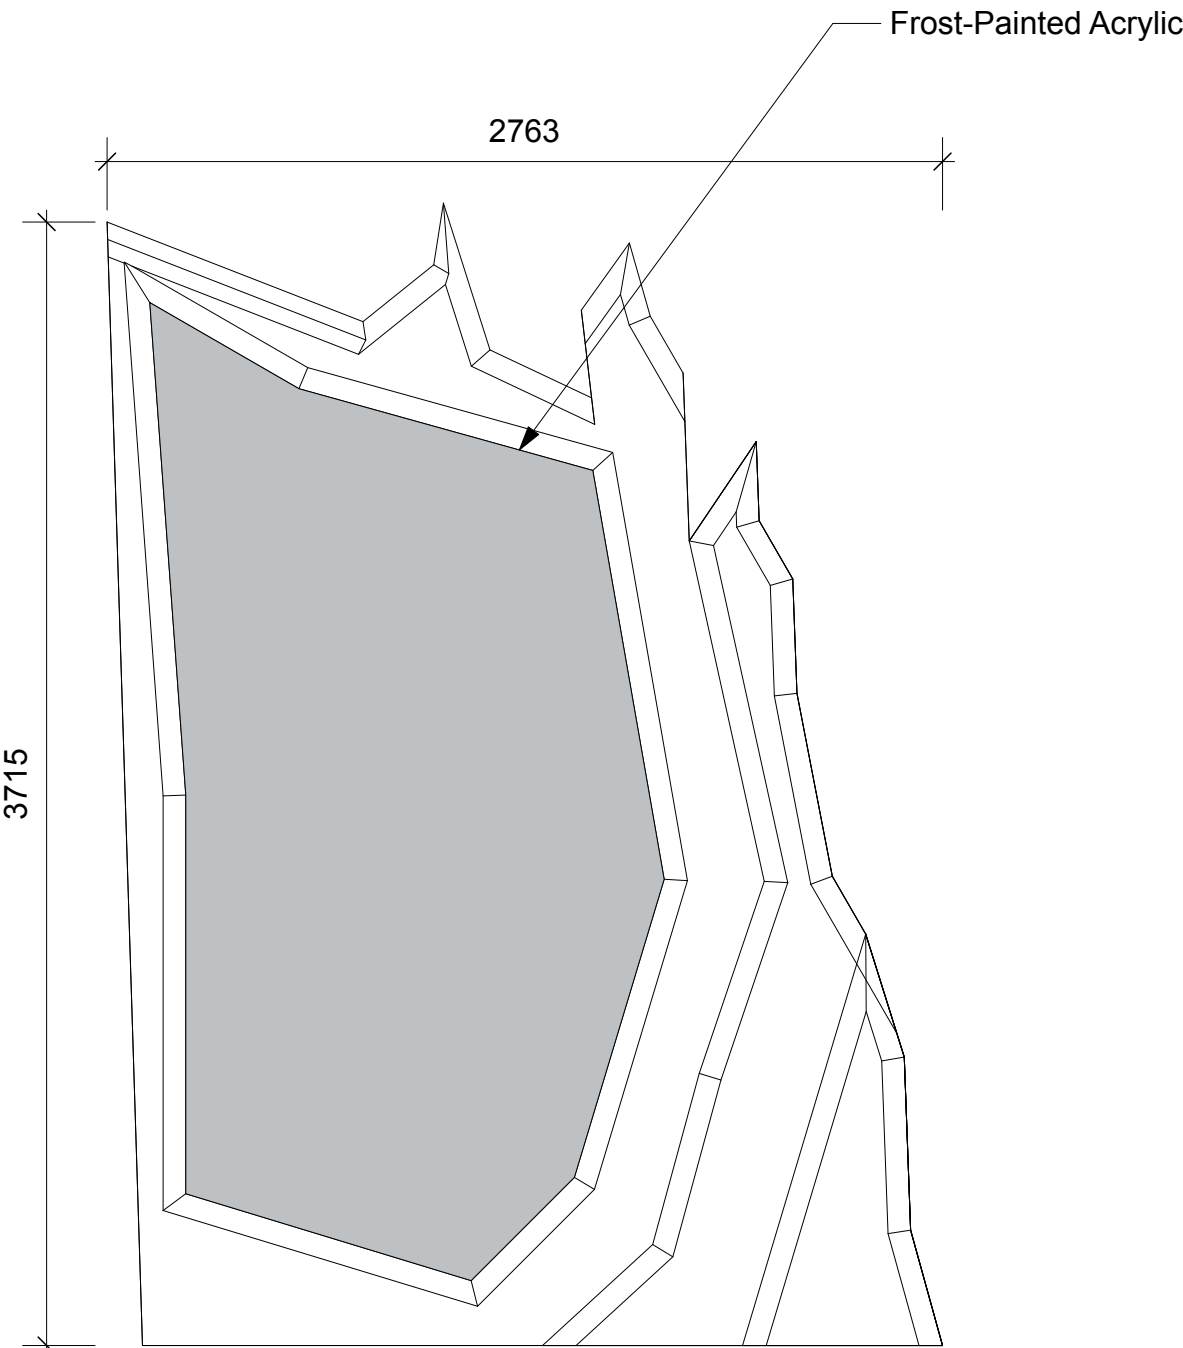

09 Ice Palace PS Front
Scale 1:25

 


10 Ice Palace PS Side
Scale 1:25


Elsa's Ice Palace is made of 3x layers of 75mm thick material.

Layer thickness can change based on materials used.


Frozen	
Stoddart Entertainment Group	
Civic Theatre Newcastle	
Elsa Ice Palace Sides Detail	
DATE:	12/07/2026
BY:	12/07/2026
FOR:	12/07/2026
1:25 @ A1	12/07/2026
09 of 26	
8.0	

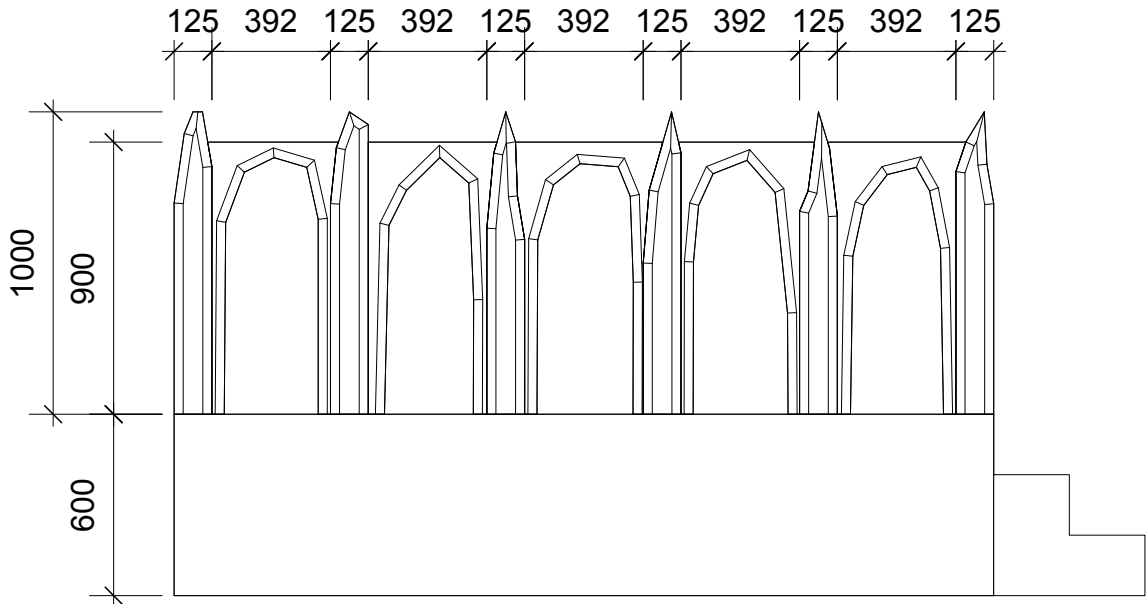


02 Staircase Piece 2 Front
Scale 1:25

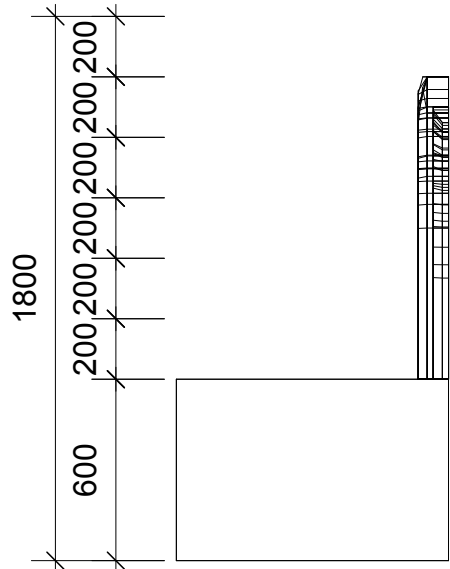


06 Staircase Piece 2 Side
Scale 1:25

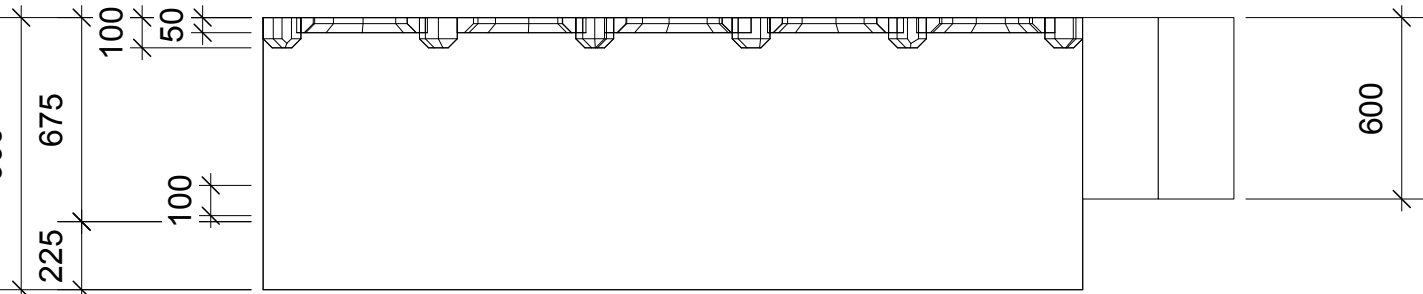


04 Staircase Piece 2 Top
Scale 1:25

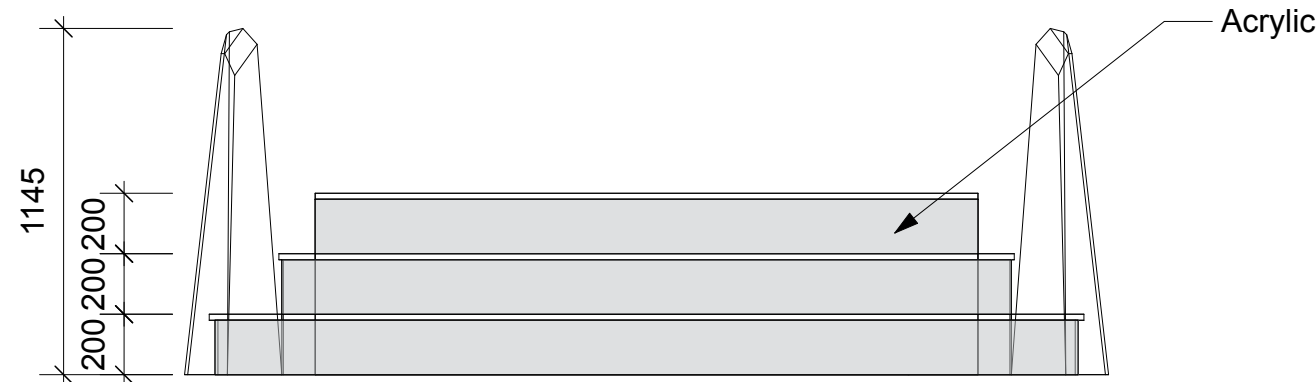


02 Staircase Piece 1 Front
Scale 1:25

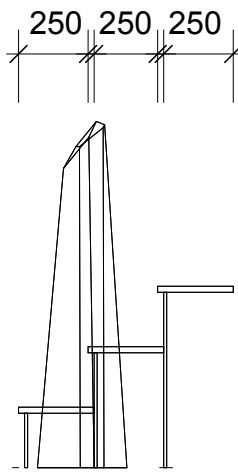

03 Staircase Piece 1 Side
Scale 1:25

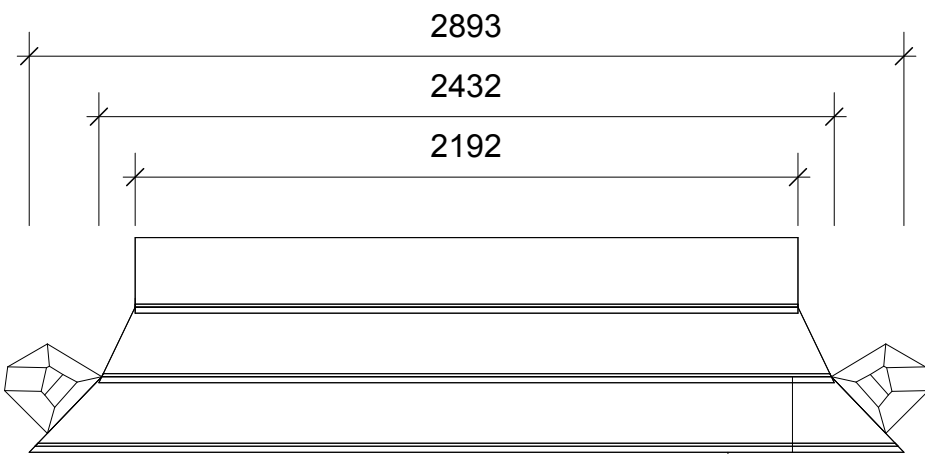

01 Staircase Piece 1 Top
Scale 1:25

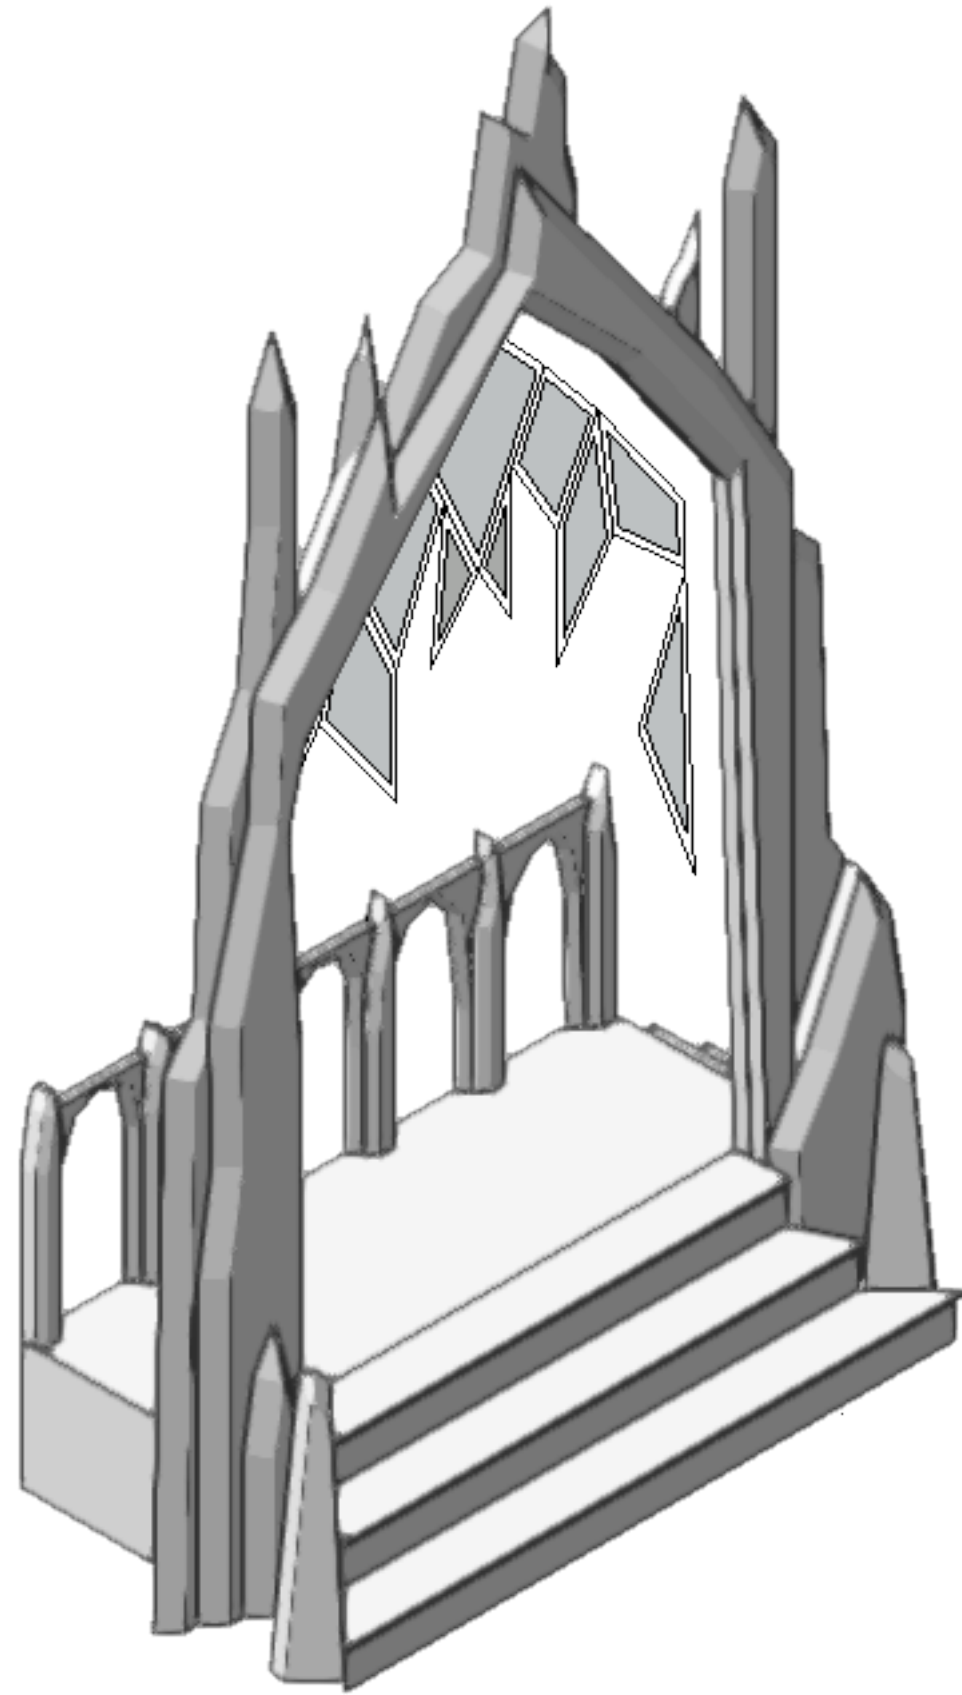


Staircase in 2 pieces.


Escape stairs required for off-stage exit/entrance.

Pieces trucked on


Frozen	
FOURWAY:	Stoddart Entertainment Group
PRICE:	Civic Theatre Newcastle
TITLE:	Elsa Ice Palace Staircase Detail
DIRECTOR:	Malcolm Trevelyan
SET DESIGNER:	Harry Gill
LIGHTING DESIGNER:	Jack Kruse
SCALE:	DATE:
1:25 @ A1	12/07/2026
DRAWING NUMBER:	
10 of 26	
DESIGNED & DRAWN BY:	CHECKED:
Harry Gill	Harry Gill
VERSION:	DATE:
3.0	2026.02.02

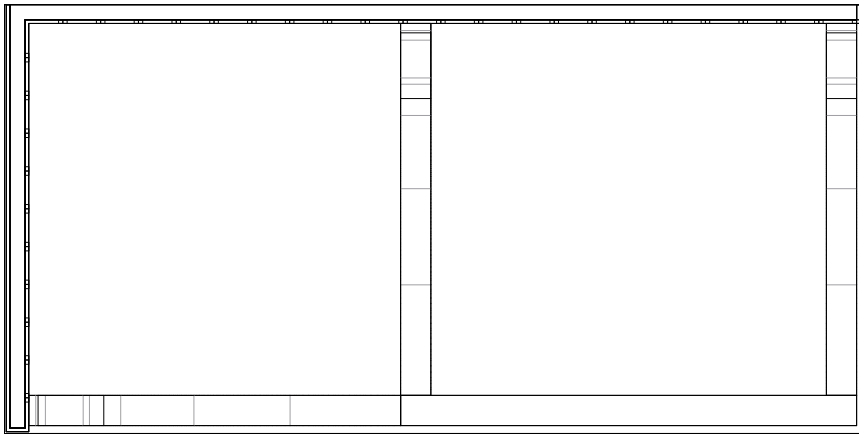


04 **Bedrom Top**
Scale 1:25

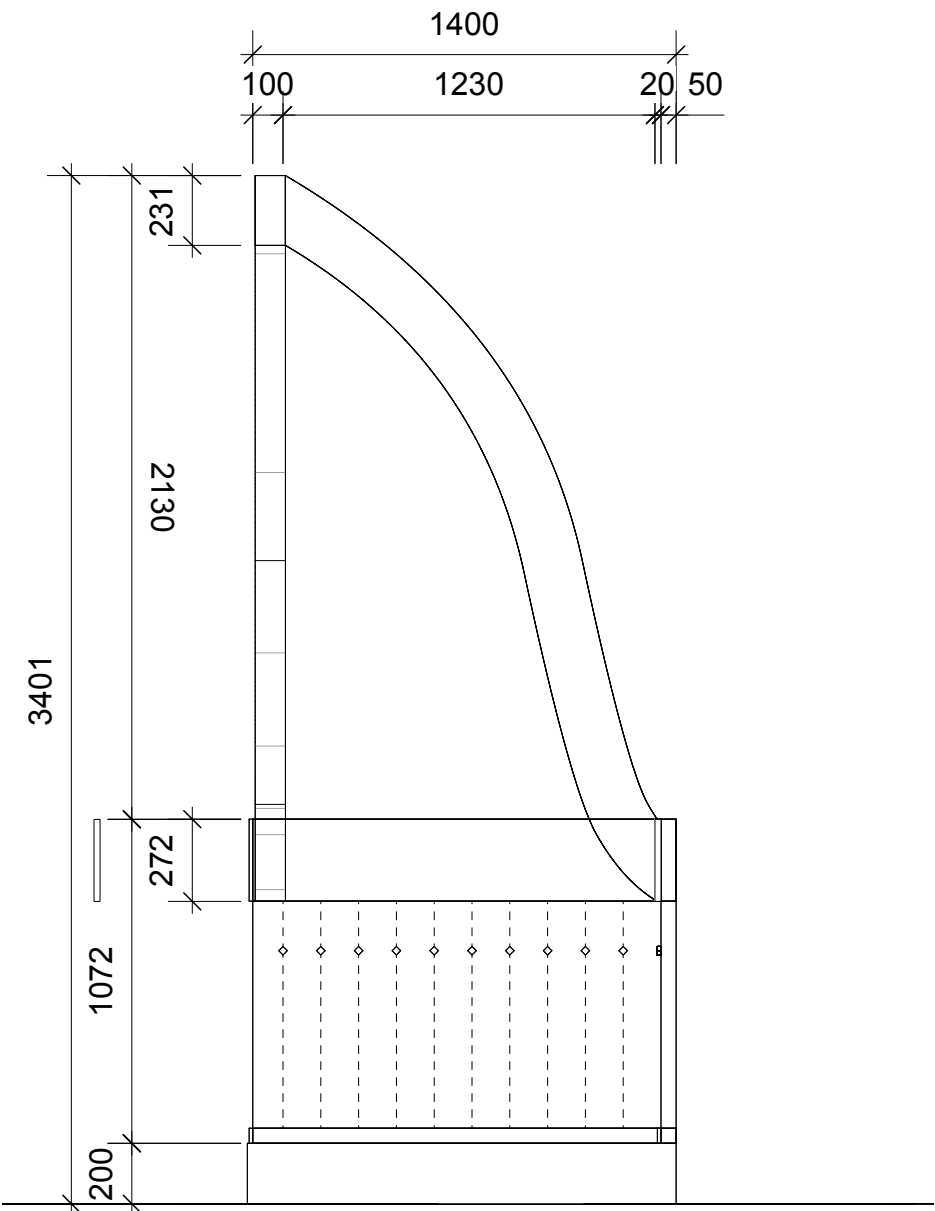

02 **Bedrom Side (Internal)**
Scale 1:25

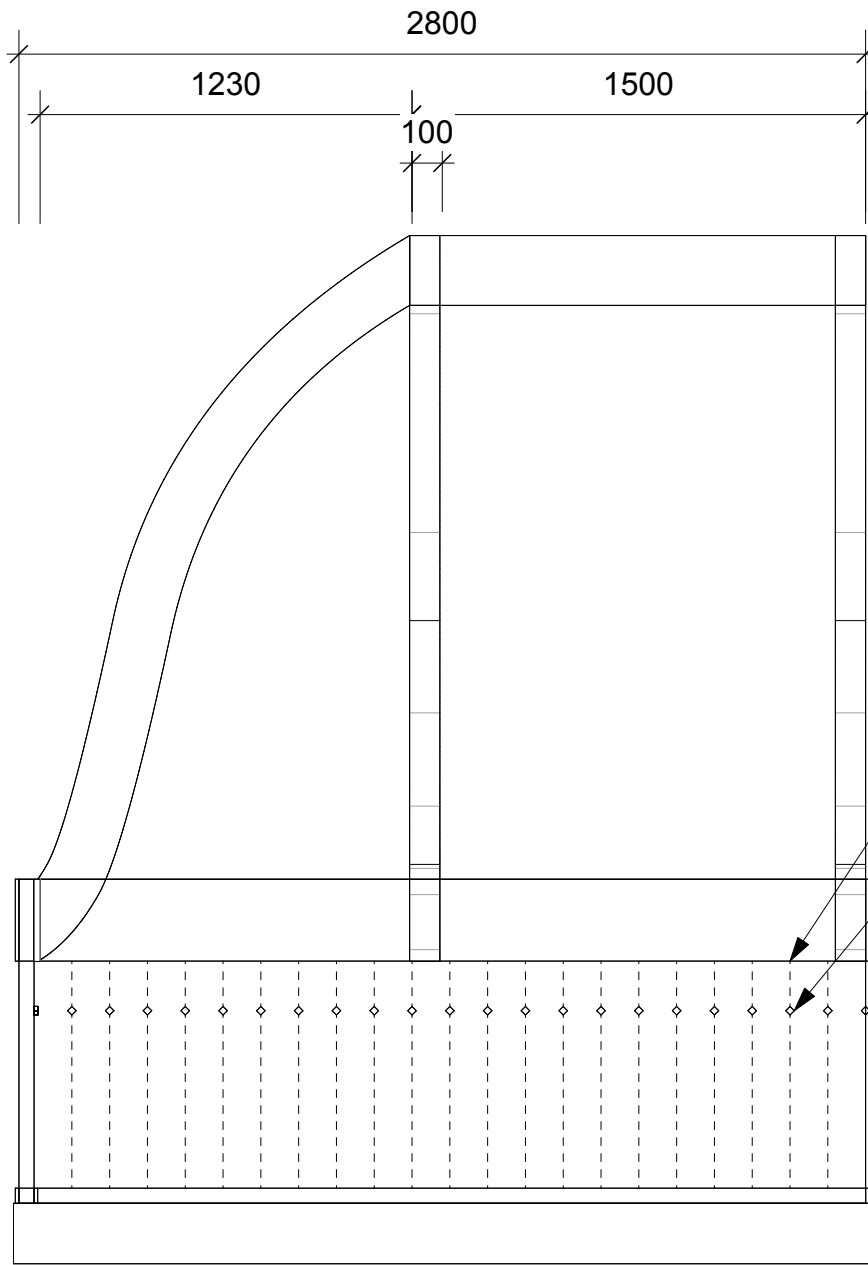

01 **Bedrom Front**
Scale 1:25

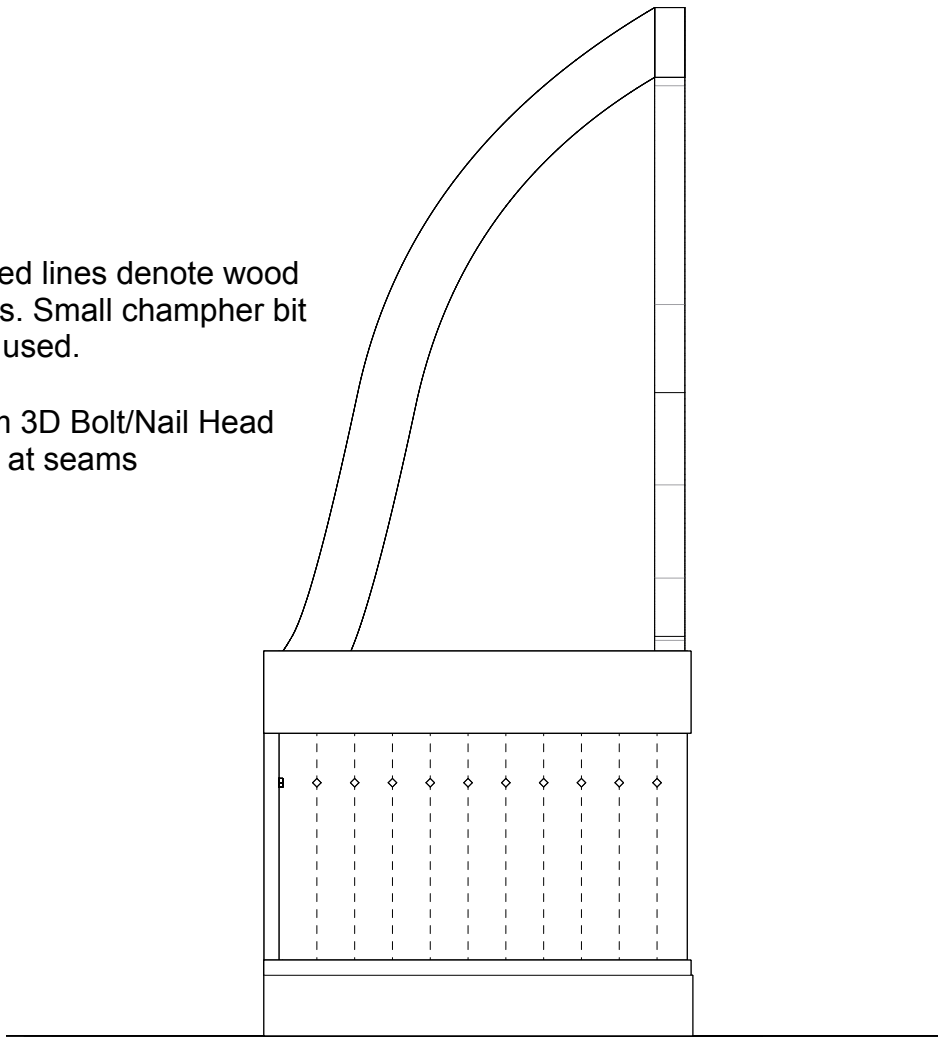


03 **Bedrom Side (External)**
Scale 1:25

x2 Bed Trucks Mirrored

50mm wall thickness allowed.

Both inside and outside of side wall to be finished, as will be seen as truck moves across stage.

Frozen	
FORWARD:	Stoddart Entertainment Group
PROJECT:	Civic Theatre Newcastle
TITLE:	Bedroom Truck Detail
DIRECTOR:	Melissa Trew-Kayworth
SET DESIGNER:	Harry Gill
LIGHTING DESIGNER:	Zach Kraske
SCALE:	DATE:
1:25 @ A2	12/07/2026
DRAWING NUMBER:	
11 of 26	
DESIGNED & DRAWN BY:	CONTACT:
Harry Gill	harry@harrygilldesigns.com
VERSION:	2026.02.02
3.0	

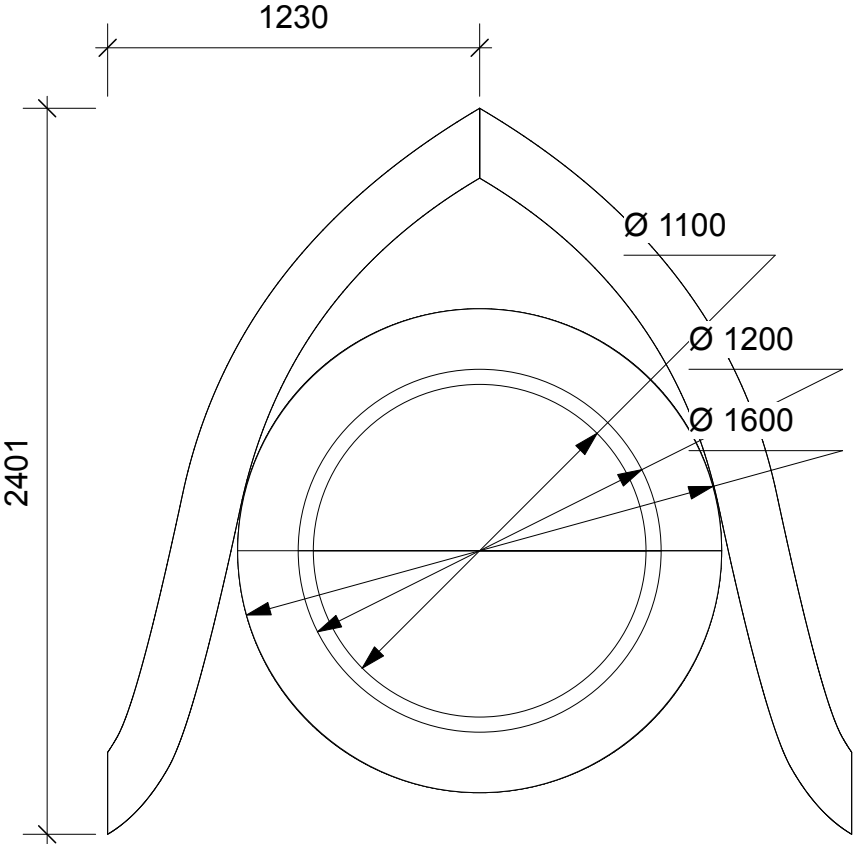

01

Bedrom Window Front

Scale 1:25



02

Bedrom Window Side

Scale 1:25

Frozen

COMPANY:
Stoddart Entertainment Group

VENUE:
Civic Theatre Newcastle

TITLE:
Bedroom Window

DIRECTOR: Madison Thew-Keyworth

SET DESIGNER: Harry Gill

LIGHTING DESIGNER: Zach Krause

SCALE: 1:25 @ A3 DATE: 12/07/2026


DRAWING NUMBER:

12 of 26


DESIGNED & DRAWN BY: CONTACT:

Harry Gill harry@harrygilldesigns.com
VERSION: 0631.002.447

3.0

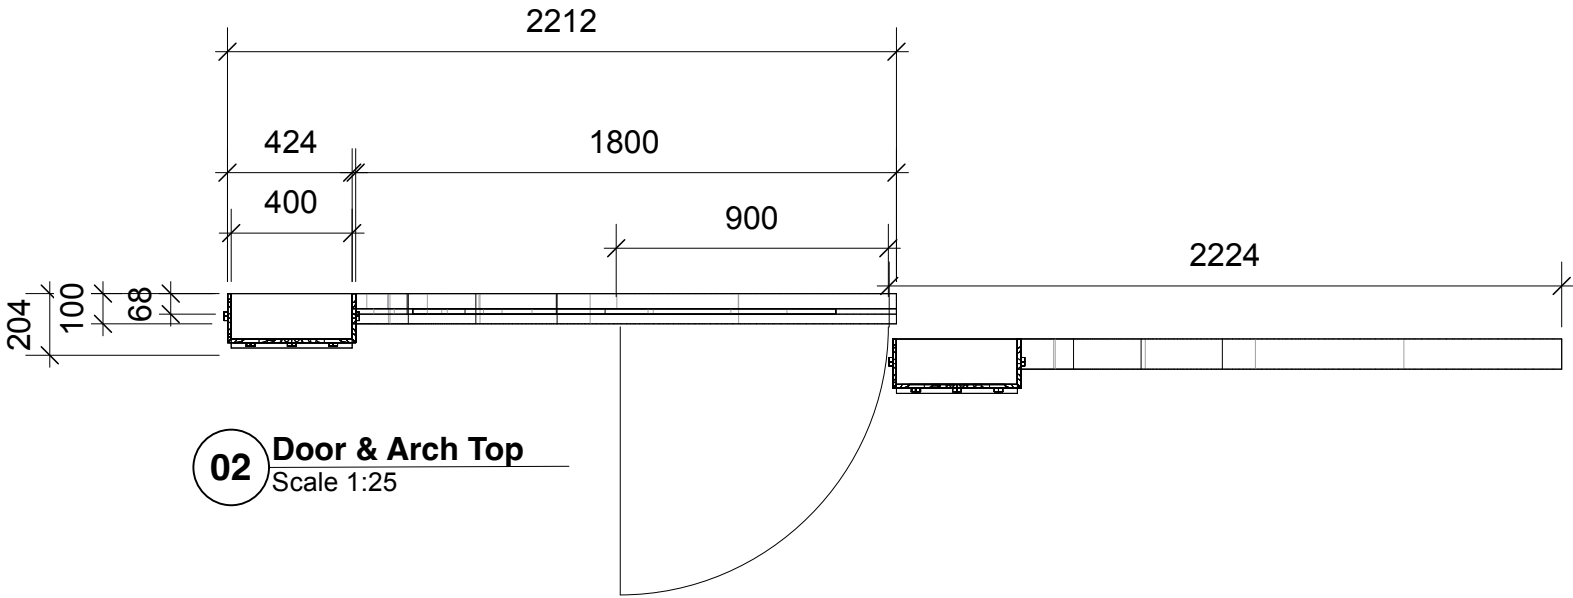

02 Door & Arch Top
Scale 1:25

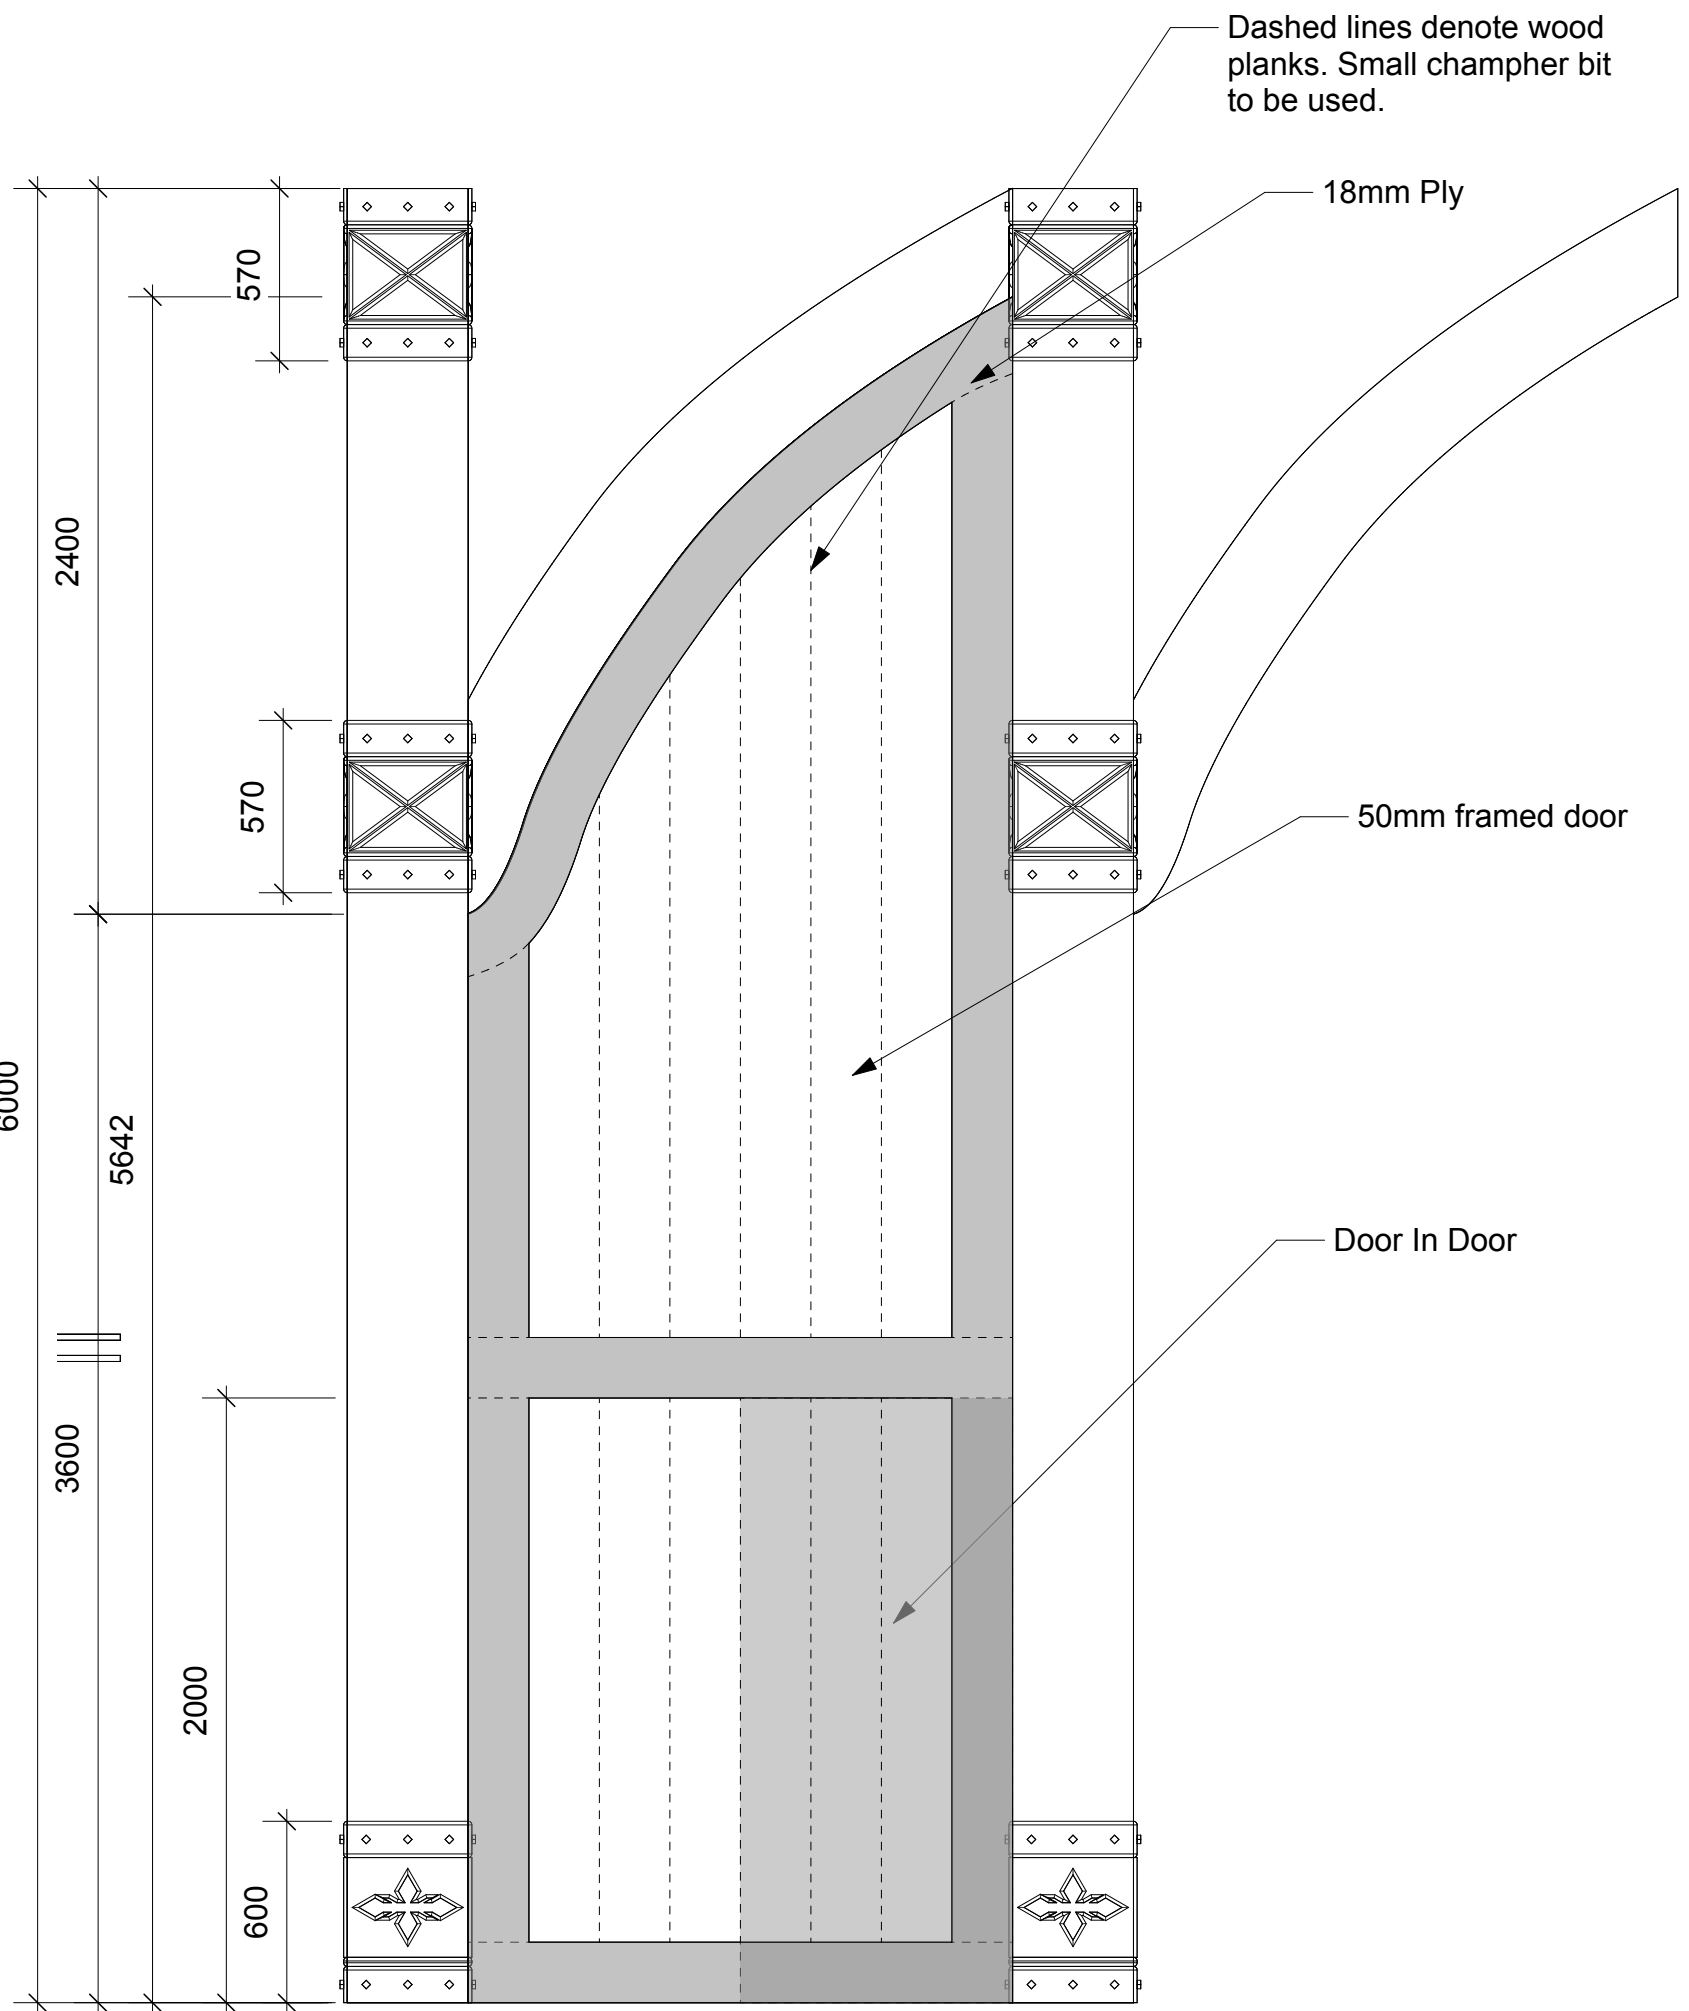

01 Door & Arch Front
Scale 1:25

Dashed lines denote wood planks. Small chamfer bit to be used.

18mm Ply

50mm framed door

Door In Door



03 Door & Arch Side
Scale 1:25

Door and Arch track seperately, but when on the same plane, should look like one piece.


Door opens upstage.

Door Inside Door opens downstage.


Door Inside Door to be disguised in door wooden plank seams

x2 of both pieces mirrored.

Frozen	
PROJECT:	Stoddart Entertainment Group
CLIENT:	Civic Theatre Newcastle
DATE:	
DESIGNER:	Markus Trew-Kayworth
BY:	Harry Gill
FORWARD DESIGNER:	Zach Krieger
SCALE:	DATE:
1:25 @ A2	12/07/2026
DRAWING NUMBER:	
13 of 26	
DESIGNED & DRAWN BY:	CONTACT:
Harry Gill	harry@markusdesigns.com
VERSION:	2024.02.02
3.0	

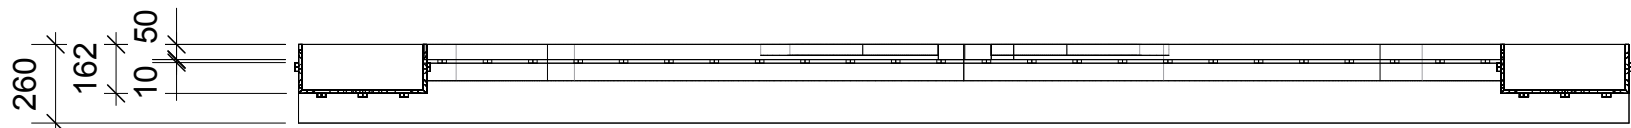


02 Chapel Wall Top
Scale 1:25

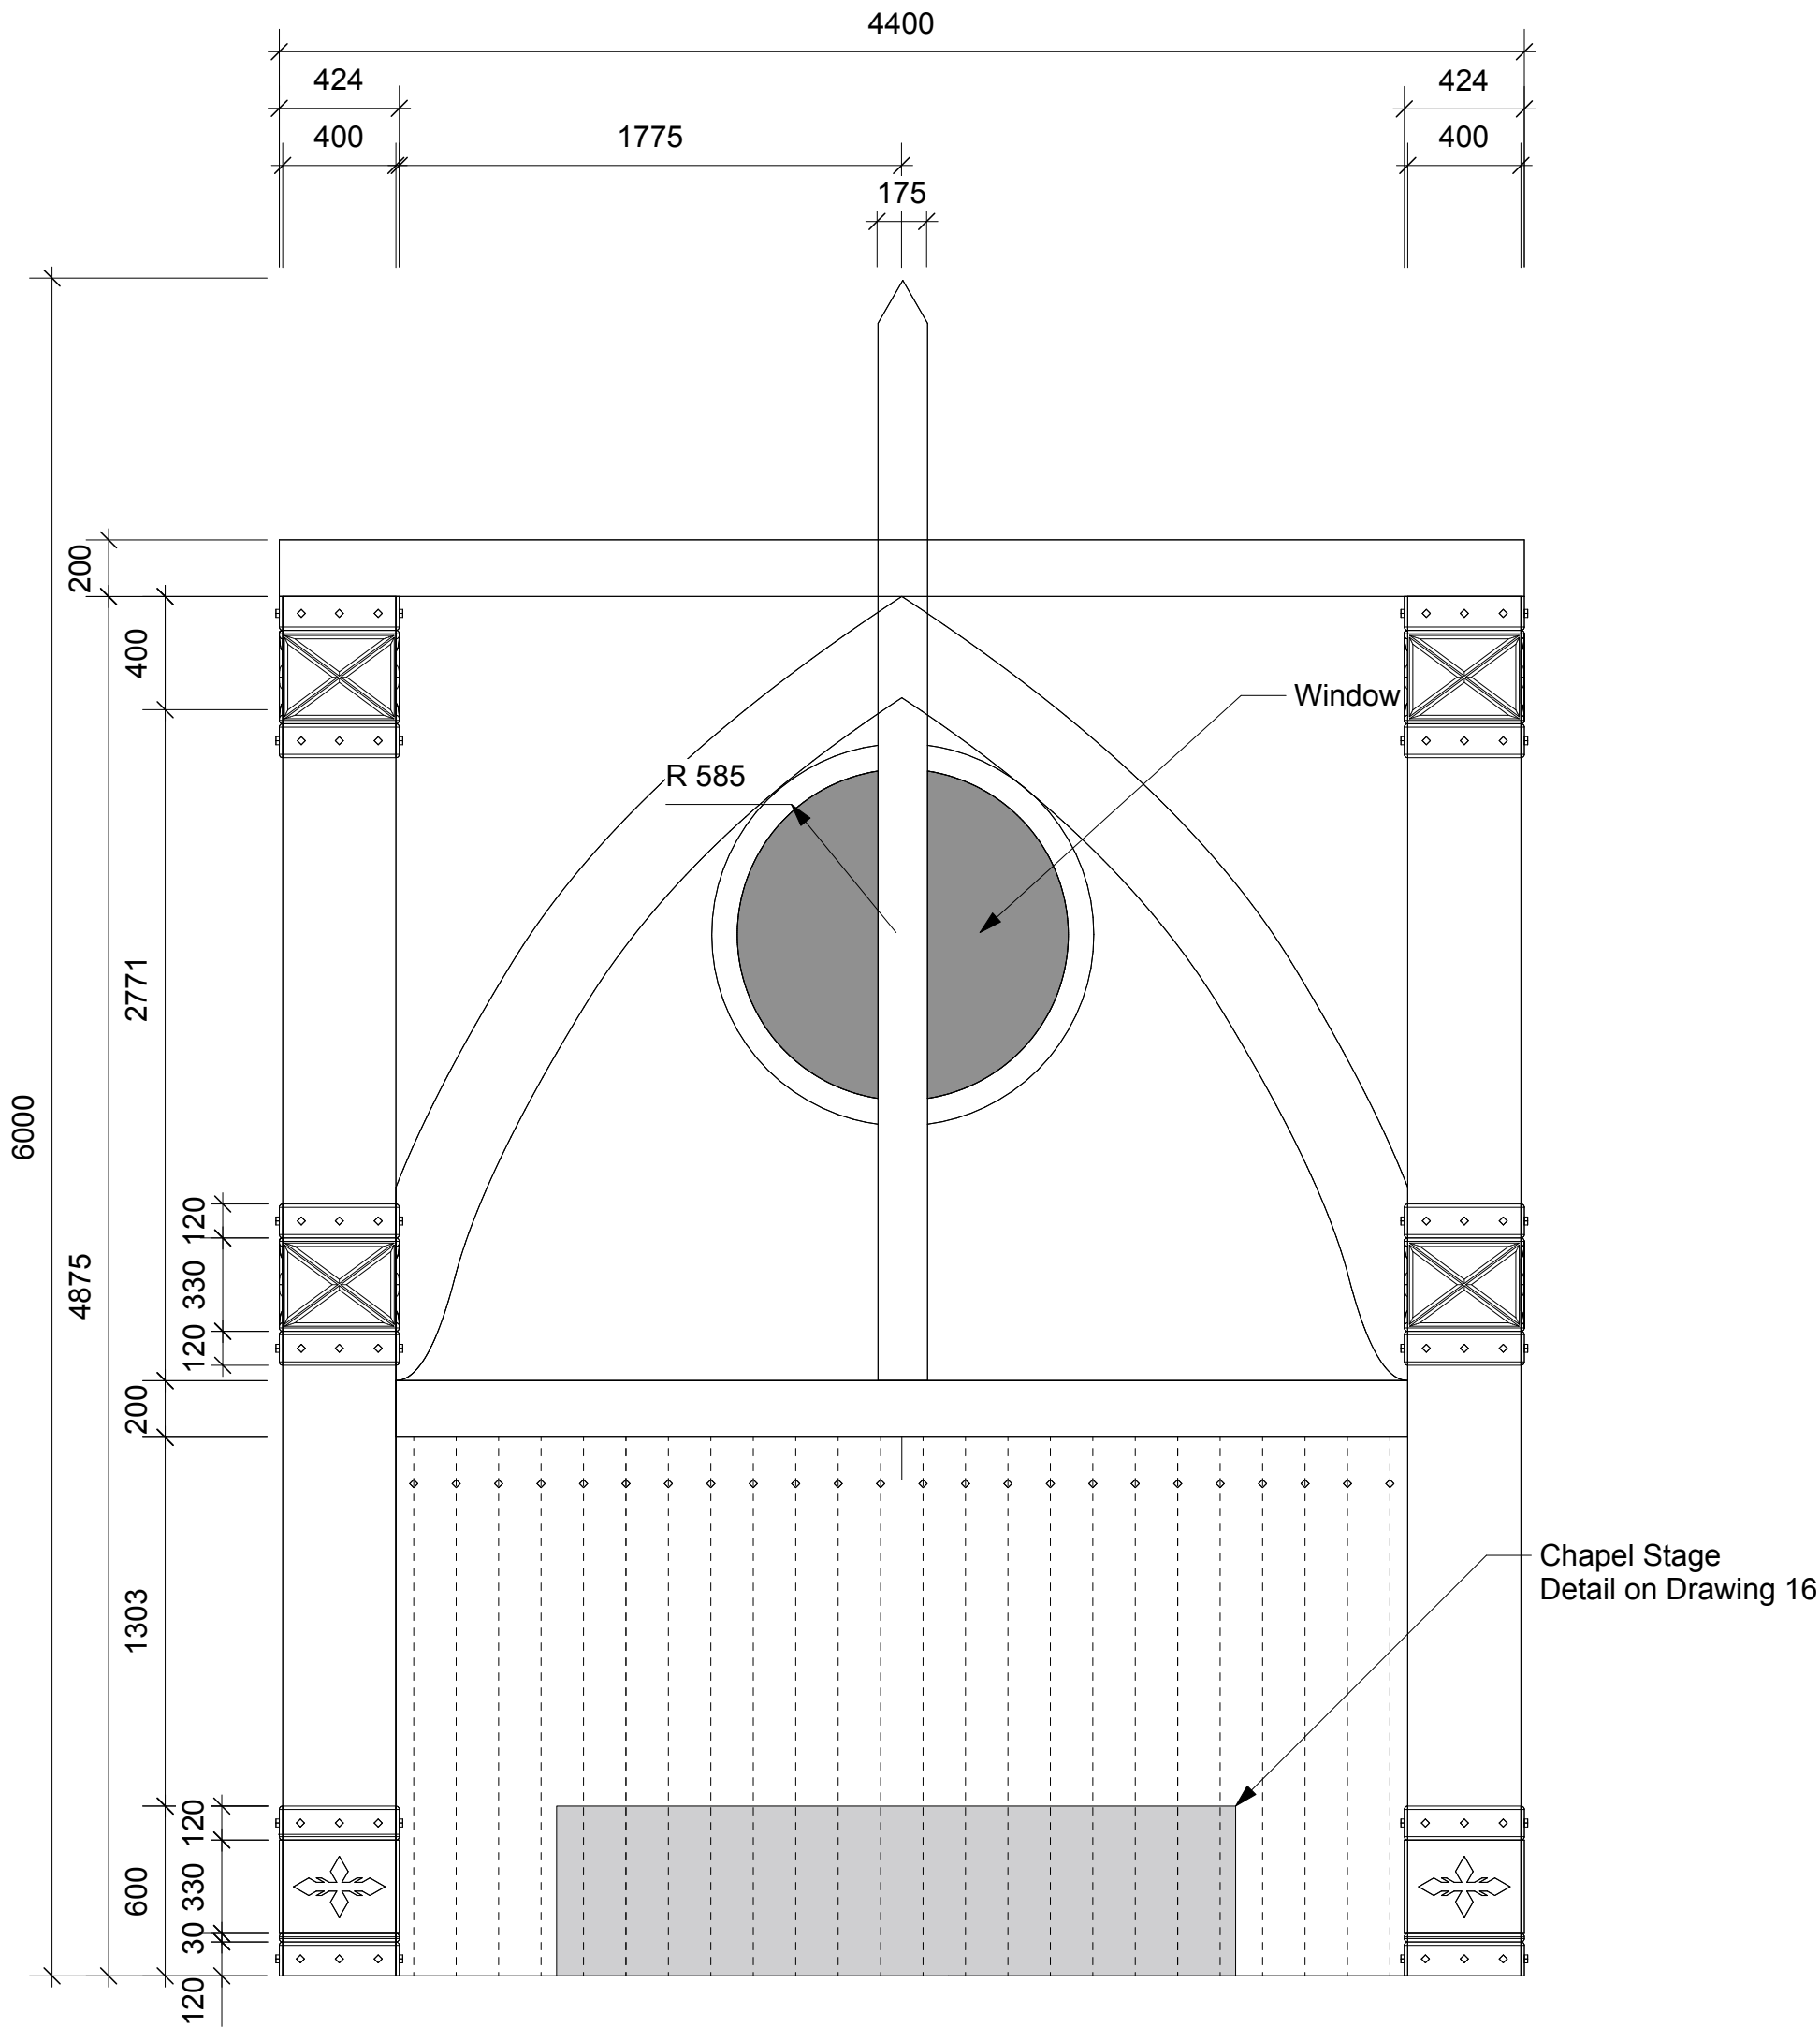

01 Chapel Wall Front
Scale 1:25




02 Chapel Wall Side
Scale 1:25

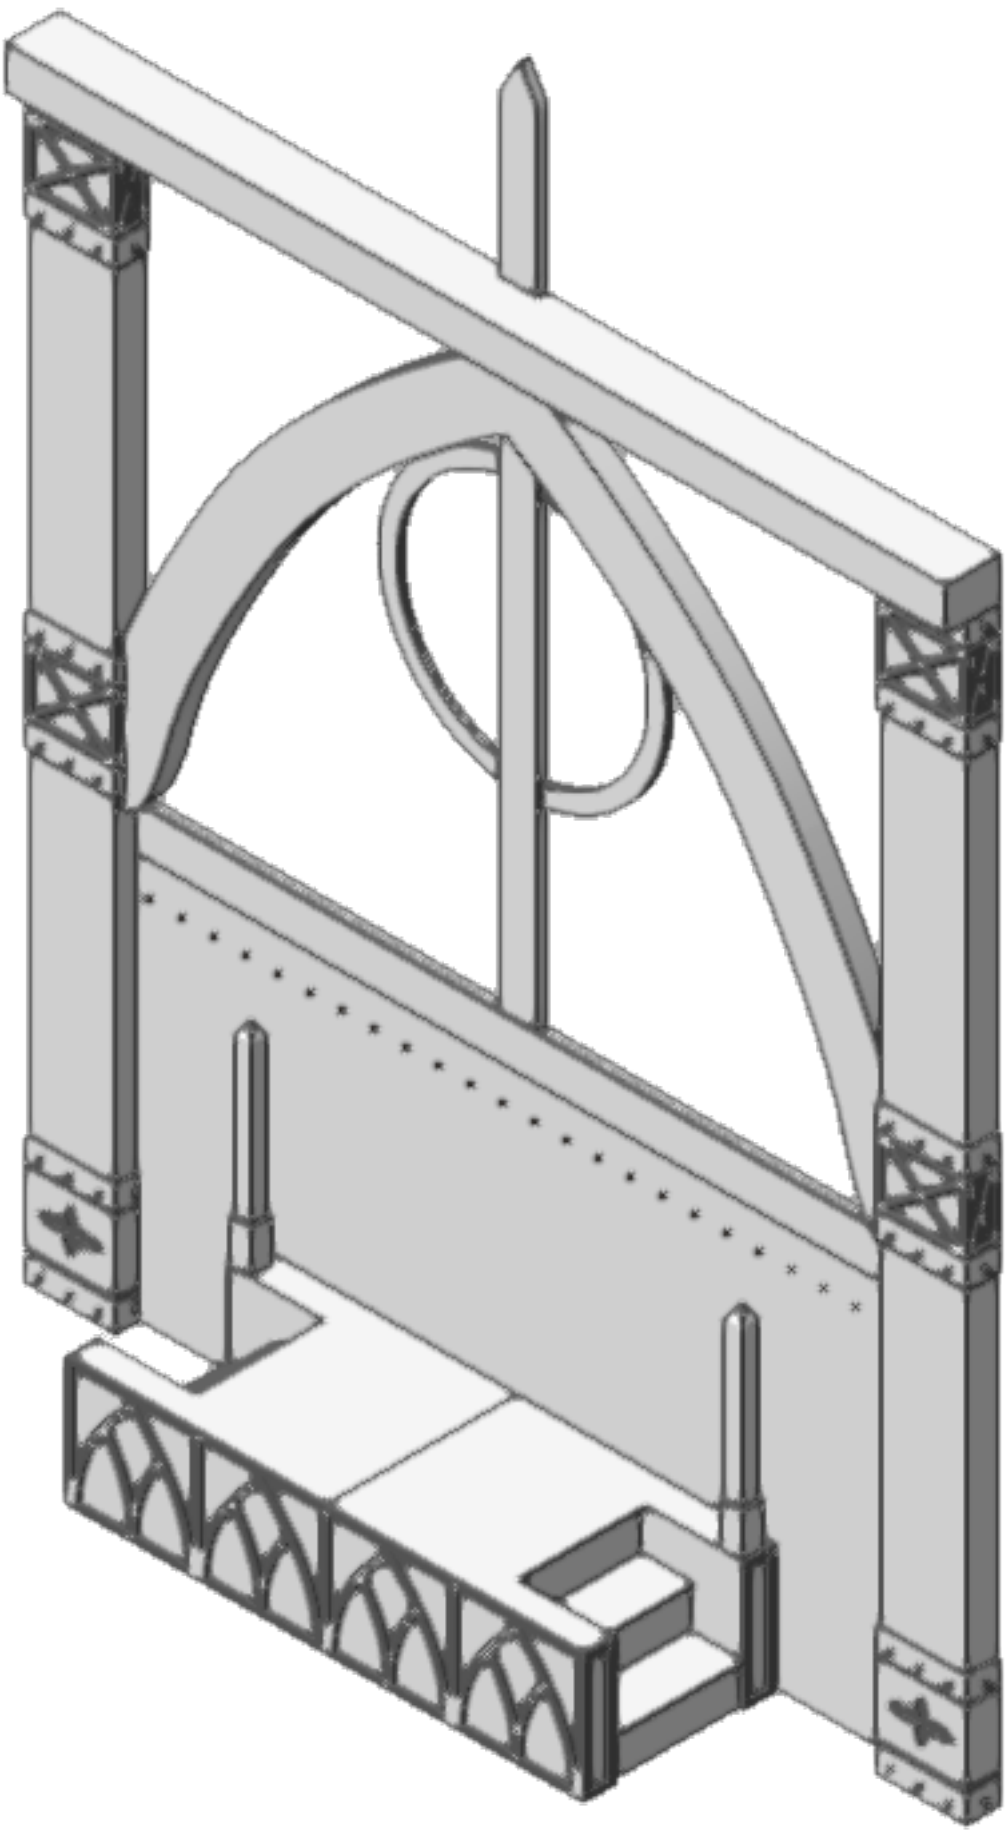


Chapel Wall flies in.

Frozen	
STODDART ENTERTAINMENT GROUP	
CIVIC THEATRE NEWCASTLE	
Chapel Wall Detail	
DIRECTOR	Markus Tress-Kayser
SET DESIGNER	Harry Gill
LIGHTING DESIGNER	Jack Krieger
SCALE	DATE
1:25 @ A2	12/07/2026
DRAWING NUMBER:	
15 of 26	
DESIGNED & DRAWN BY	COUNTRY
Harry Gill	Harry Gill
VERSION	3.0

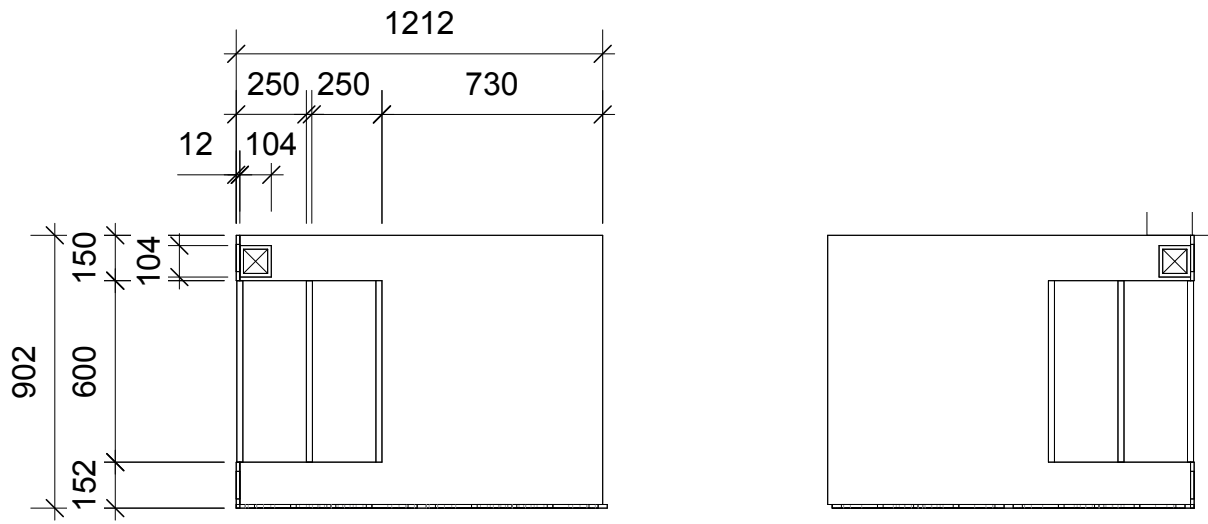


02 Chapel Stage Top
Scale 1:25

Front detail overlaps to
hide seam

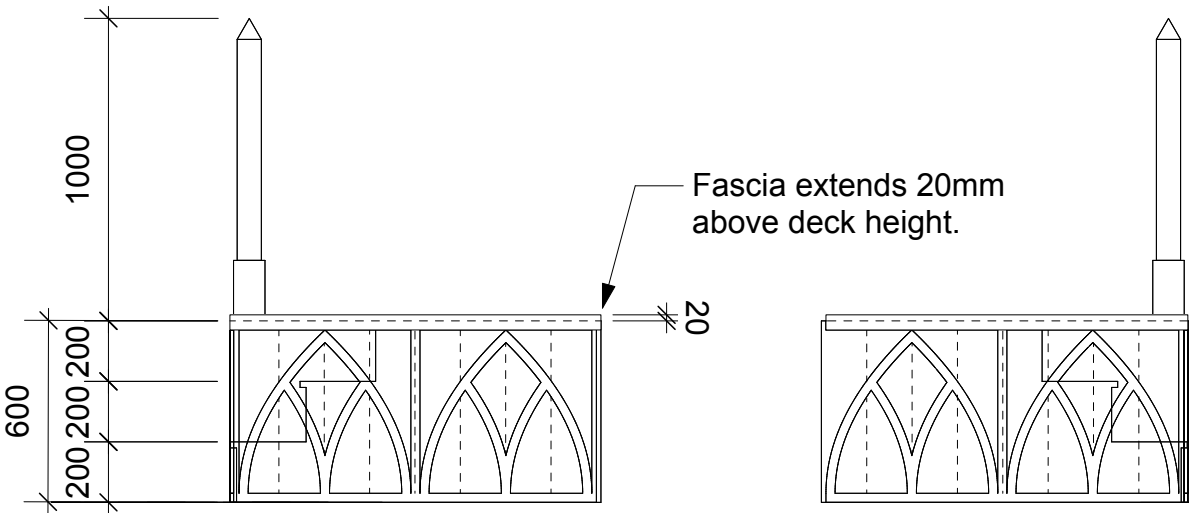

01 Chapel Stage Front
Scale 1:25

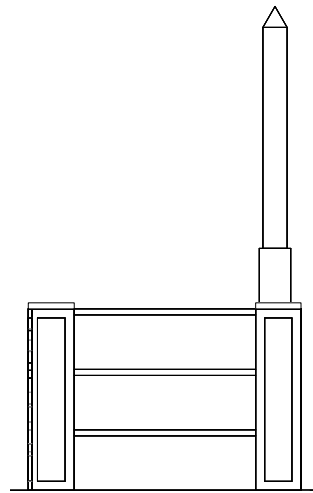

03 Chapel Stage Side
Scale 1:25


Stage trucks on on track in floor.

Inside face of trucks to have scenic finish.

Fascia extends 20mm above FFL to mask join
mechanism.


Stanchion should have enough structural
strength as is being pushed on by cast to
move truck.

Frozen	
COMPANY: Stoddart Entertainment Group	
VENUE: Civic Theatre Newcastle	
TITLE: Chapel Stage Detail	
DIRECTOR:	Madison Trew-Keyworth
SET DESIGNER:	Harry Gill
LIGHTING DESIGNER:	Zach Krause
SCALE:	DATE:
1:25 @ A3	12/07/2026
DRAWING NUMBER: 16 of 26	
DESIGNED & DRAWN BY:	CONTACT:
Harry Gill	harry@harrygilldesigns.com
VERSION: 3.0	0431 592 447

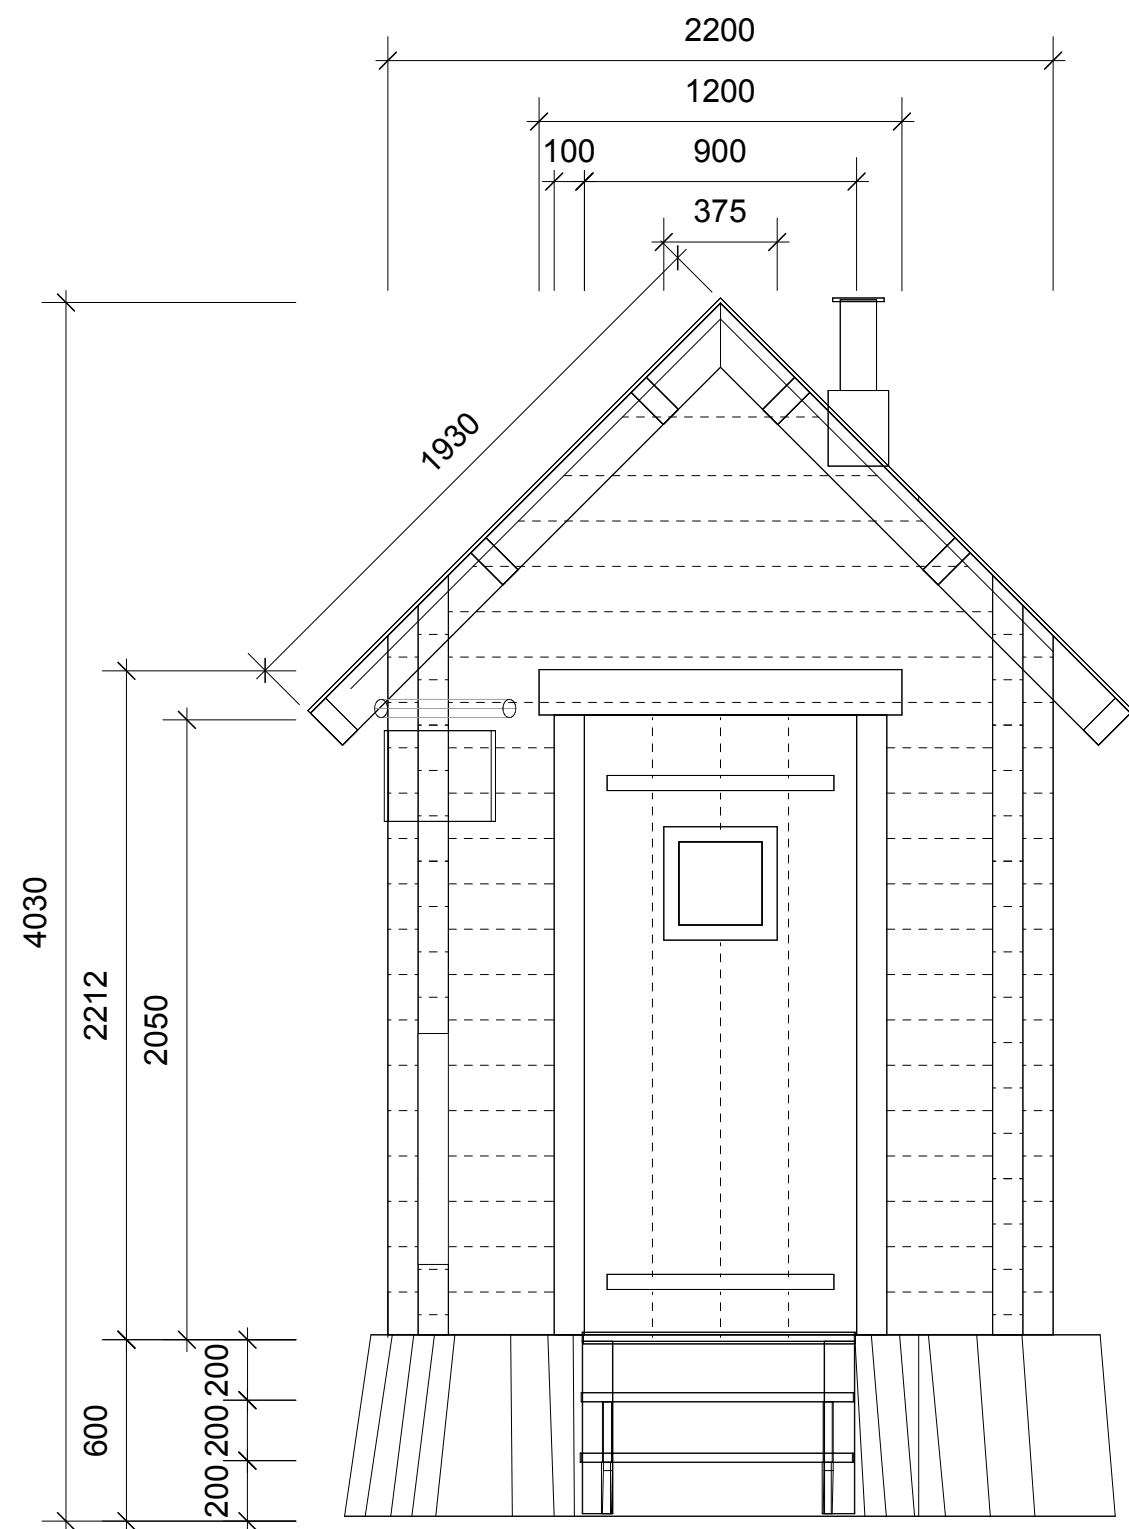


02 Okan Sauna View 1
Scale 1:25

Dashed line denotes
seperate wooden planks.
This should look like
intersecting wooden at the
corners like a log cabin.
See model & scenic
elevation for futher detail

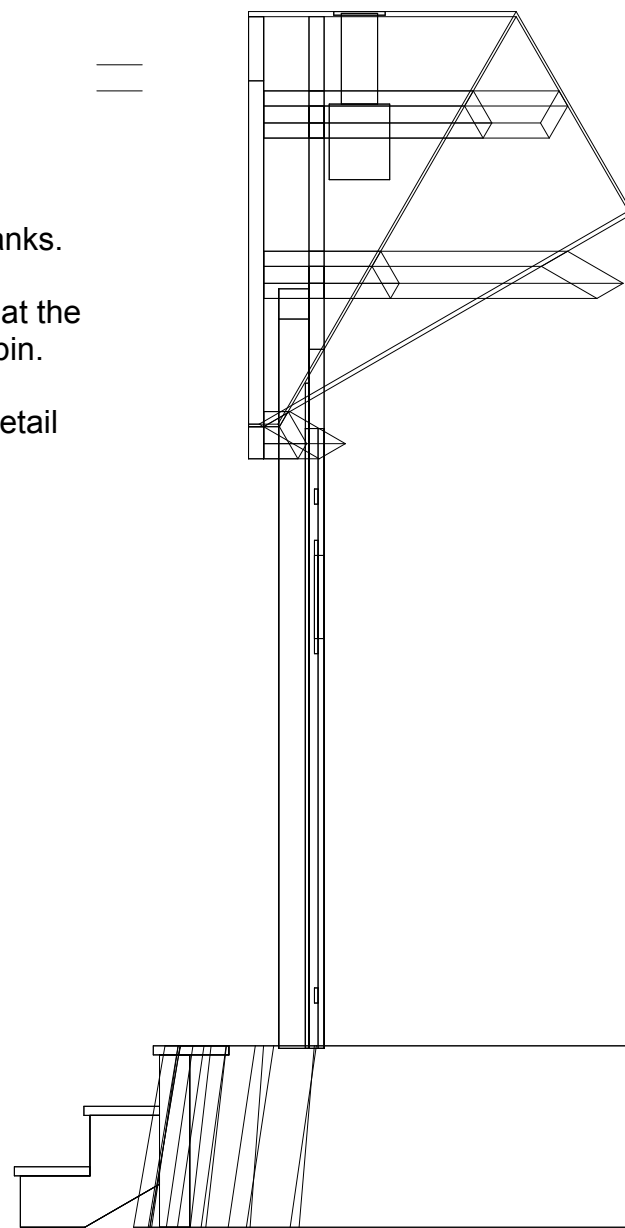

03 Okan Sauna View 2
Scale 1:25

Hanging Sign

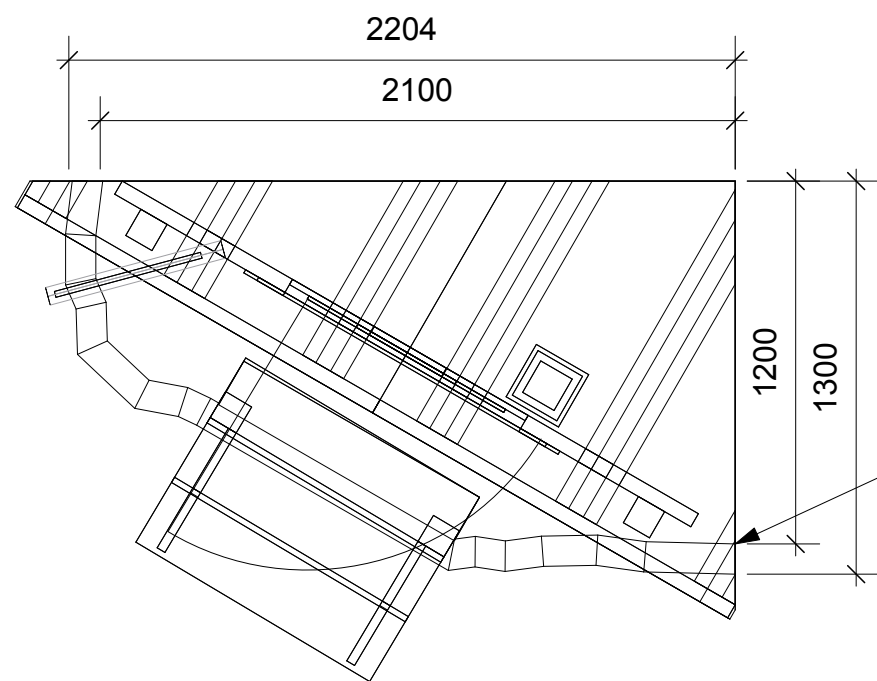

01 Oaken Sauna Top
Scale 1:25

Rocky Carving

Oaken Sauna On a Truck

100mm allowed for rocky carving

Refer to scenic elevations for rocky carving
detail.

Snow on roof. refer to scenic elevation &
model for further detail.

Frozen

STODDART ENTERTAINMENT GROUP

CIVIC THEATRE NEWCASTLE

OAKEN SAUNA DETAIL

DIRECTOR: Matthew Trew-Kayworth

ART DIRECTOR: Harry Gill


PORTING DESIGNER: Zach Kriase

SCALE: 1:25 @ A2 DATE: 12/07/2026

DRAWING NUMBER: 17 of 26

DESIGNED & DRAWN BY: CONTACT: herry@stoddartdesigns.com

3.0

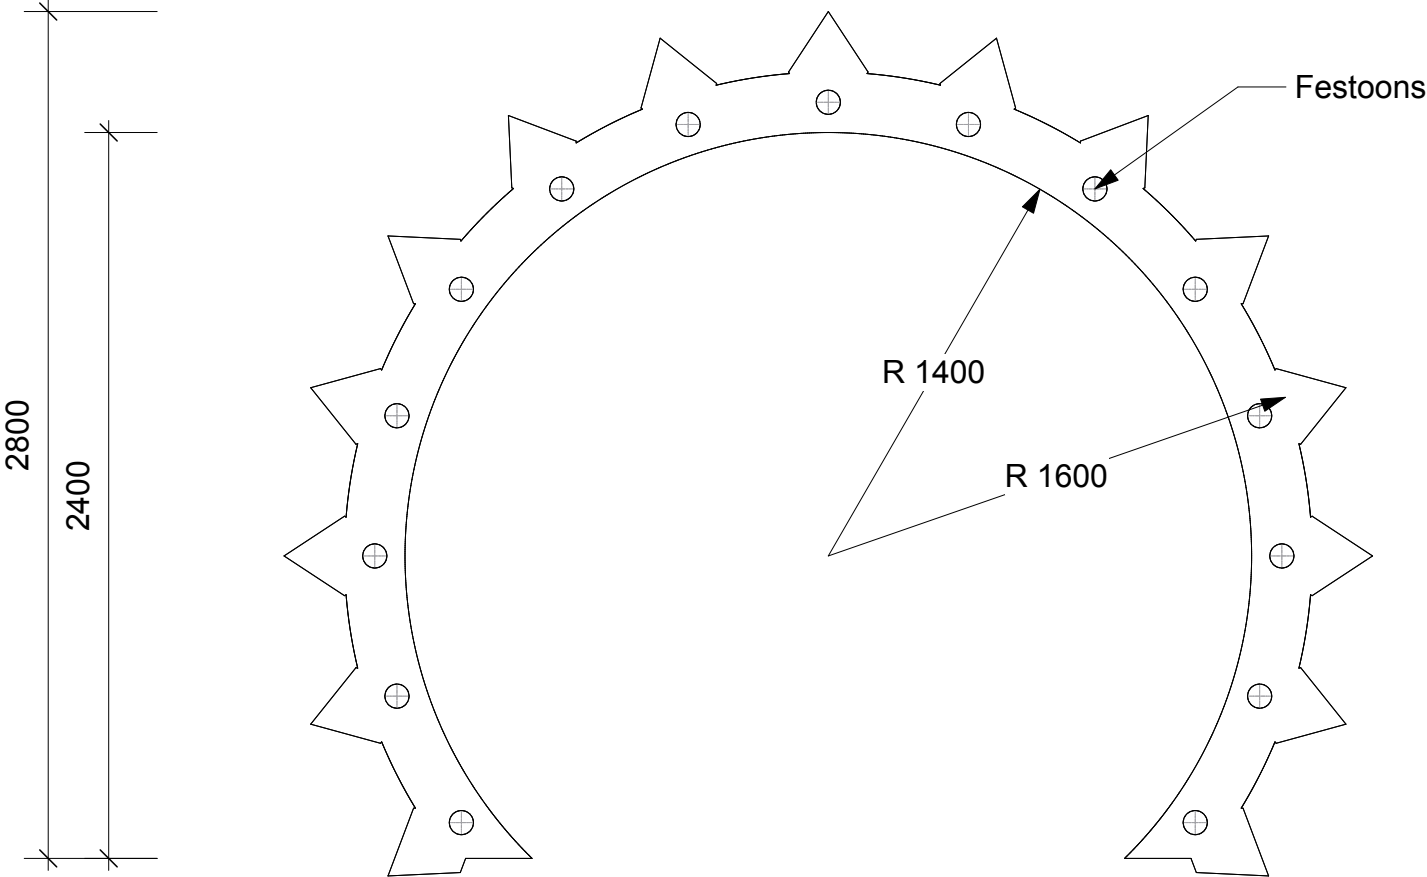

01 Sun Pros Front
Scale 1:25




02 Sun Pros Side
Scale 1:25

Flies in.


50mm nominal thickness given for frame and sun, but sun should look like a piece of paper.

Festoon ammount, spacing & hole size TBC with LD.

Frozen	
COMPANY: Stoddart Entertainment Group	
VENUE: Civic Theatre Newcastle	
TITLE: Sun Proscenium Detail	
DIRECTOR:	Madison Trew-Keyworth
SET DESIGNER:	Harry Gill
LIGHTING DESIGNER:	Zach Krause
SCALE:	DATE:
1:25 @ A3	12/07/2026
DRAWING NUMBER: 19 of 26	
DESIGNED & DRAWN BY:	CONTACT:
Harry Gill	harry@harrygilldesigns.com
VERSION: 3.0	0431 952 447

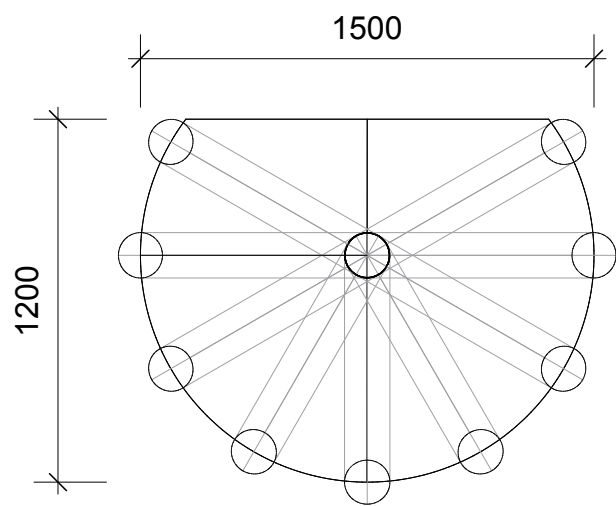

02 Bonfire Top
Scale 1:25

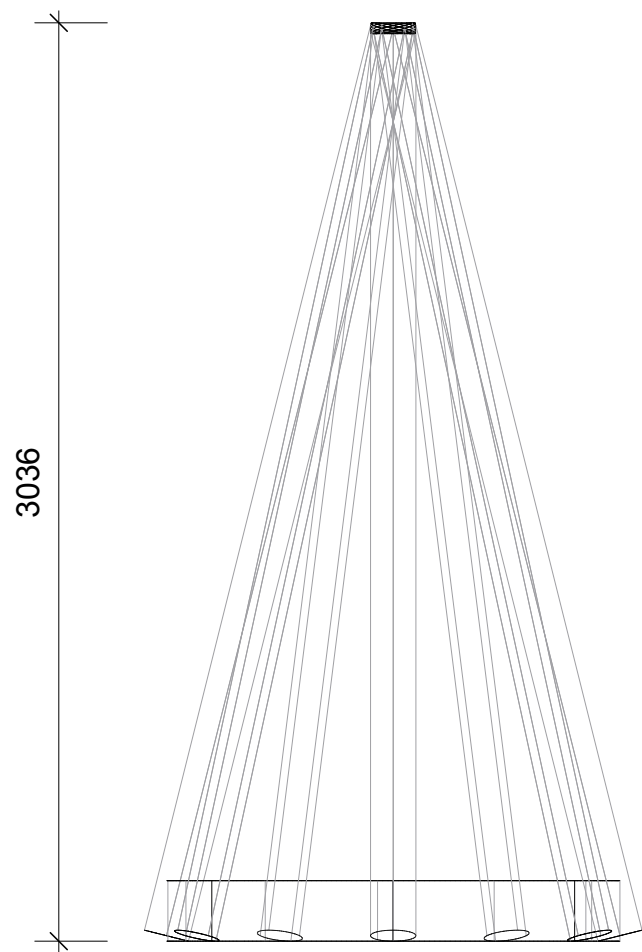

02 Bonfire Front
Scale 1:25

Bonfire made with natural looking wooden
trunks and branches

Smoke machine needed inside.

Truck disguised by branches.

Frozen

COMPANY:
Stoddart Entertainment Group

VENUE:
Civic Theatre Newcastle

TITLE:
Bonfire Detail

DIRECTOR: Madison Tseu-Keyworth

SET DESIGNER: Harry Gill

LIGHTING DESIGNER: Zach Krause

SCALE: 1:25 @ A3
DATE: 12/07/2026

DRAWING NUMBER:


21 of 26

DESIGNED & DRAWN BY:


CONTACT:

HARRY GILL
VERSION: 3.0
harry.gill@harrygilldesigns.com
0431 952 447




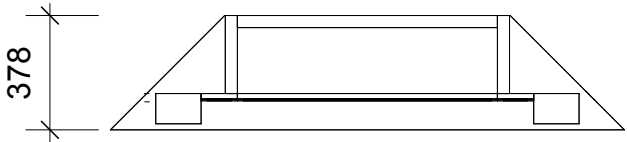


02 Fireplace Top
Scale 1:25

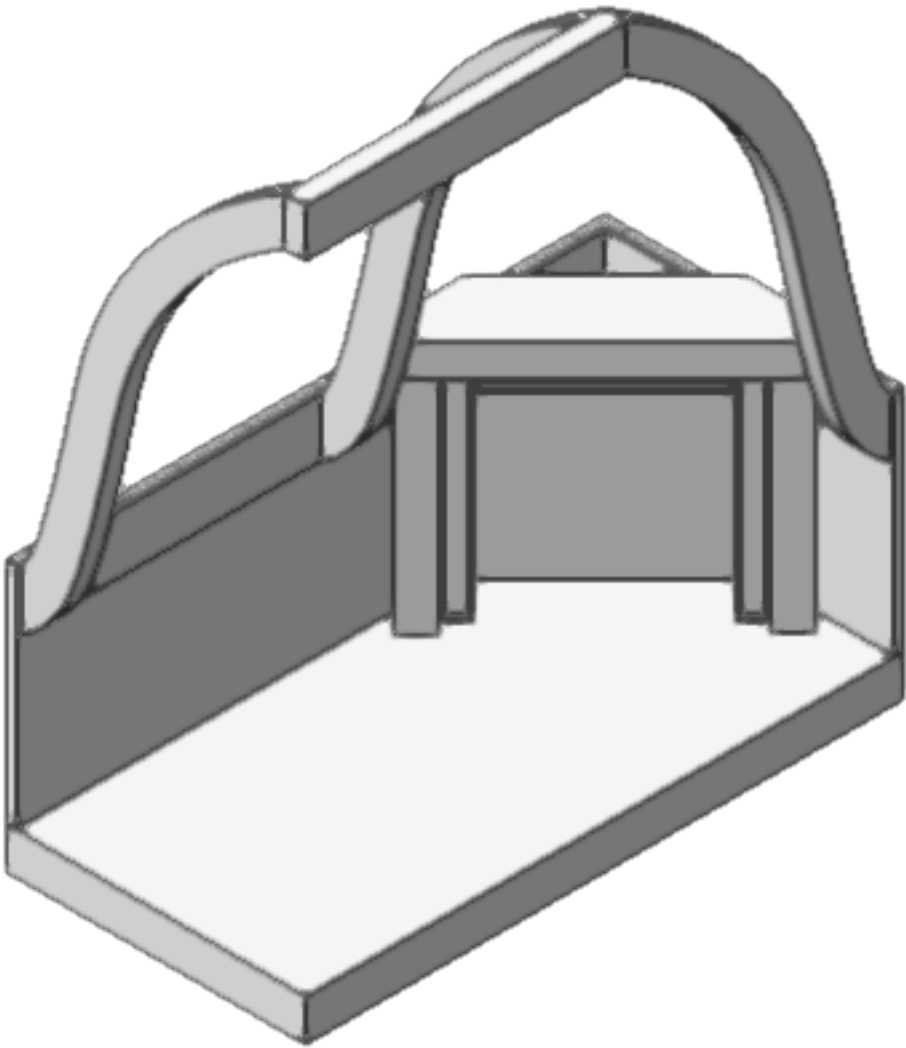

04 Fireplace Iso
Scale 1:25

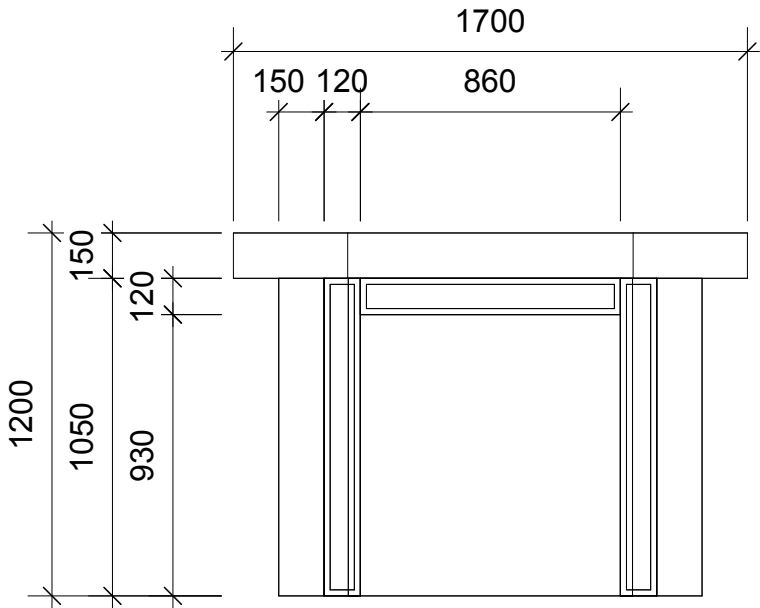


01 Fireplace Front
Scale 1:25

 


03 Fireplace Side
Scale 1:25


Frozen	
COMPANY: Stoddart Entertainment Group	
VENUE: Civic Theatre Newcastle	
TITLE: Fireplace Detail	
DIRECTOR:	Madison Tseu-Keyworth
SET DESIGNER:	Harry Gill
LIGHTING DESIGNER:	Zach Krause
SCALE:	DATE:
1:25 @ A3	12/07/2026
DRAWING NUMBER: 25 of 26	
DESIGNED & DRAWN BY:	CONTACT:
Harry Gill VERSION: 3.0	harry@harrygilldesigns.com 0431 952 447

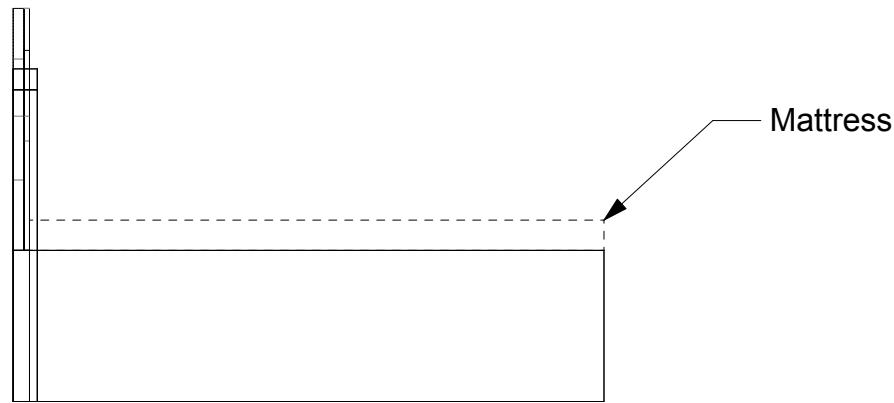

03 Bed Top
Scale 1:25

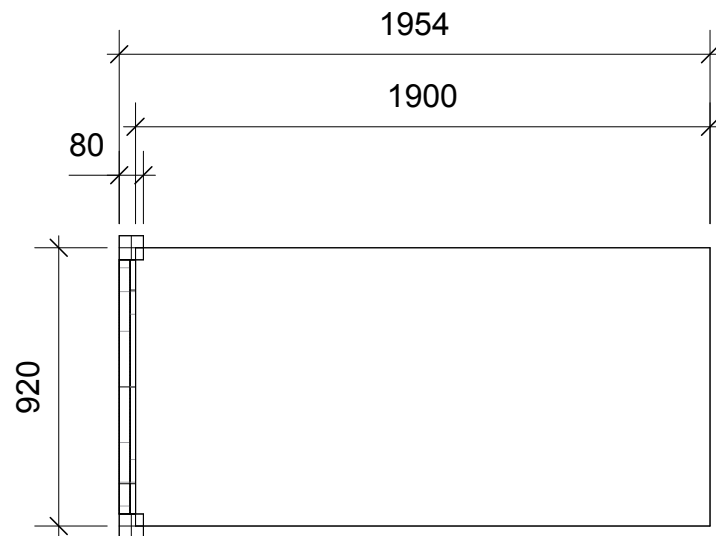

01 Bed Front
Scale 1:25

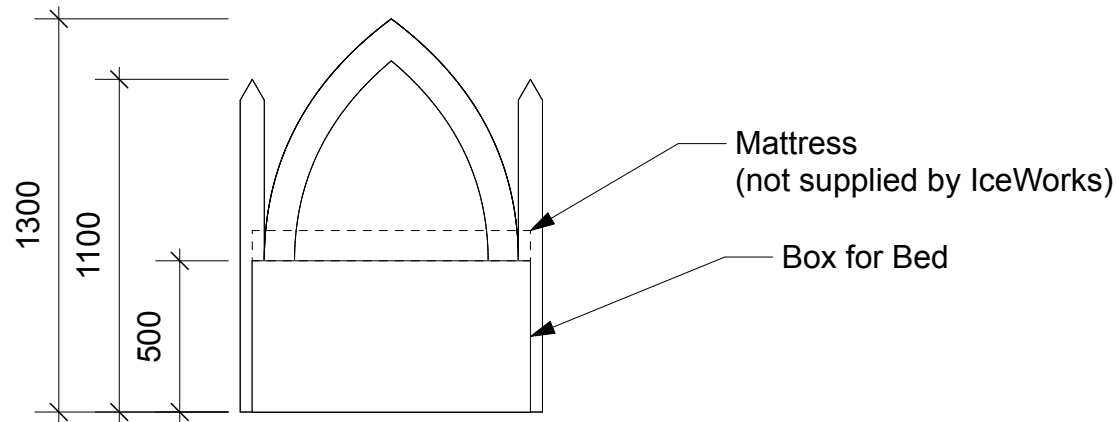

02 Bed Side
Scale 1:25

x2 Bed

Bed Box based around single bed mattress - 1900 x 920 - Access under bed needed - will be masked with valance.

Beds to be removable from bedroom truck.

Bed Box will not be visible.

Frozen	
COMPANY: Stoddart Entertainment Group	
VENUE: Civic Theatre Newcastle	
TITLE: Beds Detail	
DIRECTOR:	Madison Trew-Keyworth
SET DESIGNER:	Harry Gill
LIGHTING DESIGNER:	Zach Krause
SCALE:	DATE:
1:25 @ A3	12/07/2026
DRAWING NUMBER: 26 of 26	
DESIGNED & DRAWN BY:	CONTACT:
Harry Gill VERSION: 3.0	harry@harrygilldesigns.com 0431 952 447